■ 설계개요

사 업 명		화성동탄(2) A76-2BL 공동주택 신축공사			
대지 위치		경기도 화성시 산척동 749번지			
지역/지구		제3종 일반주거지역			
도로 현황		서측 40m도로 / 동측 16m도로 / 북측 보행자도로			
대지면적	부지면적	105,873.7000㎡			
	제외면적	0.0000㎡			
	실사용면적	**105,873.7000㎡**			
건축면적		13,425.2327㎡			
건 폐 율		**12.68%** (법정:50% 이하)			
연면적	구 분	공동주택	부대복리시설	근린생활	소계
	지 상	173,495.5971㎡	1,185.2990㎡	0.0000㎡	174,680.8961㎡
	지 하	3,006.0262㎡	79,132.3880㎡	1,234.5035㎡	83,372.9177㎡
	소 계	176,501.6233㎡	80,317.6870㎡	1,234.5035㎡	258,053.8138㎡
	합 계	**258,053.8138㎡**			
용적률 산정용 면적		174,680.8961㎡			
용적률		**164.99%** (법정:165% 이하)			
구조 / 난방방식		철근콘크리트조 / 지역난방			
세대수		**1,524세대**			
규 모		지하2층 ~ 지상 25층			
용 도		공동주택 (아파트 및 부대복리시설)			
최고높이		71.40m			

주차대수	구 분	공동주택	근린생활	합 계	비 고
	법 정	1,681 대	9 대	1,690 대	세대당 1.1 대
	계 획	2,290 대	10 대	2,300 대	세대당 1.5 대
조경면적	법 정	15.00%	(면적)	15,881.0550㎡	
	계 획	40.04%	(면적)	42,389.4000㎡	

■ 부대복리시설 설치개요

구 분		법정(상위계획) 기준	법 정	계 획	비 고
부대시설	관리사무소	10+(세대수-50)*0.05	83.7000㎡이상	173.0207㎡	지하
	MDF/방재실	-		118.5862㎡	지하
	기계/전기실	-		2,730.8881㎡	지하
	경 비 실	2개소		62.4416㎡	지상
복리시설	경 로 당	50㎡+(세대수 * 0.1)	202.4000㎡이상	216.9240㎡	지상
	어린이 집	1,000세대 이상 : 80인 * 4.29㎡ 이상 (영유아 1명당 4.29㎡이상)	343.2000㎡이상	479.6605㎡	지상
	작은도서관	500세대 이상 : 100㎡이상 (열람석6석, 도서 1,000권)	100.0000㎡이상	653.7802㎡	지하
	다함께돌봄센터	500세대 이상 : 66㎡ 이상	66.0000㎡이상	169.6636㎡	지하
	주민운동시설	500세대 이상	-	1,412.1383㎡	지하
	어린이놀이터	1000세대 이상 : 500㎡+(세대수*0.7)	1,566.8000㎡이상	1,650.0000㎡	지상
	기타복리시설	티하우스, 게스트하우스, 스카이라운지	-	3,602.4619㎡	지하 / 지상
	총 면적 기준	1,000세대 이상 : 500㎡+세대수 x 2㎡	3,548.0000㎡이상	8,184.6285㎡	주택조례

[법정] 주차 및 자전거 대수 산출근거	구 분	면적 기준		세대당 대수 기준	합 계	비 고
	공동주택	전용85이하	전용/85㎡ 1,117.2 대	세대당1.1대	1,681 대	1,681 대	주택조례 : 1.0대 공모지침 : 1.5대
		전용85초과	전용/70㎡ 564.0 대				

[법정] 주차 및 자전거 대수 산출근거	구 분	법 정	계 획		비 고
	확장형주차	주차대수의 30% 이상	687.0 대	736 대	32.14%	
	장애인주차	(법정) 주차대수의 4% 이상	67.2 대	68 대	4.05%	
	경차	주차대수 10%미만	229.0 대	196 대	8.56%	
	전기차주차	주차대수 5 %	85.0 대	161 대	7.03%	
	자전거보관소	(법정) 주차대수의 20% 이상	337.0 대	385 대	22.90%	(근생 20대 포함)
	근린생활 시설	135㎡당 1대 이상	9.14 대	10 대	109.36%	

시설별 면적표	구 분	지 상	지 하	소 계	비 고
	공동주택	173,495.5971㎡	3,006.0262㎡	176,501.6233㎡	
	복리시설	1,185.2990㎡	4,291.2397㎡	5,476.5387㎡	
	기계실/전기실	-	2,730.8881㎡	2,730.8881㎡	
	지하주차장	-	72,110.2602㎡	72,110.2602㎡	
	근린생활 시설	0.0000㎡	1,234.5035㎡	1,234.5035㎡	
	합 계	174,680.8961㎡	83,372.9177㎡	**258,053.8138㎡**	

■ 분양 면적표

구 분		세대수	세대비율	주거 전용면적	주거 공용면적			공급면적 (분양면적)	기타 공용면적					계약면적	비 고
					벽체공용	코아공용	소 계		부대복리	기계/전기실	동출입구(지하)	지하주차장	소 계		
60㎡초과 85㎡이하	84A	**677세대**	44.42%	**84.6454**	7.2274	17.6422	24.8696	**109.5150**	3.4483	1.7195	1.8927	45.4028	52.4633	**161.9783**	
	84B	**316세대**	20.73%	**84.7828**	7.1662	17.6708	24.8370	**109.6198**	3.4537	1.7222	1.8958	45.4765	52.5482	**162.1680**	
	84C	**14세대**	0.92%	**84.7828**	7.1662	17.6708	24.8370	**109.6198**	3.4537	1.7222	1.8958	45.4765	52.5482	**162.1680**	
	84D	**114세대**	7.48%	**84.8801**	7.8017	17.6912	25.4929	**110.3730**	3.4577	1.7242	1.8979	45.5289	52.6087	**162.9817**	
85㎡초과	97A	**386세대**	25.33%	**97.6197**	7.1297	20.3465	27.4762	**125.0959**	3.9767	1.9831	2.1827	52.3622	60.5047	**185.6006**	
	97B	**14세대**	0.92%	**97.6197**	7.1297	20.3465	27.4762	**125.0959**	3.9767	1.9831	2.1827	52.3622	60.5047	**185.6006**	
	142P	**3세대**	0.20%	**142.9795**	13.3934	29.8006	43.1940	**186.1735**	5.8246	2.9045	3.1971	76.6927	88.6189	**274.7924**	
합 계		**1,524세대**	100.00%	**134,436.4097**	11,039.2498	28,019.9376	39,059.1874	**173,495.5971**	5,476.5387	2,730.8881	3,006.0262	72,110.2602	83,323.7132	**256,819.3103**	

경기주택도시공사

설계명 PROJECT TITLE

화성동탄(2)A76-2BL
민간참여 공동주택사업

주기 NOTE

NO	DATE	REVISION DESCRIPTION	APPD
△			
△			
△			
△			

설계 DESIGN
파트장
본부장
PM
담당

대표전화

축 척 SCALE
A1 1 / NONE
A3 1 / NONE

일 자 DATE
2025. 10.

설계번호 PROJECT NO.
AR - 23 - 026

도면화일명 DWG. FILE NAME

도면번호 SHEET NO.
A00 - 014

도면명 SUBJECT TITLE
설계개요

■ 동별/층별 면적개요

구분	동별	층수 및 세대수		지하층			지상층																									연면적	건축면적
		최고층수	세대수	지하2층	지하1층	지하층소계	1층	2층	3층	4층	5층	6층	7층	8층	9층	10층	11층	12층	13층	14층	15층	16층	17층	18층	19층	20층	21층	22층	23층	24층	25층	지상층소계		
아파트	3531동	24층	88세대	104.9089		104.9089	296.6480	283.5659	481.2885	481.2885	481.2885	481.2885	481.2885	481.2885	481.2885	481.2885	481.2885	481.2885	481.2885	481.2885	481.2885	481.2885	481.2885	481.2885	481.2885	481.2885	481.2885	481.2885	259.8635	245.3347	-	10,711.1821	10,816.0910	678.7055
	3532동	15층	63세대	97.9102		97.9102	461.1812	443.0803	537.8247	537.8247	537.8247	537.8247	537.8247	537.8247	537.8247	537.8247	537.8247	537.8247	537.8247	219.6530	219.6530	192.2803	-	-	-	-	-	-	-	-	-	6,914.0948	7,012.0050	771.9152
	3533동	7층	32세대	96.0182		96.0182	460.8700	442.6893	537.4337	537.4337	537.4337	537.4337	537.4337	510.0610	-	-	-	-	-	-	-	-	-	-	-	-	-	-	-	-	-	3,563.3551	3,659.3733	771.9152
	3534동	16층	66세대	99.8512		99.8512	461.4508	443.3498	538.0942	538.0942	538.0942	538.0942	538.0942	538.0942	538.0942	538.0942	538.0942	538.0942	538.0942	226.2388	226.2388	226.2388	226.2388	-	-	-	-	-	-	-	-	7,190.6978	7,290.5490	771.9152
	3535동	19층	82세대	110.6185		110.6185	474.1494	456.0651	550.7930	550.7930	550.7930	550.7930	550.7930	550.7930	550.7930	550.7930	550.7930	550.7930	550.7930	550.7930	523.4203	331.1400	331.1400	331.1400	331.1400	331.1400	-	-	-	-	-	9,168.0578	9,278.6763	789.6364
	3536동	19층	51세대	67.3184		67.3184	264.2558	258.2503	351.8529	351.8529	351.8529	351.8529	351.8529	351.8529	351.8529	351.8529	351.8529	351.8529	351.8529	351.8529	351.8529	351.8529	243.2169	243.2169	243.2169	243.2169	243.2169	-	-	-	-	-	6,069.4614	6,136.7798	512.1996
	3537동	24층	84세대	123.5508	121.2368	244.7876	380.8432	360.6750	458.4204	458.4204	458.4204	458.4204	458.4204	458.4204	458.4204	458.4204	458.4204	458.4204	458.4204	458.4204	458.4204	458.4204	458.4204	458.4204	458.4204	458.4204	458.4204	239.0996	239.0996	239.0996	239.0996	239.0996	-	9,730.1630	9,974.9506	667.6207
	3538동	19층	74세대	118.9256	113.2494	232.1750	457.9344	437.6046	437.6046	437.6046	437.6046	437.6046	437.6046	437.6046	437.6046	437.6046	437.6046	437.6046	437.6046	437.6046	437.6046	437.6046	437.6046	437.6046	437.6046	218.8023	-	-	-	-	-	8,116.0149	8,348.1899	639.0294
	3539동	24층	89세대	111.5949	127.5737	239.1686	406.8186	386.1848	483.9303	483.9303	483.9303	483.9303	483.9303	483.9303	483.9303	483.9303	483.9303	483.9303	483.9303	483.9303	483.9303	483.9303	483.9303	483.9303	483.9303	483.9303	378.8179	378.8179	378.8179	378.8179	378.8179	-	10,913.9080	11,153.0766	694.3926
	3540동	25층	116세대	140.9633	140.7595	281.7228	376.8353	454.9803	561.3515	561.3515	561.3515	561.3515	561.3515	561.3515	561.3515	561.3515	561.3515	561.3515	561.3515	561.3515	561.3515	561.3515	561.3515	561.3515	561.3515	561.3515	561.3515	561.3515	561.3515	339.1503	339.1503	339.1503	13,076.2965	13,358.0193	808.8813
	3541동	25층	119세대	137.3245	139.9763	277.3008	472.8026	454.9803	561.3515	561.3515	561.3515	561.3515	561.3515	561.3515	561.3515	561.3515	561.3515	561.3515	561.3515	561.3515	561.3515	561.3515	561.3515	561.3515	561.3515	561.3515	561.3515	561.3515	561.3515	339.1503	339.1503	339.1503	13,394.4650	13,671.7658	810.2773
	3542동	25층	119세대	131.9384	128.5333	260.4717	469.4632	451.5925	557.5576	557.5576	557.5576	557.5576	557.5576	557.5576	557.5576	557.5576	557.5576	557.5576	557.5576	557.5576	557.5576	557.5576	557.5576	557.5576	557.5576	557.5576	557.5576	557.5576	557.5576	557.5576	557.5576	335.3564	335.3564	13,300.4781	13,560.9498	802.2922
	3543동	25층	111세대	116.7376	110.7651	227.5027	369.7417	354.2245	554.1552	554.1552	554.1552	554.1552	554.1552	554.1552	554.1552	554.1552	554.1552	554.1552	554.1552	554.1552	554.1552	554.1552	554.1552	554.1552	554.1552	554.1552	554.1552	554.1552	554.1552	335.3564	335.3564	335.3564	335.3564	335.3564	12,375.5418	12,603.0445	782.4661
	3544동	25층	96세대	109.3932	106.5416	215.9348	287.4085	272.0988	483.1571	483.1571	483.1571	483.1571	483.1571	483.1571	483.1571	483.1571	483.1571	483.1571	483.1571	483.1571	483.1571	483.1571	483.1571	483.1571	483.1571	483.1571	483.1571	483.1571	483.1571	483.1571	483.1571	483.1571	483.1571	483.1571	11,672.1206	11,888.0554	679.8491
	3545동	25층	117세대	115.3414	115.4482	230.7896	389.2623	371.8210	561.1145	561.1145	561.1145	561.1145	561.1145	561.1145	561.1145	561.1145	561.1145	561.1145	561.1145	561.1145	561.1145	561.1145	561.1145	561.1145	561.1145	561.1145	561.1145	561.1145	561.1145	339.0866	339.0866	13,222.6610	13,453.4506	800.1836
	3546동	25층	96세대	104.7655		104.7655	270.7042	258.9680	443.7944	443.7944	443.7944	443.7944	443.7944	443.7944	443.7944	443.7944	443.7944	443.7944	443.7944	443.7944	443.7944	443.7944	443.7944	443.7944	443.7944	443.7944	443.7944	443.7944	443.7944	443.7944	443.7944	443.7944	10,736.9434	10,841.7089	631.0389
	3547동	25층	121세대	114.7817		114.7817	375.1446	361.5356	547.9772	547.9772	547.9772	547.9772	547.9772	547.9772	547.9772	547.9772	547.9772	547.9772	547.9772	547.9772	547.9772	547.9772	547.9772	547.9772	547.9772	547.9772	547.9772	547.9772	547.9772	547.9772	547.9772	547.9772	13,340.1558	13,454.9375	783.8378
	소 계(1)	17 동	1,524세대	1,901.9423	1,104.0839	3,006.0262	6,675.5138	6,491.6661	8,647.7013	8,647.7013	8,647.7013	8,647.7013	8,620.3286	8,110.2676	8,110.2676	8,110.2676	8,110.2676	8,110.2676	7,480.2405	7,452.8678	7,233.2148	6,932.2985	6,706.0597	6,706.0597	6,487.2574	5,369.6650	5,150.8662	5,150.8662	4,707.2400	4,026.2809	3,163.0287	173,495.5971	176,501.6233	12,396.1561
부대복리시설	218동	관리사무소		-	291.6069	291.6069	-	-	-	-																					-	291.6069	-
	219동	작은도서관		-	653.7802	653.7802	-	-	-	-																					-	653.7802	-
	220동	주민공용시설 (주민회의실,코인세탁실, 기타)		-	554.6253	554.6253	-	-	-	-																					-	554.6253	-
	221동	그리너리카페		-	105.9000	105.9000	-	-	-	-																					-	105.9000	-
	222동	근로자휴게실		-	58.5005	58.5005	-	-	-	-																					-	58.5005	-
	223동	경로당		-	-	-	216.9240	-	-	-																					216.9240	216.9240	220.1600
	224동	어린이집		-	-	-	479.6605	-	-	-																					479.6605	479.6605	491.5820
	225동	다함께돌봄센터		-	169.6636	169.6636	-	-	-	-																					-	169.6636	-
	225동A	어린이실내놀이터		-	157.5975	157.5975	-	-	-	-																					-	157.5975	-
	226동	티하우스		-	-	-	112.5075	-	-	-																					112.5075	112.5075	110.9262
	227동	게스트하우스		-	-	-	106.6710	-	-	-																					106.6710	106.6710	110.0277
	228동	여성공동작업실-1		-	47.7494	47.7494	-	-	-	-																					-	47.7494	-
	229동	여성공동작업실-2		-	31.5782	31.5782	-	-	-	-																					-	31.5782	-
	230동	스카이라운지		-	-	-	-	-	-	-																				176.5594		176.5594	176.5594	-
	231동	골프연습장 및 주민공동시설		2,079.1725	-	2,079.1725	-	-	-	-																					-	2,079.1725	-
	232동	경비실-1		-	-	-	37.6629	-	-	-																					37.6629	37.6629	37.6629
	233동	경비실-2		-	-	-	24.7787	-	-	-																					24.7787	24.7787	24.7787
	234동	키즈스테이션-1		-	45.8594	45.8594	-	-	-	-																					-	45.8594	-
	235동	키즈스테이션-2		-	-	-	30.5350	-	-	-																					30.5350	30.5350	33.9391
	236동	재활용품보관소		95.2062	-	95.2062	-	-	-	-																					-	95.2062	-
	소 계(2)			2,174.3787	2,116.8610	4,291.2397	1,008.7386	-	-	-	17,295.4026	-	-	-	-	-	-	-	-	-	-	-	-	-	-	-	-	-	-	-	176.5594	-	1,185.2990	5,476.5387	1,029.0766
	237동	배수펌프실-1, -2		63.6133	-	63.6133	-	-	-	-																							63.6133	
		제연챔버		332.5993	582.3029	914.9022	-	-	-	-																					-	914.9022	-
		동전기실		118.3684	126.1972	244.5656	-	-	-	-																					-	244.5656	-
		우수조 관리층-1		107.5372	-	107.5372	-	-	-	-																					-	107.5372	-
		우수조 관리층-2		61.0828	-	61.0828	-	-	-	-																					-	61.0828	-
		우수조 관리층-3		60.3069	-	60.3069	-	-	-																						-	60.3069	
		우수조 관리층-4		75.8379	-	75.8379	-	-	-																						-	75.8379	
		우수조 관리층-5		59.8785	-	59.8785	-	-	-																						-	59.8785	
		우수조 관리층-6		55.2010	-	55.2010	-	-	-																						-	55.2010	
		우수조 관리층-7		78.0385	-	78.0385	-	-	-																						-	78.0385	
		우수조 관리층-8		90.1800	-	90.1800	-	-	-																						-	90.1800	
		기계실		495.0096	-	495.0096	-	-	-	-																					-	495.0096	-
		전기실		299.0891	-	299.0891	-	-	-	-																					-	299.0891	
		발전기실		125.6455	-	125.6455	-	-	-	-																					-	125.6455	
	소 계(3)			2,022.3880	708.5001	2,730.8881	-	-	-	-	-	-	-	-	-	-	-	-	-	-	-	-	-	-	-	-	-	-	-	-	-	2,730.8881	-
	238동 지하주차장	지하주차장(램품포함)		51,372.2747	20,672.7008	72,044.9755	-	-	-	-																					-	72,044.9755	-
		주차장(내부계단,외부출입구홀)		22.1200	43.1647	65.2847	-	-	-	-																					-	65.2847	-
	소 계(4)			51,394.3947	20,715.8655	72,110.2602	-	-	-	-	-	-	-	-	-	-	-	-	-	-	-	-	-	-	-	-	-	-	-	-	-	72,110.2602	-
아파트 소계(1+2+3+4)				57,493.1037	24,645.3105	82,138.4142	7,684.2534	6,491.6661	8,647.7013	25,943.1039	8,647.7013	8,647.7013	8,620.3286	8,110.2676	8,110.2676	8,110.2676	8,110.2676	8,110.2676	7,480.2405	7,452.8678	7,233.2148	6,932.2985	6,706.0597	6,706.0597	6,487.2574	5,369.6650	5,150.8662	5,150.8662	4,707.2400	4,202.8403	3,163.0287	174,680.8961	256,819.3103	13,425.2327
근린생활시설	239동	근린생활시설-1		-	280.8709	280.8709	-	-	-	-																					-	280.8709	-
	240동	근린생활시설-2		-	953.6326	953.6326	-	-	-	-																					-	953.6326	-
	소 계(5)			-	1,234.5035	1,234.5035	-	-	-	-	-	-	-	-	-	-	-	-	-	-	-	-	-	-	-	-	-	-	-	-	-	1,234.5035	-
총 계(1+2+3+4+5)				57,493.1037	25,879.8140	83,372.9177	7,684.2534	6,491.6661	8,647.7013	25,943.1039	8,647.7013	8,647.7013	8,620.3286	8,110.2676	8,110.2676	8,110.2676	8,110.2676	8,110.2676	7,480.2405	7,452.8678	7,233.2148	6,932.2985	6,706.0597	6,706.0597	6,487.2574	5,369.6650	5,150.8662	5,150.8662	4,707.2400	4,202.8403	3,163.0287	174,680.8961	258,053.8138	13,425.2327

경기주택도시공사

설계명 PROJECT TITLE

화성동탄(2)A76-2BL
민간참여 공동주택사업

주기 NOTE

NO	DATE	REVISION DESCRIPTION	APPD
△			
△			
△			
△			

설 계 DESIGN
- 파트장
- 본부장
- PM
- 담당

대표전화

축 척 SCALE
- A1 1 / NONE
- A3 1 / NONE

일 자 DATE 2025. 10.


설계번호 PROJECT NO. AR - 23 - 026

도면화일명 DWG. FILE NAME

도면번호 SHEET NO. A00 - 015

도면명 SUBJECT TITLE

동별개요

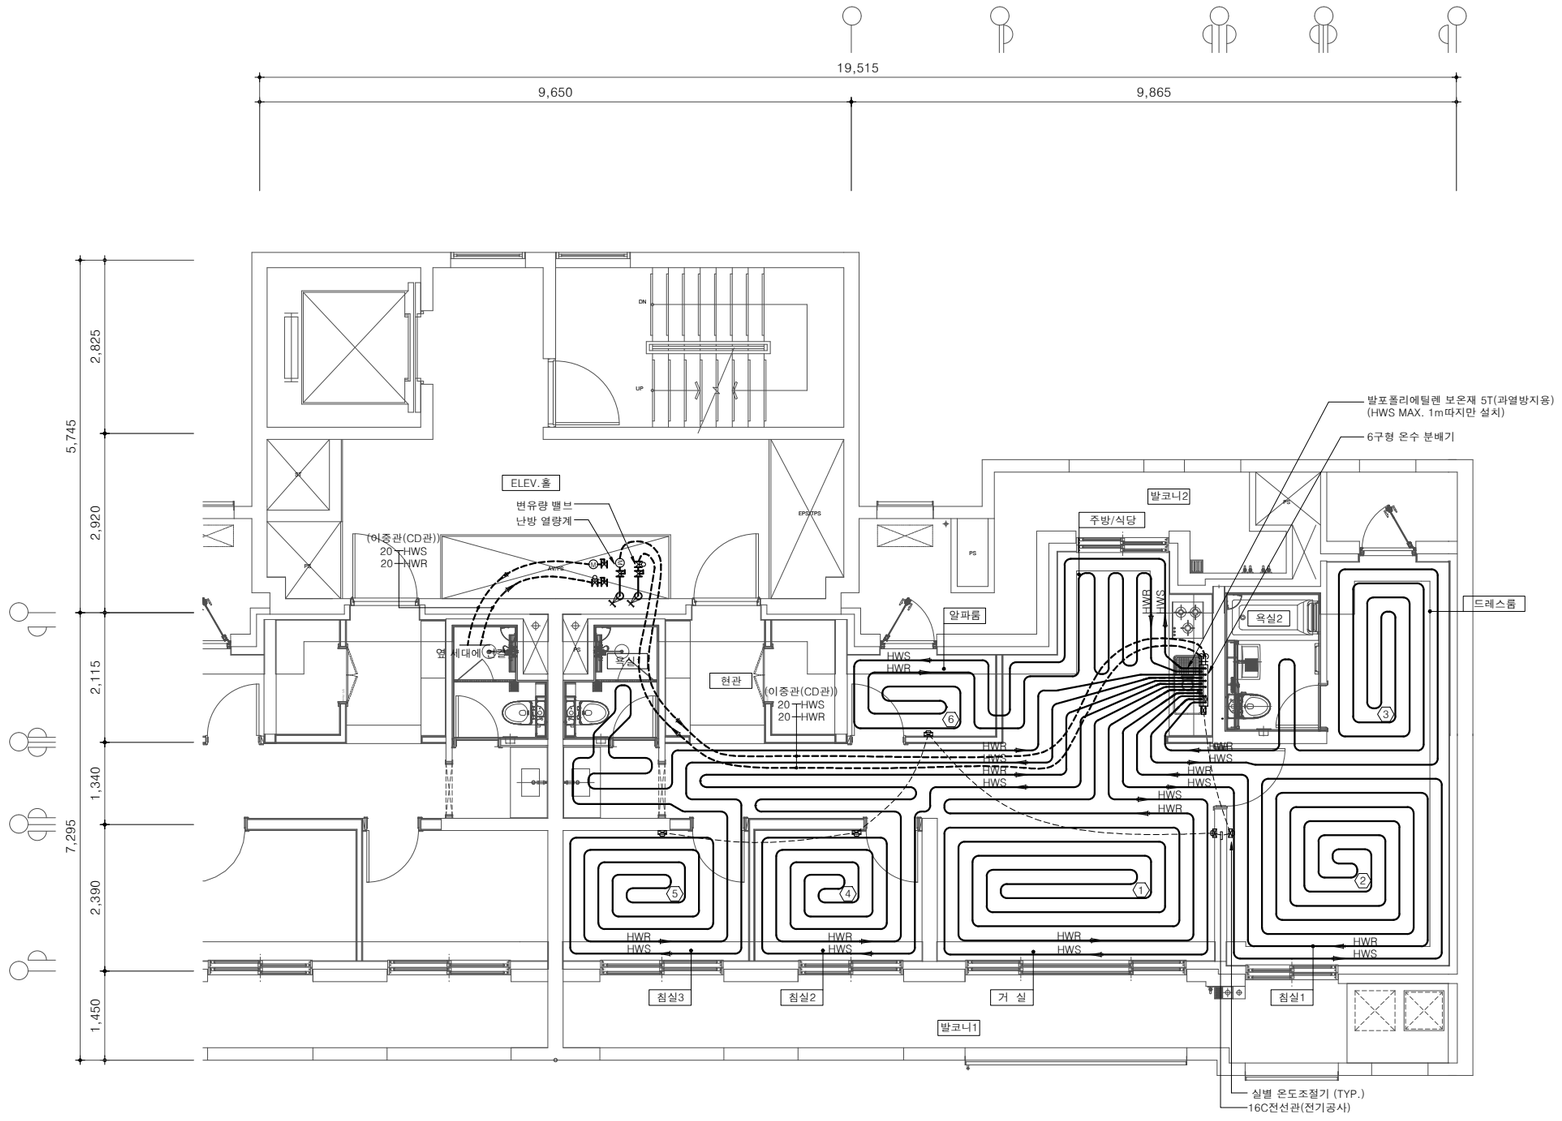

COIL SCHEDULE

번 호	실 명	코일간격(mm)	관경(Φ)	코일길이(m)	재질	비 고
①	거 실	230	15	61	PB	
②	침실1	230	15	60	PB	
③		230	15	40	PB	
④	침실2	230	15	53	PB	
⑤	침실3	230	15	59	PB	
⑥	알파룸	230	15	38	PB	

*보일러~온수분배기까지는 PB이중관 임.

M 84m²A형 단위세대 난방배관 평면도(기본형)

축 척 : 1/100

경기주택도시공사
GYEONGGI HOUSING & URBAN DEVELOPMENT CORPORATION

설계명 PROJECT TITLE

화성동탄(2)A76-2BL
민간참여 공동주택사업

주기 NOTE

1. 배관위치, 배관 및 밸브류 구경은 현장 여건에 따라 변경 될 수 있음.
2. 난방 코일길이, 조닝 및 벽체 이격거리는 현장여건에 따라 변경 가능.
3. 세대별 일괄 가동 정지가 가능하며, 실별 온도 제어가 가능한 자동 온도조절장치 설치.
4. 난방 공급관은 외벽측부터 공급해야하며, 환수관이 외벽측에 공급공급될 경우 온수분배기 하부에서 공급관과 환수관을 교차 시공한다.
5. 붙박이장 및 냉장고장 하부 등은 결로방지를 위해 난방코일을 적용하고 코일피치는 약 300mm로 하며 현장여건에 따라 변경 가능.
6. 실별 제어 조작 스위치는 전기스위치와 겸용으로 사용하며, 현장여건에 따라 유동적으로 변경될 수 있다.
7. 각 실별로 난방조닝이 2개로 나눠질 경우, 조작스위치 하나에서 연동하여 동시 제어가 되도록 한다.
8. 최상층, 최하층은 코일피치 200mm로 적용 한다.

NO	DATE	REVISION DESCRIPTION	APPD
△			
△			
△			
△			

설 계
DESIGN

대표전화

축 척	SCALE
A1	1 / 50
A3	1 / 100


일 자 DATE
2025. 12.

설계번호 PROJECT NO.
AR - 23 - 026

도면화일명 DWG. FILE NAME

도면번호 SHEET NO.
MH – 001

도면명 SUBJECT TITLE
84m²A형 단위세대
난방배관 평면도(기본형)

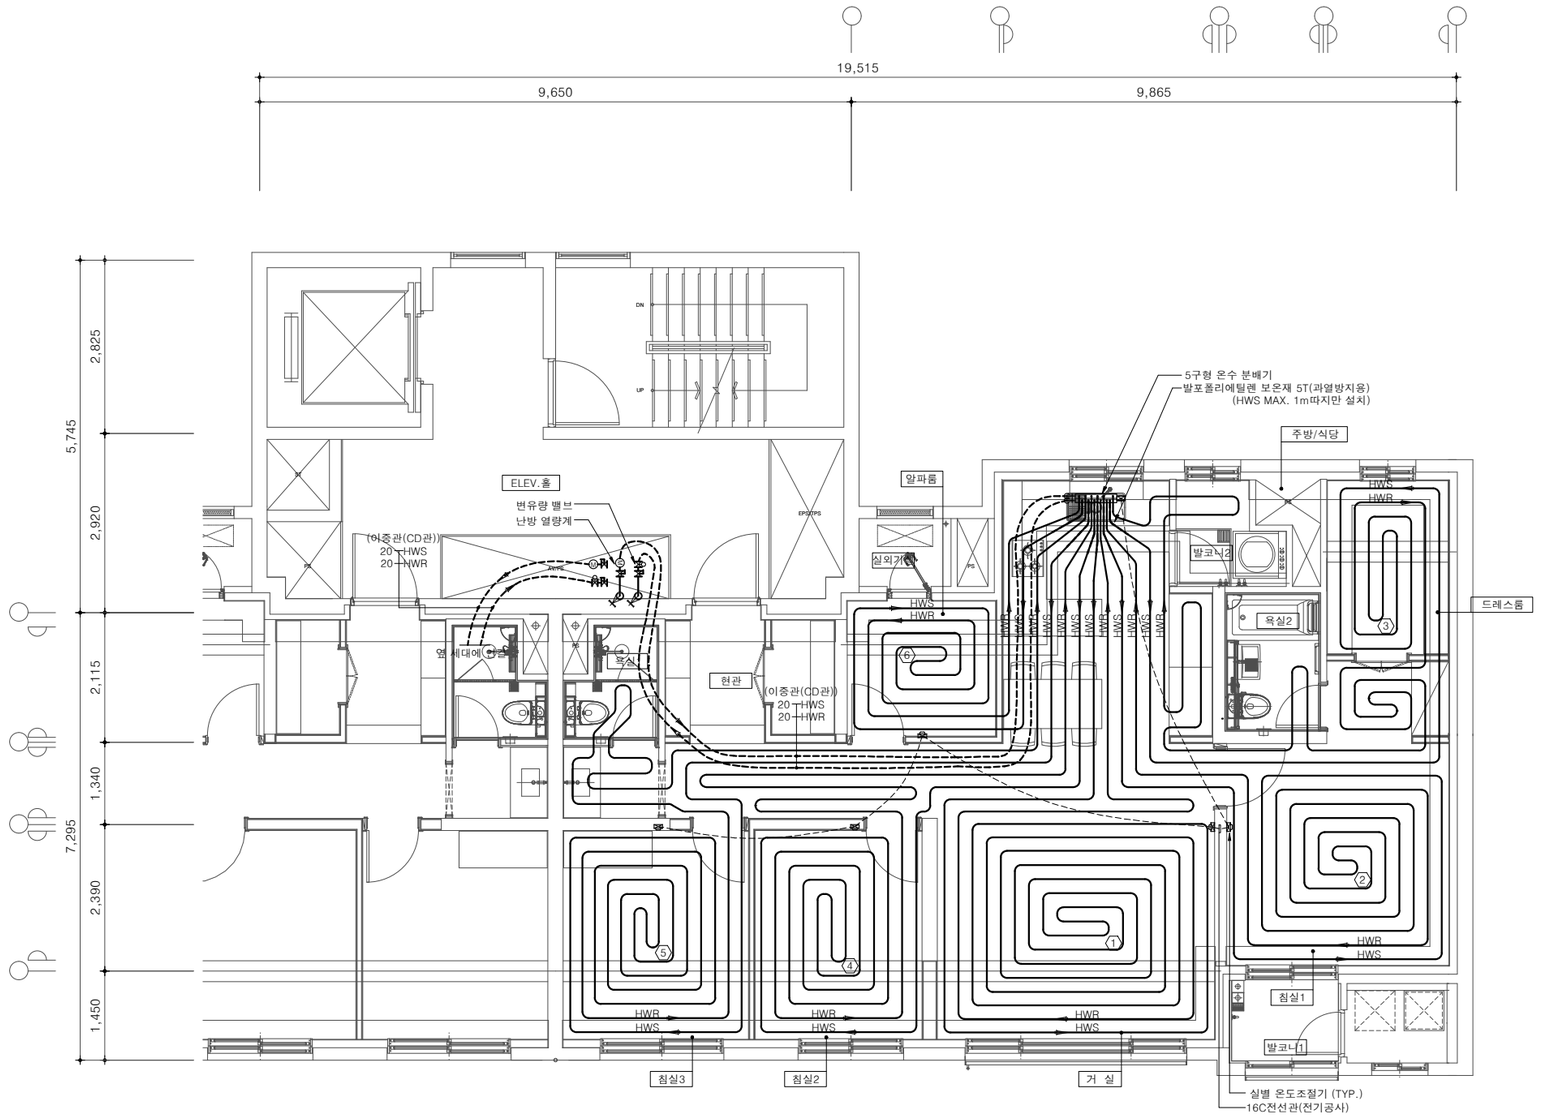

COIL SCHEDULE

번 호	실 명	코일간격(mm)	관경(Φ)	코일길이(m)	재질	비 고
①	거 실	230	15	91	PB	
②	침실1	230	15	64	PB	
③		230	15	64	PB	
④	침실2	230	15	70	PB	
⑤	침실3	230	15	79	PB	
⑥	알파룸	230	15	38	PB	
*보일러~온수분배기까지는 PB이중관 임.						

M 84m²A형 단위세대 난방배관 평면도(확장형)

축 척 : 1/100

경기주택도시공사
GYEONGGI HOUSING & URBAN DEVELOPMENT CORPORATION

설계명 PROJECT TITLE

화성동탄(2)A76-2BL
민간참여 공동주택사업

주기 NOTE

1. 배관위치, 배관 및 밸브류 구경은 현장 여건에 따라 변경 될 수 있음.
2. 난방 코일길이, 조닝 및 벽체 이격거리는 현장여건에 따라 변경 가능.
3. 세대별 일괄 가동 정지가 가능하며, 실별 온도 제어가 가능한 자동 온도조절장치 설치.
4. 난방 공급관은 외벽측부터 공급해야하며, 환수관이 외벽측에 공급될 경우 온수분배기 하부에서 공급관과 환수관을 교차 시공한다.
5. 붙박이장 및 냉장고장 하부 등은 결로방지를 위해 난방코일을 적용하고 코일피치는 약 300mm로 하며 현장여건에 따라 변경 가능.
6. 실별 제어 조작 스위치는 전기스위치와 겸용으로 사용하며, 현장여건에 따라 유동적으로 변경될 수 있다.
7. 각 실별로 난방조닝이 2개로 나눠질 경우, 조작스위치 하나에서 연동하여 동시 제어가 되도록 한다.
8. 최상층, 최하층은 코일피치 200mm로 적용 한다.

NO	DATE	REVISION DESCRIPTION	APPD
△			
△			
△			
△			

설 계
DESIGN

대표전화

축 척	SCALE
A1	1 / 50
A3	1 / 100


일 자 DATE
2025. 12.

설계번호 PROJECT NO.
AR - 23 - 026

도면화일명 DWG. FILE NAME

도면번호 SHEET NO.
MH - 002

도면명 SUBJECT TITLE
84m²A형 단위세대
난방배관 평면도(확장형)

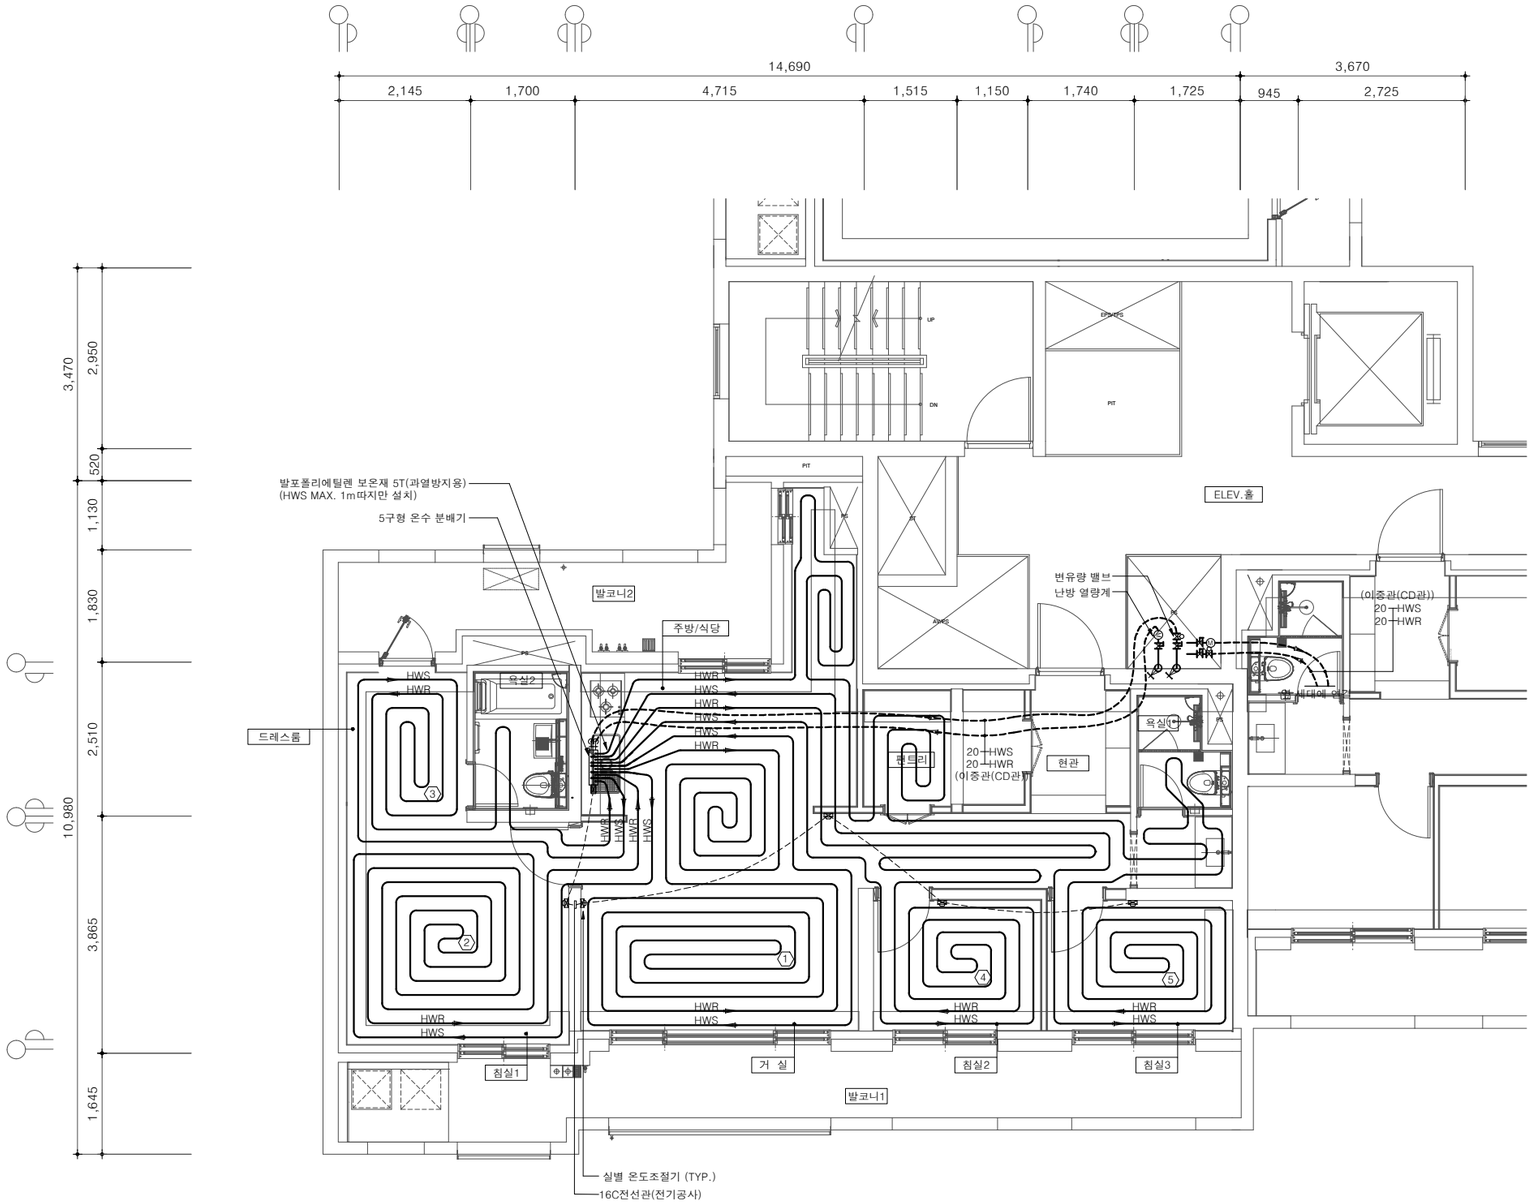

COIL SCHEDULE

번 호	실 명	코일간격(mm)	관경(Φ)	코일길이(m)	재질	비 고
①	거 실	230	15	76	PB	
②	침실1	230	15	58	PB	
③		230	15	41	PB	
④	침실2	230	15	55	PB	
⑤	침실3	230	15	85	PB	

*보일러~온수분배기까지는 PB이중관 임.

84m²B형 단위세대 난방배관 평면도(기본형)

축 척 : 1/100

경기주택도시공사
GYEONGGI HOUSING & URBAN DEVELOPMENT CORPORATION

설계명 PROJECT TITLE

화성동탄(2)A76-2BL
민간참여 공동주택사업

주기 NOTE

1. 배관위치, 배관 및 밸브류 구경은 현장 여건에 따라 변경 될 수 있음.
2. 난방 코일길이, 조닝 및 벽체 이격거리는 현장여건에 따라 변경 가능.
3. 세대별 일괄 가동 정지가 가능하며, 실별 온도 제어가 가능한 자동 온도조절장치 설치.
4. 난방 공급관은 외벽측부터 공급해야하며, 환수관이 외벽측에 공급될 경우 온수분배기 하부에서 공급관과 환수관을 교차 시공한다.
5. 붙박이장 및 냉장고장 하부 등은 결로방지를 위해 난방코일을 적용하고 코일피치는 약 300mm로 하며 현장여건에 따라 변경 가능.
6. 실별 제어 조작 스위치는 전기스위치와 겸용으로 사용하며, 현장여건에 따라 유동적으로 변경될 수 있다.
7. 각 실별로 난방조닝이 2개로 나눠질 경우, 조작스위치 하나에서 연동하여 동시 제어가 되도록 한다.
8. 최상층, 최하층은 코일피치 200mm로 적용 한다.

NO	DATE	REVISION DESCRIPTION	APPD

설 계
DESIGN

대표전화

축 척	SCALE
A1	1 / 50
A3	1 / 100


일 자 DATE
2025. 12.

설계번호 PROJECT NO.
AR - 23 - 026

도면화일명 DWG. FILE NAME

도면번호 SHEET NO.
MH - 003

도면명 SUBJECT TITLE
84m²B형 단위세대
난방배관 평면도(기본형)

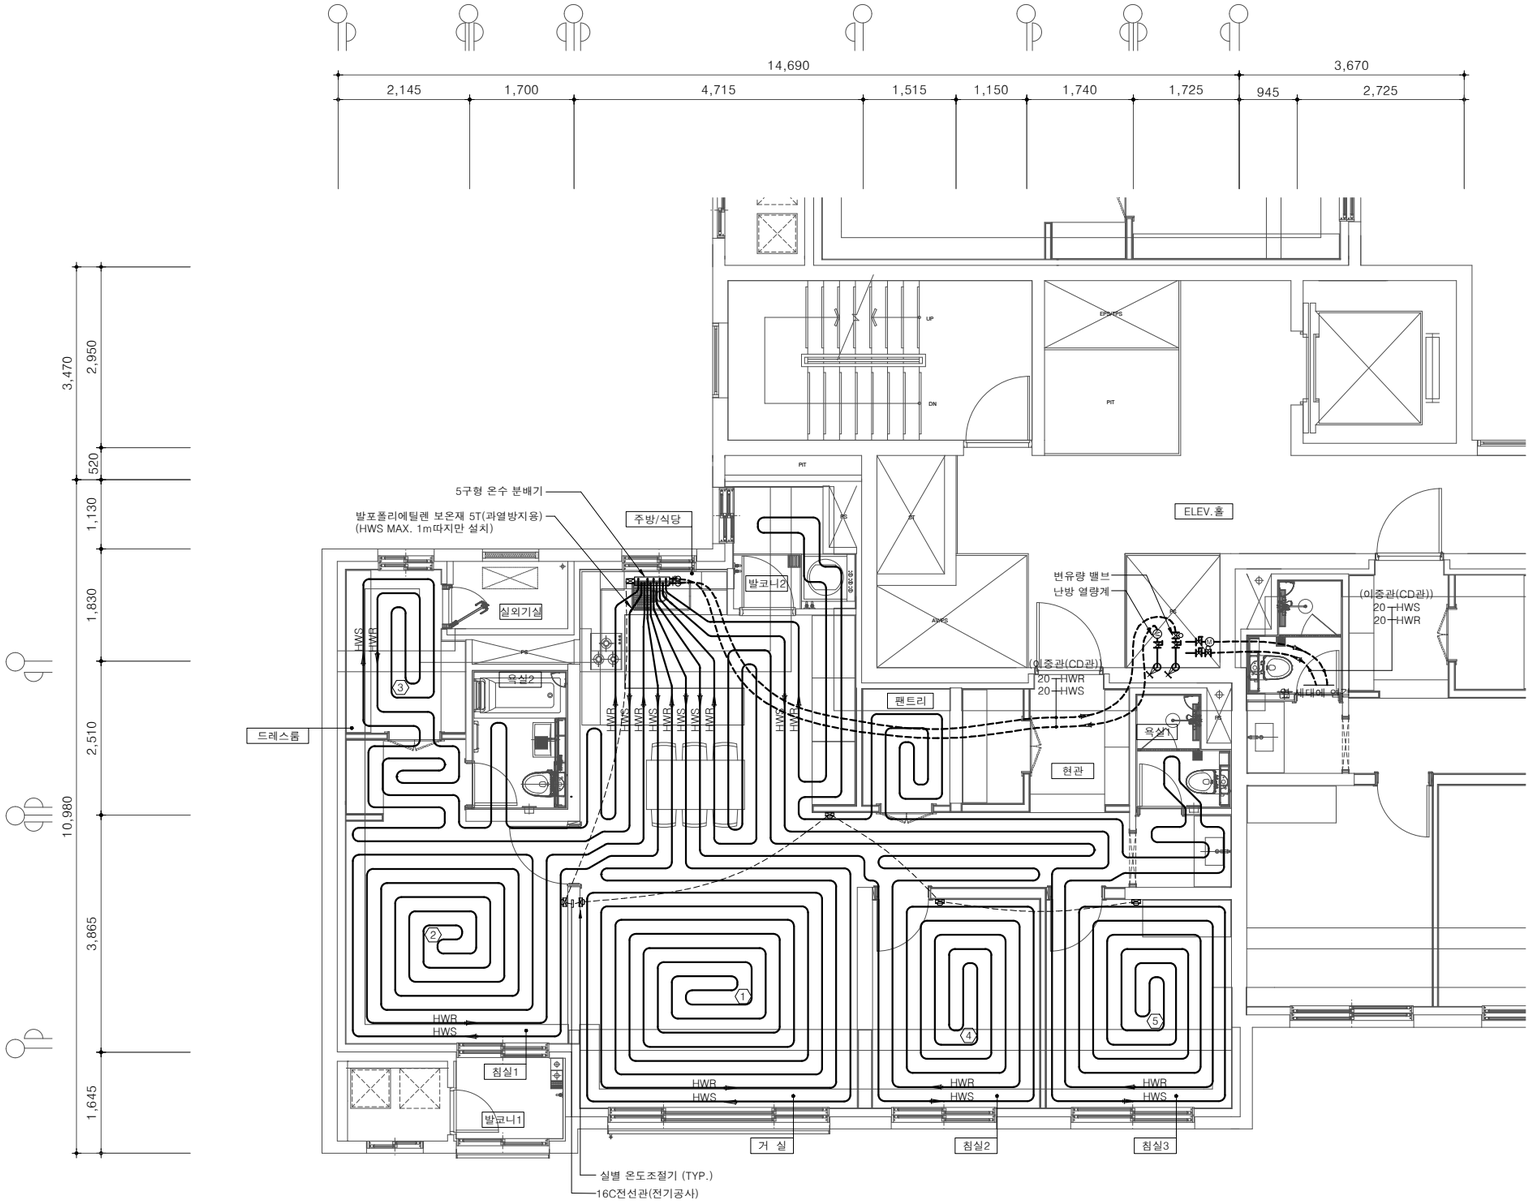

COIL SCHEDULE

번 호	실 명	코일간격(mm)	관경(Φ)	코일길이(m)	재질	비 고
①	거 실	230	15	91	PB	
②	침실1	230	15	63	PB	
③		230	15	50	PB	
④	침실2	230	15	82	PB	
⑤	침실3	230	15	100	PB	

*보일러~온수분배기까지는 PB이중관 임.

84m²B형 단위세대 난방배관 평면도(확장형)

축 척 : 1/100

경기주택도시공사

설계명 PROJECT TITLE

화성동탄(2)A76-2BL
민간참여 공동주택사업

주기 NOTE


1. 배관위치, 배관 및 밸브류 구경은 현장 여건에 따라 변경 될 수 있음.
2. 난방 코일길이, 조닝 및 벽체 이격거리는 현장여건에 따라 변경 가능.
3. 세대별 일괄 가동 정지가 가능하며, 실별 온도 제어가 가능한 자동 온도조절장치 설치.
4. 난방 공급관은 외벽측부터 공급해야하며, 환수관이 외벽측에 공급공급될 경우 온수분배기 하부에서 공급관과 환수관을 교차 시공한다.
5. 붙박이장 및 냉장고장 하부 등은 결로방지를 위해 난방코일을 적용하고 코일피치는 약 300mm로 하며 현장여건에 따라 변경 가능.
6. 실별 제어 조작 스위치는 전기스위치와 겸용으로 사용하며, 현장여건에 따라 유동적으로 변경될 수 있다.
7. 각 실별로 난방조닝이 2개로 나눠질 경우, 조작스위치 하나에서 연동하여 동시 제어가 되도록 한다.
8. 최상층, 최하층은 코일피치 200mm로 적용 한다.

NO	DATE	REVISION DESCRIPTION	APPD
△			
△			
△			
△			

설 계
DESIGN

대표전화

축 척	SCALE
A1	1 / 50
A3	1 / 100
일 자 DATE	2025. 12.
설계번호 PROJECT NO.	AR - 23 - 026
도면화일명 DWG. FILE NAME	
도면번호 SHEET NO.	MH - 004
도면명 SUBJECT TITLE	84m²B형 단위세대 난방배관 평면도(확장형)

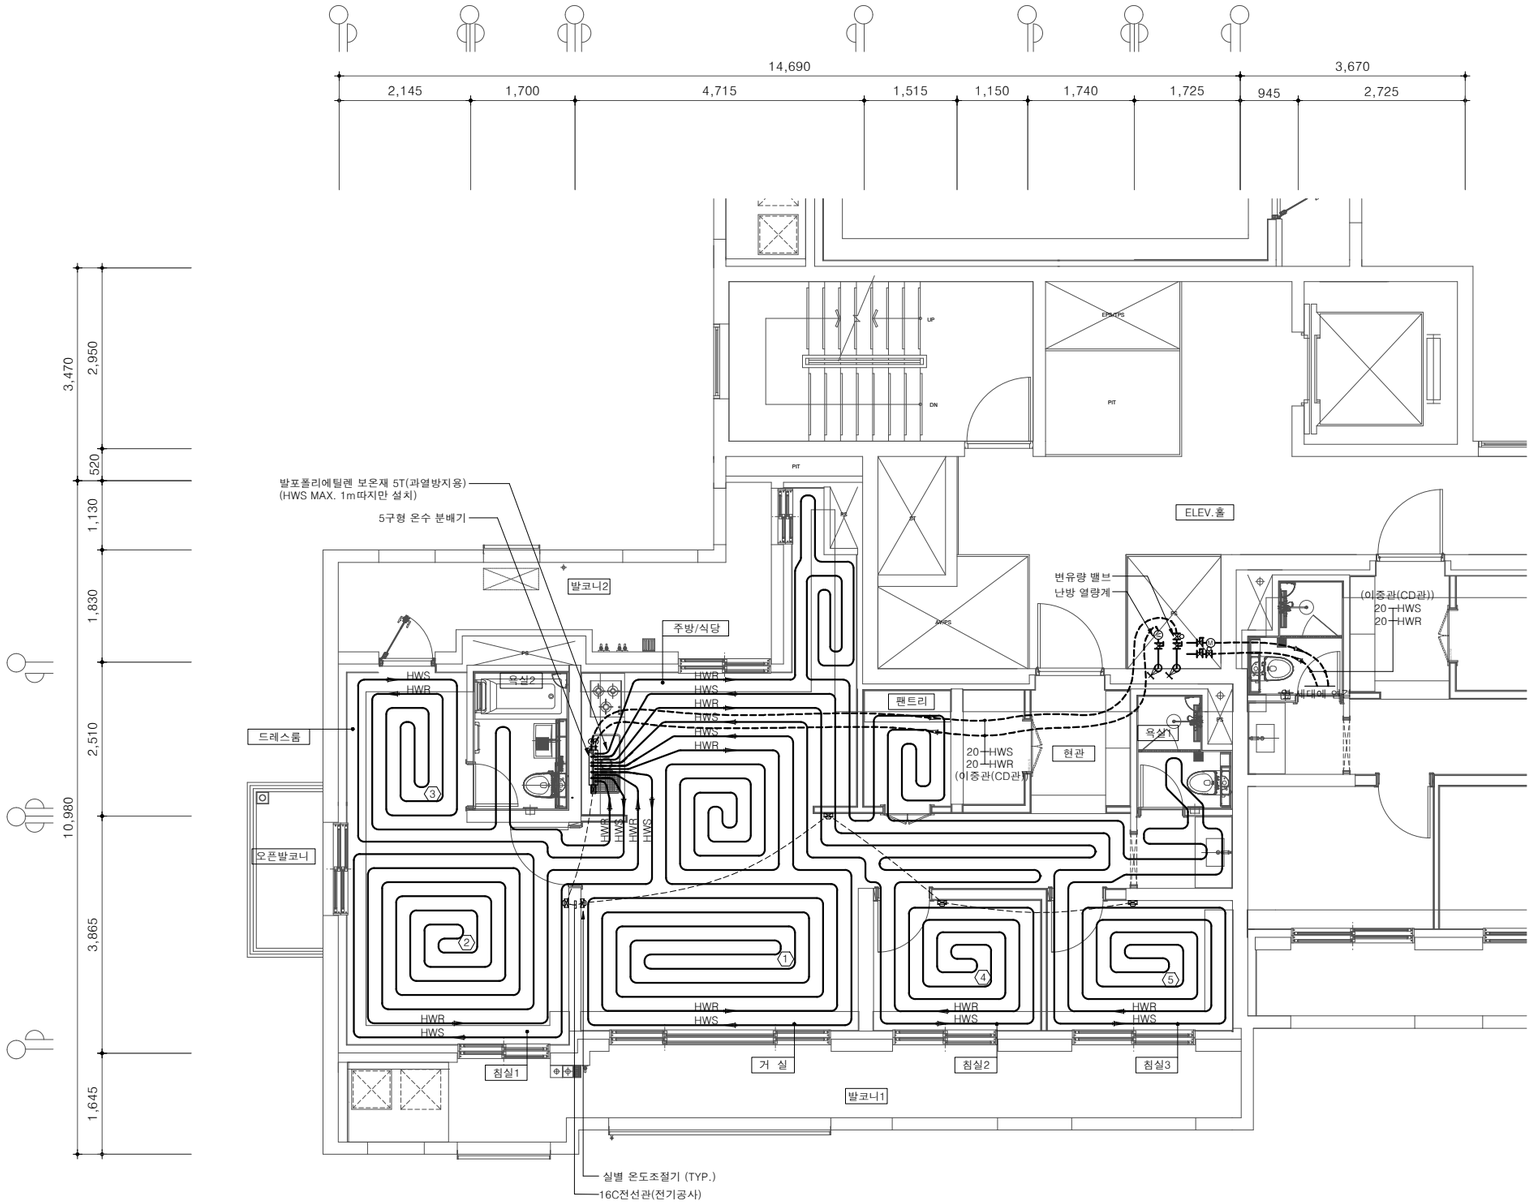

COIL SCHEDULE

번 호	실 명	코일간격(mm)	관경(Φ)	코일길이(m)	재질	비 고
①	거 실	230	15	76	PB	
②	침실1	230	15	58	PB	
③		230	15	41	PB	
④	침실2	230	15	55	PB	
⑤	침실3	230	15	85	PB	

*보일러~온수분배기까지는 PB이중관 임.

84m²C형 단위세대 난방배관 평면도(기본형)

축 척 : 1/100

경기주택도시공사
GYEONGGI HOUSING & URBAN DEVELOPMENT CORPORATION

설계명 PROJECT TITLE

화성동탄(2)A76-2BL
민간참여 공동주택사업


주기 NOTE

1. 배관위치, 배관 및 밸브류 구경은 현장 여건에 따라 변경 될 수 있음.
2. 난방 코일길이, 조닝 및 벽체 이격거리는 현장여건에 따라 변경 가능.
3. 세대별 일괄 가동 정지가 가능하며, 실별 온도 제어가 가능한 자동 온도조절장치 설치.
4. 난방 공급관은 외벽측부터 공급해야하며, 환수관이 외벽측에 공급공급될 경우 온수분배기 하부에서 공급관과 환수관을 교차 시공한다.
5. 붙박이장 및 냉장고장 하부 등은 결로방지를 위해 난방코일을 적용하고 코일피치는 약 300mm로 하며 현장여건에 따라 변경 가능.
6. 실별 제어 조작 스위치는 전기스위치와 겸용으로 사용하며, 현장여건에 따라 유동적으로 변경될 수 있다.
7. 각 실별로 난방조닝이 2개로 나눠질 경우, 조작스위치 하나에서 연동하여 동시 제어가 되도록 한다.
8. 최상층, 최하층은 코일피치 200mm로 적용 한다.

NO	DATE	REVISION DESCRIPTION	APPD

설 계
DESIGN

대표전화	
축 척	SCALE
A1	1 / 50
A3	1 / 100
일 자	DATE
	2025. 12.
설계번호	PROJECT NO.
	AR - 23 - 026
도면화일명	DWG. FILE NAME
도면번호	SHEET NO.
	MH - 005
도면명	SUBJECT TITLE
	84m²C형 단위세대 난방배관 평면도(기본형)

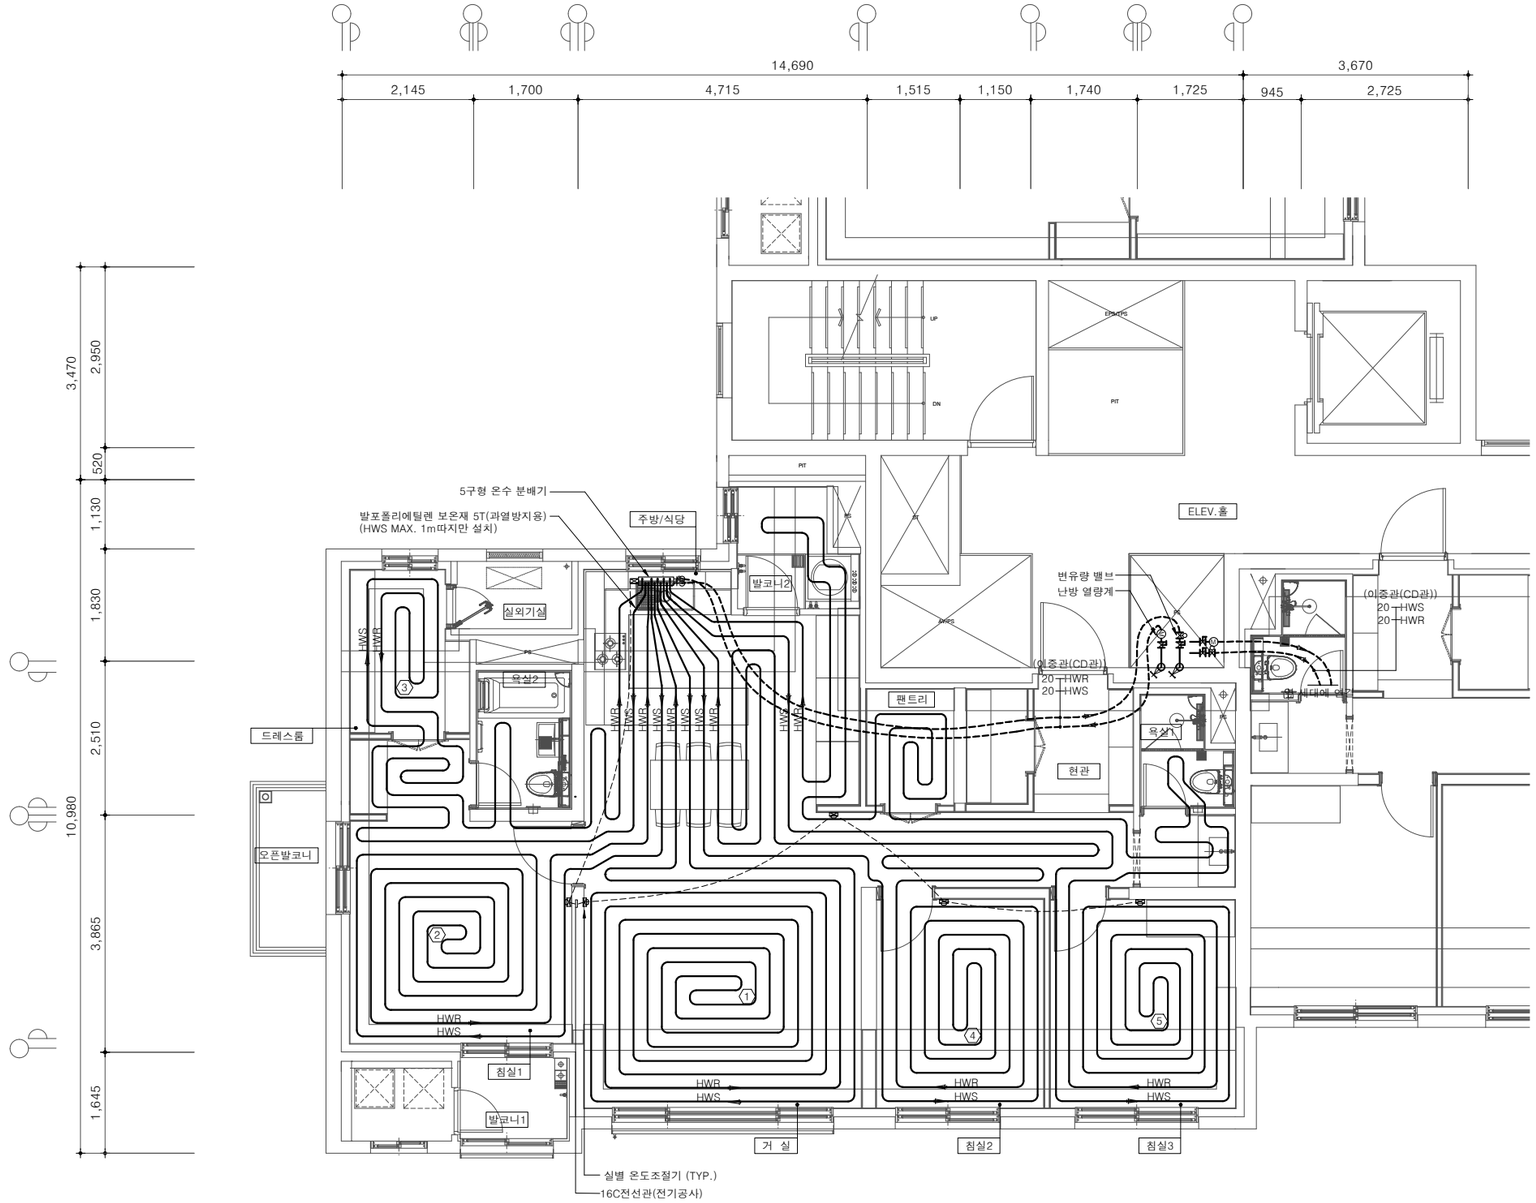

COIL SCHEDULE

번 호	실 명	코일간격(mm)	관경(Φ)	코일길이(m)	재질	비 고
①	거 실	230	15	91	PB	
②	침실1	230	15	63	PB	
③		230	15	50	PB	
④	침실2	230	15	82	PB	
⑤	침실3	230	15	100	PB	

*보일러~온수분배기까지는 PB이중관 임.

M 84m²C형 단위세대 난방배관 평면도(확장형)

축 척 : 1/100

경기주택도시공사
GYEONGGI HOUSING & URBAN DEVELOPMENT CORPORATION

설계명 PROJECT TITLE

화성동탄(2)A76-2BL
민간참여 공동주택사업

주기 NOTE

1. 배관위치, 배관 및 밸브류 구경은 현장 여건에 따라 변경 될 수 있음.
2. 난방 코일길이, 조닝 및 벽체 이격거리는 현장여건에 따라 변경 가능.
3. 세대별 일괄 가동 정지가 가능하며, 실별 온도 제어가 가능한 자동 온도조절장치 설치.
4. 난방 공급관은 외벽측부터 공급해야하며, 환수관이 외벽측에 공급공급될 경우 온수분배기 하부에서 공급관과 환수관을 교차 시공한다.
5. 붙박이장 및 냉장고장 하부 등은 결로방지를 위해 난방코일을 적용하고 코일피치는 약 300mm로 하며 현장여건에 따라 변경 가능.
6. 실별 제어 조작 스위치는 전기스위치와 겸용으로 사용하며, 현장여건에 따라 유동적으로 변경될 수 있다.
7. 각 실별로 난방조닝이 2개로 나눠질 경우, 조작스위치 하나에서 연동하여 동시 제어가 되도록 한다.
8. 최상층, 최하층은 코일피치 200mm로 적용 한다.

NO	DATE	REVISION DESCRIPTION	APPD
△			
△			
△			
△			
△			

설 계
DESIGN

대표전화

축 척	SCALE
A1	1 / 50
A3	1 / 100


일 자 DATE
2025. 12.

설계번호 PROJECT NO.
AR - 23 - 026

도면화일명 DWG. FILE NAME

도면번호 SHEET NO.
MH – 006

도면명 SUBJECT TITLE
84m²C형 단위세대
난방배관 평면도(확장형)

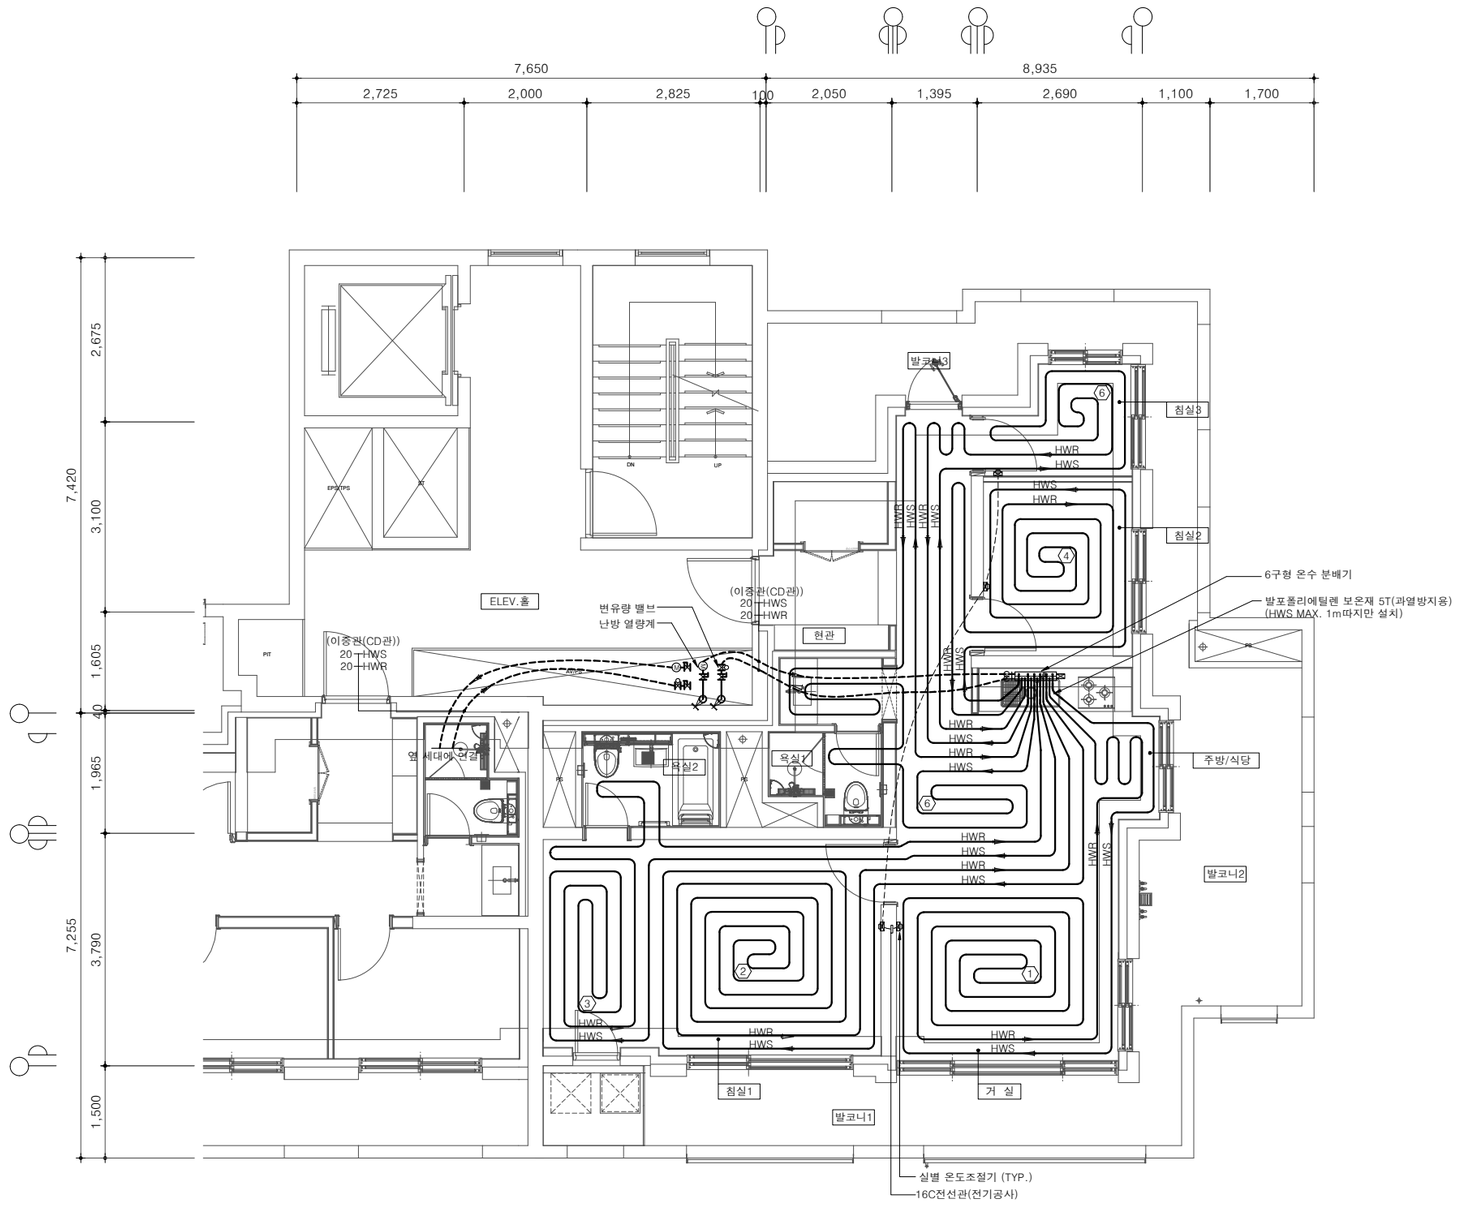

COIL SCHEDULE

번 호	실 명	코일간격(mm)	관경(Φ)	코일길이(m)	재질	비 고
①	거 실	230	15	58	PB	
②	침실1	230	15	65	PB	
③		230	15	51	PB	
④	침실2	230	15	43	PB	
⑤	침실3	230	15	34	PB	
⑥	복 도	230	15	35	PB	

*보일러~온수분배기까지는 PB이중관 임.

84m²D형 단위세대 난방배관 평면도(기본형)

축 척 : 1/100

경기주택도시공사
GYEONGGI HOUSING & URBAN DEVELOPMENT CORPORATION

설계명 PROJECT TITLE

화성동탄(2)A76-2BL
민간참여 공동주택사업

주기 NOTE

1. 배관위치, 배관 및 밸브류 구경은 현장 여건에 따라 변경 될 수 있음.
2. 난방 코일길이, 조닝 및 벽체 이격거리는 현장여건에 따라 변경 가능.
3. 세대별 일괄 가동 정지가 가능하며, 실별 온도 제어가 가능한 자동 온도조절장치 설치.
4. 난방 공급관은 외벽측부터 공급해야하며, 환수관이 외벽측에 공급공급될 경우 온수분배기 하부에서 공급관과 환수관을 교차 시공한다.
5. 붙박이장 및 냉장고장 하부 등은 결로방지를 위해 난방코일을 적용하고 코일피치는 약 300mm로 하며 현장여건에 따라 변경 가능.
6. 실별 제어 조작 스위치는 전기스위치와 겸용으로 사용하며, 현장여건에 따라 유동적으로 변경될 수 있다.
7. 각 실별로 난방조닝이 2개로 나눠질 경우, 조작스위치 하나에서 연동하여 동시 제어가 되도록 한다.
8. 최상층, 최하층은 코일피치 200mm로 적용 한다.

NO	DATE	REVISION DESCRIPTION	APPD
△			
△			
△			
△			
△			

설 계
DESIGN

대표전화

축 척	SCALE
A1	1 / 50
A3	1 / 100


일 자 DATE
2025. 12.

설계번호 PROJECT NO.
AR - 23 - 026

도면화일명 DWG. FILE NAME

도면번호 SHEET NO.
MH – 007

도면명 SUBJECT TITLE
84m²D형 단위세대
난방배관 평면도(기본형)

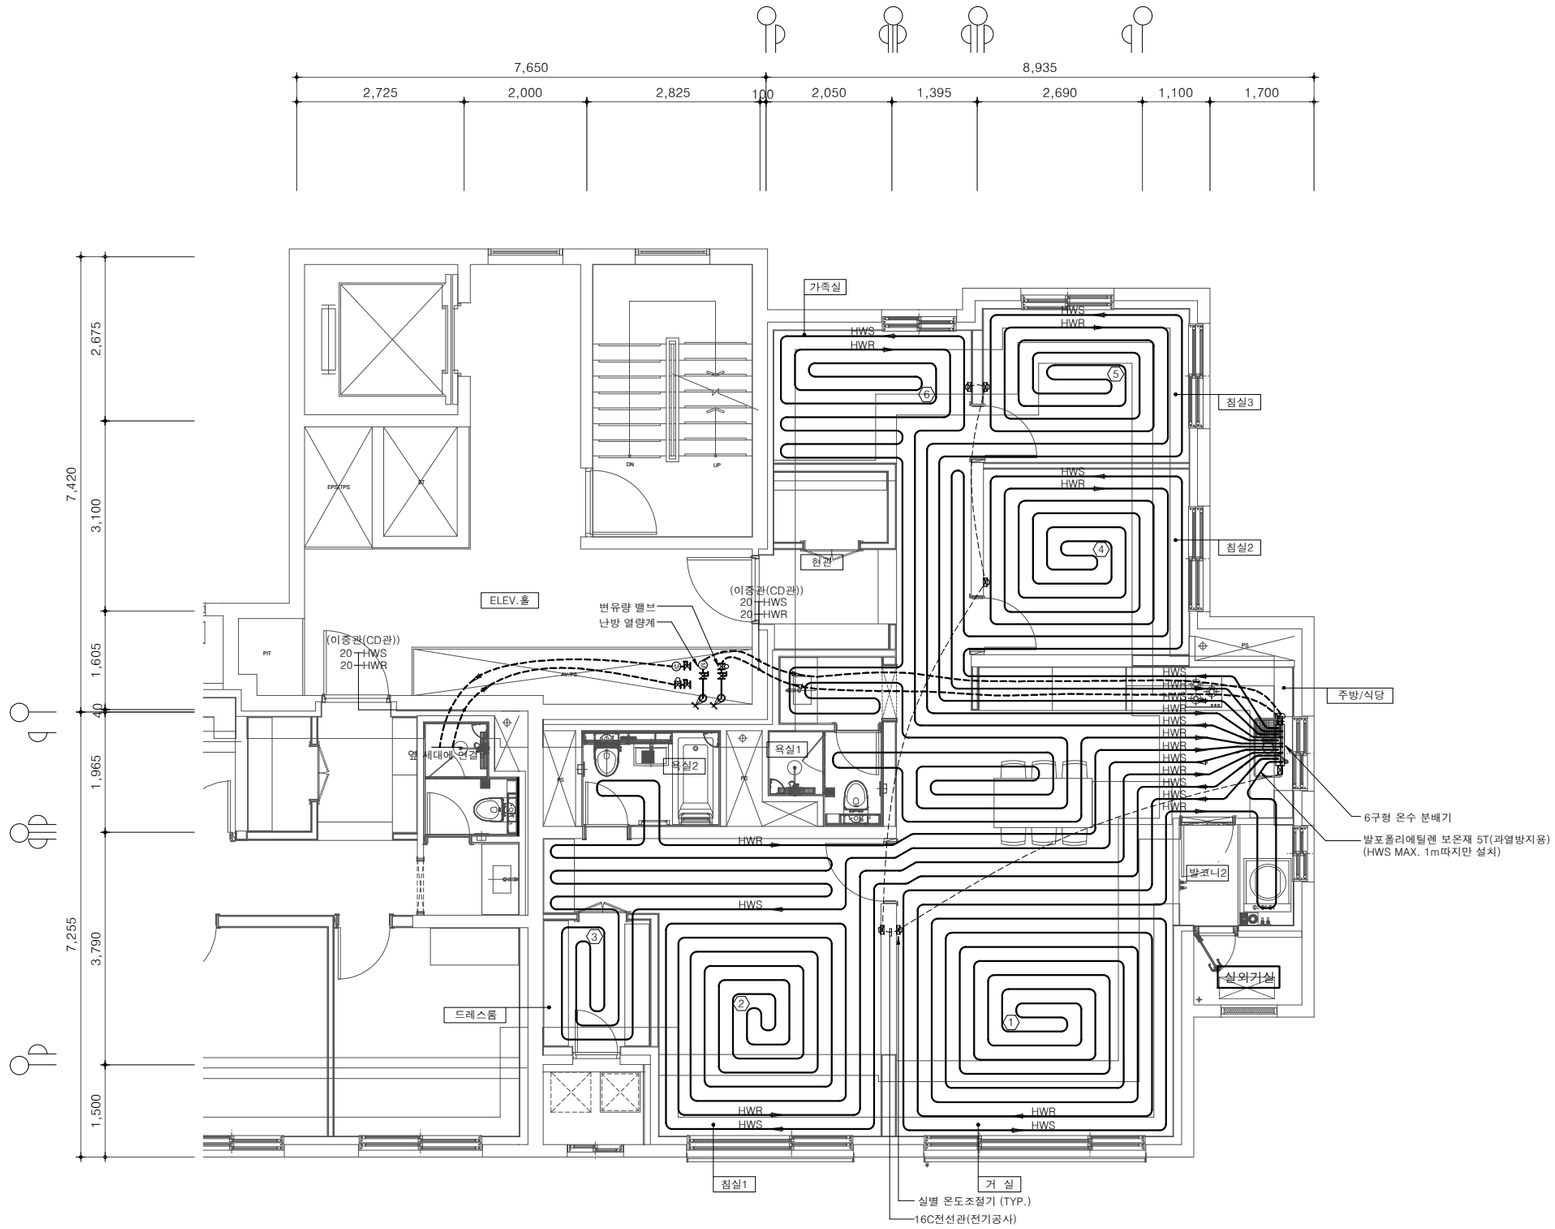

COIL SCHEDULE

번 호	실 명	코일간격(mm)	관경(Φ)	코일길이(m)	재질	비 고
①	거 실	230	15	93	PB	
②	침실1	230	15	76	PB	
③		230	15	64	PB	
④	침실2	230	15	66	PB	
⑤	침실3	230	15	62	PB	
⑥	가족실	230	15	77	PB	
*보일러~온수분배기까지는 PB이중관 임.						

84m²D형 단위세대 난방배관 평면도(확장형)

축 척 : 1/100

경기주택도시공사
GYEONGGI HOUSING & URBAN DEVELOPMENT CORPORATION

설계명 PROJECT TITLE

화성동탄(2)A76-2BL
민간참여 공동주택사업

주기 NOTE

1. 배관위치, 배관 및 밸브류 구경은 현장 여건에 따라 변경 될 수 있음.
2. 난방 코일길이, 조닝 및 벽체 이격거리는 현장여건에 따라 변경 가능.
3. 세대별 일괄 가동 정지가 가능하며, 실별 온도 제어가 가능한 자동 온도조절장치 설치.
4. 난방 공급관은 외벽측부터 공급해야하며, 환수관이 외벽측에 공급될 경우 온수분배기 하부에서 공급관과 환수관을 교차 시공한다.
5. 붙박이장 및 냉장고장 하부 등은 결로방지를 위해 난방코일을 적용하고 코일피치는 약 300mm로 하며 현장여건에 따라 변경 가능.
6. 실별 제어 조작 스위치는 전기스위치와 겸용으로 사용하며, 현장여건에 따라 유동적으로 변경될 수 있다.
7. 각 실별로 난방조닝이 2개로 나눠질 경우, 조작스위치 하나에서 연동하여 동시 제어가 되도록 한다.
8. 최상층, 최하층은 코일피치 200mm로 적용 한다.

NO	DATE	REVISION DESCRIPTION	APPD
△			
△			
△			
△			

설 계
DESIGN

대표전화

축 척	SCALE
A1	1 / 50
A3	1 / 100


일 자 DATE
2025. 12.

설계번호 PROJECT NO.
AR - 23 - 026

도면화일명 DWG. FILE NAME

도면번호 SHEET NO.
MH - 008

도면명 SUBJECT TITLE
84m²D형 단위세대
난방배관 평면도(확장형)

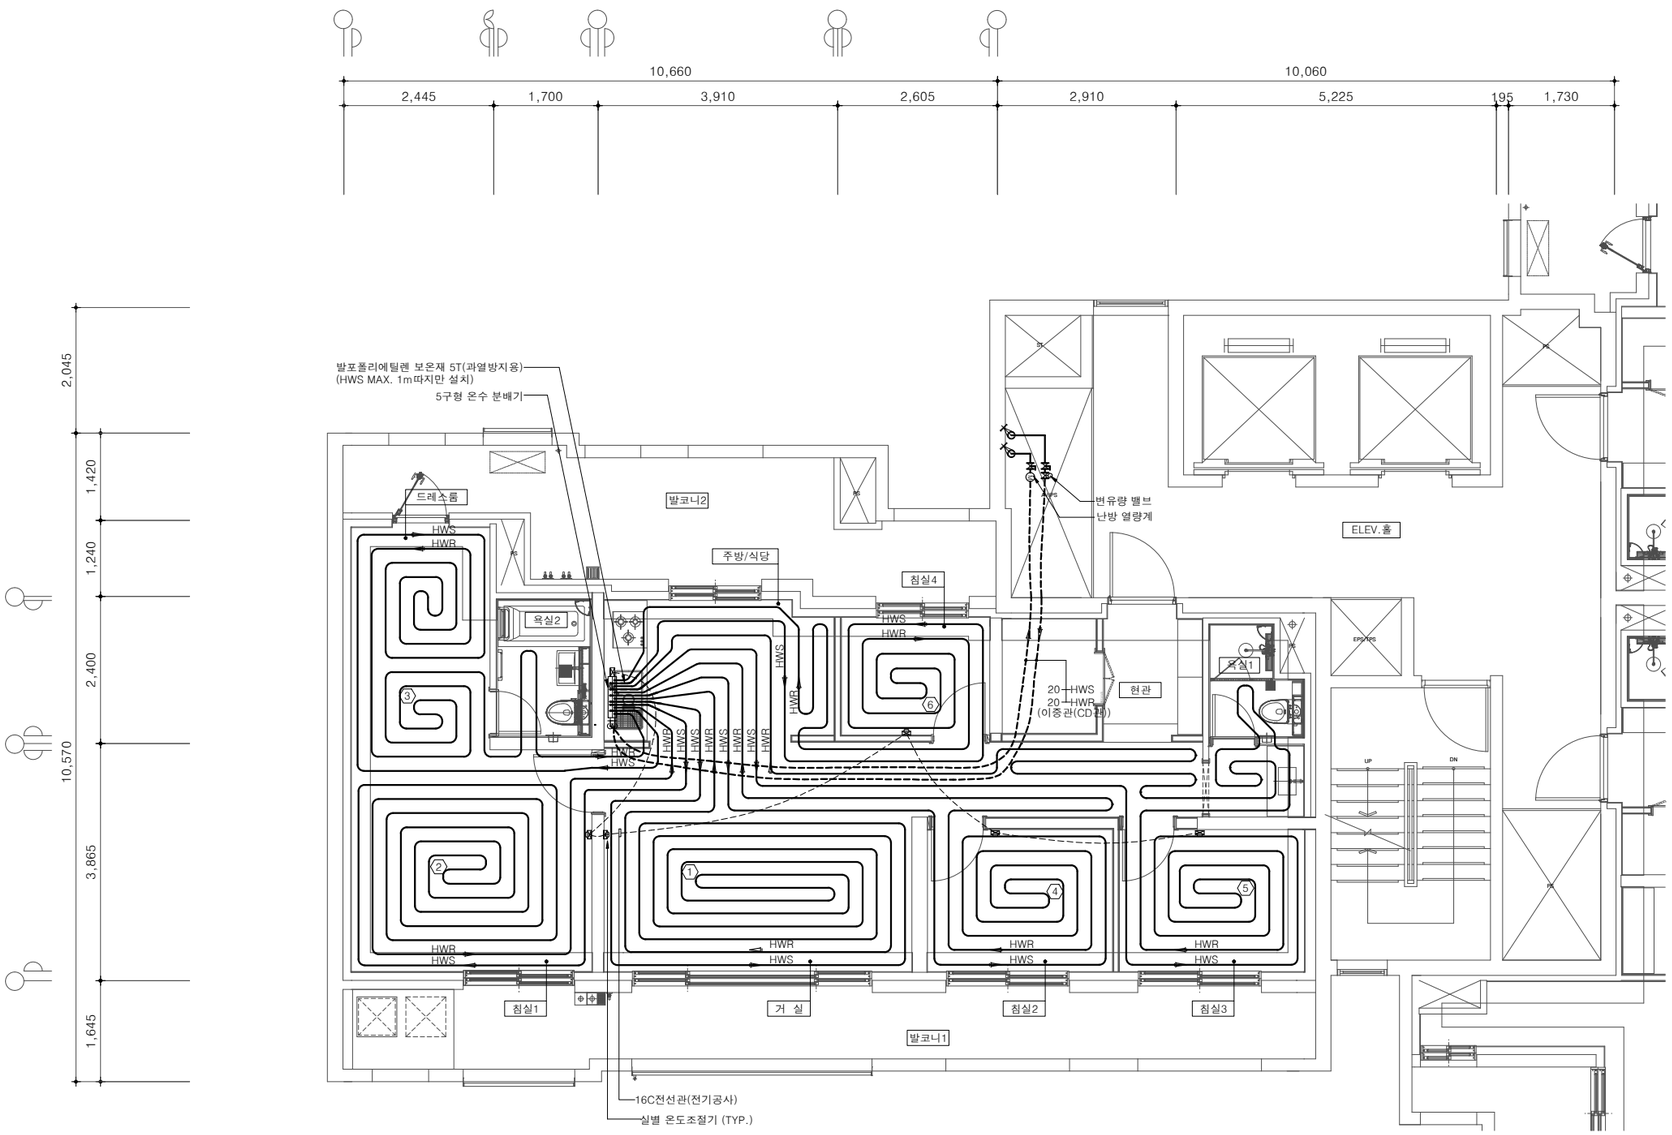

COIL SCHEDULE

번 호	실 명	코일간격(mm)	관경(Φ)	코일길이(m)	재질	비 고
①	거 실	230	15	69	PB	
②	침실1	230	15	63	PB	
③		230	15	52	PB	
④	침실2	230	15	53	PB	
⑤	침실3	230	15	72	PB	
⑥	침실4	230	15	43	PB	

*보일러~온수분배기까지는 PB이중관 임.

M 97m²A형 단위세대 난방배관 평면도(기본형)

축 척 : 1/100

경기주택도시공사
GYEONGGI HOUSING & URBAN DEVELOPMENT CORPORATION

설계명 PROJECT TITLE

화성동탄(2)A76-2BL
민간참여 공동주택사업

주기 NOTE

1. 배관위치, 배관 및 밸브류 구경은 현장 여건에 따라 변경 될 수 있음.
2. 난방 코일길이, 조닝 및 벽체 이격거리는 현장여건에 따라 변경 가능.
3. 세대별 일괄 가동 정지가 가능하며, 실별 온도 제어가 가능한 자동 온도조절장치 설치.
4. 난방 공급관은 외벽측부터 공급해야하며, 환수관이 외벽측에 공급공급될 경우 온수분배기 하부에서 공급관과 환수관을 교차 시공한다.
5. 붙박이장 및 냉장고장 하부 등은 결로방지를 위해 난방코일을 적용하고 코일피치는 약 300mm로 하며 현장여건에 따라 변경 가능.
6. 실별 제어 조작 스위치는 전기스위치와 겸용으로 사용하며, 현장여건에 따라 유동적으로 변경될 수 있다.
7. 각 실별로 난방조닝이 2개로 나눠질 경우, 조작스위치 하나에서 연동하여 동시 제어가 되도록 한다.
8. 최상층, 최하층은 코일피치 200mm로 적용 한다.

NO	DATE	REVISION DESCRIPTION	APPD

설 계
DESIGN

대표전화

축 척	SCALE
A1	1 / 50
A3	1 / 100


일 자 DATE
2025. 12.

설계번호 PROJECT NO.
AR - 23 - 026

도면화일명 DWG. FILE NAME

도면번호 SHEET NO.
MH - 009

도면명 SUBJECT TITLE
97m²A형 단위세대
난방배관 평면도(기본형)

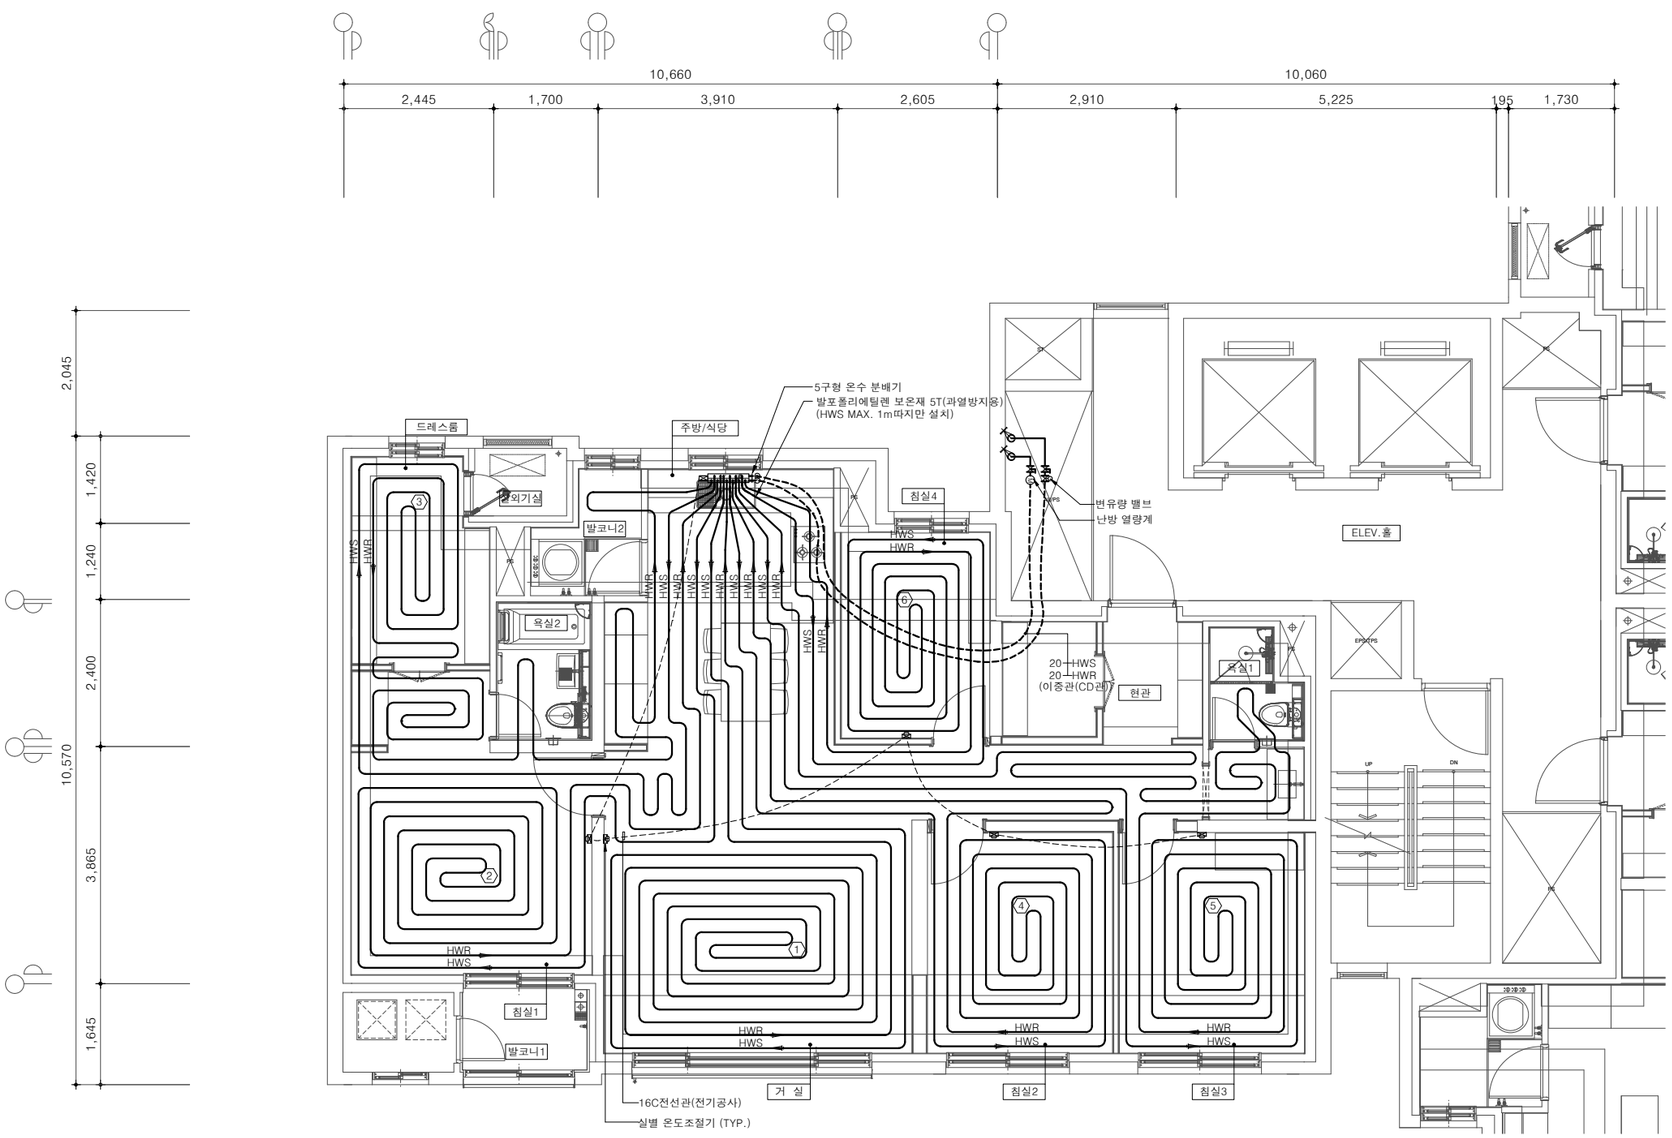

COIL SCHEDULE

번 호	실 명	코일간격(mm)	관경(Φ)	코일길이(m)	재질	비 고
①	거 실	230	15	96	PB	
②	침실1	230	15	74	PB	
③		230	15	75	PB	
④	침실2	230	15	73	PB	
⑤	침실3	230	15	91	PB	
⑥	침실4	230	15	57	PB	
*보일러~온수분배기까지는 PB이중관 임.						

97m²A형 단위세대 난방배관 평면도(확장형)

축 척 : 1/100

경기주택도시공사
GYEONGGI HOUSING & URBAN DEVELOPMENT CORPORATION

설계명 PROJECT TITLE

화성동탄(2)A76-2BL
민간참여 공동주택사업

주기 NOTE

1. 배관위치, 배관 및 밸브류 구경은 현장 여건에 따라 변경 될 수 있음.
2. 난방 코일길이, 조닝 및 벽체 이격거리는 현장여건에 따라 변경 가능.
3. 세대별 일괄 가동 정지가 가능하며, 실별 온도 제어가 가능한 자동 온도조절장치 설치.
4. 난방 공급관은 외벽측부터 공급해야하며, 환수관이 외벽측에 공급될 경우 온수분배기 하부에서 공급관과 환수관을 교차 시공한다.
5. 붙박이장 및 냉장고장 하부 등은 결로방지를 위해 난방코일을 적용하고 코일피치는 약 300mm로 하며 현장여건에 따라 변경 가능.
6. 실별 제어 조작 스위치는 전기스위치와 겸용으로 사용하며, 현장여건에 따라 유동적으로 변경될 수 있다.
7. 각 실별로 난방조닝이 2개로 나눠질 경우, 조작스위치 하나에서 연동하여 동시 제어가 되도록 한다.
8. 최상층, 최하층은 코일피치 200mm로 적용 한다.

NO	DATE	REVISION DESCRIPTION	APPD

설 계
DESIGN

대표전화

축 척	SCALE
A1	1 / 50
A3	1 / 100


일 자 DATE
2025. 12.

설계번호 PROJECT NO.
AR - 23 - 026

도면화일명 DWG. FILE NAME

도면번호 SHEET NO.
MH - 010

도면명 SUBJECT TITLE
97m²A형 단위세대
난방배관 평면도(확장형)

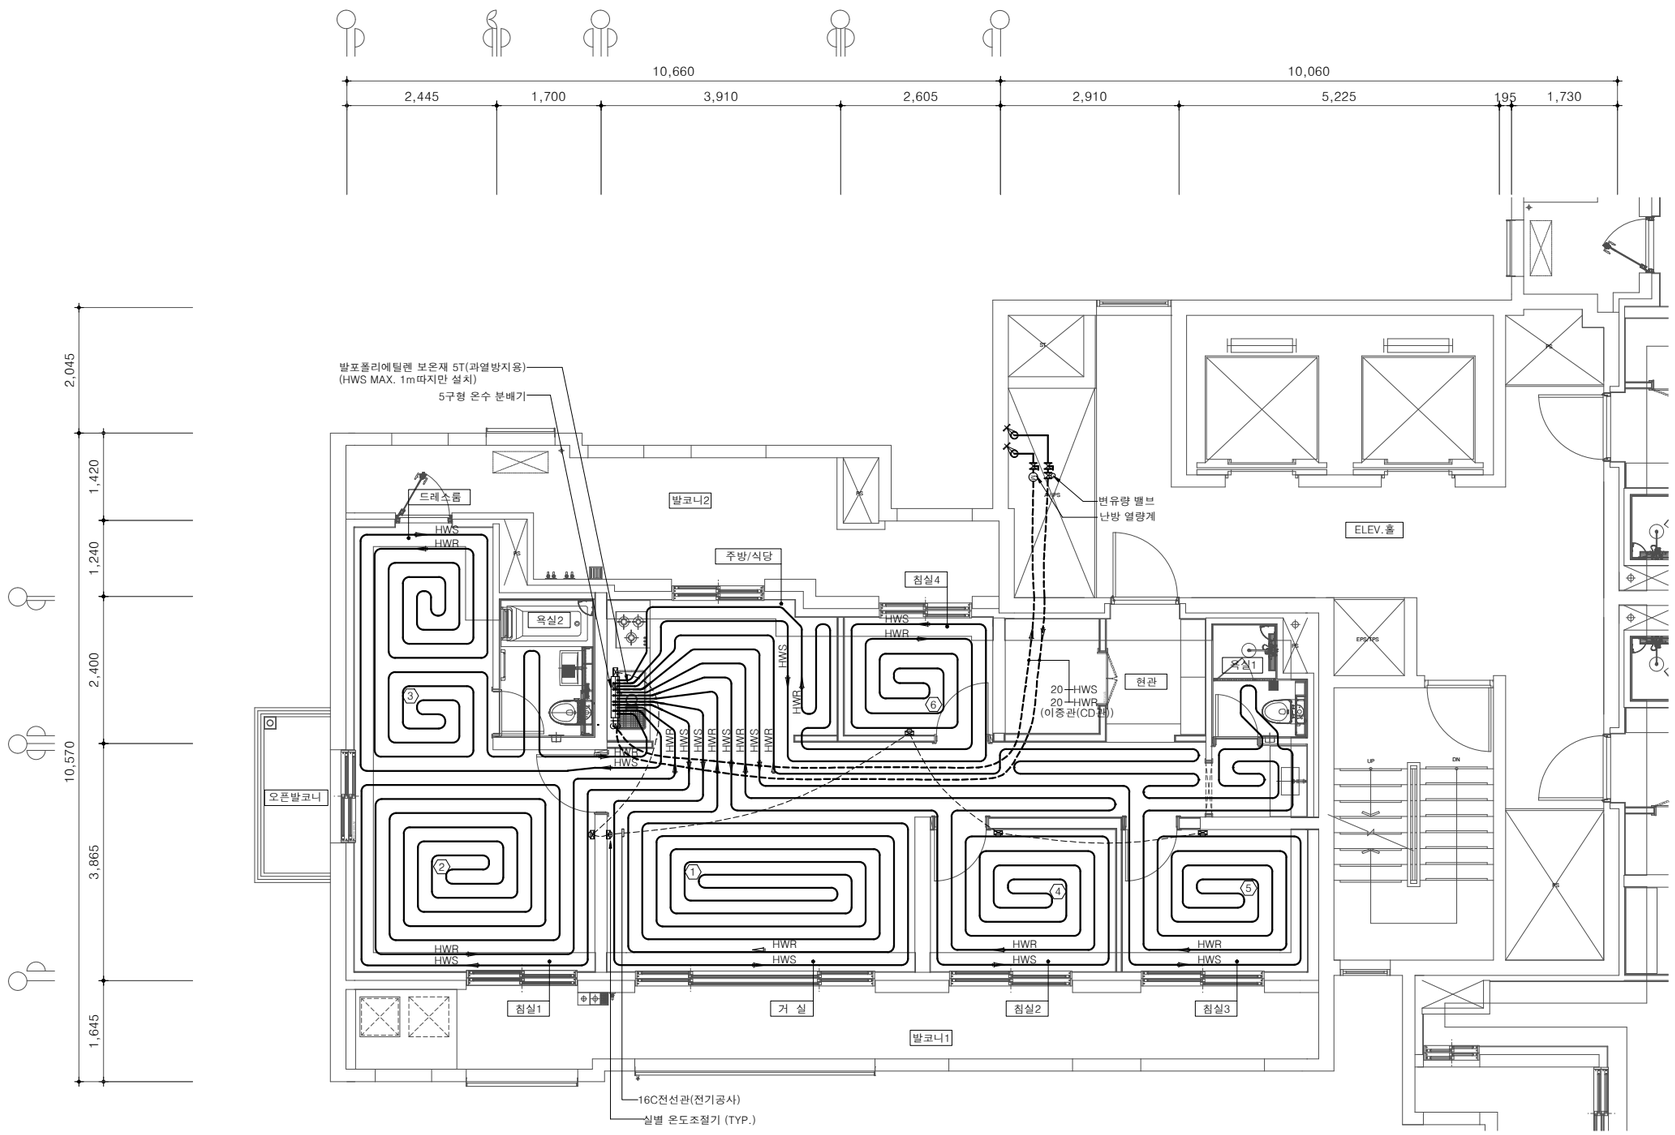

COIL SCHEDULE

번 호	실 명	코일간격(mm)	관경(Φ)	코일길이(m)	재질	비 고
①	거 실	230	15	69	PB	
②	침실1	230	15	63	PB	
③		230	15	52	PB	
④	침실2	230	15	53	PB	
⑤	침실3	230	15	72	PB	
⑥	침실4	230	15	43	PB	

*보일러~온수분배기까지는 PB이중관 임.

M 97m²B형 단위세대 난방배관 평면도(기본형)

축 척 : 1/100

경기주택도시공사
GYEONGGI HOUSING & URBAN DEVELOPMENT CORPORATION

설계명 PROJECT TITLE

화성동탄(2)A76-2BL
민간참여 공동주택사업

주기 NOTE


1. 배관위치, 배관 및 밸브류 구경은 현장 여건에 따라 변경 될 수 있음.
2. 난방 코일길이, 조닝 및 벽체 이격거리는 현장여건에 따라 변경 가능.
3. 세대별 일괄 가동 정지가 가능하며, 실별 온도 제어가 가능한 자동 온도조절장치 설치.
4. 난방 공급관은 외벽측부터 공급해야하며, 환수관이 외벽측에 공급될 경우 온수분배기 하부에서 공급관과 환수관을 교차 시공한다.
5. 붙박이장 및 냉장고장 하부 등은 결로방지를 위해 난방코일을 적용하고 코일피치는 약 300mm로 하며 현장여건에 따라 변경 가능.
6. 실별 제어 조작 스위치는 전기스위치와 겸용으로 사용하며, 현장여건에 따라 유동적으로 변경될 수 있다.
7. 각 실별로 난방조닝이 2개로 나눠질 경우, 조작스위치 하나에서 연동하여 동시 제어가 되도록 한다.
8. 최상층, 최하층은 코일피치 200mm로 적용 한다.

NO	DATE	REVISION DESCRIPTION	APPD

설 계
DESIGN

대표전화

축 척	SCALE
A1	1 / 50
A3	1 / 100
일 자	DATE
	2025. 12.
설계번호	PROJECT NO.
	AR - 23 - 026
도면화일명	DWG. FILE NAME
도면번호	SHEET NO.
	MH - 011
도면명	SUBJECT TITLE
	97m²B형 단위세대 난방배관 평면도(기본형)

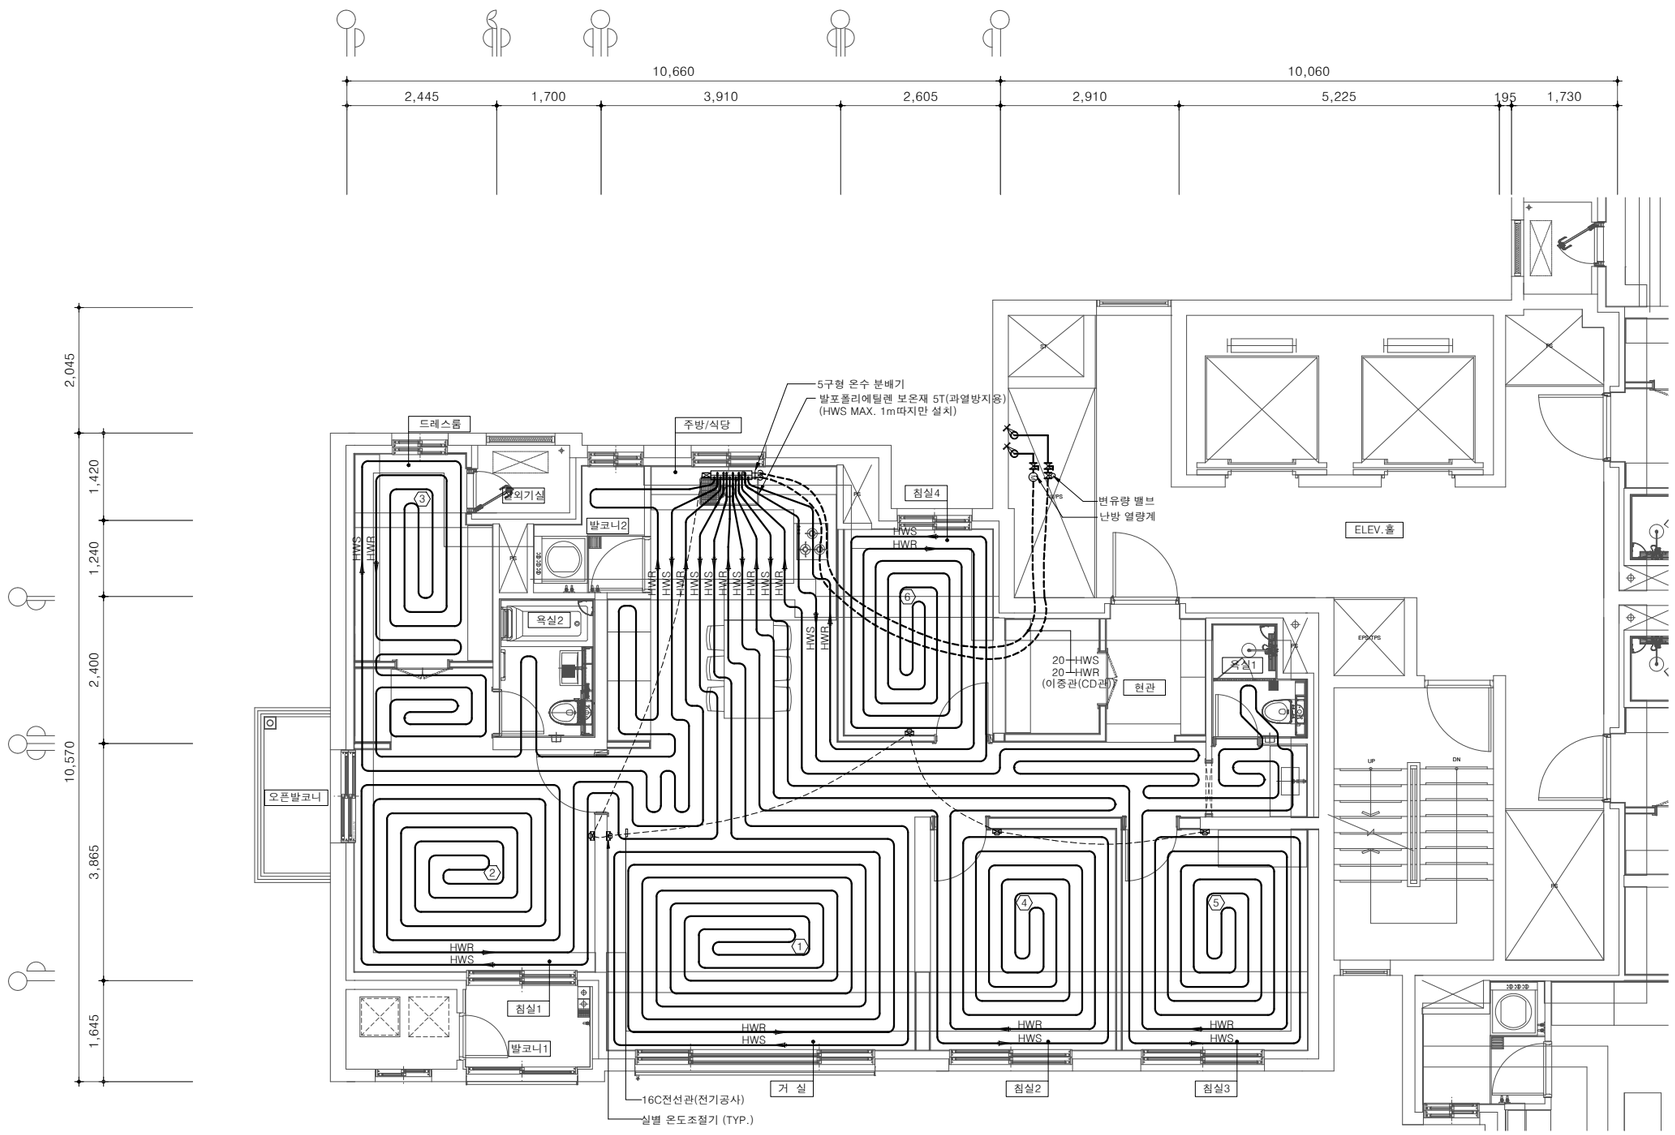

COIL SCHEDULE

번 호	실 명	코일간격(mm)	관경(Φ)	코일길이(m)	재질	비 고
①	거 실	230	15	96	PB	
②	침실1	230	15	74	PB	
③		230	15	75	PB	
④	침실2	230	15	73	PB	
⑤	침실3	230	15	91	PB	
⑥	침실4	230	15	57	PB	

*보일러~온수분배기까지는 PB이중관 임.

97m²B형 단위세대 난방배관 평면도(확장형)

축 척 : 1/100

경기주택도시공사

설계명 PROJECT TITLE

화성동탄(2)A76-2BL
민간참여 공동주택사업

주기 NOTE


1. 배관위치, 배관 및 밸브류 구경은 현장 여건에 따라 변경 될 수 있음.
2. 난방 코일길이, 조닝 및 벽체 이격거리는 현장여건에 따라 변경 가능.
3. 세대별 일괄 가동 정지가 가능하며, 실별 온도 제어가 가능한 자동 온도조절장치 설치.
4. 난방 공급관은 외벽측부터 공급해야하며, 환수관이 외벽측에 공급될 경우 온수분배기 하부에서 공급관과 환수관을 교차 시공한다.
5. 붙박이장 및 냉장고장 하부 등은 결로방지를 위해 난방코일을 적용하고 코일피치는 약 300mm로 하며 현장여건에 따라 변경 가능.
6. 실별 제어 조작 스위치는 전기스위치와 겸용으로 사용하며, 현장여건에 따라 유동적으로 변경될 수 있다.
7. 각 실별로 난방조닝이 2개로 나눠질 경우, 조작스위치 하나에서 연동하여 동시 제어가 되도록 한다.
8. 최상층, 최하층은 코일피치 200mm로 적용 한다.

NO	DATE	REVISION DESCRIPTION	APPD

설 계
DESIGN

대표전화

축 척	SCALE
A1	1 / 50
A3	1 / 100
일 자 DATE	2025. 12.
설계번호 PROJECT NO.	AR - 23 - 026
도면화일명 DWG. FILE NAME	
도면번호 SHEET NO.	MH - 012
도면명 SUBJECT TITLE	97m²B형 단위세대 난방배관 평면도(확장형)

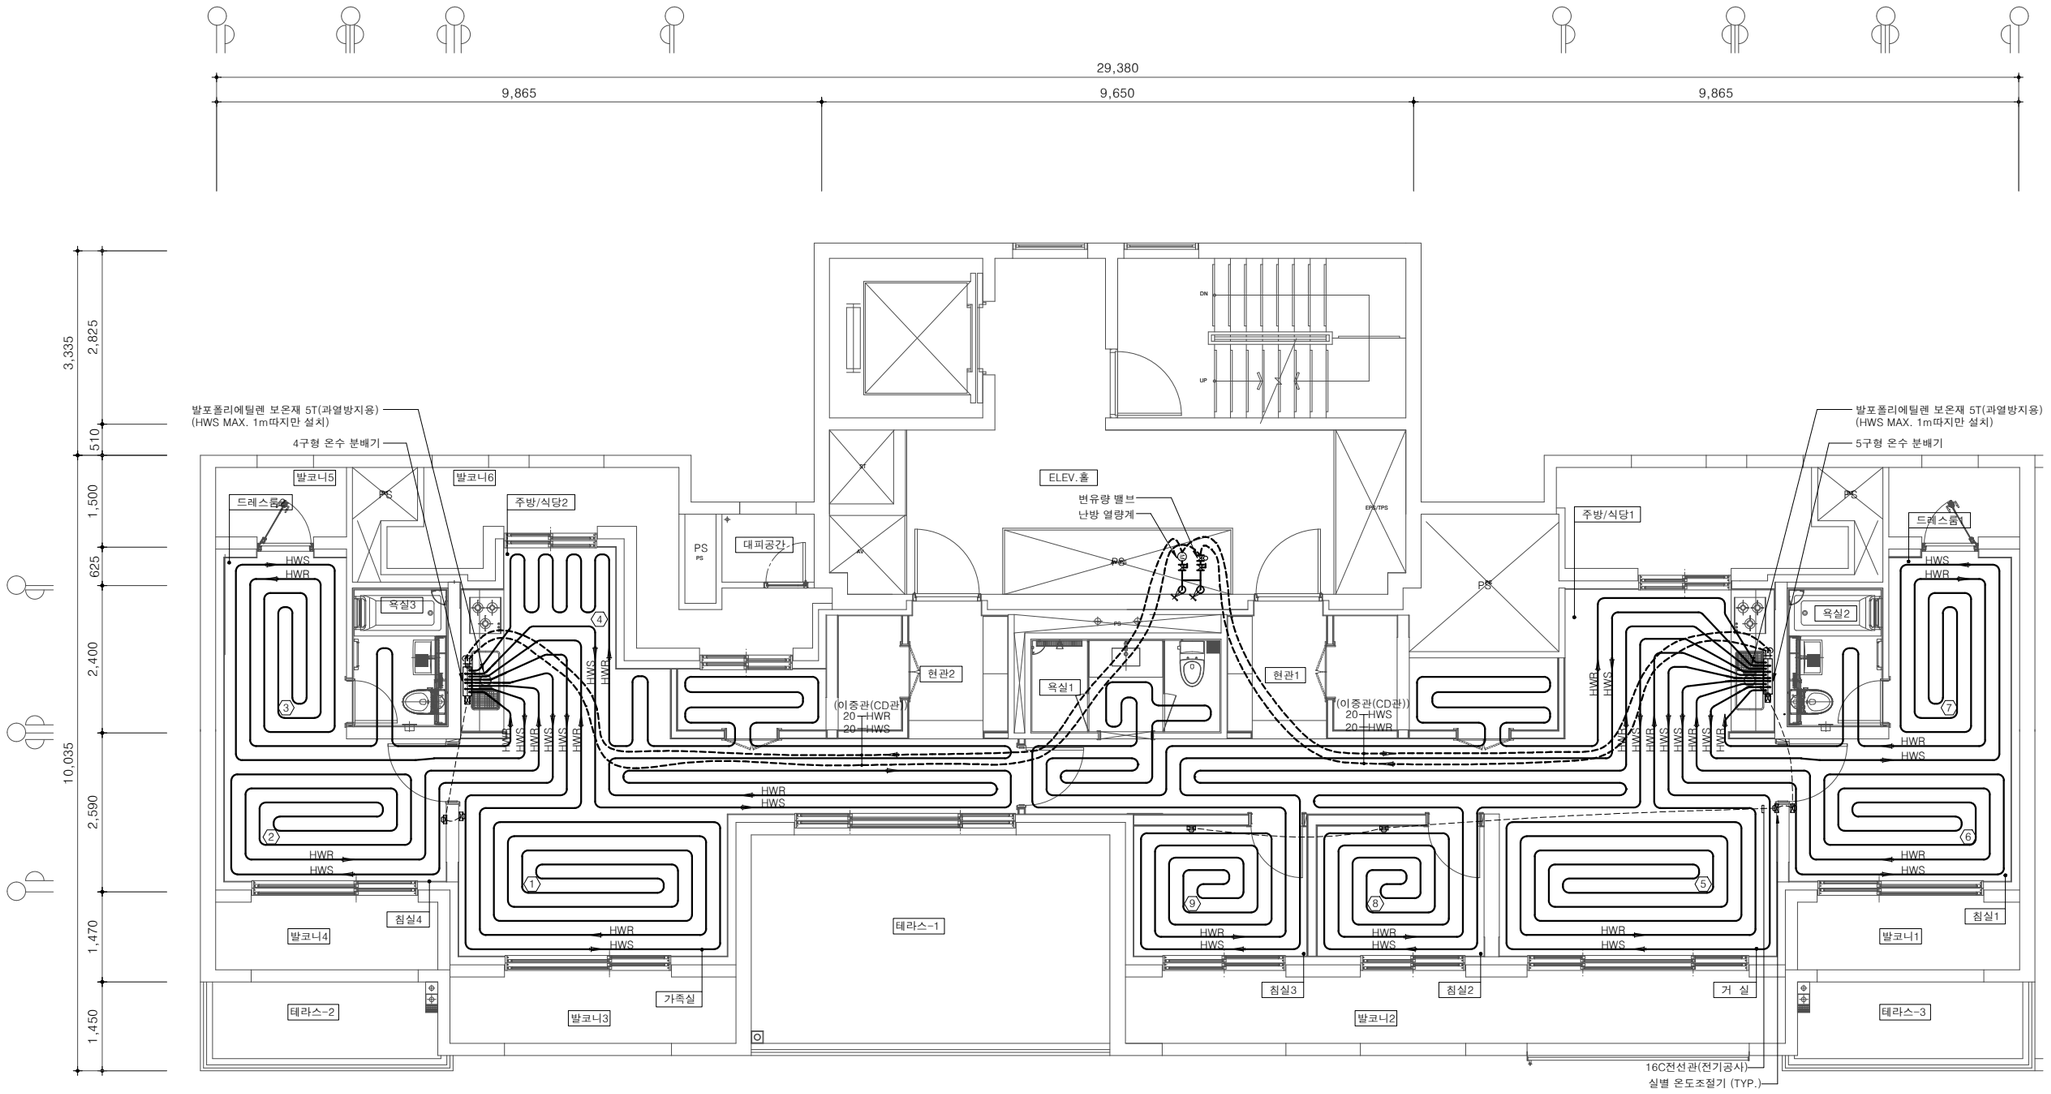

COIL SCHEDULE(좌측)

번 호	실 명	코일간격(mm)	관경(Φ)	코일길이(m)	재질	비 고
①	거 실	230	15	58	PB	
②	침실1	230	15	39	PB	
③		230	15	41	PB	
④	복 도	230	15	71	PB	

*보일러~온수분배기까지는 PB이중관 임.

COIL SCHEDULE(우측)

번 호	실 명	코일간격(mm)	관경(Φ)	코일길이(m)	재질	비 고
⑤	거 실	230	15	58	PB	
⑥	침실1	230	15	39	PB	
⑦		230	15	41	PB	
⑧	침실2	230	15	63	PB	
⑨	침실3	230	15	87	PB	

*보일러~온수분배기까지는 PB이중관 임.

142m²P형 단위세대 난방배관 평면도(기본형)

축 척 : 1/100

경기주택도시공사
GYEONGGI HOUSING & URBAN DEVELOPMENT CORPORATION

설계명 PROJECT TITLE

화성동탄(2)A76-2BL
민간참여 공동주택사업

주기 NOTE

1. 배관위치, 배관 및 밸브류 구경은 현장 여건에 따라 변경 될 수 있음.
2. 난방 코일길이, 조닝 및 벽체 이격거리는 현장여건에 따라 변경 가능.
3. 세대별 일괄 가동 정지가 가능하며, 실별 온도 제어가 가능한 자동 온도조절장치 설치.
4. 난방 공급관은 외벽측부터 공급해야하며, 환수관이 외벽측에 공급될 경우 온수분배기 하부에서 공급관과 환수관을 교차 시공한다.
5. 붙박이장 및 냉장고장 하부 등은 결로방지를 위해 난방코일을 적용하고 코일피치는 약 300mm로 하며 현장여건에 따라 변경 가능.
6. 실별 제어 조작 스위치는 전기스위치와 겸용으로 사용하며, 현장여건에 따라 유동적으로 변경될 수 있다.
7. 각 실별로 난방조닝이 2개로 나눠질 경우, 조작스위치 하나에서 연동하여 동시 제어가 되도록 한다.
8. 최상층, 최하층은 코일피치 200mm로 적용 한다.

NO	DATE	REVISION DESCRIPTION	APPD
△			
△			
△			
△			

설 계
DESIGN

대표전화

축 척	SCALE
A1	1 / 50
A3	1 / 100


일 자 DATE
2025. 12.

설계번호 PROJECT NO.
AR - 23 - 026

도면화일명 DWG. FILE NAME

도면번호 SHEET NO.
MH - 013

도면명 SUBJECT TITLE
142m²P형 단위세대
난방배관 평면도(기본형)

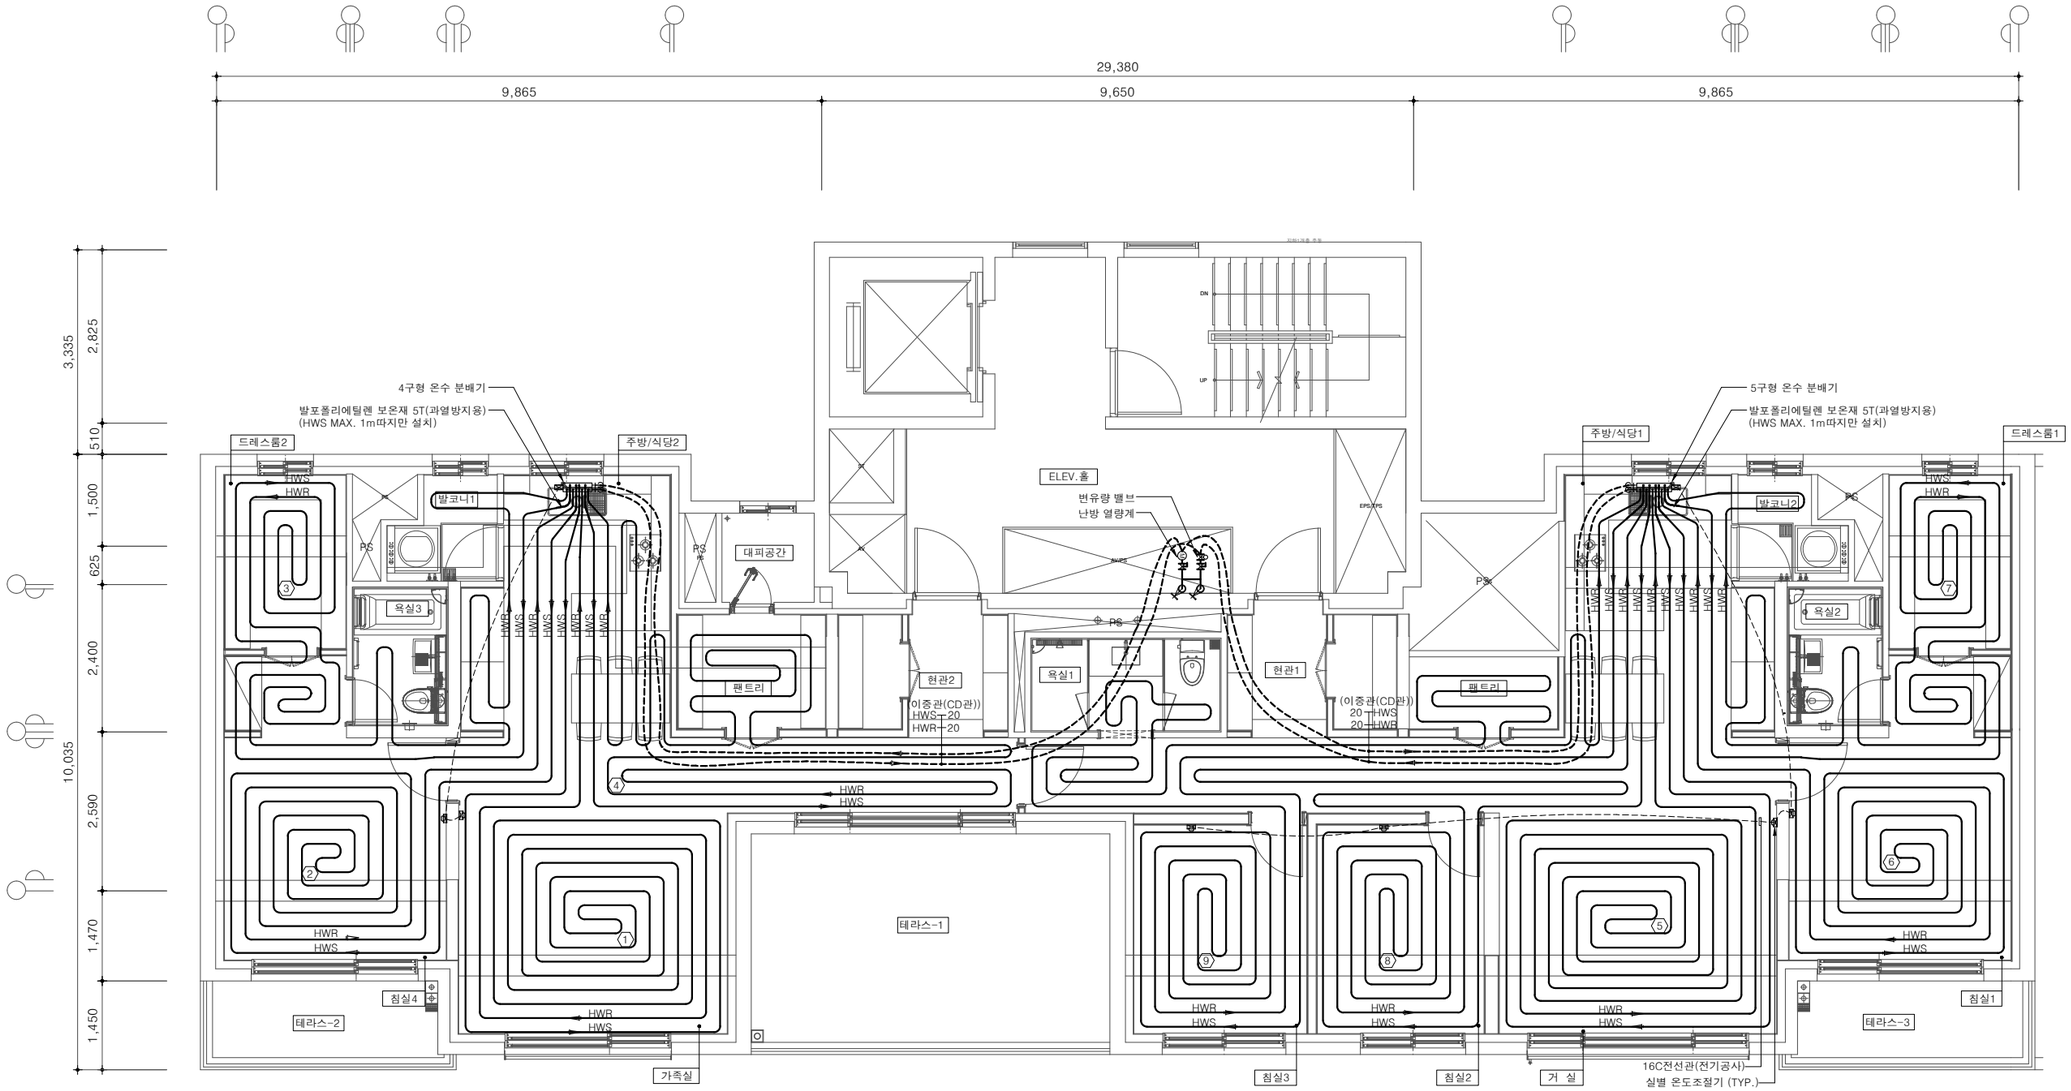

COIL SCHEDULE(좌측)

번 호	실 명	코일간격(mm)	관경(Φ)	코일길이(m)	재질	비 고
①	거 실	230	15	85	PB	
②	침실1	230	15	64	PB	
③		230	15	64	PB	
④	복 도	230	15	75	PB	

*보일러~온수분배기까지는 PB이중관 임.

COIL SCHEDULE(우측)

번 호	실 명	코일간격(mm)	관경(Φ)	코일길이(m)	재질	비 고
⑤	거 실	230	15	86	PB	
⑥	침실1	230	15	64	PB	
⑦		230	15	64	PB	
⑧	침실2	230	15	77	PB	
⑨	침실3	230	15	100	PB	

*보일러~온수분배기까지는 PB이중관 임.

142m²P형 단위세대 난방배관 평면도(확장형)

축 척 : 1/100

경기주택도시공사
GYEONGGI HOUSING & URBAN DEVELOPMENT CORPORATION

설계명 PROJECT TITLE

화성동탄(2)A76-2BL
민간참여 공동주택사업

주기 NOTE

1. 배관위치, 배관 및 밸브류 구경은 현장 여건에 따라 변경 될 수 있음.
2. 난방 코일길이, 조닝 및 벽체 이격 거리는 현장여건에 따라 변경 가능.
3. 세대별 일괄 가동 정지가 가능하며, 실별 온도 제어가 가능한 자동 온도 조절장치 설치.
4. 난방 공급관은 외벽측부터 공급 해야하며, 환수관이 외벽측에 공급 공급될 경우 온수분배기 하부에서 공급관과 환수관을 교차 시공한다.
5. 붙박이장 및 냉장고장 하부 등은 결로방지를 위해 난방코일을 적용 하고 코일피치는 약 300mm로 하며 현장여건에 따라 변경 가능.
6. 실별 제어 조작 스위치는 전기 스위치와 겸용으로 사용하며, 현장 여건에 따라 유동적으로 변경될 수 있다.
7. 각 실별로 난방조닝이 2개로 나눠질 경우, 조작스위치 하나에서 연동 하여 동시 제어가 되도록 한다.
8. 최상층, 최하층은 코일피치 200mm로 적용 한다.

NO	DATE	REVISION DESCRIPTION	APPD

설 계
DESIGN

대표전화

축 척	SCALE
A1	1 / 50
A3	1 / 100


일 자 DATE
2025. 12.

설계번호 PROJECT NO.
AR - 23 - 026

도면화일명 DWG. FILE NAME

도면번호 SHEET NO.
MH - 014

도면명 SUBJECT TITLE
142m²P형 단위세대
난방배관 평면도(확장형)

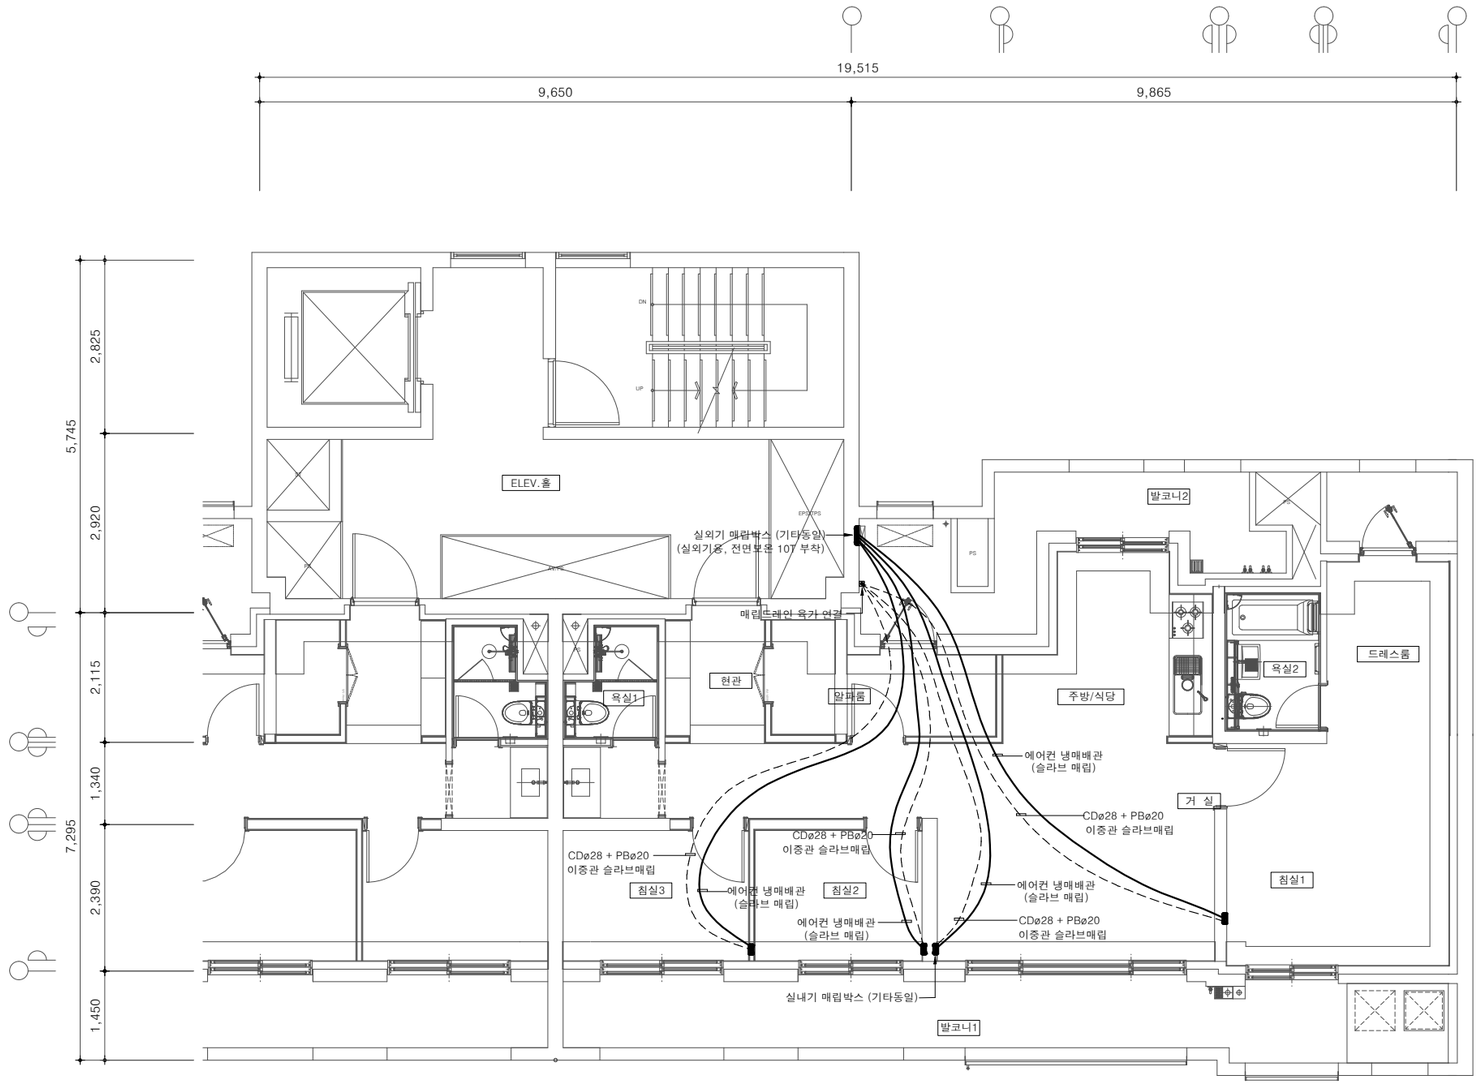

■ 에어컨 냉매배관 일람표

구 분	가 스 관	액 관	통 신 선	전 원 선
침 실1	12.7	6.35	VCTF 1.5x3C	CV 4.0x3C
침 실2	12.7	6.35	VCTF 1.5x3C	CV 4.0x3C
침 실3	12.7	6.35	VCTF 1.5x3C	CV 4.0x3C
거 실	15.88	6.35	VCTF 1.5x3C	CV 4.0x3C

84m²A형 단위세대 냉매배관 평면도(기본형)

축 척 : 1/100

경기주택도시공사
GYEONGGI HOUSING & URBAN DEVELOPMENT CORPORATION

설계명 PROJECT TITLE

화성동탄(2)A76-2BL
민간참여 공동주택사업

주기 NOTE
1. 배관위치, 배관 및 밸브류 구경은 현장 여건에 따라 변경 될 수 있음.
2. 신축이음 및 앙카류 등 배관 부속류 위치는 현장 여건에 따라 변경 될 수 있음.
3. 배관의 매립방식은 이중관을 이용하여 수리 및 교체가 용이하도록 함.
4. 센서식 풋밸브 씽크수전 설치

NO	DATE	REVISION DESCRIPTION	APPD
△			
△			
△			
△			

설 계
DESIGN

대표전화

축 척	SCALE
A1	1 / 50
A3	1 / 100


일 자 DATE
2025. 12.

설계번호 PROJECT NO.
AR - 23 - 026

도면화일명 DWG. FILE NAME

도면번호 SHEET NO.
MH - 015

도면명 SUBJECT TITLE
84m²A형 단위세대
냉매배관 평면도(기본형)

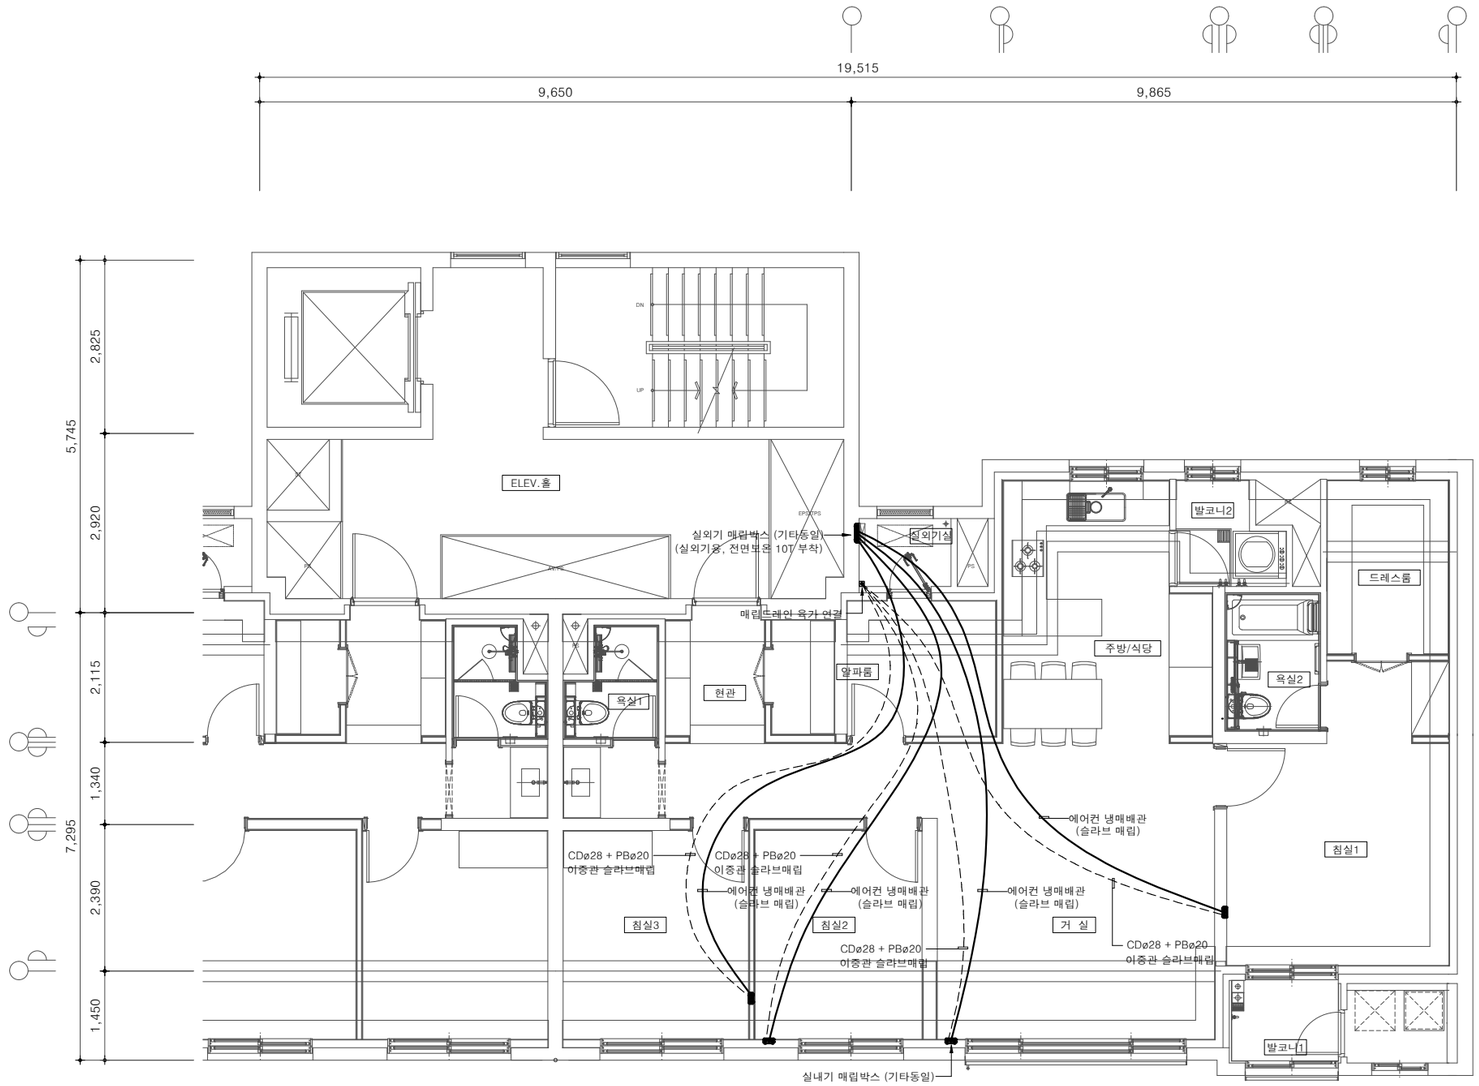

에어컨 냉매배관 일람표

구 분	가 스 관	액 관	통 신 선	전 원 선
침 실1	12.7	6.35	VCTF 1.5x3C	CV 4.0x3C
침 실2	12.7	6.35	VCTF 1.5x3C	CV 4.0x3C
침 실3	12.7	6.35	VCTF 1.5x3C	CV 4.0x3C
거 실	15.88	6.35	VCTF 1.5x3C	CV 4.0x3C

84m²A형 단위세대 냉매배관 평면도(확장형)

축 척 : 1/100

경기주택도시공사
GYEONGGI HOUSING & URBAN DEVELOPMENT CORPORATION

설계명 PROJECT TITLE

화성동탄(2)A76-2BL
민간참여 공동주택사업

주기 NOTE
1. 배관위치, 배관 및 밸브류 구경은 현장 여건에 따라 변경 될 수 있음.
2. 신축이음 및 앙카류 등 배관 부속류 위치는 현장 여건에 따라 변경 될 수 있음.
3. 배관의 매립방식은 이중관을 이용하여 수리 및 교체가 용이하도록 함.
4. 센서식 풋밸브 씽크수전 설치

NO	DATE	REVISION DESCRIPTION	APPD
△			
△			
△			
△			

설 계
DESIGN

대표전화

축 척	SCALE
A1	1 / 50
A3	1 / 100


일 자 DATE
2025. 12.

설계번호 PROJECT NO.
AR - 23 - 026

도면화일명 DWG. FILE NAME

도면번호 SHEET NO.
MH – 016

도면명 SUBJECT TITLE
84m²A형 단위세대
냉매배관 평면도(확장형)

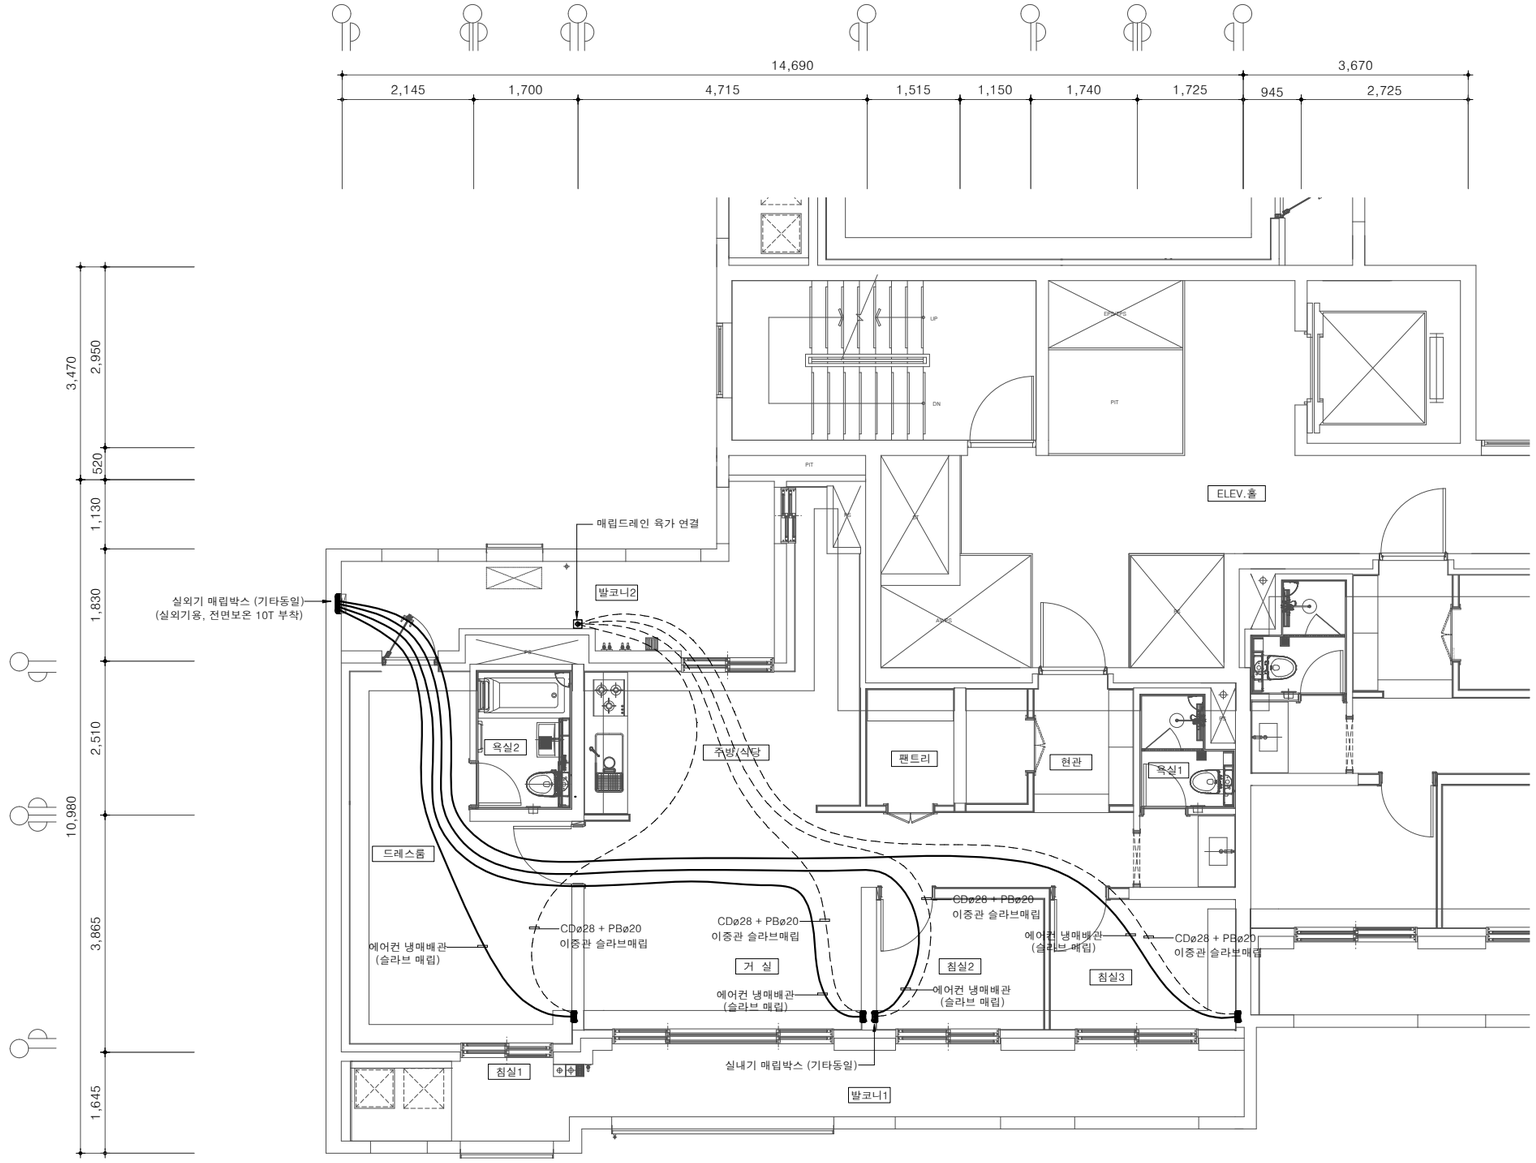

에어컨 냉매배관 일람표

구 분	가 스 관	액 관	통 신 선	전 원 선
침 실1	12.7	6.35	VCTF 1.5x3C	CV 4.0x3C
침 실2	12.7	6.35	VCTF 1.5x3C	CV 4.0x3C
침 실3	12.7	6.35	VCTF 1.5x3C	CV 4.0x3C
거 실	15.88	6.35	VCTF 1.5x3C	CV 4.0x3C

M 84m²B형 단위세대 냉매배관 평면도(기본형)

축 척 : 1/100

경기주택도시공사
GYEONGGI HOUSING & URBAN DEVELOPMENT CORPORATION

설계명 PROJECT TITLE

화성동탄(2)A76-2BL
민간참여 공동주택사업

주기 NOTE
1. 배관위치, 배관 및 밸브류 구경은 현장 여건에 따라 변경 될 수 있음.
2. 신축이음 및 앙카류 등 배관 부속류 위치는 현장 여건에 따라 변경 될 수 있음.
3. 배관의 매립방식은 이중관을 이용하여 수리 및 교체가 용이하도록 함.
4. 센서식 풋밸브 씽크수전 설치

NO	DATE	REVISION DESCRIPTION	APPD

설 계
DESIGN

대표전화

축 척	SCALE
A1	1 / 50
A3	1 / 100


일 자 DATE
2025. 12.

설계번호 PROJECT NO.
AR - 23 - 026

도면화일명 DWG. FILE NAME

도면번호 SHEET NO.
MH – 017

도면명 SUBJECT TITLE
84m²B형 단위세대
냉매배관 평면도(기본형)

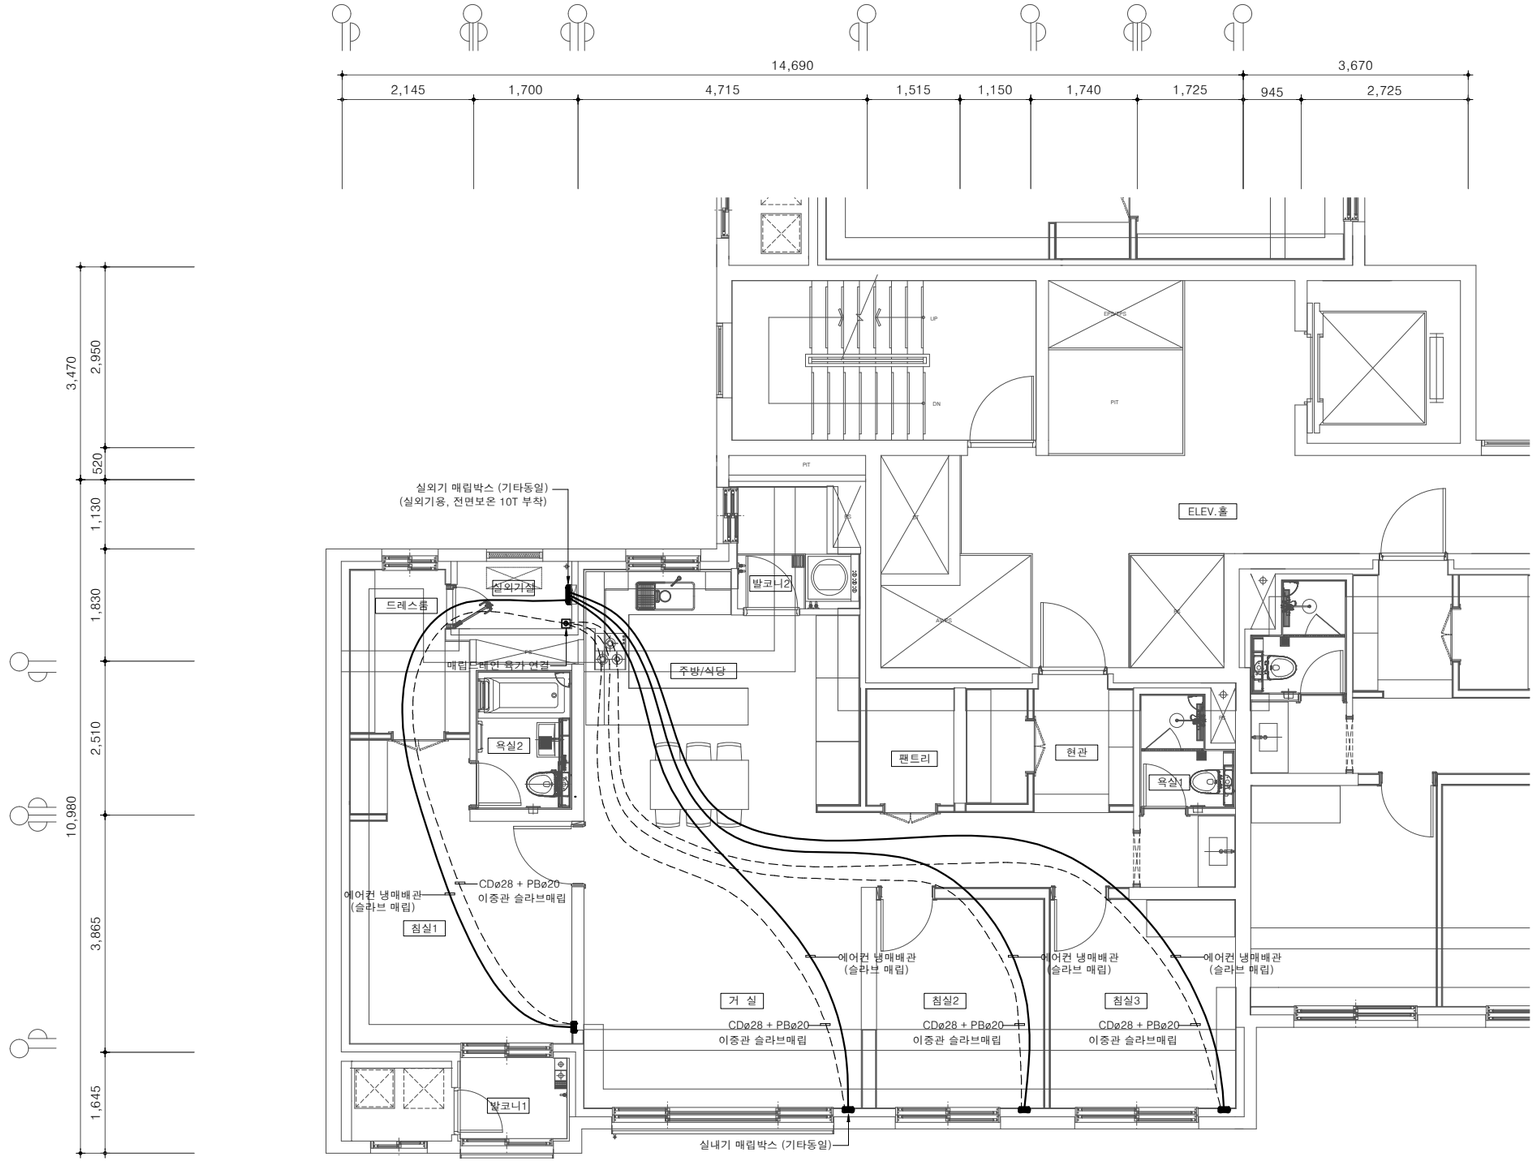

■ 에어컨 냉매배관 일람표

구 분	가 스 관	액 관	통 신 선	전 원 선
침 실1	12.7	6.35	VCTF 1.5x3C	CV 4.0x3C
침 실2	12.7	6.35	VCTF 1.5x3C	CV 4.0x3C
침 실3	12.7	6.35	VCTF 1.5x3C	CV 4.0x3C
거 실	15.88	6.35	VCTF 1.5x3C	CV 4.0x3C

M 84m²B형 단위세대 냉매배관 평면도(확장형)

축 척 : 1/100

경기주택도시공사
GYEONGGI HOUSING & URBAN DEVELOPMENT CORPORATION

설계명 PROJECT TITLE

화성동탄(2)A76-2BL
민간참여 공동주택사업

주기 NOTE
1. 배관위치, 배관 및 밸브류 구경은 현장 여건에 따라 변경 될 수 있음.
2. 신축이음 및 앙카류 등 배관 부속류 위치는 현장 여건에 따라 변경 될 수 있음.
3. 배관의 매립방식은 이중관을 이용하여 수리 및 교체가 용이하도록 함.
4. 센서식 풋밸브 씽크수전 설치

NO	DATE	REVISION DESCRIPTION	APPD

설 계
DESIGN

대표전화

축 척	SCALE
A1	1 / 50
A3	1 / 100


일 자 DATE
2025. 12.

설계번호 PROJECT NO.
AR - 23 - 026

도면화일명 DWG. FILE NAME

도면번호 SHEET NO.
MH - 018

도면명 SUBJECT TITLE
84m²B형 단위세대
냉매배관 평면도(확장형)

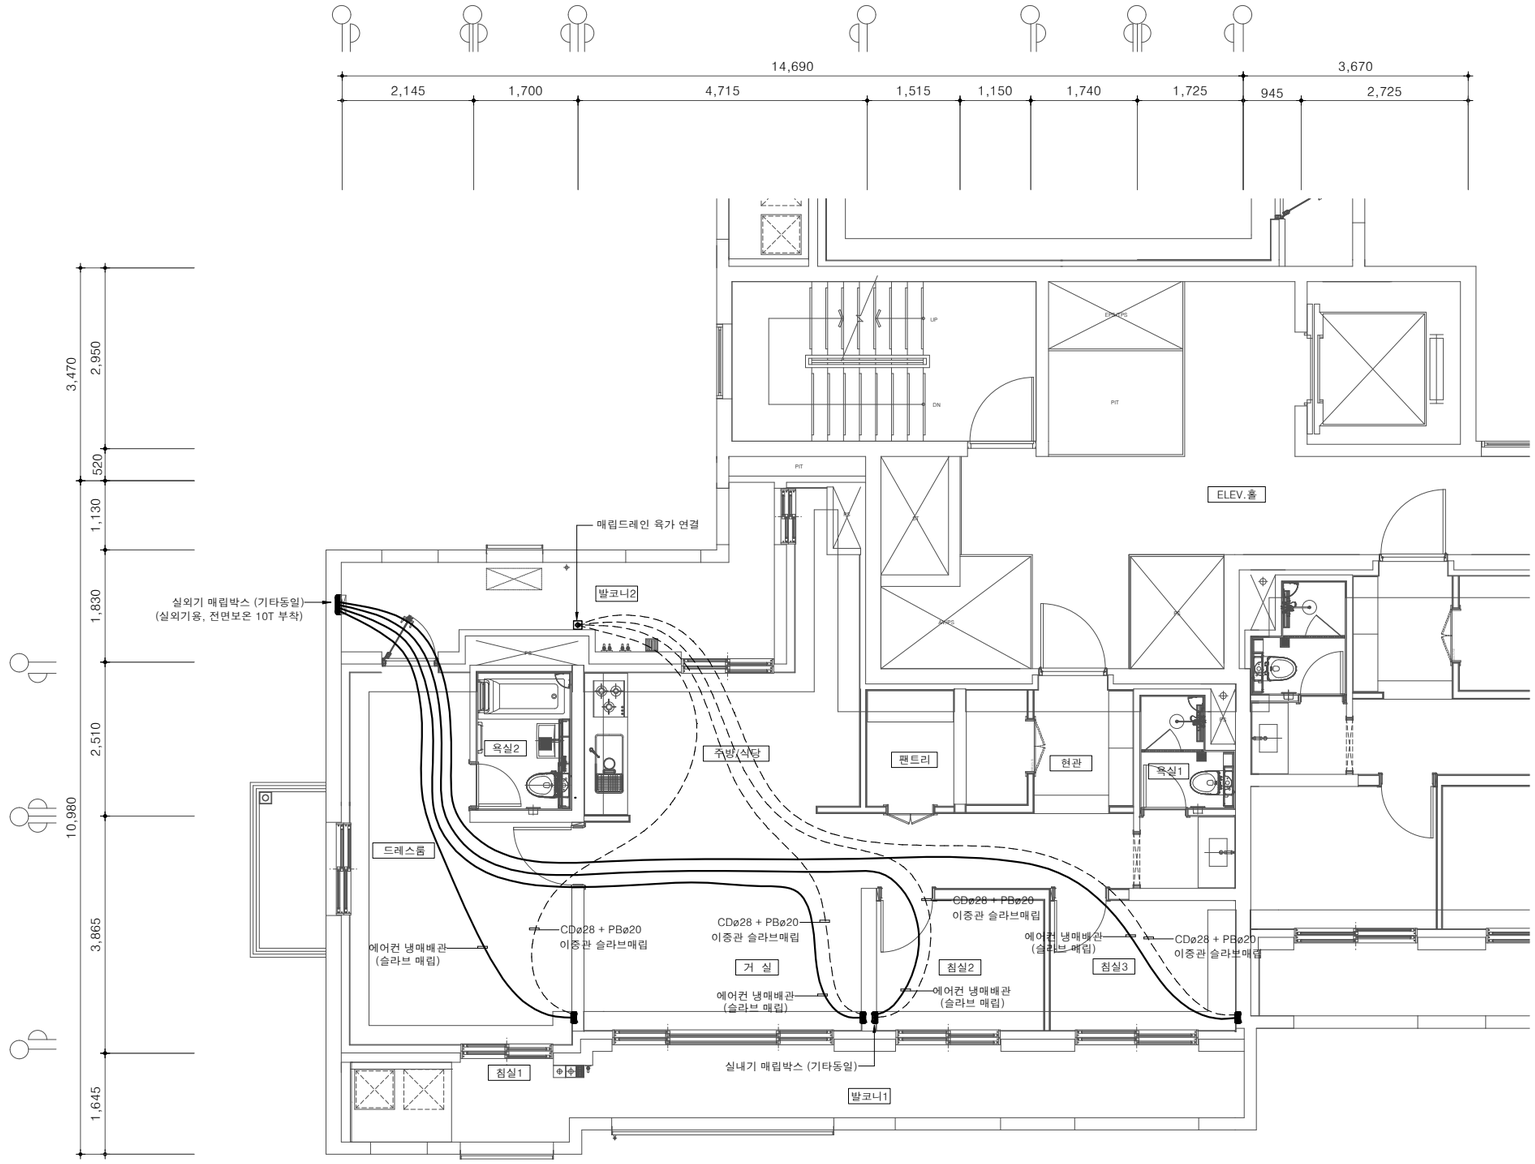

에어컨 냉매배관 일람표

구 분	가 스 관	액 관	통 신 선	전 원 선
침 실1	12.7	6.35	VCTF 1.5x3C	CV 4.0x3C
침 실2	12.7	6.35	VCTF 1.5x3C	CV 4.0x3C
침 실3	12.7	6.35	VCTF 1.5x3C	CV 4.0x3C
거 실	15.88	6.35	VCTF 1.5x3C	CV 4.0x3C

M 84m²C형 단위세대 냉매배관 평면도(기본형)

축 척 : 1/100

경기주택도시공사
GYEONGGI HOUSING & URBAN DEVELOPMENT CORPORATION

설계명 PROJECT TITLE

화성동탄(2)A76-2BL
민간참여 공동주택사업

주기 NOTE
1. 배관위치, 배관 및 밸브류 구경은 현장 여건에 따라 변경 될 수 있음.
2. 신축이음 및 앙카류 등 배관 부속류 위치는 현장 여건에 따라 변경 될 수 있음.
3. 배관의 매립방식은 이중관을 이용하여 수리 및 교체가 용이하도록 함.
4. 센서식 풋밸브 씽크수전 설치

NO	DATE	REVISION DESCRIPTION	APPD

설 계
DESIGN

대표전화

축 척	SCALE
A1	1 / 50
A3	1 / 100


일 자 DATE
2025. 12.

설계번호 PROJECT NO.
AR - 23 - 026

도면화일명 DWG. FILE NAME

도면번호 SHEET NO.
MH - 019

도면명 SUBJECT TITLE
84m²C형 단위세대
냉매배관 평면도(기본형)

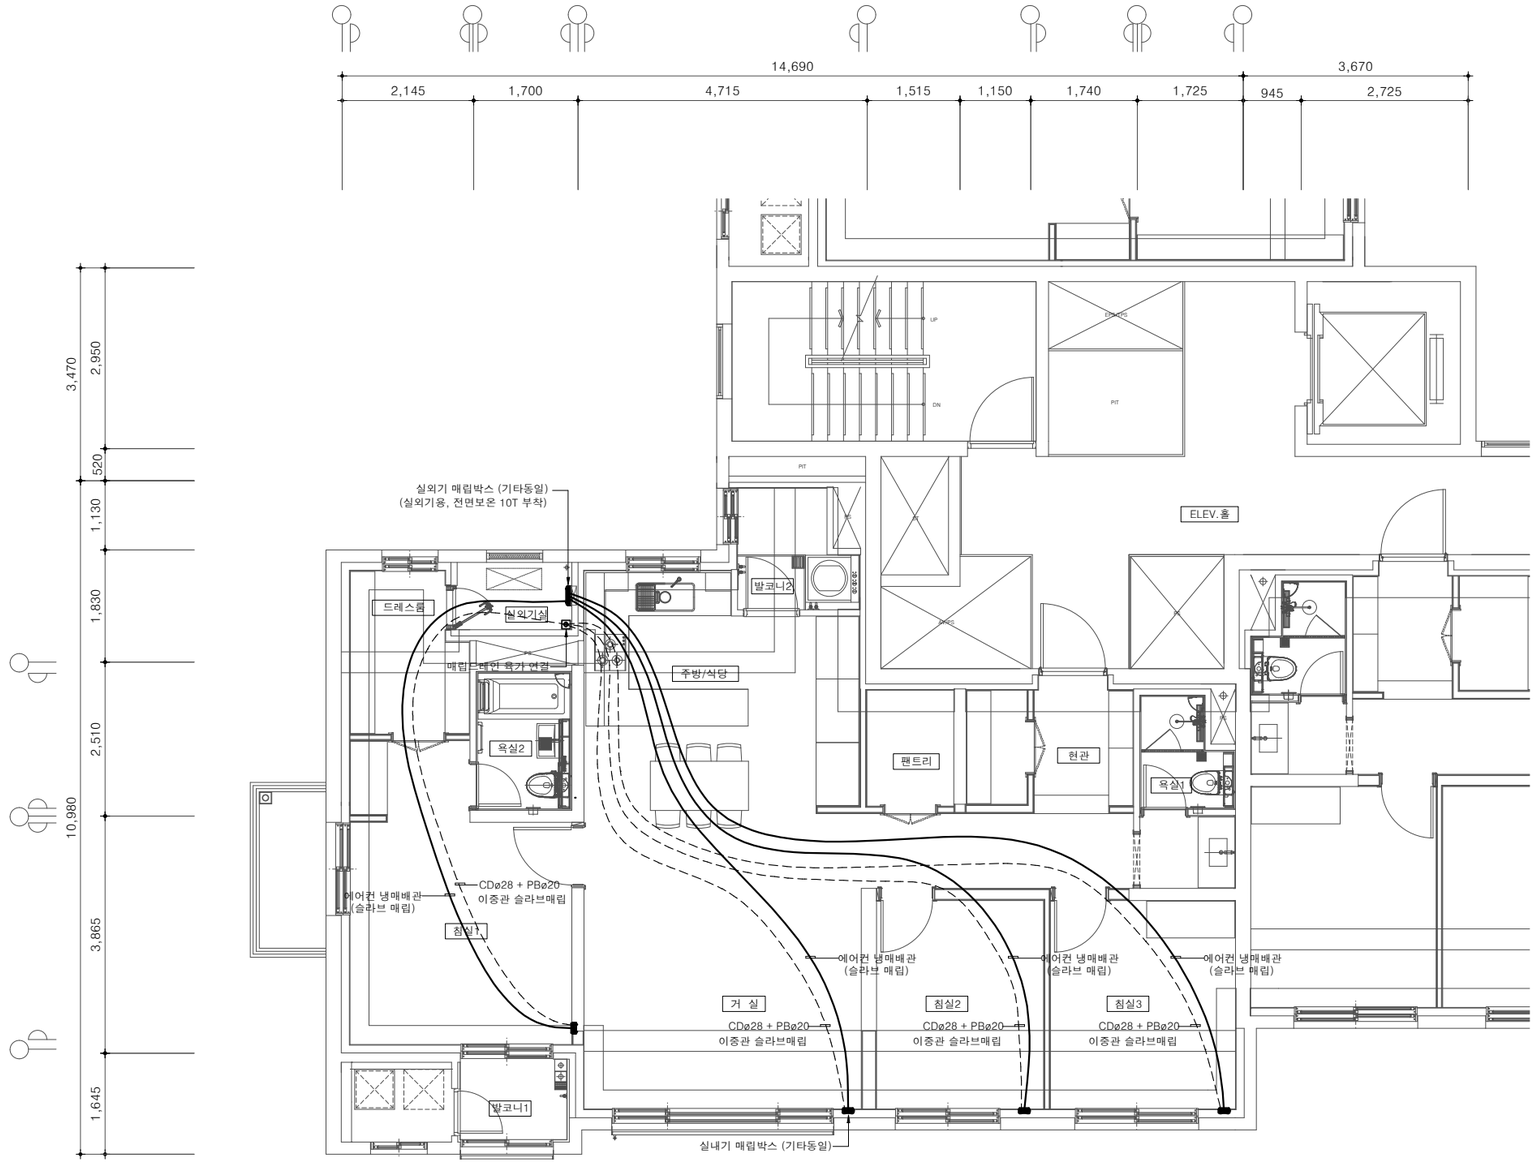

에어컨 냉매배관 일람표

구 분	가 스 관	액 관	통 신 선	전 원 선
침 실1	12.7	6.35	VCTF 1.5x3C	CV 4.0x3C
침 실2	12.7	6.35	VCTF 1.5x3C	CV 4.0x3C
침 실3	12.7	6.35	VCTF 1.5x3C	CV 4.0x3C
거 실	15.88	6.35	VCTF 1.5x3C	CV 4.0x3C

84m²C형 단위세대 냉매배관 평면도(확장형)

축 척 : 1/100

경기주택도시공사
GYEONGGI HOUSING & URBAN DEVELOPMENT CORPORATION

설계명 PROJECT TITLE

화성동탄(2)A76-2BL
민간참여 공동주택사업

주기 NOTE
1. 배관위치, 배관 및 밸브류 구경은 현장 여건에 따라 변경 될 수 있음.
2. 신축이음 및 앙카류 등 배관 부속류 위치는 현장 여건에 따라 변경 될 수 있음.
3. 배관의 매립방식은 이중관을 이용하여 수리 및 교체가 용이하도록 함.
4. 센서식 풋밸브 씽크수전 설치

NO	DATE	REVISION DESCRIPTION	APPD

설 계
DESIGN

대표전화

축 척	SCALE
A1	1 / 50
A3	1 / 100


일 자 DATE
2025. 12.

설계번호 PROJECT NO.
AR - 23 - 026

도면화일명 DWG. FILE NAME

도면번호 SHEET NO.
MH – 020

도면명 SUBJECT TITLE
84m²C형 단위세대
냉매배관 평면도(확장형)

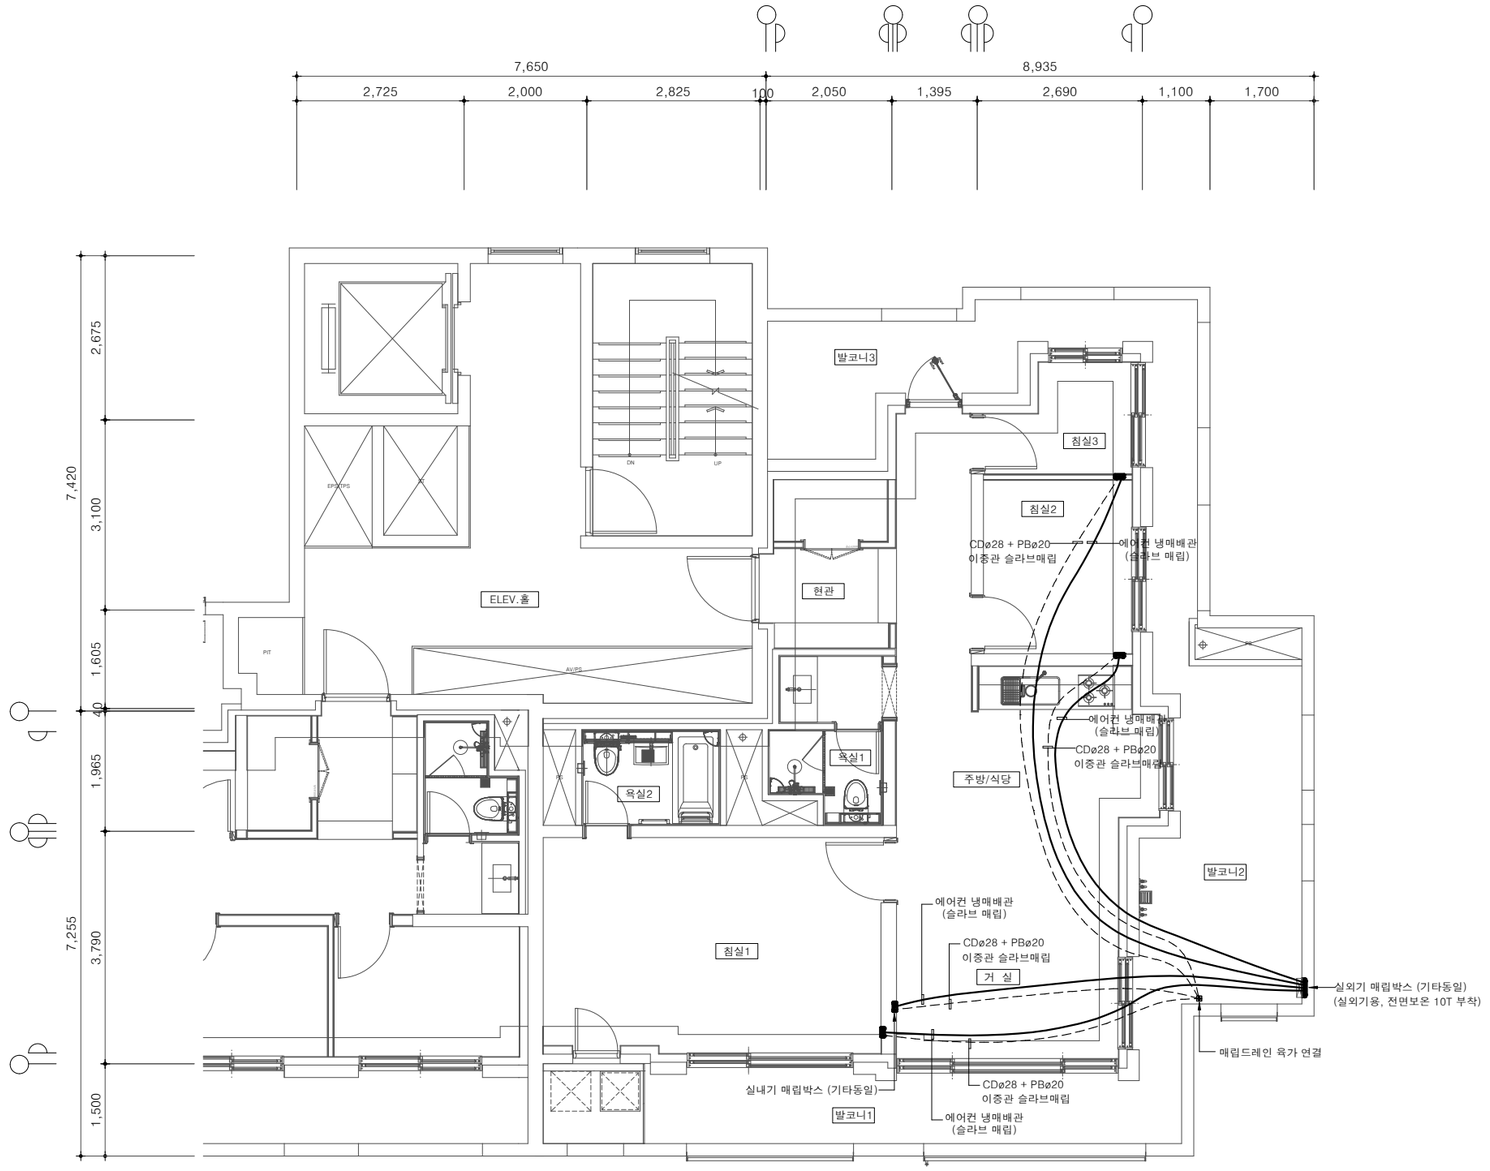

■ 에어컨 냉매배관 일람표

구 분	가 스 관	액 관	통 신 선	전 원 선
침 실1	12.7	6.35	VCTF 1.5x3C	CV 4.0x3C
침 실2	12.7	6.35	VCTF 1.5x3C	CV 4.0x3C
침 실3	12.7	6.35	VCTF 1.5x3C	CV 4.0x3C
거 실	15.88	6.35	VCTF 1.5x3C	CV 4.0x3C

84m²D형 단위세대 냉매배관 평면도(기본형)

축 척 : 1/100

경기주택도시공사
GYEONGGI HOUSING & URBAN DEVELOPMENT CORPORATION

설계명 PROJECT TITLE

화성동탄(2)A76-2BL
민간참여 공동주택사업

주기 NOTE
1. 배관위치, 배관 및 밸브류 구경은 현장 여건에 따라 변경 될 수 있음.
2. 신축이음 및 앙카류 등 배관 부속류 위치는 현장 여건에 따라 변경 될 수 있음.
3. 배관의 매립방식은 이중관을 이용하여 수리 및 교체가 용이하도록 함.
4. 센서식 풋밸브 씽크수전 설치

NO	DATE	REVISION DESCRIPTION	APPD
△			
△			
△			
△			

설 계
DESIGN

대표전화

축 척	SCALE
A1	1 / 50
A3	1 / 100


일 자 DATE
2025. 12.

설계번호 PROJECT NO.
AR - 23 - 026

도면화일명 DWG. FILE NAME

도면번호 SHEET NO.
MH - 021

도면명 SUBJECT TITLE
84m²D형 단위세대
냉매배관 평면도(기본형)

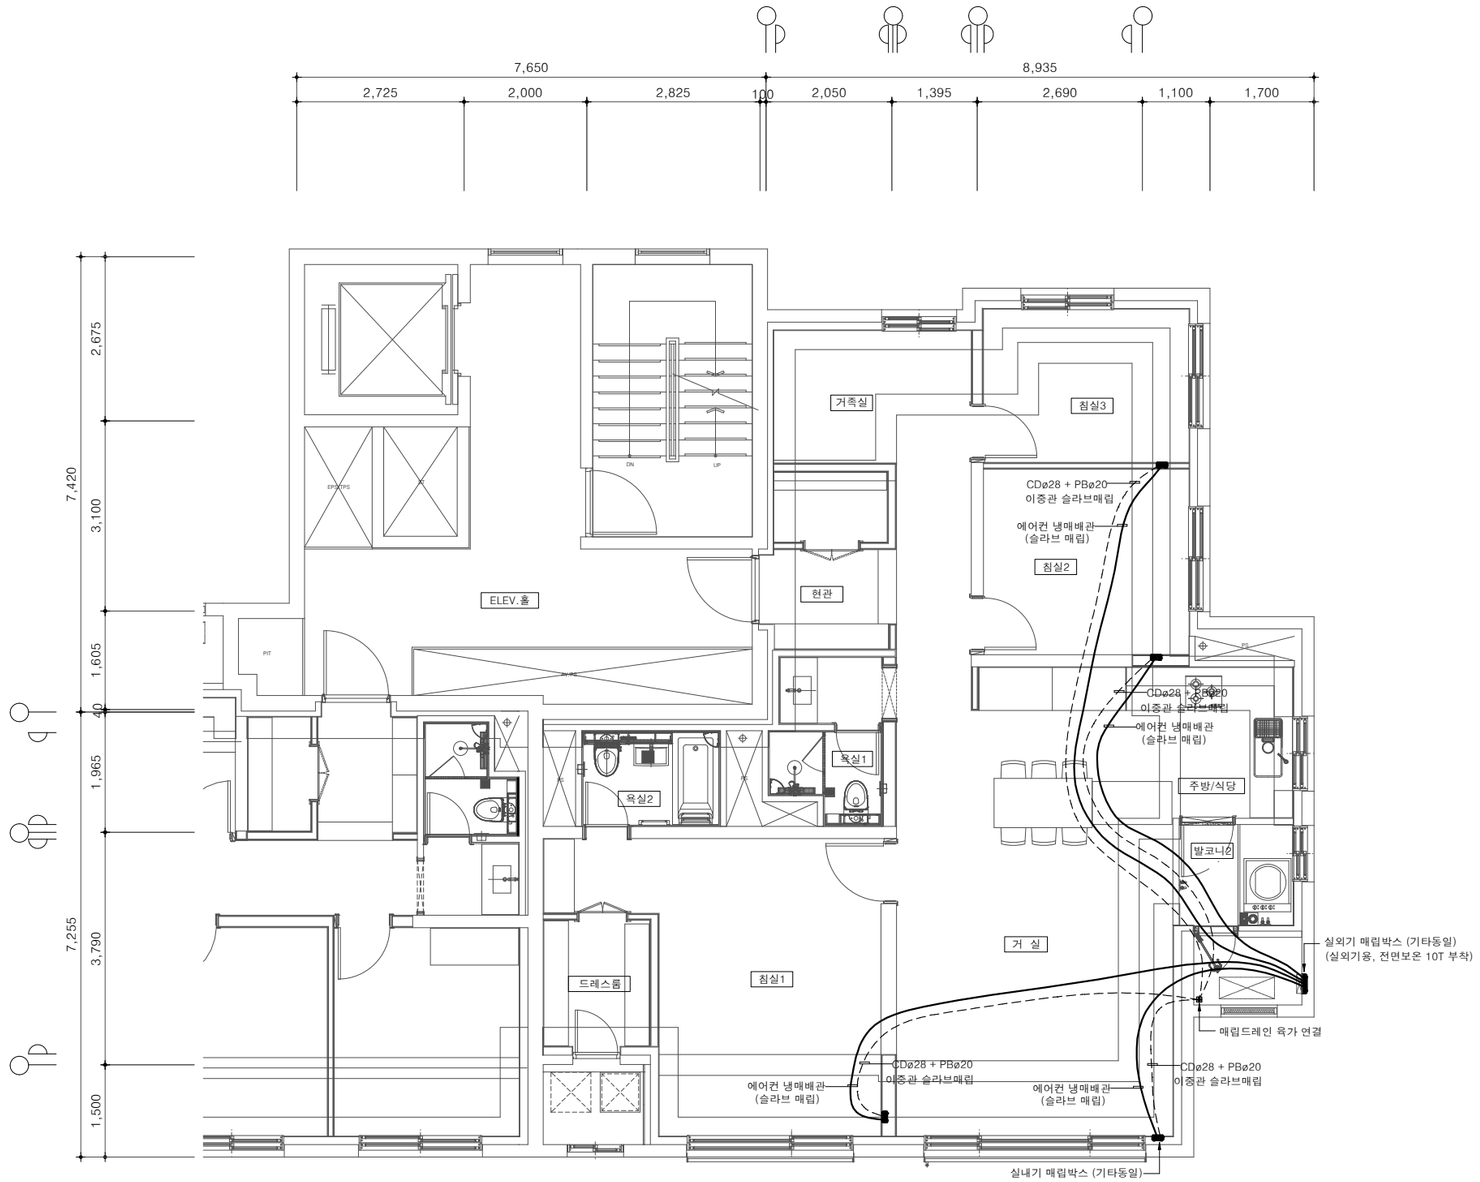

에어컨 냉매배관 일람표

구 분	가 스 관	액 관	통 신 선	전 원 선
침 실1	12.7	6.35	VCTF 1.5x3C	CV 4.0x3C
침 실2	12.7	6.35	VCTF 1.5x3C	CV 4.0x3C
침 실3	12.7	6.35	VCTF 1.5x3C	CV 4.0x3C
거 실	15.88	6.35	VCTF 1.5x3C	CV 4.0x3C

84m²D형 단위세대 냉매배관 평면도(확장형)

축 척 : 1/100

경기주택도시공사
GYEONGGI HOUSING & URBAN DEVELOPMENT CORPORATION

설계명 PROJECT TITLE

화성동탄(2)A76-2BL
민간참여 공동주택사업

주기 NOTE
1. 배관위치, 배관 및 밸브류 구경은 현장 여건에 따라 변경 될 수 있음.
2. 신축이음 및 앙카류 등 배관 부속류 위치는 현장 여건에 따라 변경 될 수 있음.
3. 배관의 매립방식은 이중관을 이용하여 수리 및 교체가 용이하도록 함.
4. 센서식 풋밸브 씽크수전 설치

NO	DATE	REVISION DESCRIPTION	APPD
△			
△			
△			
△			

설 계
DESIGN

대표전화

축 척	SCALE
A1	1 / 50
A3	1 / 100


일 자 DATE
2025. 12.

설계번호 PROJECT NO.
AR - 23 - 026

도면화일명 DWG. FILE NAME

도면번호 SHEET NO.
MH - 022

도면명 SUBJECT TITLE
84m²D형 단위세대
냉매배관 평면도(확장형)

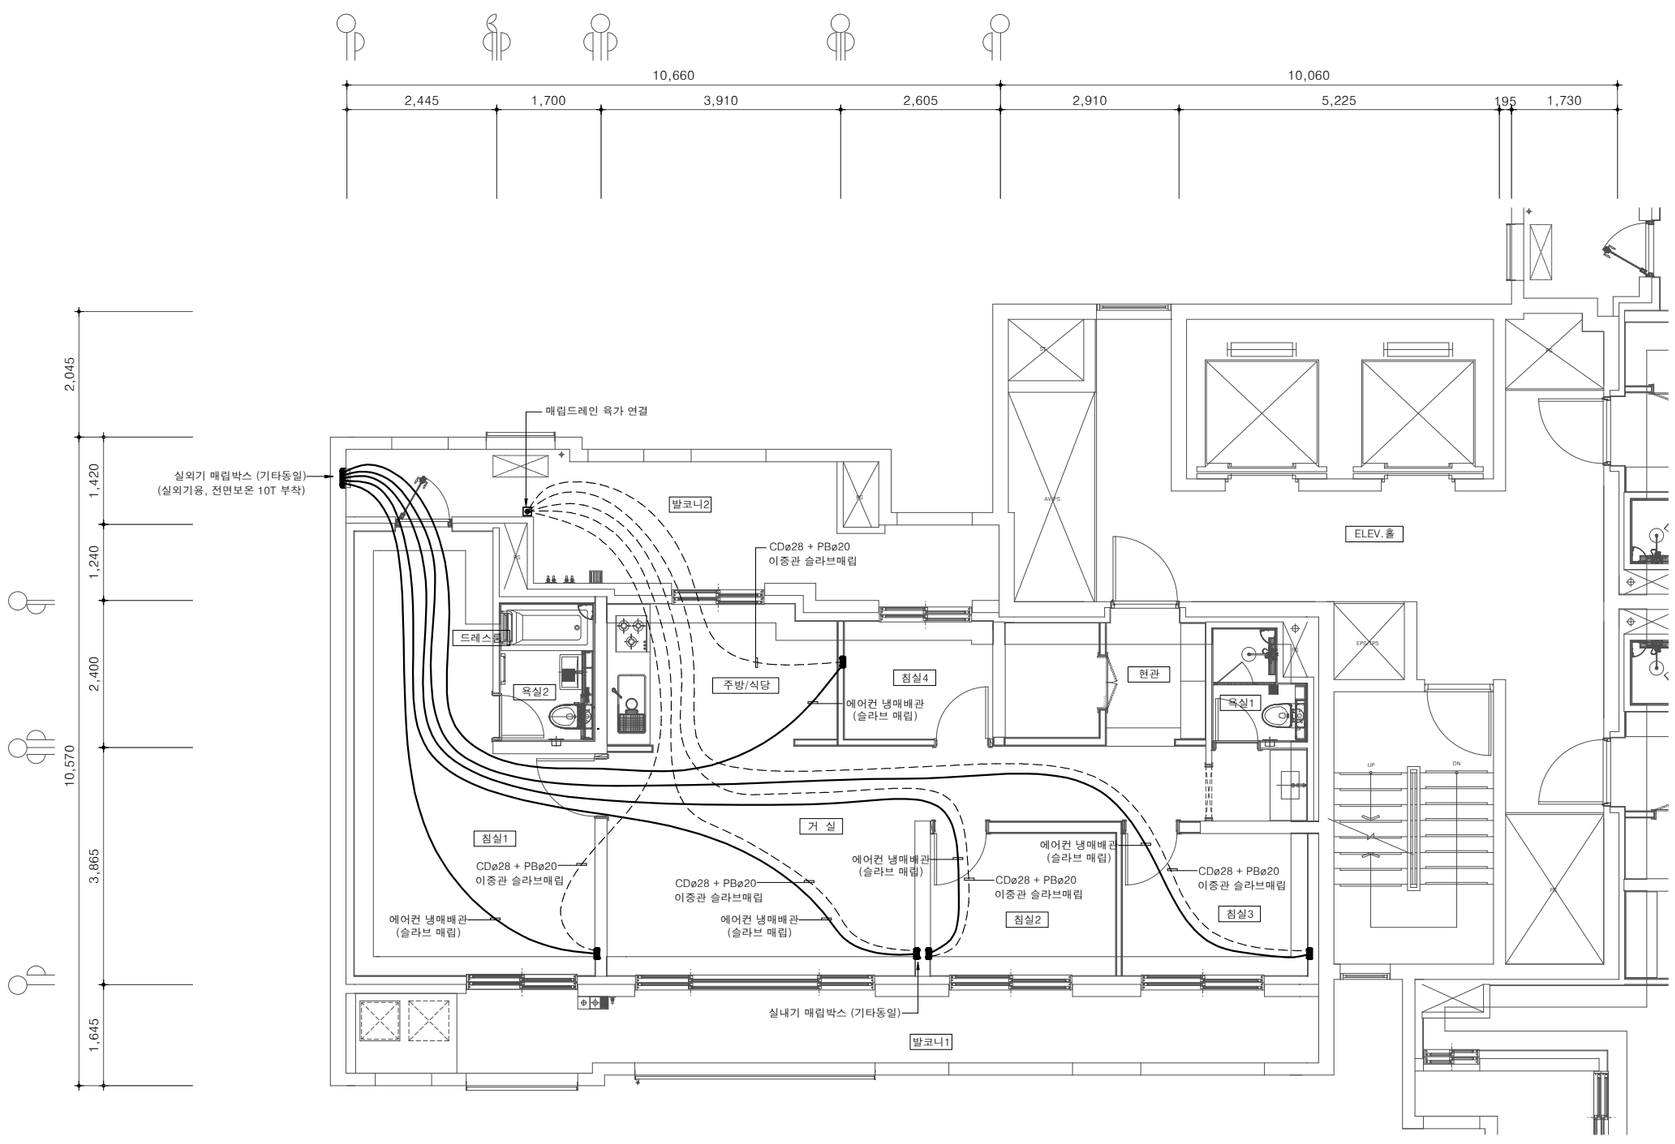

■ 에어컨 냉매배관 일람표

구 분	가 스 관	액 관	통 신 선	전 원 선
침 실1	12.7	6.35	VCTF 1.5x3C	CV 4.0x3C
침 실2	12.7	6.35	VCTF 1.5x3C	CV 4.0x3C
침 실3	12.7	6.35	VCTF 1.5x3C	CV 4.0x3C
거 실	15.88	6.35	VCTF 1.5x3C	CV 4.0x3C

M 97m²A형 단위세대 냉매배관 평면도(기본형)

축 척 : 1/100

경기주택도시공사
GYEONGGI HOUSING & URBAN DEVELOPMENT CORPORATION

설계명 PROJECT TITLE

화성동탄(2)A76-2BL
민간참여 공동주택사업

주기 NOTE

NO	DATE	REVISION DESCRIPTION	APPD
△			
△			
△			
△			

설 계
DESIGN

대표전화

축 척	SCALE
A1	1 / 50
A3	1 / 100


일 자 DATE
2025. 12.

설계번호 PROJECT NO.
AR - 23 - 026

도면화일명 DWG. FILE NAME

도면번호 SHEET NO.
MH – 023

도면명 SUBJECT TITLE
97m²A형 단위세대
냉매배관 평면도(기본형)

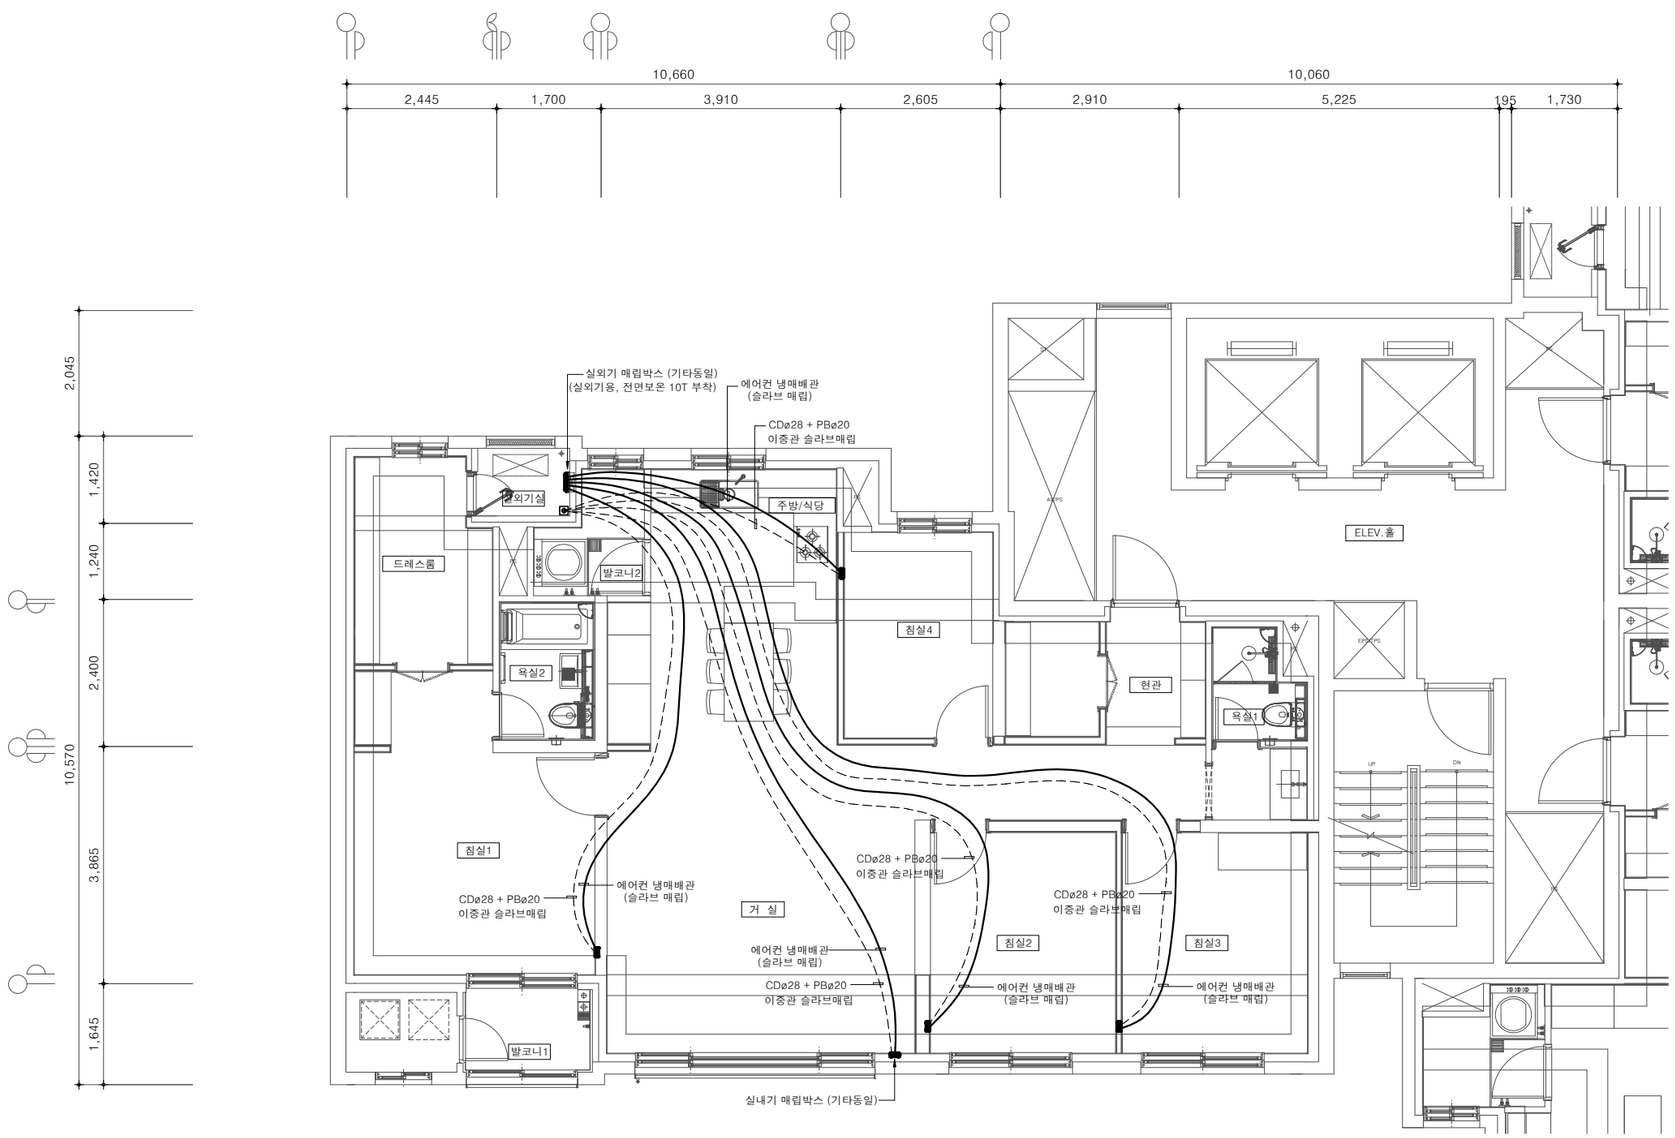

에어컨 냉매배관 일람표

구 분	가 스 관	액 관	통 신 선	전 원 선
침 실1	12.7	6.35	VCTF 1.5x3C	CV 4.0x3C
침 실2	12.7	6.35	VCTF 1.5x3C	CV 4.0x3C
침 실3	12.7	6.35	VCTF 1.5x3C	CV 4.0x3C
거 실	15.88	6.35	VCTF 1.5x3C	CV 4.0x3C

M 97m²A형 단위세대 냉매배관 평면도(확장형)

축 척 : 1/100

경기주택도시공사
GYEONGGI HOUSING & URBAN DEVELOPMENT CORPORATION

설계명 PROJECT TITLE

화성동탄(2)A76-2BL
민간참여 공동주택사업

주기 NOTE

NO	DATE	REVISION DESCRIPTION	APPD
△			
△			
△			
△			

설 계
DESIGN

대표전화

축 척	SCALE
A1	1 / 50
A3	1 / 100


일 자 DATE
2025. 12.

설계번호 PROJECT NO.
AR - 23 - 026

도면화일명 DWG. FILE NAME

도면번호 SHEET NO.
MH - 024

도면명 SUBJECT TITLE
97m²A형 단위세대
냉매배관 평면도(확장형)

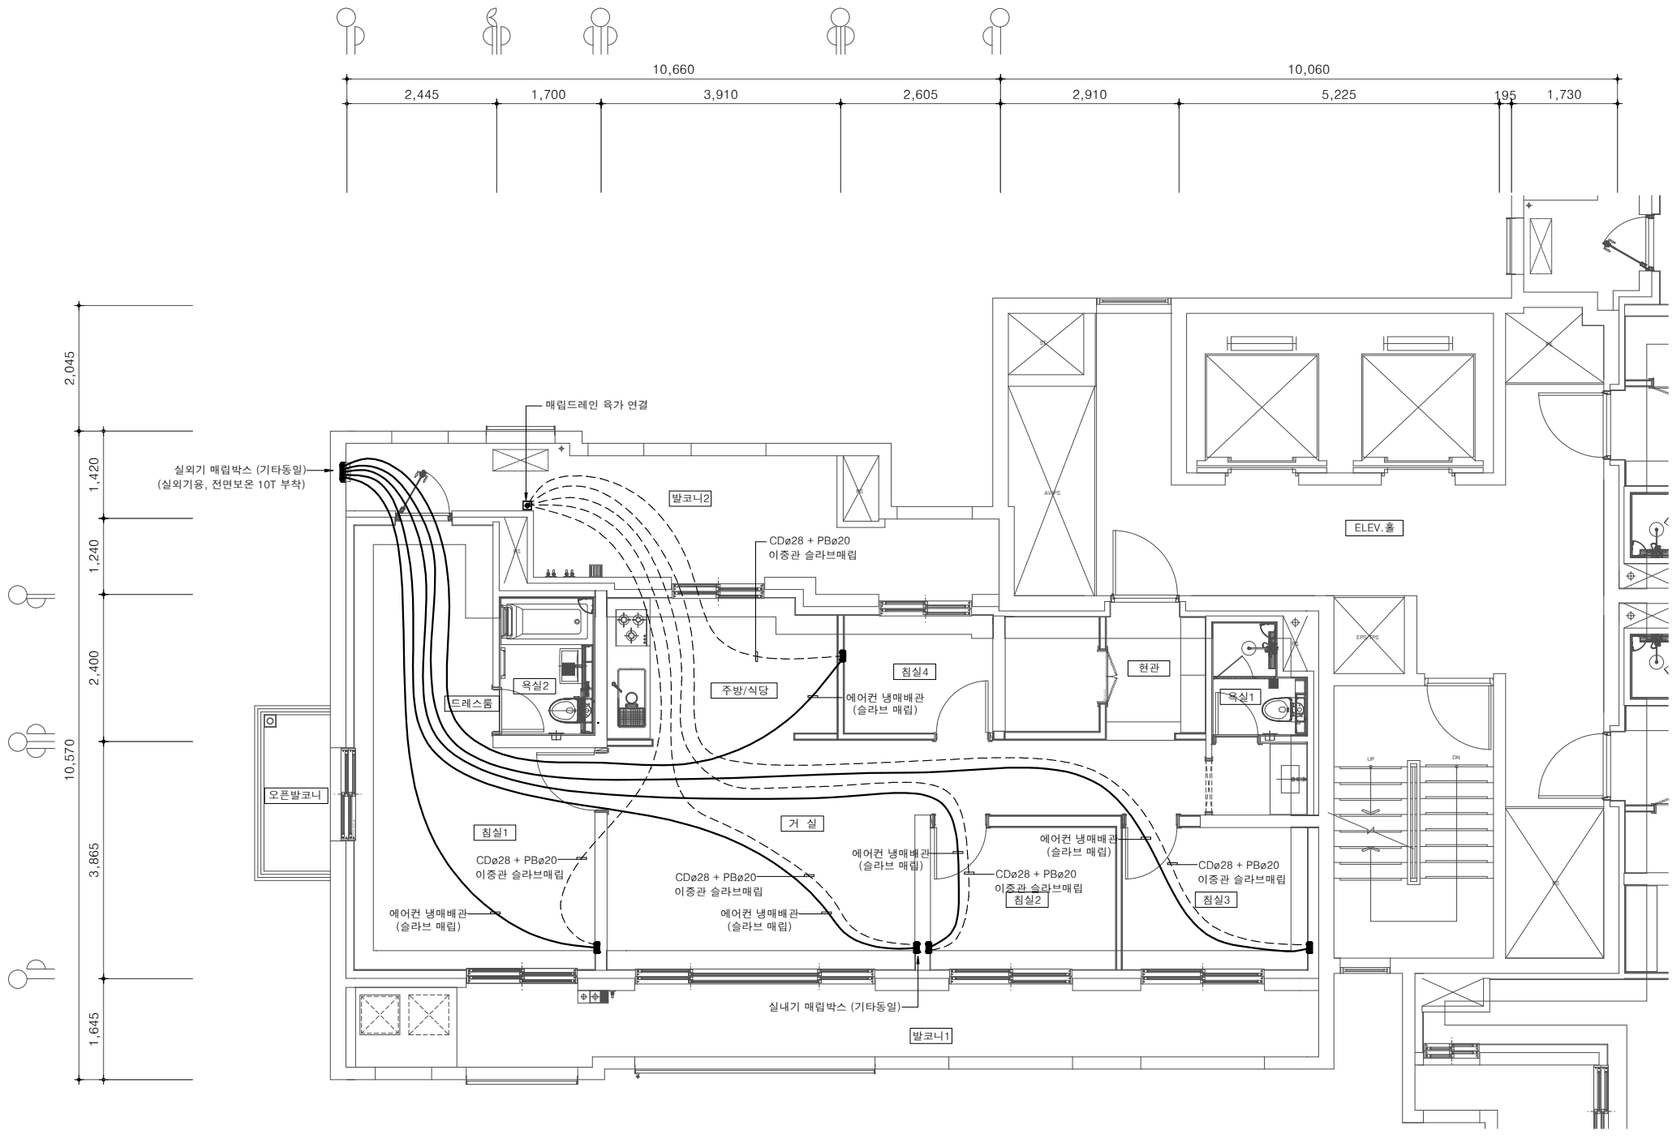

에어컨 냉매배관 일람표

구 분	가 스 관	액 관	통 신 선	전 원 선
침 실1	12.7	6.35	VCTF 1.5x3C	CV 4.0x3C
침 실2	12.7	6.35	VCTF 1.5x3C	CV 4.0x3C
침 실3	12.7	6.35	VCTF 1.5x3C	CV 4.0x3C
거 실	15.88	6.35	VCTF 1.5x3C	CV 4.0x3C

M 97m²B형 단위세대 냉매배관 평면도(기본형)

축 척 : 1/100

경기주택도시공사
GYEONGGI HOUSING & URBAN DEVELOPMENT CORPORATION

설계명 PROJECT TITLE

화성동탄(2)A76-2BL
민간참여 공동주택사업

주기 NOTE

NO	DATE	REVISION DESCRIPTION	APPD
△			
△			
△			
△			

설 계
DESIGN

대표전화

축 척	SCALE
A1	1 / 50
A3	1 / 100


일 자 DATE
2025. 12.

설계번호 PROJECT NO.
AR - 23 - 026

도면화일명 DWG. FILE NAME

도면번호 SHEET NO.
MH – 025

도면명 SUBJECT TITLE
97m²B형 단위세대
냉매배관 평면도(기본형)

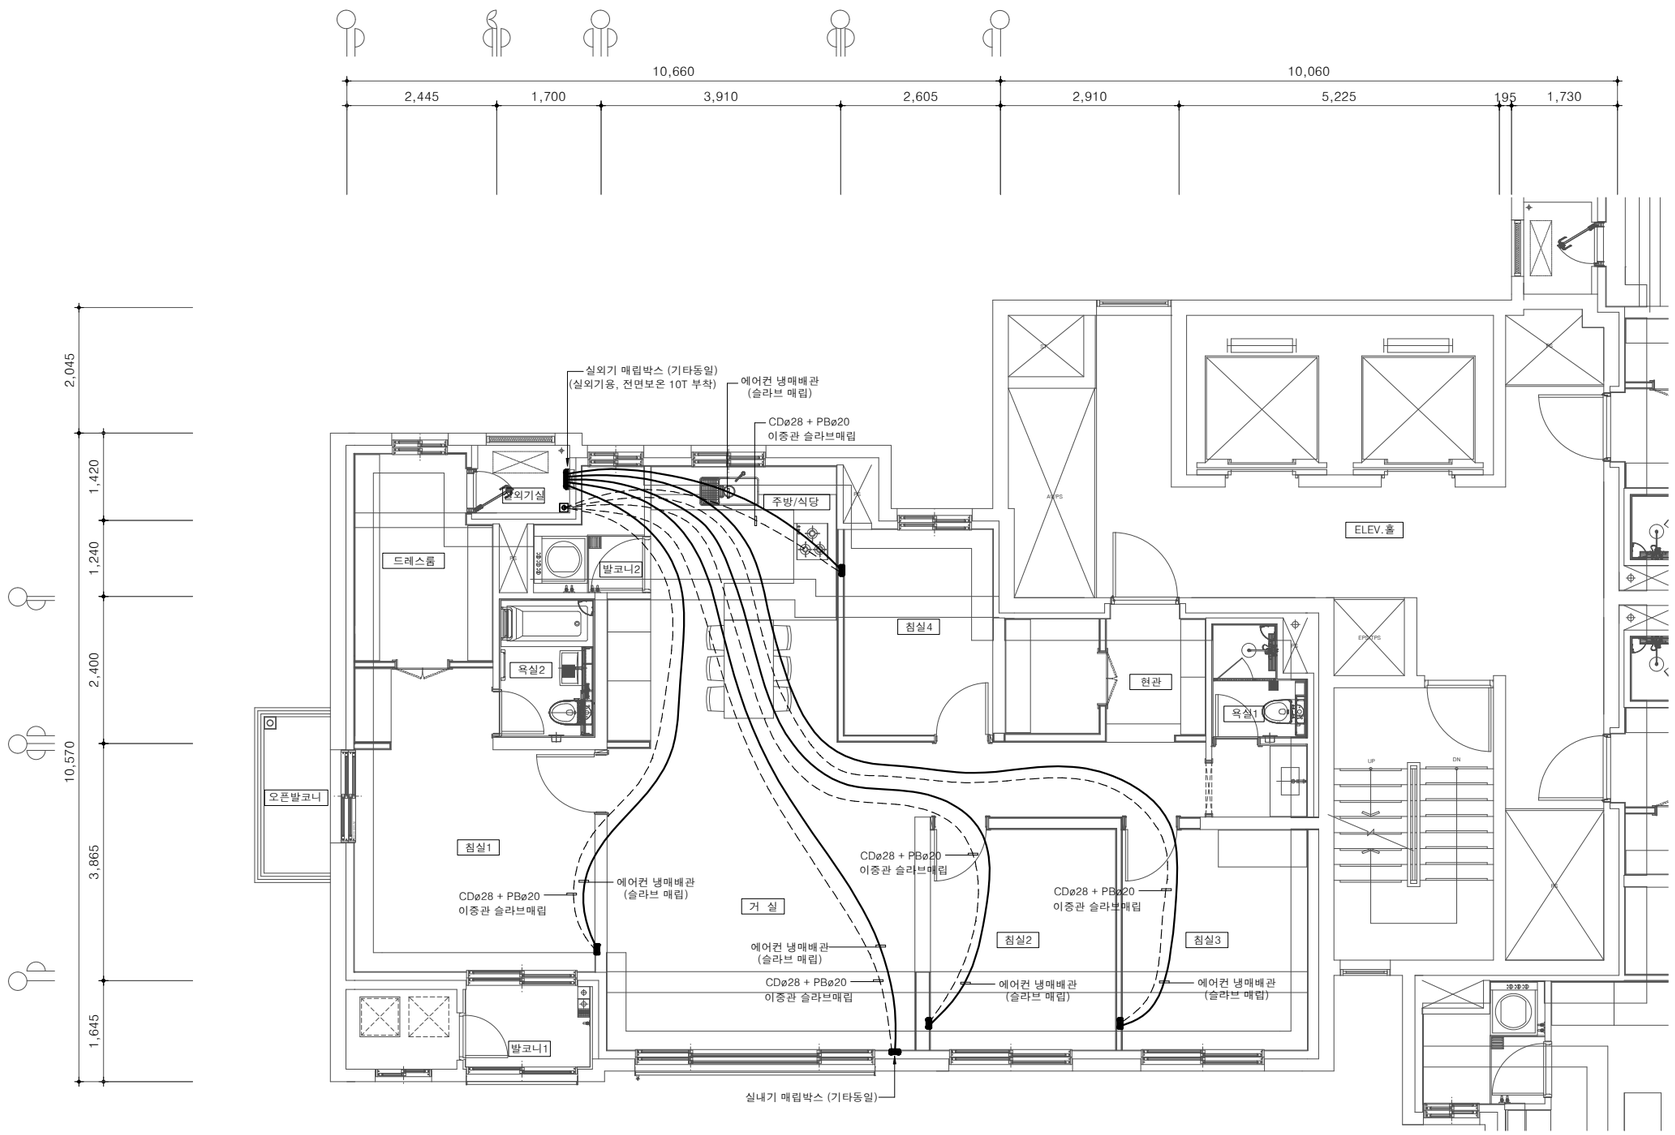

에어컨 냉매배관 일람표

구 분	가 스 관	액 관	통 신 선	전 원 선
침 실1	12.7	6.35	VCTF 1.5x3C	CV 4.0x3C
침 실2	12.7	6.35	VCTF 1.5x3C	CV 4.0x3C
침 실3	12.7	6.35	VCTF 1.5x3C	CV 4.0x3C
거 실	15.88	6.35	VCTF 1.5x3C	CV 4.0x3C

97m²B형 단위세대 냉매배관 평면도(확장형)

축 척 : 1/100

경기주택도시공사
GYEONGGI HOUSING & URBAN DEVELOPMENT CORPORATION

설계명 PROJECT TITLE

화성동탄(2)A76-2BL
민간참여 공동주택사업

주기 NOTE

NO	DATE	REVISION DESCRIPTION	APPD

설 계
DESIGN

대표전화

축 척	SCALE
A1	1 / 50
A3	1 / 100


일 자 DATE
2025. 12.

설계번호 PROJECT NO.
AR - 23 - 026

도면화일명 DWG. FILE NAME

도면번호 SHEET NO.
MH - 026

도면명 SUBJECT TITLE
97m²B형 단위세대
냉매배관 평면도(확장형)

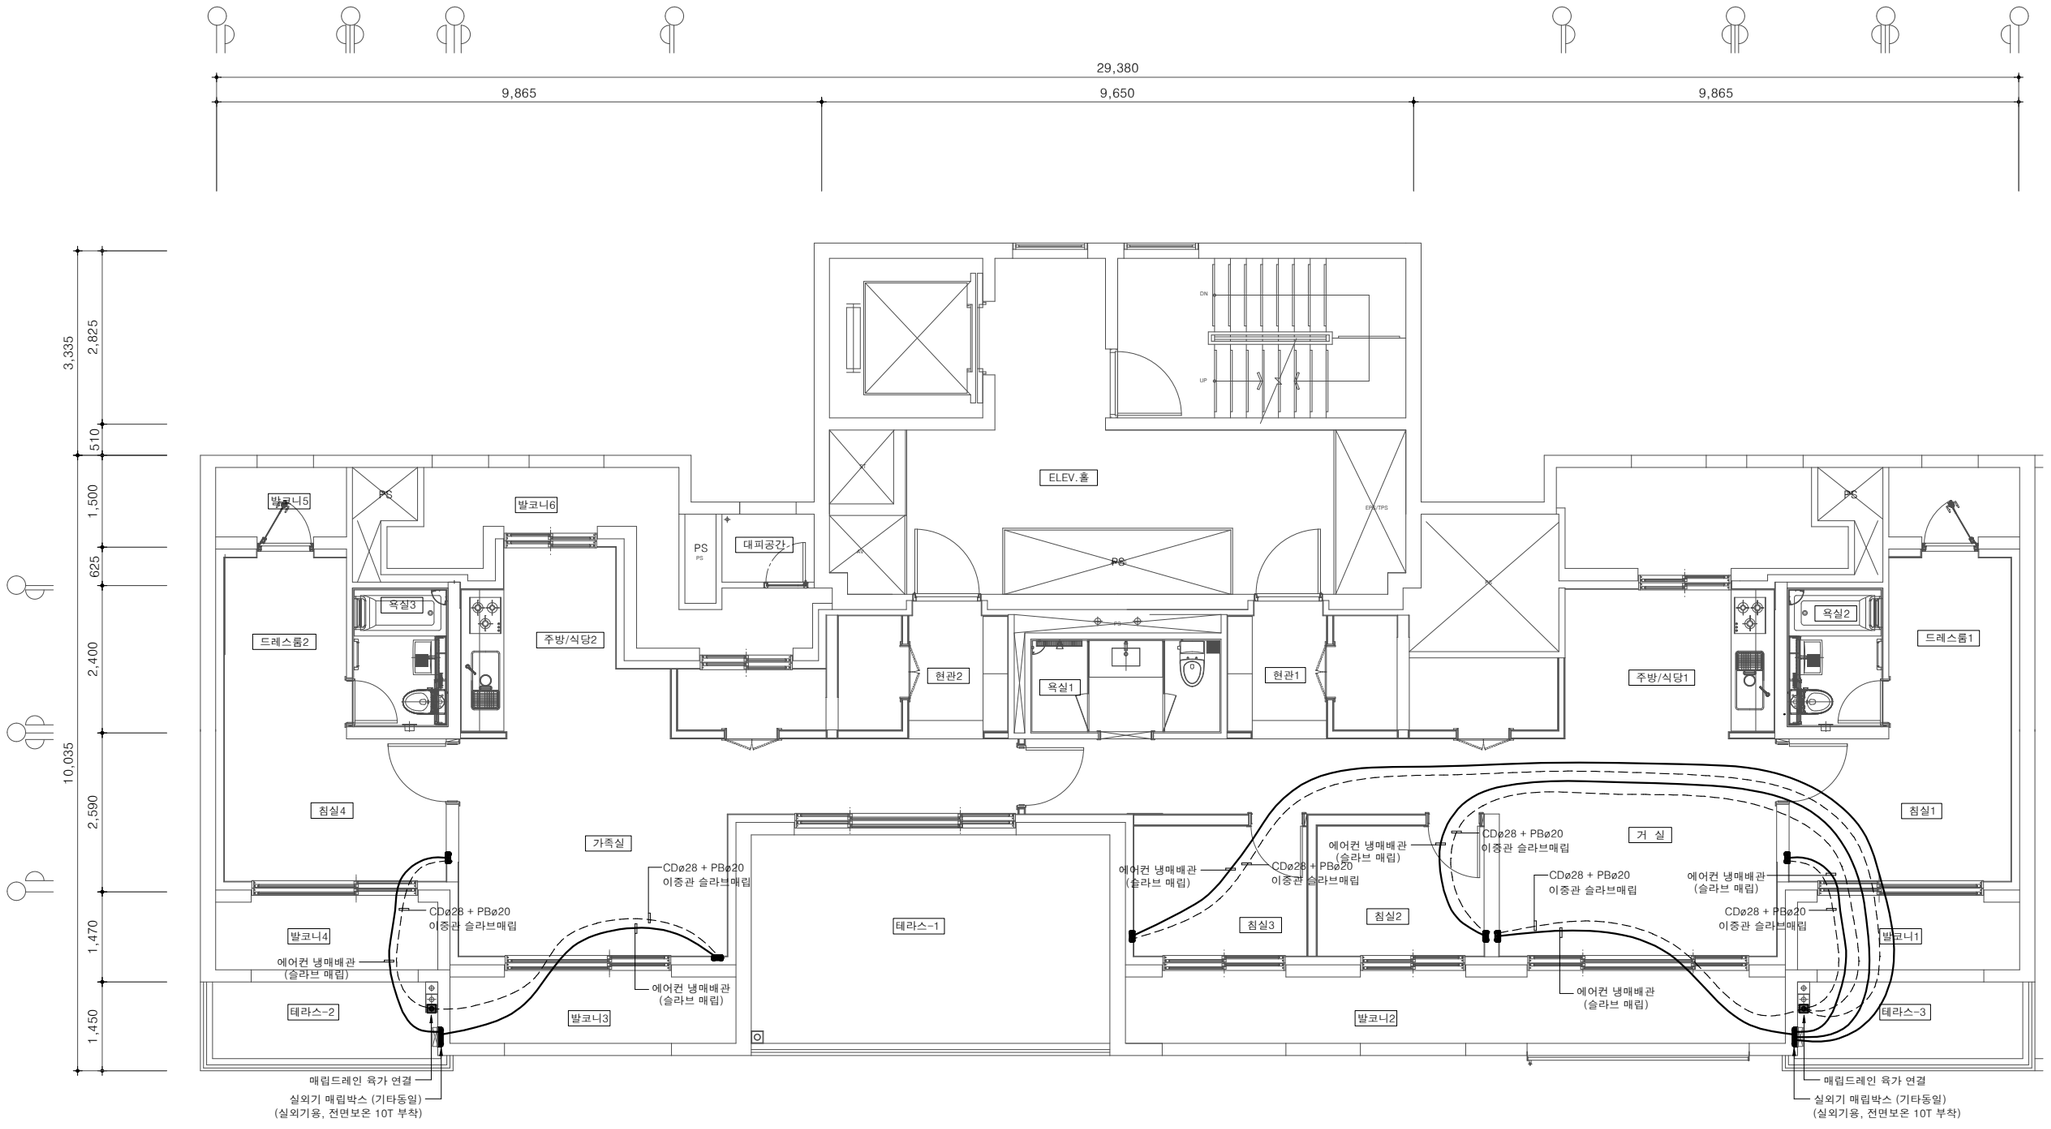

에어컨 냉매배관 일람표

구 분	가 스 관	액 관	통 신 선	전 원 선
침 실1	12.7	6.35	VCTF 1.5x3C	CV 4.0x3C
침 실2	12.7	6.35	VCTF 1.5x3C	CV 4.0x3C
침 실3	12.7	6.35	VCTF 1.5x3C	CV 4.0x3C
침 실4	12.7	6.35	VCTF 1.5x3C	CV 4.0x3C
거 실	15.88	6.35	VCTF 1.5x3C	CV 4.0x3C
가족실	15.88	6.35	VCTF 1.5x3C	CV 4.0x3C

142m²P형 단위세대 냉매배관 평면도(기본형)

축 척 : 1/100

경기주택도시공사
GYEONGGI HOUSING & URBAN DEVELOPMENT CORPORATION

설계명 PROJECT TITLE

화성동탄(2)A76-2BL
민간참여 공동주택사업

주기 NOTE

NO	DATE	REVISION DESCRIPTION	APPD
△			
△			
△			
△			

설 계
DESIGN

대표전화

축 척	SCALE
A1	1 / 50
A3	1 / 100


일 자 DATE
2025. 12.

설계번호 PROJECT NO.
AR - 23 - 026

도면화일명 DWG. FILE NAME

도면번호 SHEET NO.
MH - 027

도면명 SUBJECT TITLE
142m²A형 단위세대
냉매배관 평면도(기본형)

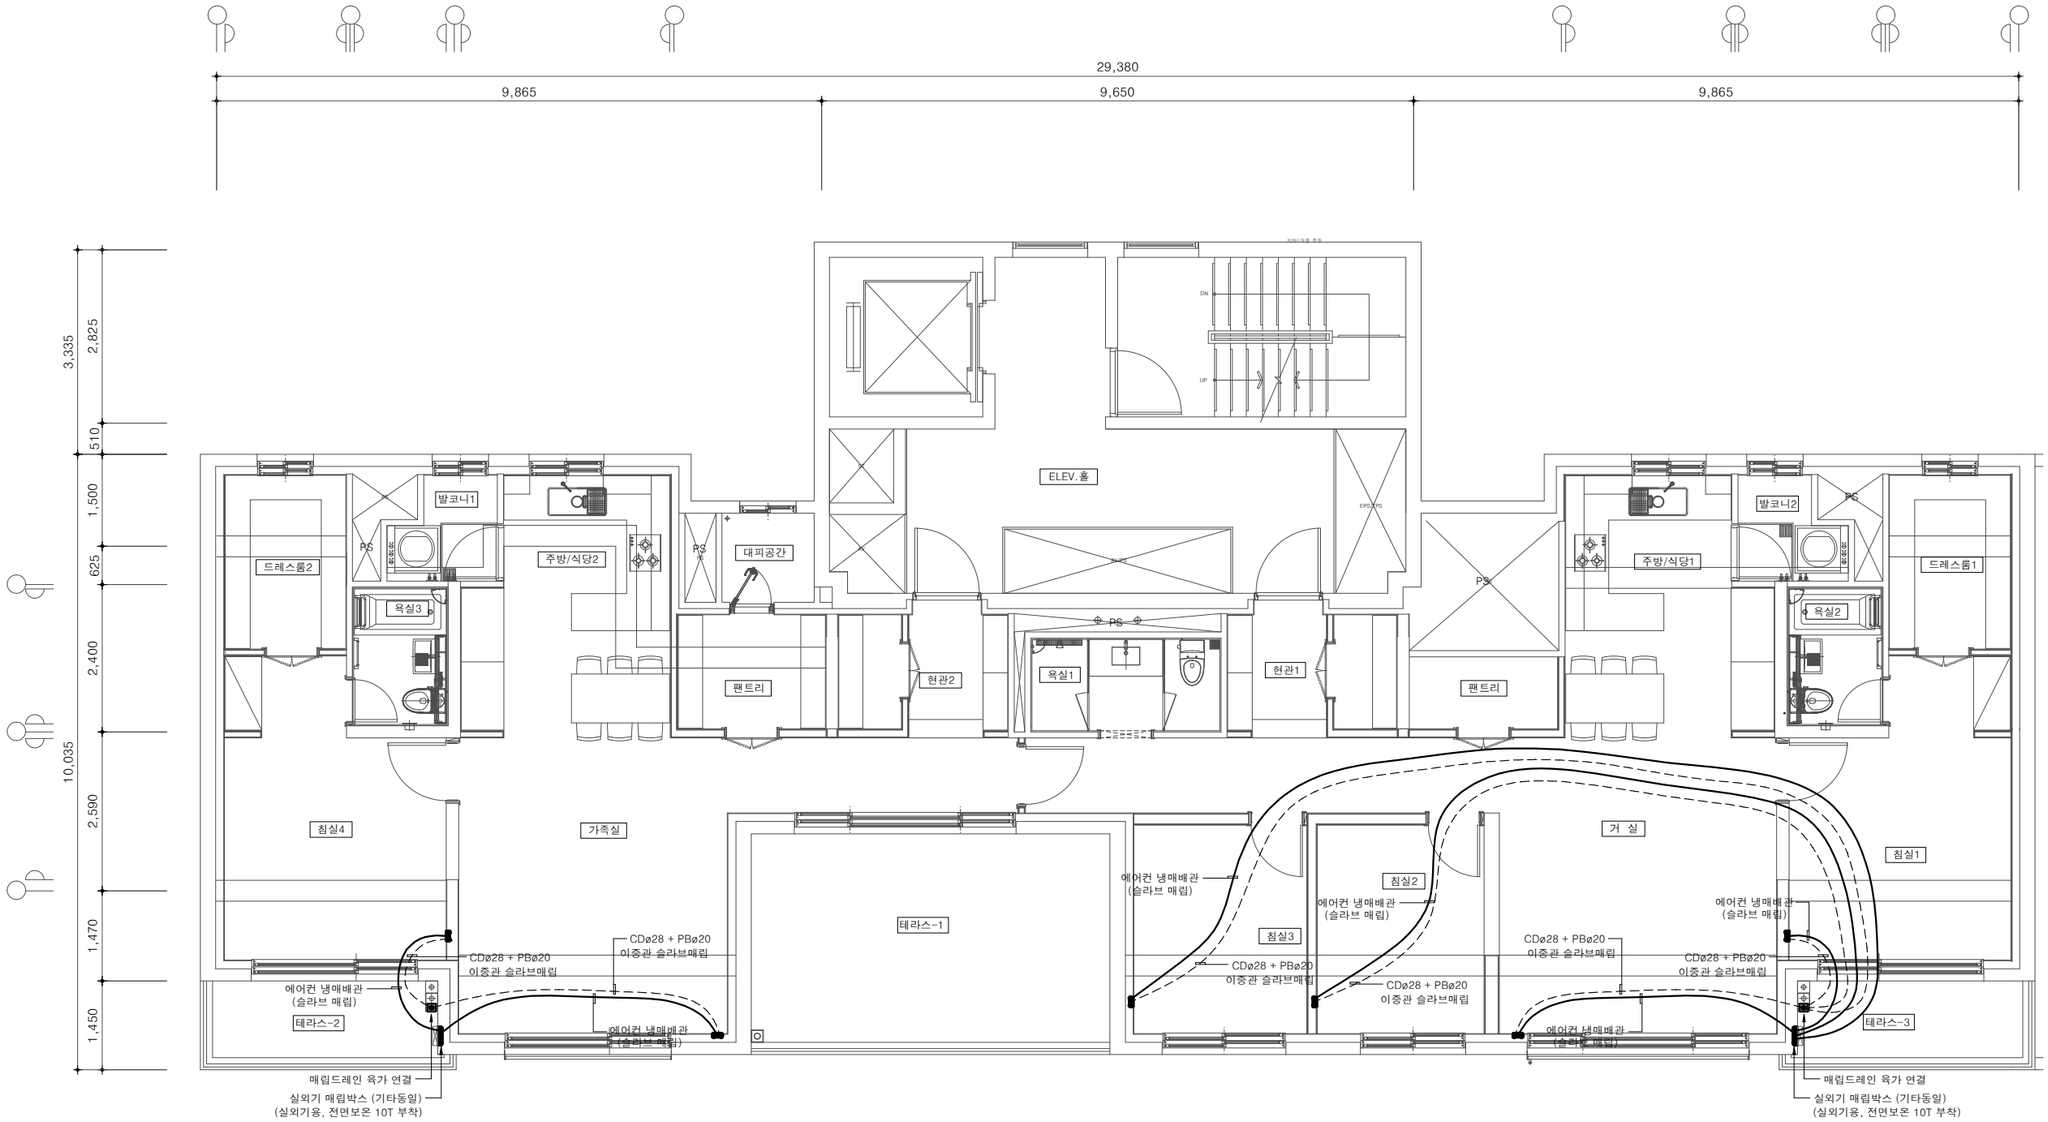

에어컨 냉매배관 일람표

구 분	가 스 관	액 관	통 신 선	전 원 선
침 실1	12.7	6.35	VCTF 1.5x3C	CV 4.0x3C
침 실2	12.7	6.35	VCTF 1.5x3C	CV 4.0x3C
침 실3	12.7	6.35	VCTF 1.5x3C	CV 4.0x3C
침 실4	12.7	6.35	VCTF 1.5x3C	CV 4.0x3C
거 실	15.88	6.35	VCTF 1.5x3C	CV 4.0x3C
가족실	15.88	6.35	VCTF 1.5x3C	CV 4.0x3C

M 142m²P형 단위세대 냉매배관 평면도(확장형)

축 척 : 1/100

경기주택도시공사
GYEONGGI HOUSING & URBAN DEVELOPMENT CORPORATION

설계명 PROJECT TITLE

화성동탄(2)A76-2BL
민간참여 공동주택사업

주기 NOTE

NO	DATE	REVISION DESCRIPTION	APPD

설 계
DESIGN

대표전화

축 척	SCALE
A1	1 / 50
A3	1 / 100


일 자 DATE
2025. 12.

설계번호 PROJECT NO.
AR - 23 - 026

도면화일명 DWG. FILE NAME

도면번호 SHEET NO.
MH - 028

도면명 SUBJECT TITLE
142m²A형 단위세대
냉매배관 평면도(확장형)

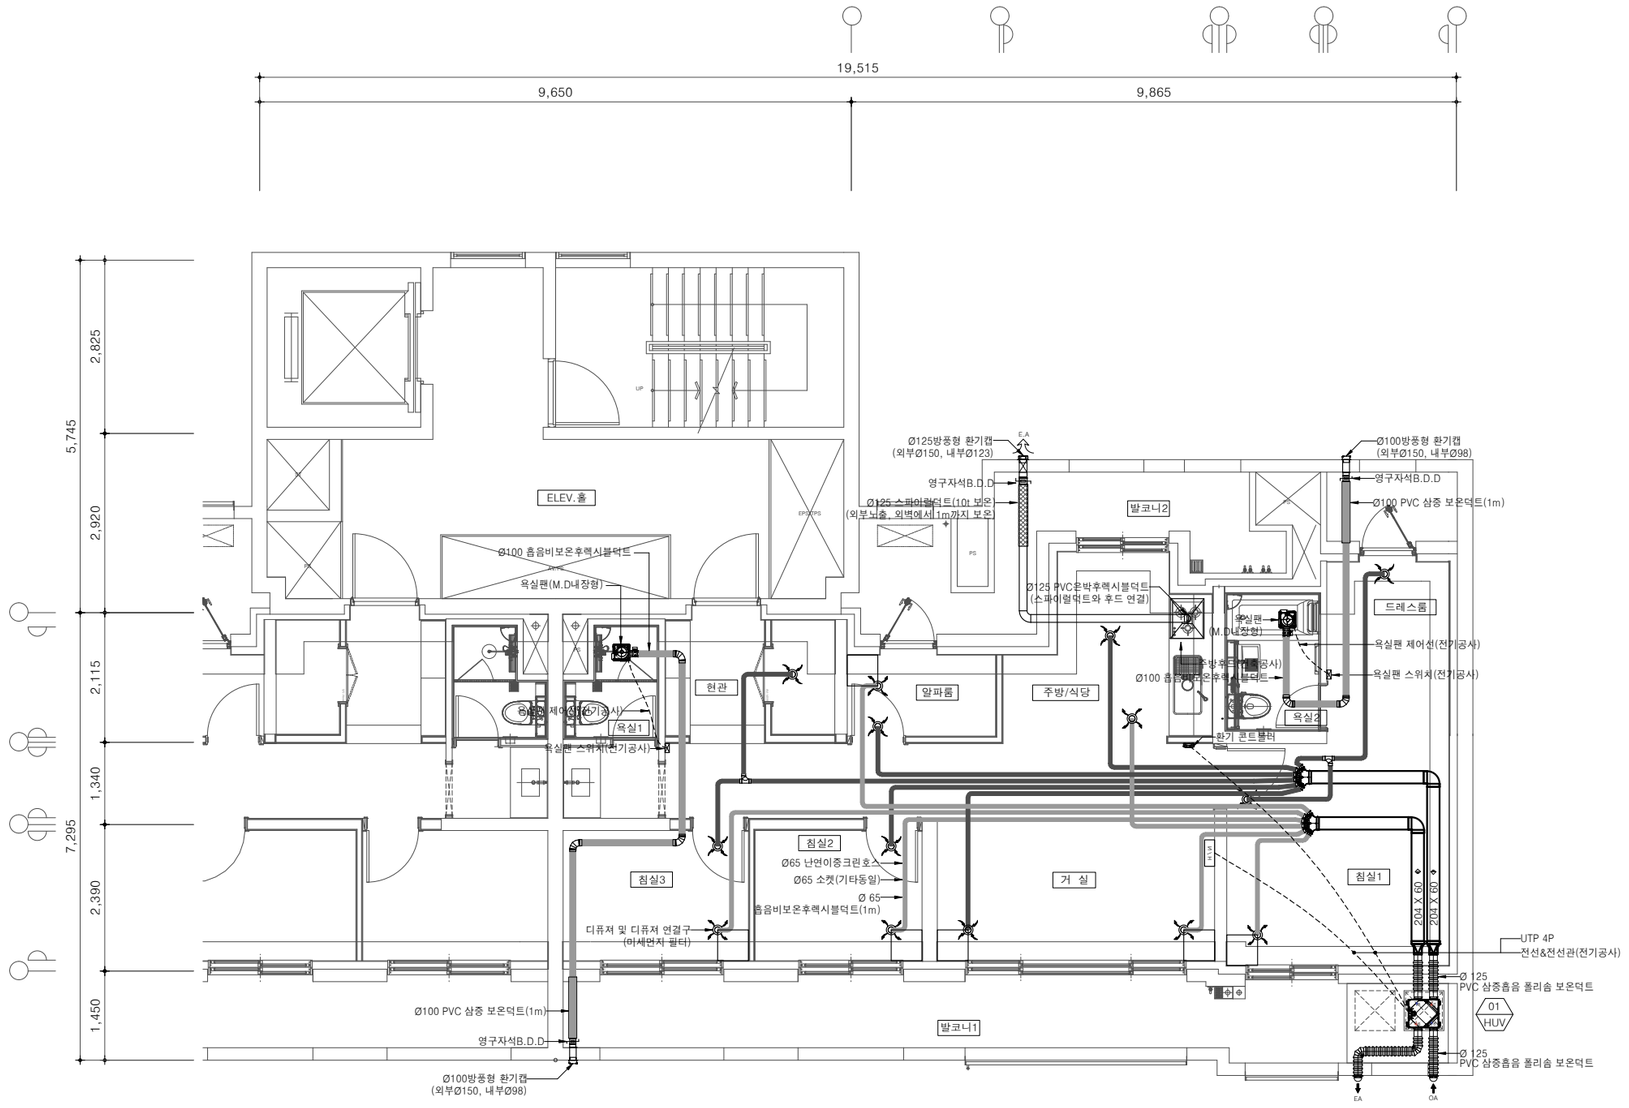

84m²A형 단위세대 환기덕트 평면도(기본형)

축 척 : 1/100

경기주택도시공사
GYEONGGI HOUSING & URBAN DEVELOPMENT CORPORATION

설계명 PROJECT TITLE

화성동탄(2)A76-2BL
민간참여 공동주택사업

주기 NOTE

1. 디퓨저 위치, 수량, 제어반 위치 및 장비사양은 현장여건에 따라 변경 될 수 있음.
2. 환기 콘트롤러 및 욕실팬 스위치는 현장여건에 따라 변경될 수 있음.
3. 환기용 급,배기 덕트의 디퓨저 연결 부분은 흡음비보온 후렉시블덕트 (길이 1m)를 설치하고, 이후 난연이중 크린호스를 설치
4. 디퓨저 연결구에는 미세먼지 필터를 설치
5. 덕트 루트는 현장여건에 따라 변경될 수 있음.
6. 예시와 같은 역풍방지캡은 직배기의 환기캡에 사용하며, 전열교환기의 환기캡은 상단의 도피로가 없는 타입으로 시공한다.
7. 주방후드 직배기는 스파이럴덕트를 통하여 외부로 배출하며, 외부 노출 및 외벽으로부터 1m까지는 10t 보온한다.
8. 욕실 직배기는 욕실에 고정압환을 설치하고 덕트를 통하여 외부로 배출한다. 변경 될 수 있음.
9. 욕실배출덕트 중 욕실 내부에는 흡음 비보온 후렉시블덕트를 설치하고, 거실 등에 설치되는 배기덕트는 난연이중크린호스를 설치하며, 외벽에서 약 1m까지는 PVC 삼중보온덕트를 설치한다.
10. 20l상의 통합 배기를 하는 경우 연결되는 각 실의 배기팬은 MD 부착형을 적용한다.

NO	DATE	REVISION DESCRIPTION	APPD
△			
△			
△			
△			

설 계
DESIGN

대표전화

축 척	SCALE
A1	1 / 50
A3	1 / 100


일 자 DATE
2025. 12.

설계번호 PROJECT NO.
AR - 23 - 026

도면화일명 DWG. FILE NAME

도면번호 SHEET NO.
MD - 001

도면명 SUBJECT TITLE
84m²A형 단위세대
환기덕트 평면도(기본형)

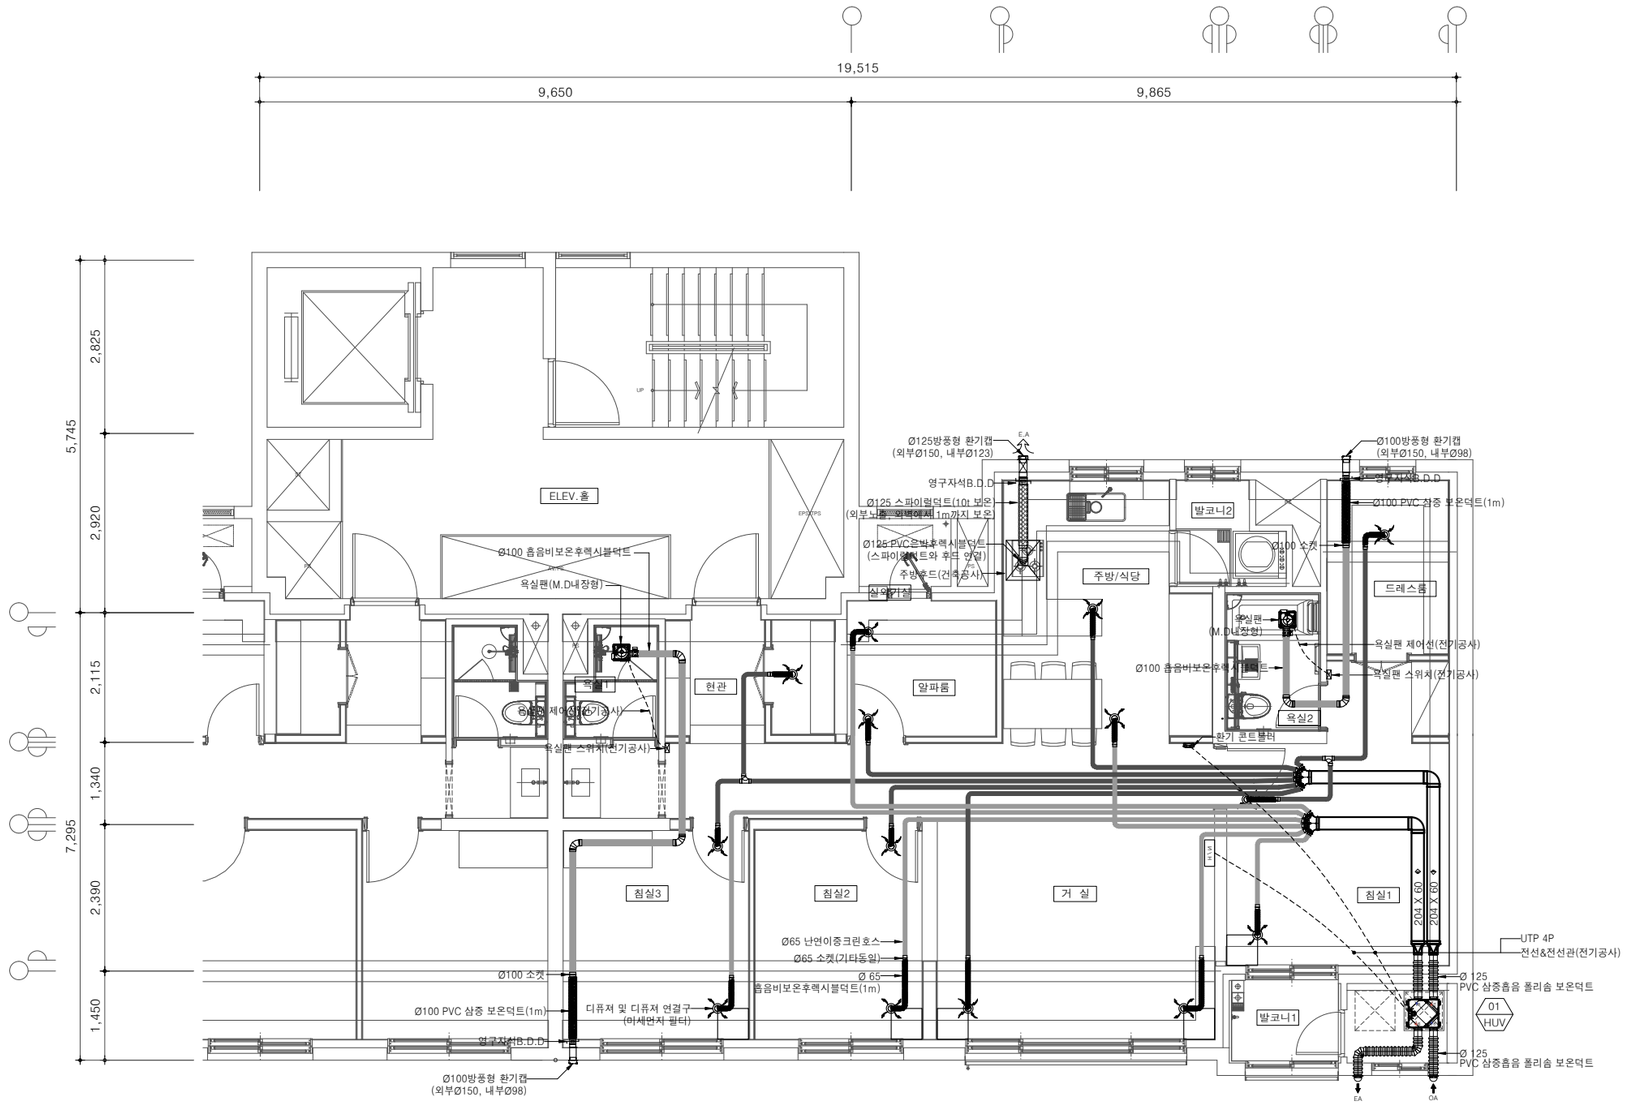

84m²A형 단위세대 환기덕트 평면도(확장형)

축 척 : 1/100

경기주택도시공사
GYEONGGI HOUSING & URBAN DEVELOPMENT CORPORATION

설계명 PROJECT TITLE

화성동탄(2)A76-2BL 민간참여 공동주택사업

주기 NOTE

1. 디퓨저 위치, 수량, 제어반 위치 및 장비사양은 현장여건에 따라 변경 될 수 있음.
2. 환기 콘트롤러 및 욕실팬 스위치는 현장여건에 따라 변경될 수 있음.
3. 환기옹 급,배기 덕트의 디퓨저 연결 부분은 흡음비보온 후렉시블덕트 (길이 1m)를 설치하고, 이후 난연이중 크린호스를 설치
4. 디퓨저 연결구에는 미세먼지 필터를 설치
5. 덕트 루트는 현장여건에 따라 변경될 수 있음.
6. 예시와 같은 역풍방지캡은 직배기의 환기캡에 사용하며, 전열교환기의 환기캡은 상단의 도피로가 없는 타입으로 시공한다.
7. 주방후드 직배기는 스파이럴덕트를 통하여 외부로 배출하며, 외부 노출 및 외벽으로부터 1m까지는 10t 보온한다.
8. 욕실 직배기는 욕실에 고정압환을 설치하고 덕트를 통하여 외부로 배출한다. 변경 될 수 있음.
9. 욕실배출덕트 중 욕실 내부에는 흡음 비보온 후렉시블덕트를 설치하고, 거실 등에 설치되는 배기덕트는 난연이중크린호스를 설치하며, 외벽에서 약 1m까지는 PVC 삼중보온덕트를 설치한다.
10. 20상의 통합 배기를 하는 경우 연결되는 각 실의 배기팬은 MD 부착형을 적용한다.

NO	DATE	REVISION DESCRIPTION	APPD
△			
△			
△			
△			

설 계
DESIGN

대표전화

축 척	SCALE
A1	1 / 50
A3	1 / 100

일 자 DATE 2025. 12.


설계번호 PROJECT NO. AR - 23 - 026

도면화일명 DWG. FILE NAME

도면번호 SHEET NO. MD – 002

도면명 SUBJECT TITLE

84m²A형 단위세대
환기덕트 평면도(확장형)

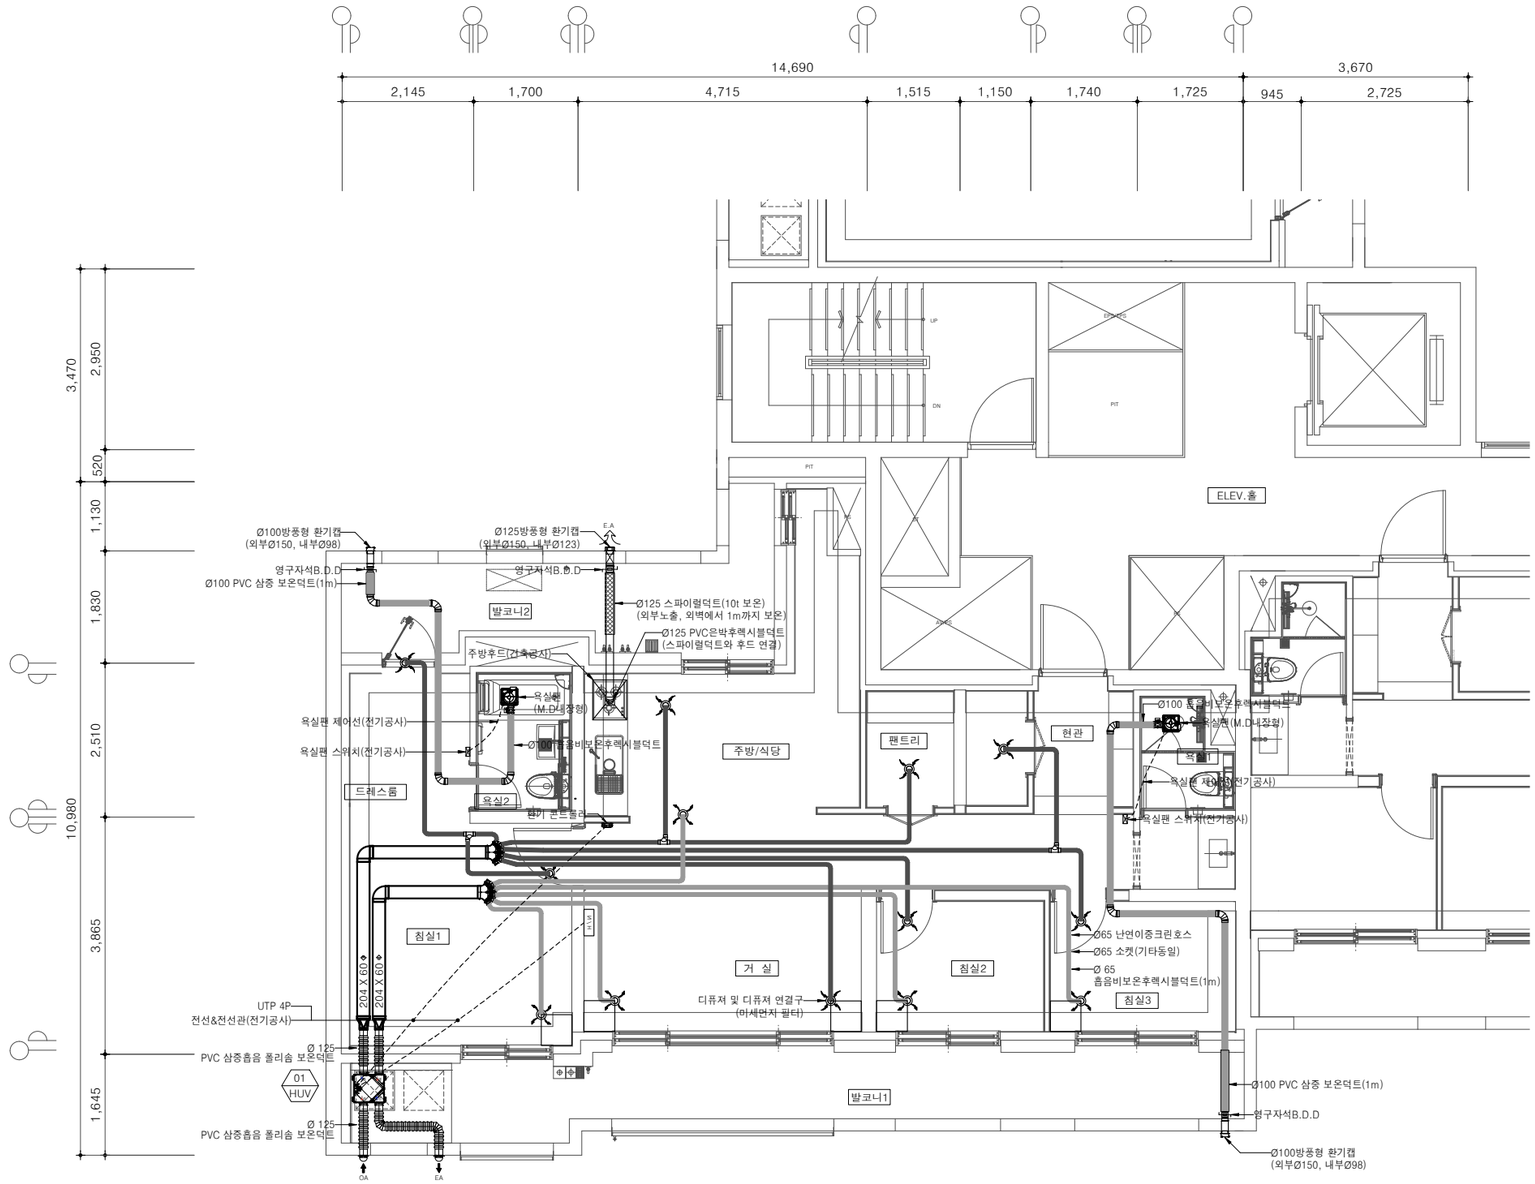

84m²B형 단위세대 환기덕트 평면도(기본형)

축 척 : 1/100

경기주택도시공사
GYEONGGI HOUSING & URBAN DEVELOPMENT CORPORATION

설계명 PROJECT TITLE

화성동탄(2)A76-2BL
민간참여 공동주택사업

주기 NOTE

1. 디퓨저 위치, 수량, 제어반 위치 및 장비사양은 현장여건에 따라 변경 될 수 있음.
2. 환기 콘트롤러 및 욕실팬 스위치는 현장여건에 따라 변경될 수 있음.
3. 환기용 급,배기 덕트의 디퓨저 연결 부분은 흡음비보온 후렉시블덕트 (길이 1m)를 설치하고, 이후 난연이중 크린호스를 설치
4. 디퓨저 연결구에는 미세먼지 필터를 설치
5. 덕트 루트는 현장여건에 따라 변경될 수 있음.
6. 에시와 같은 역풍방지캡은 직배기의 환기캡에 사용하며, 전열교환기의 환기캡은 상단의 도피로가 없는 타입으로 시공한다.
7. 주방후드 직배기는 스파이럴덕트를 통하여 외부로 배출하며, 외부 노출 및 외벽으로부터 1m까지는 10t 보온한다.
8. 욕실 직배기는 욕실에 고정압환을 설치하고 덕트를 통하여 외부로 배출한다. 변경 될 수 있음.
9. 욕실배출덕트 중 욕실 내부에는 흡음 비보온 후렉시블덕트를 설치하고, 거실 등에 설치되는 배기닥트는 난연이중크린호스를 설치하며, 외벽에서 약 1m까지는 PVC 삼중보온덕트를 설치한다.
10. 2이상의 통합 배기를 하는 경우 연결되는 각 실의 배기팬은 MD 부착형을 적용한다.

NO	DATE	REVISION DESCRIPTION	APPD
△			
△			
△			
△			

설 계
DESIGN

대표전화

축 척	SCALE
A1	1 / 50
A3	1 / 100


일 자 DATE
2025. 12.

설계번호 PROJECT NO.
AR - 23 - 026

도면화일명 DWG. FILE NAME

도면번호 SHEET NO.
MD - 003

도면명 SUBJECT TITLE
84m²B형 단위세대
환기덕트 평면도(기본형)

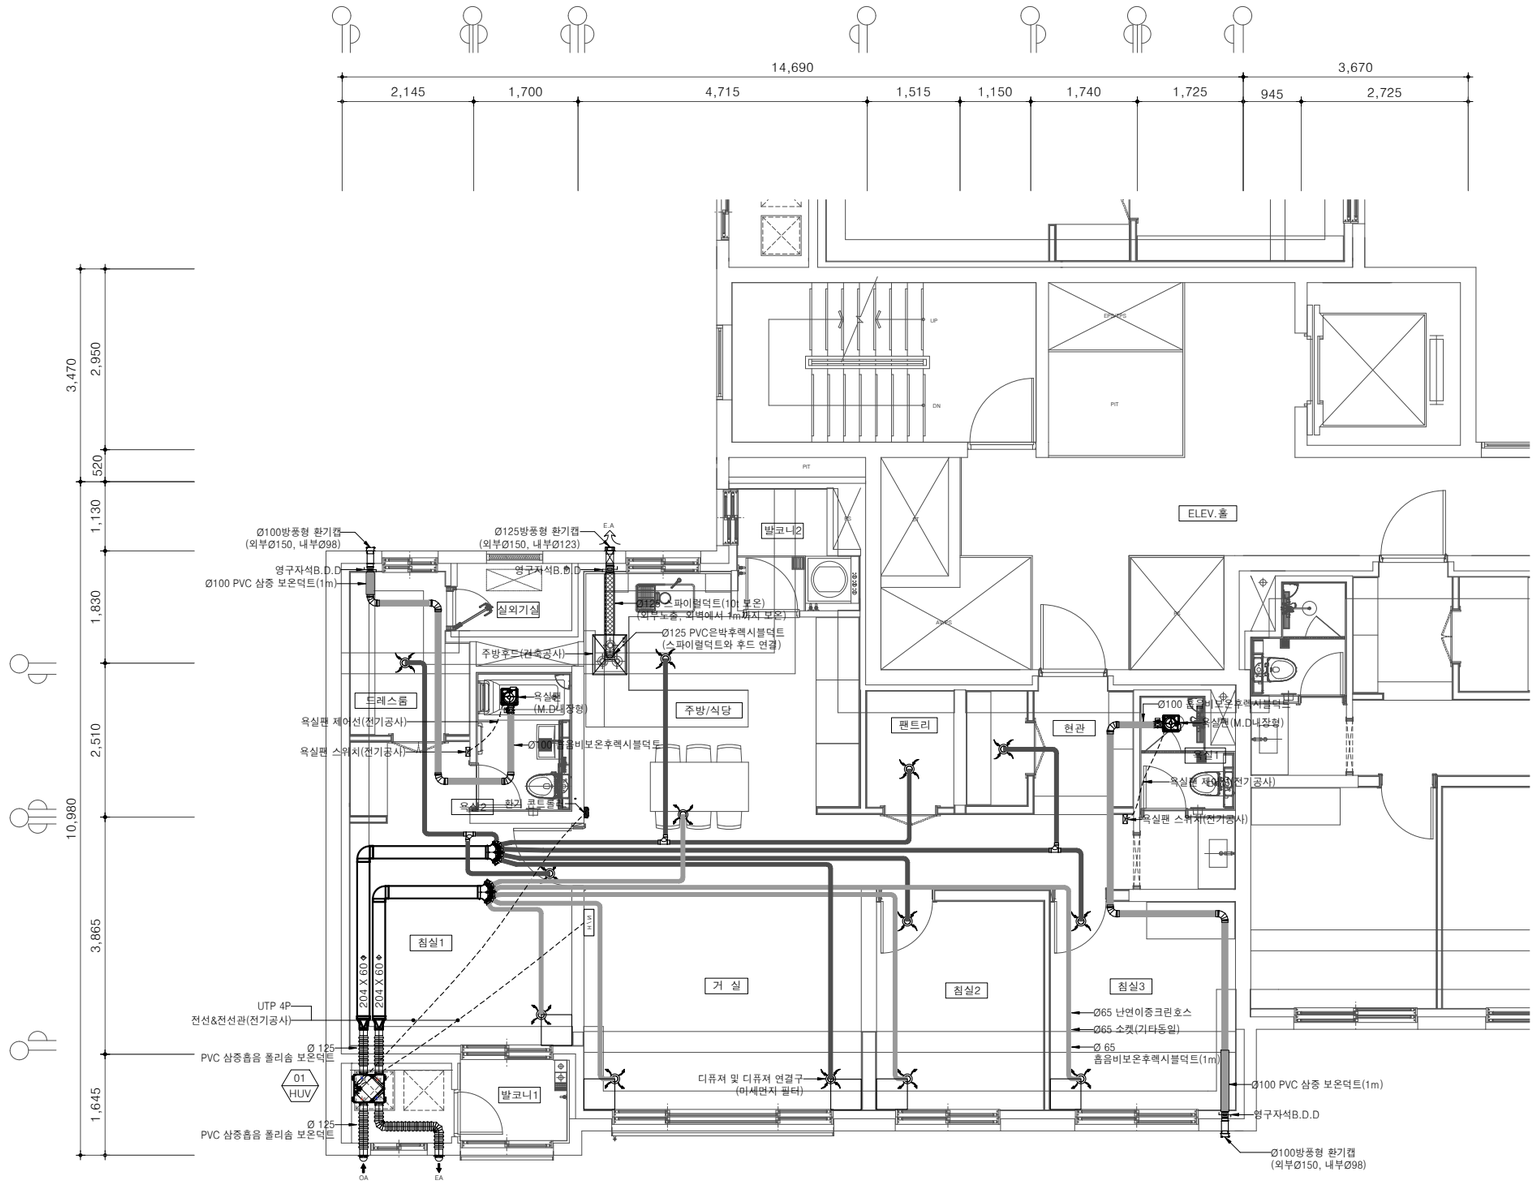

84m²B형 단위세대 환기덕트 평면도(확장형)

축 척 : 1/100

경기주택도시공사
GYEONGGI HOUSING & URBAN DEVELOPMENT CORPORATION

설계명 PROJECT TITLE

화성동탄(2)A76-2BL 민간참여 공동주택사업

주기 NOTE

1. 디퓨저 위치, 수량, 제어반 위치 및 장비사양은 현장여건에 따라 변경 될 수 있음.
2. 환기 콘트롤러 및 욕실팬 스위치는 현장여건에 따라 변경될 수 있음.
3. 환기용 급,배기 덕트의 디퓨저 연결 부분은 흡음비보온 후렉시블덕트 (길이 1m)를 설치하고, 이후 난연이중 크린호스를 설치
4. 디퓨저 연결구에는 미세먼지 필터를 설치
5. 덕트 루트는 현장여건에 따라 변경될 수 있음.
6. 에시와 같은 역풍방지캡은 직배기의 환기캡에 사용하며, 전열교환기의 환기캡은 상단의 도피로가 없는 타입으로 시공한다.
7. 주방후드 직배기는 스파이럴덕트를 통하여 외부로 배출하며, 외부 노출 및 외벽으로부터 1m까지는 10t 보온한다.
8. 욕실 직배기는 욕실에 고정압환을 설치하고 덕트를 통하여 외부로 배출한다. 변경 될 수 있음.
9. 욕실배출덕트 중 욕실 내부에는 흡음 비보온 후렉시블덕트를 설치하고, 거실 등에 설치되는 배기덕트는 난연이중크린호스를 설치하며, 외벽에서 약 1m까지는 PVC 삼중보온덕트를 설치한다.
10. 20상의 통합 배기를 하는 경우 연결되는 각 실의 배기팬은 MD 부착형을 적용한다.

NO	DATE	REVISION DESCRIPTION	APPD
△			
△			
△			
△			

설 계
DESIGN

대표전화

축 척	SCALE
A1	1 / 50
A3	1 / 100


일 자 DATE
2025. 12.

설계번호 PROJECT NO.
AR - 23 - 026

도면화일명 DWG. FILE NAME

도면번호 SHEET NO.
MD - 004

도면명 SUBJECT TITLE
84m²B형 단위세대
환기덕트 평면도(확장형)

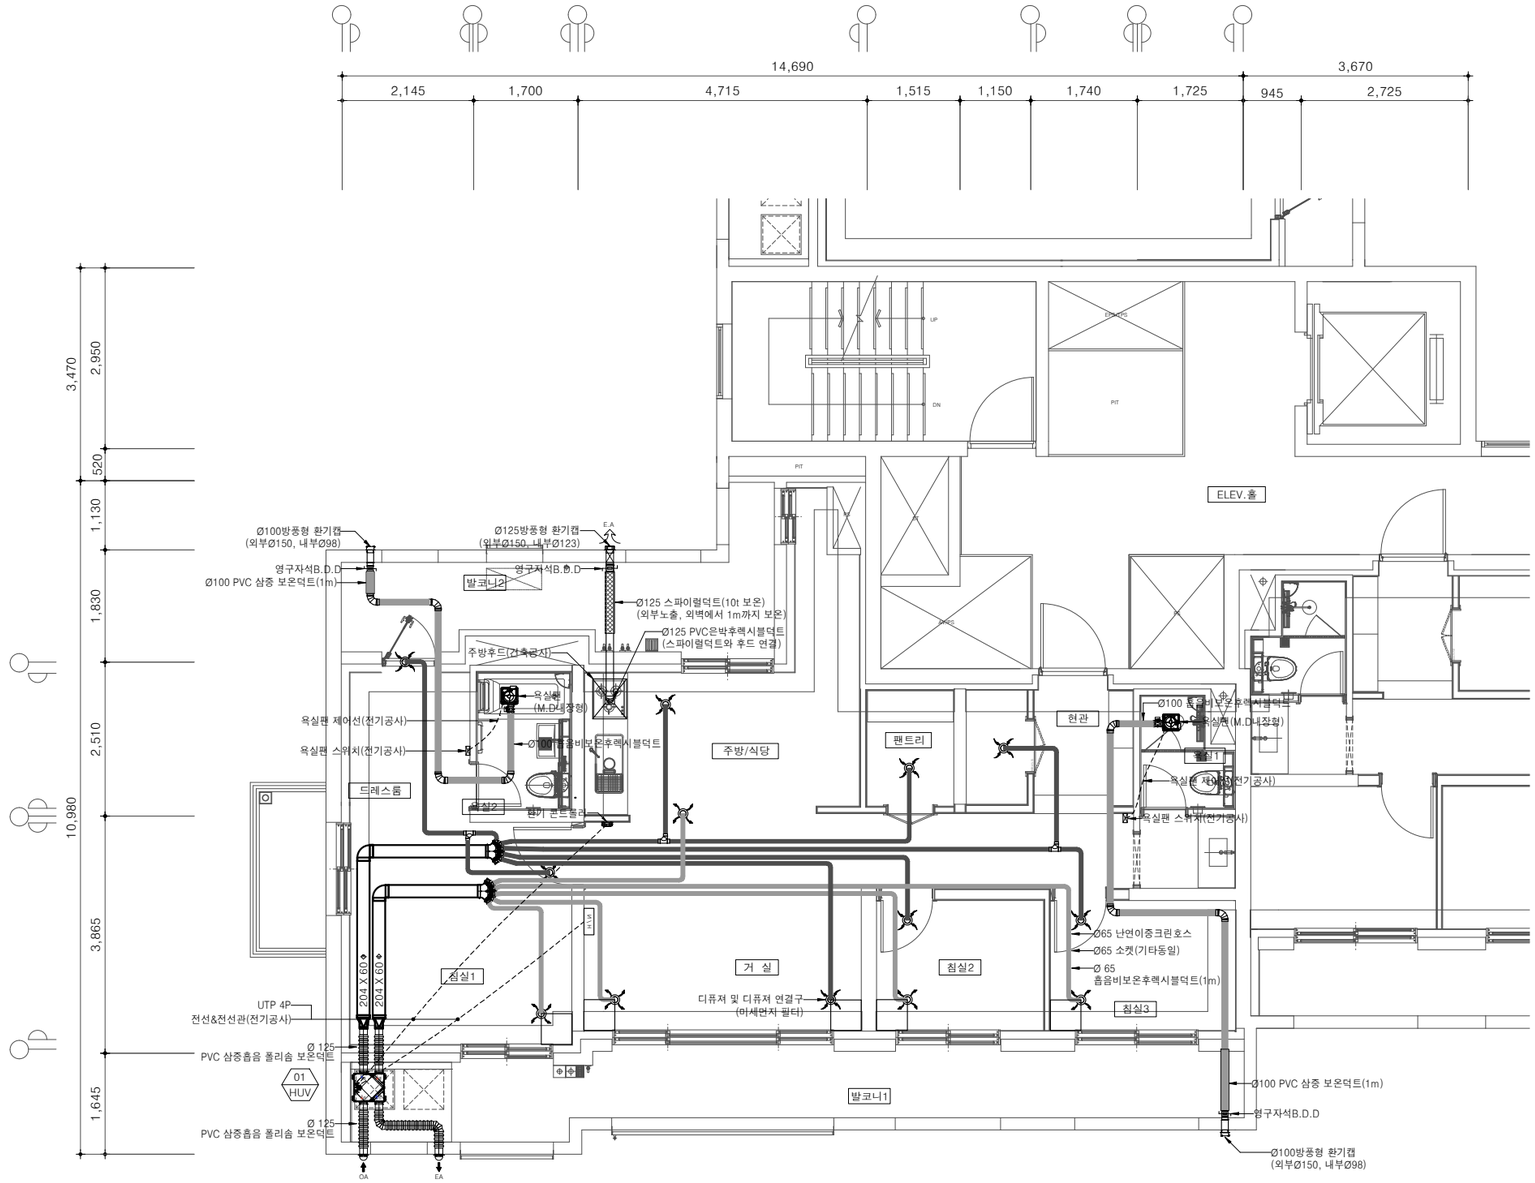

84m²C형 단위세대 환기덕트 평면도(기본형)

축 척 : 1/100

경기주택도시공사
GYEONGGI HOUSING & URBAN DEVELOPMENT CORPORATION

설계명 PROJECT TITLE

화성동탄(2)A76-2BL 민간참여 공동주택사업

주기 NOTE

1. 디퓨저 위치, 수량, 제어반 위치 및 장비사양은 현장여건에 따라 변경 될 수 있음.
2. 환기 콘트롤러 및 욕실팬 스위치는 현장여건에 따라 변경될 수 있음.
3. 환기용 급,배기 덕트의 디퓨저 연결 부분은 흡음비보온 후렉시블덕트 (길이 1m)를 설치하고, 이후 난연이중 크린호스를 설치
4. 디퓨저 연결구에는 미세먼지 필터를 설치
5. 덕트 루트는 현장여건에 따라 변경될 수 있음.
6. 에시와 같은 역풍방지캡은 직배기의 환기캡에 사용하며, 전열교환기의 환기캡은 상단의 도피로가 없는 타입으로 시공한다.
7. 주방후드 직배기는 스파이럴덕트를 통하여 외부로 배출하며, 외부 노출 및 외벽으로부터 1m까지는 10t 보온한다.
8. 욕실 직배기는 욕실에 고정압환을 설치하고 덕트를 통하여 외부로 배출한다. 변경 될 수 있음.
9. 욕실배출덕트 중 욕실 내부에는 흡음 비보온 후렉시블덕트를 설치하고, 거실 등에 설치되는 배기닥트는 난연이중크린호스를 설치하며, 외벽에서 약 1m까지는 PVC 삼중보온덕트를 설치한다.
10. 2이상의 통합 배기를 하는 경우 연결되는 각 실의 배기팬은 MD 부착형을 적용한다.

NO	DATE	REVISION DESCRIPTION	APPD

설 계
DESIGN

대표전화

축 척	SCALE
A1	1 / 50
A3	1 / 100


일 자 DATE
2025. 12.

설계번호 PROJECT NO.
AR - 23 - 026

도면화일명 DWG. FILE NAME

도면번호 SHEET NO.
MD – 005

도면명 SUBJECT TITLE
84m²C형 단위세대
환기덕트 평면도(기본형)

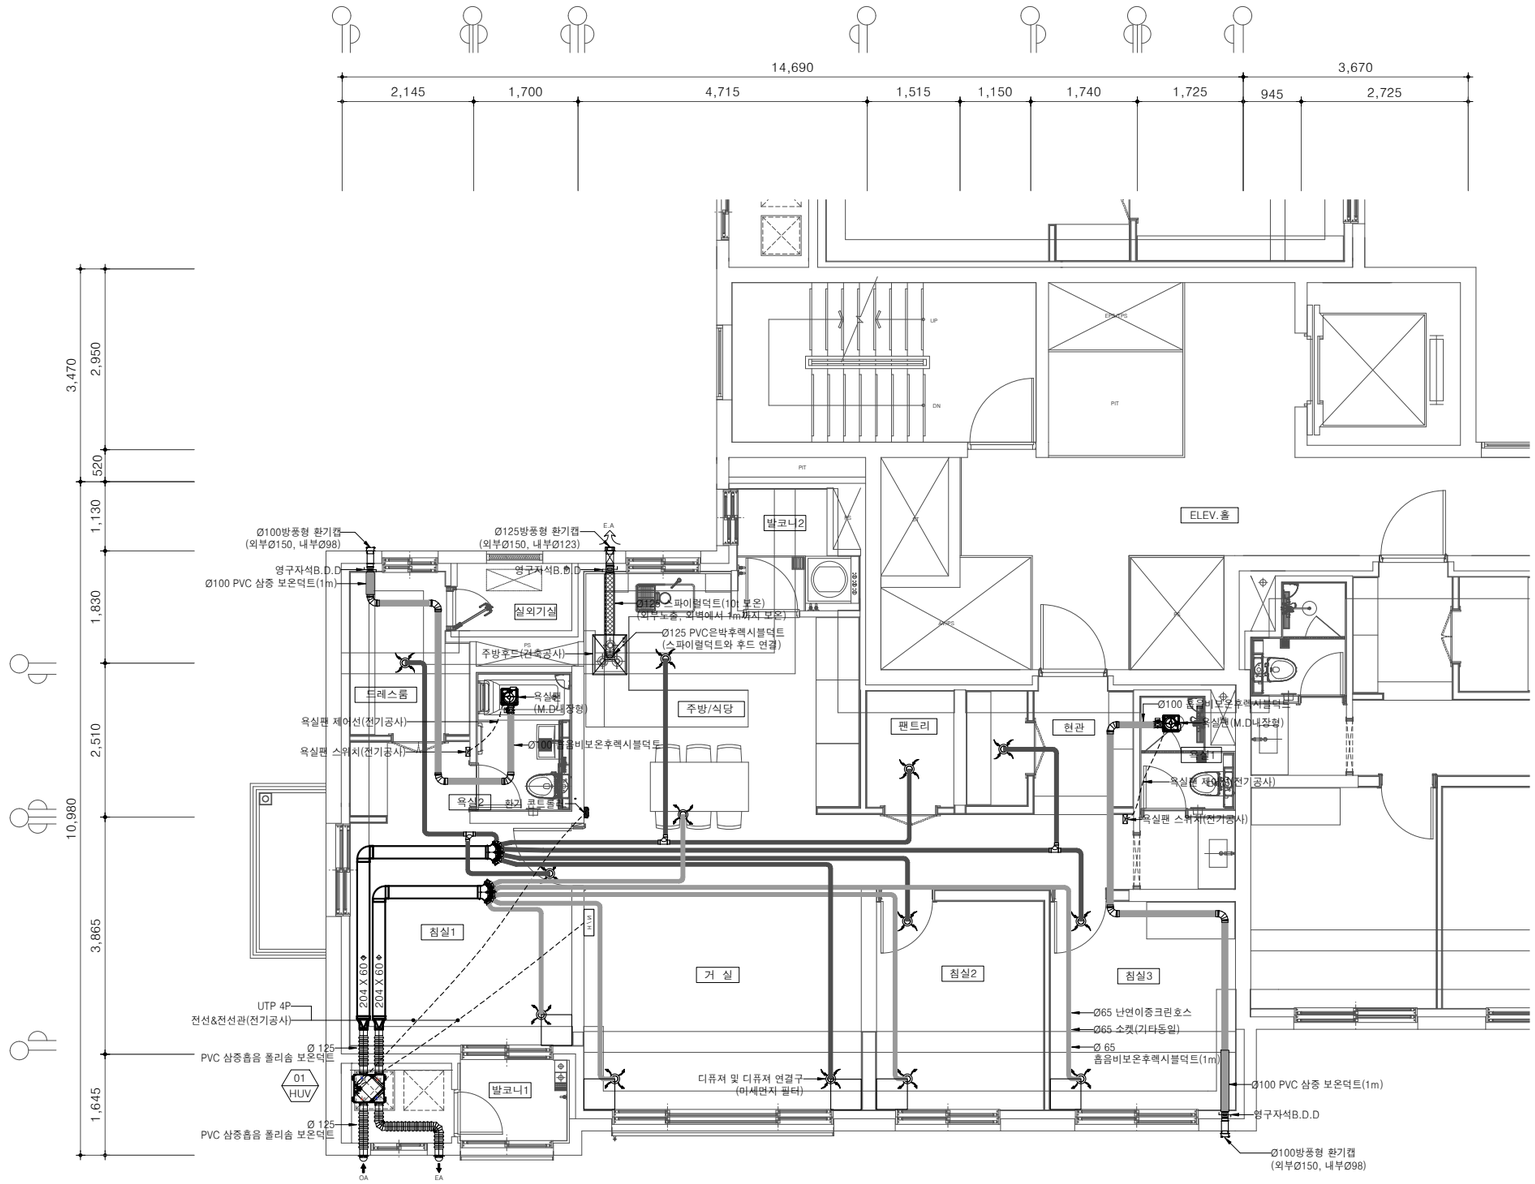

84m²C형 단위세대 환기덕트 평면도(확장형)

축 척 : 1/100

경기주택도시공사
GYEONGGI HOUSING & URBAN DEVELOPMENT CORPORATION

설계명 PROJECT TITLE

화성동탄(2)A76-2BL
민간참여 공동주택사업

주기 NOTE

1. 디퓨저 위치, 수량, 제어반 위치 및 장비사양은 현장여건에 따라 변경 될 수 있음.
2. 환기 콘트롤러 및 욕실팬 스위치는 현장여건에 따라 변경될 수 있음.
3. 환기용 급,배기 덕트의 디퓨저 연결 부분은 흡음비보온 후렉시블덕트 (길이 1m)를 설치하고, 이후 난연이중 크린호스를 설치
4. 디퓨저 연결구에는 미세먼지 필터를 설치
5. 덕트 루트는 현장여건에 따라 변경될 수 있음.
6. 에시와 같은 역풍방지캡은 직배기의 환기캡에 사용하며, 전열교환기의 환기캡은 상단의 도피로가 없는 타입으로 시공한다.
7. 주방후드 직배기는 스파이럴덕트를 통하여 외부로 배출하며, 외부 노출 및 외벽으로부터 1m까지는 10t 보온한다.
8. 욕실 직배기는 욕실에 고정압환을 설치하고 덕트를 통하여 외부로 배출한다. 변경 될 수 있음.
9. 욕실배출덕트 중 욕실 내부에는 흡음 비보온 후렉시블덕트를 설치하고, 거실 등에 설치되는 배기덕트는 난연이중크린호스를 설치하며, 외벽에서 약 1m까지는 PVC 삼중보온덕트를 설치한다.
10. 2이상의 통합 배기를 하는 경우 연결되는 각 실의 배기팬은 MD 부착형을 적용한다.

NO	DATE	REVISION DESCRIPTION	APPD

설 계
DESIGN

대표전화

축 척	SCALE
A1	1 / 50
A3	1 / 100


일 자 DATE
2025. 12.

설계번호 PROJECT NO.
AR - 23 - 026

도면화일명 DWG. FILE NAME

도면번호 SHEET NO.
MD – 006

도면명 SUBJECT TITLE
84m²C형 단위세대
환기덕트 평면도(확장형)

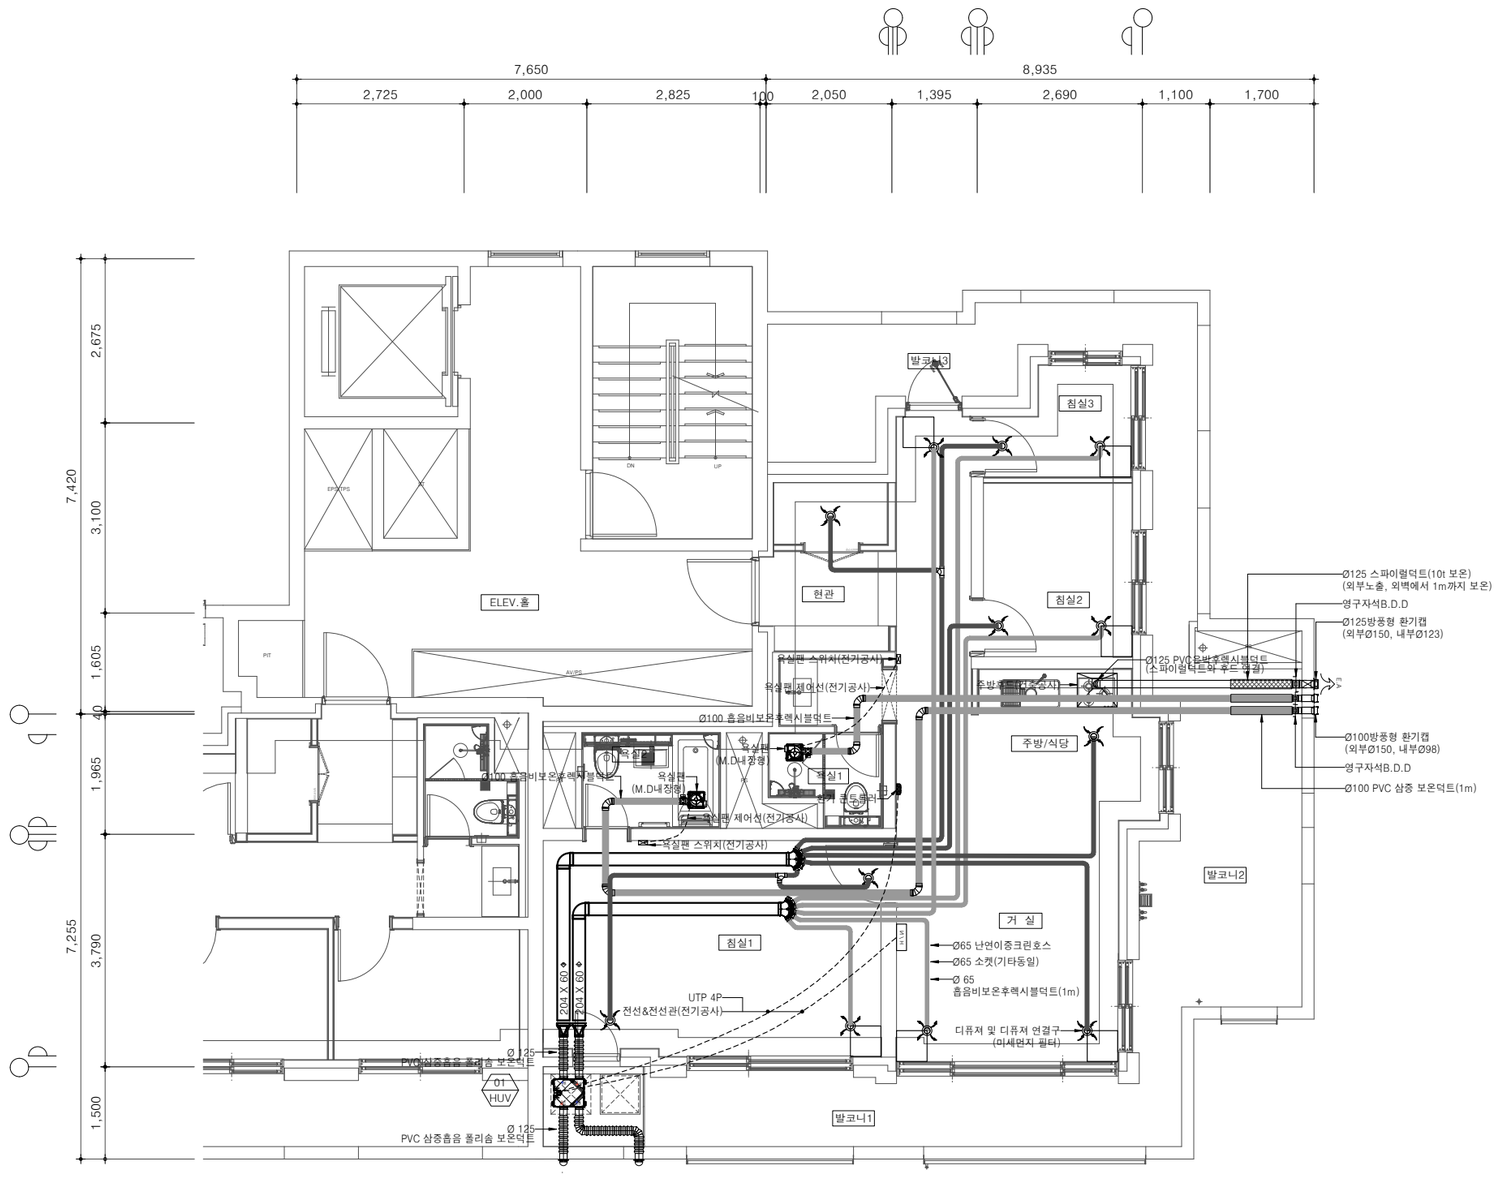

84m²D형 단위세대 환기덕트 평면도(기본형)

축 척 : 1/100

경기주택도시공사
GYEONGGI HOUSING & URBAN DEVELOPMENT CORPORATION

설계명 PROJECT TITLE

화성동탄(2)A76-2BL
민간참여 공동주택사업


주기 NOTE

1. 디퓨저 위치, 수량, 제어반 위치 및 장비사양은 현장여건에 따라 변경 될 수 있음.
2. 환기 콘트롤러 및 욕실팬 스위치는 현장여건에 따라 변경될 수 있음.
3. 환기용 급,배기 덕트의 디퓨저 연결 부분은 흡음비보온 후렉시블덕트 (길이 1m)를 설치하고, 이후 난연이중 크린호스를 설치
4. 디퓨저 연결구에는 미세먼지 필터를 설치
5. 덕트 루트는 현장여건에 따라 변경될 수 있음.
6. 예시와 같은 역풍방지캡은 직배기의 환기캡에 사용하며, 전열교환기의 환기캡은 상단의 도피로가 없는 타입으로 시공한다.
7. 주방후드 직배기는 스파이럴덕트를 통하여 외부로 배출하며, 외부 노출 및 외벽으로부터 1m까지는 10t 보온한다.
8. 욕실 직배기는 욕실에 고정압환을 설치하고 덕트를 통하여 외부로 배출한다. 변경 될 수 있음.
9. 욕실배출덕트 중 욕실 내부에는 흡음 비보온 후렉시블덕트를 설치하고, 거실 등에 설치되는 배기닥트는 난연이중크린호스를 설치하며, 외벽에서 약 1m까지는 PVC 삼중보온덕트를 설치한다.
10. 2이상의 통합 배기를 하는 경우 연결되는 각 실의 배기팬은 MD 부착형을 적용한다.

NO	DATE	REVISION DESCRIPTION	APPD
△			
△			
△			
△			

설 계
DESIGN

대표전화	
축 척	SCALE
A1	1 / 50
A3	1 / 100
일 자	DATE
	2025. 12.
설계번호	PROJECT NO.
	AR - 23 - 026
도면화일명	DWG. FILE NAME
도면번호	SHEET NO.
	MD – 007
도면명	SUBJECT TITLE
	84m²D형 단위세대 환기덕트 평면도(기본형)

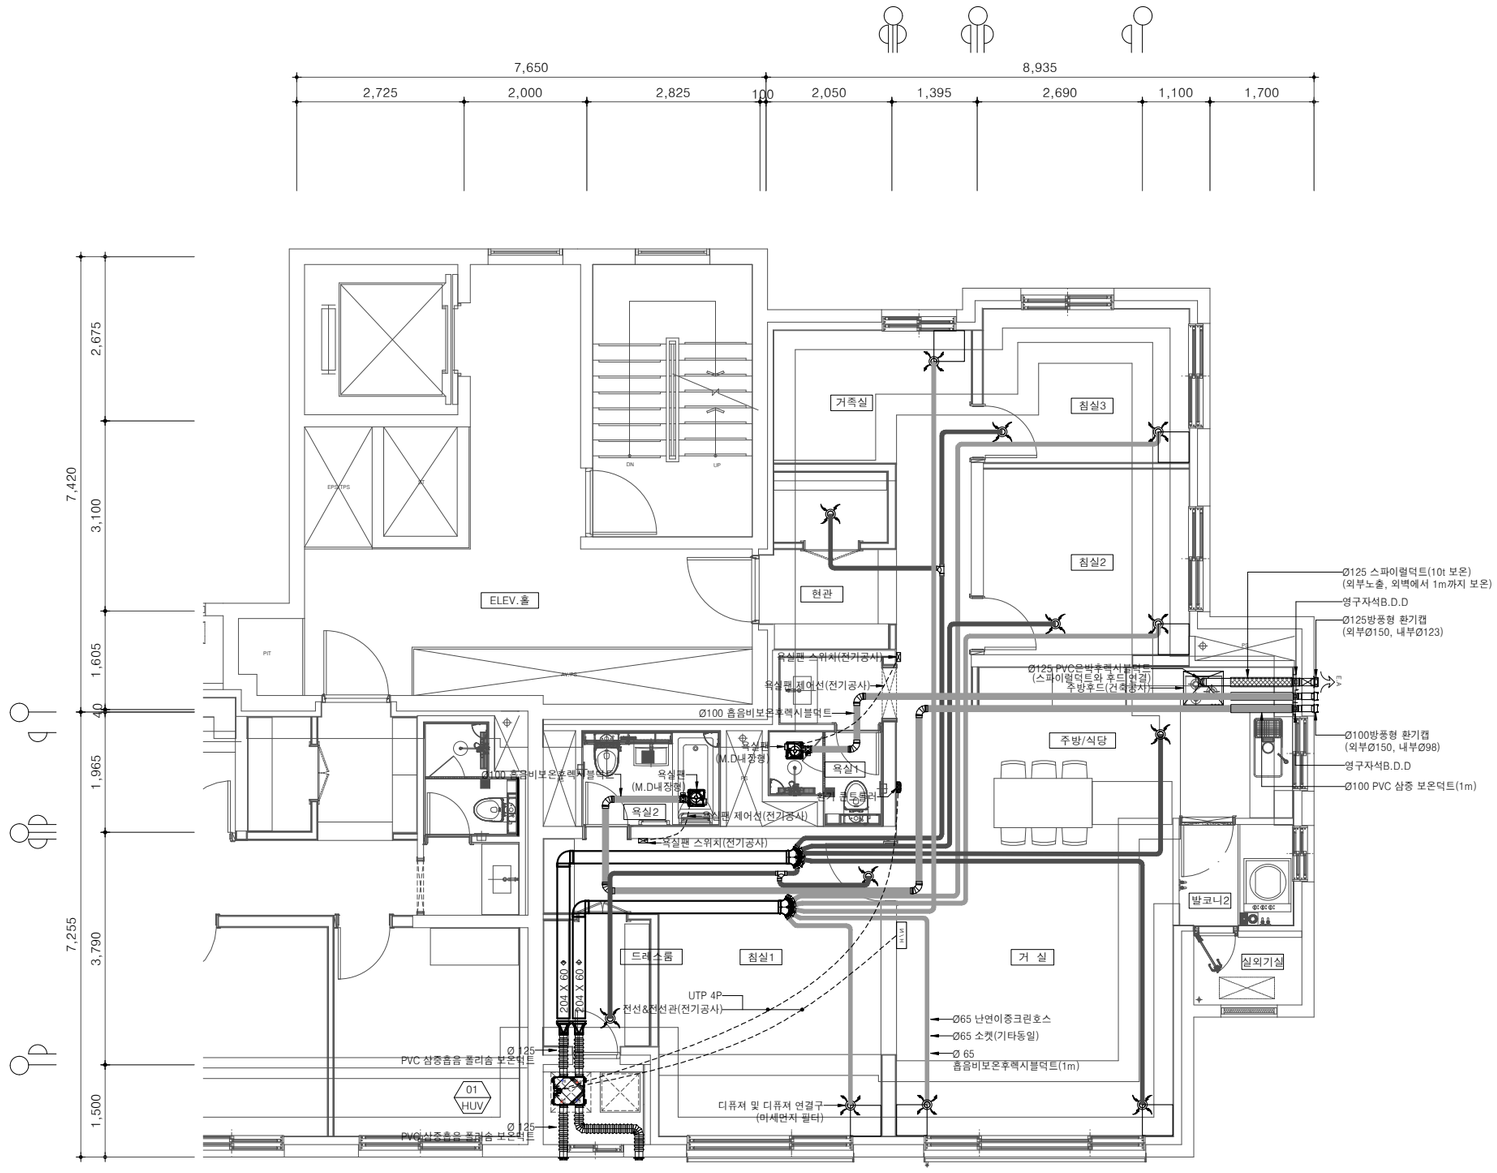

84m²D형 단위세대 환기덕트 평면도(확장형)

축 척 : 1/100

경기주택도시공사
GYEONGGI HOUSING & URBAN DEVELOPMENT CORPORATION

설계명 PROJECT TITLE

화성동탄(2)A76-2BL
민간참여 공동주택사업

주기 NOTE


1. 디퓨저 위치, 수량, 제어반 위치 및 장비사양은 현장여건에 따라 변경 될 수 있음.
2. 환기 콘트롤러 및 욕실팬 스위치는 현장여건에 따라 변경될 수 있음.
3. 환기용 급,배기 덕트의 디퓨저 연결 부분은 흡음비보온 후렉시블덕트 (길이 1m)를 설치하고, 이후 난연이중 크린호스를 설치
4. 디퓨저 연결구에는 미세먼지 필터를 설치
5. 덕트 루트는 현장여건에 따라 변경될 수 있음.
6. 예시와 같은 역풍방지캡은 직배기의 환기캡에 사용하며, 전열교환기의 환기캡은 상단의 도피로가 없는 타입으로 시공한다.
7. 주방후드 직배기는 스파이럴덕트를 통하여 외부로 배출하며, 외부 노출 및 외벽으로부터 1m까지는 10t 보온한다.
8. 욕실 직배기는 욕실에 고정압환을 설치하고 덕트를 통하여 외부로 배출한다. 변경 될 수 있음.
9. 욕실배출덕트 중 욕실 내부에는 흡음 비보온 후렉시블덕트를 설치하고, 거실 등에 설치되는 배기닥트는 난연이중크린호스를 설치하며, 외벽에서 약 1m까지는 PVC 삼중보온덕트를 설치한다.
10. 2이상의 통합 배기를 하는 경우 연결되는 각 실의 배기팬은 MD 부착형을 적용한다.

NO	DATE	REVISION DESCRIPTION	APPD
△			
△			
△			
△			

설 계
DESIGN

대표전화

축 척	SCALE
A1	1 / 50
A3	1 / 100
일 자 DATE	2025. 12.
설계번호 PROJECT NO.	AR - 23 - 026
도면화일명 DWG. FILE NAME	
도면번호 SHEET NO.	MD – 008
도면명 SUBJECT TITLE	84m²D형 단위세대 환기덕트 평면도(확장형)

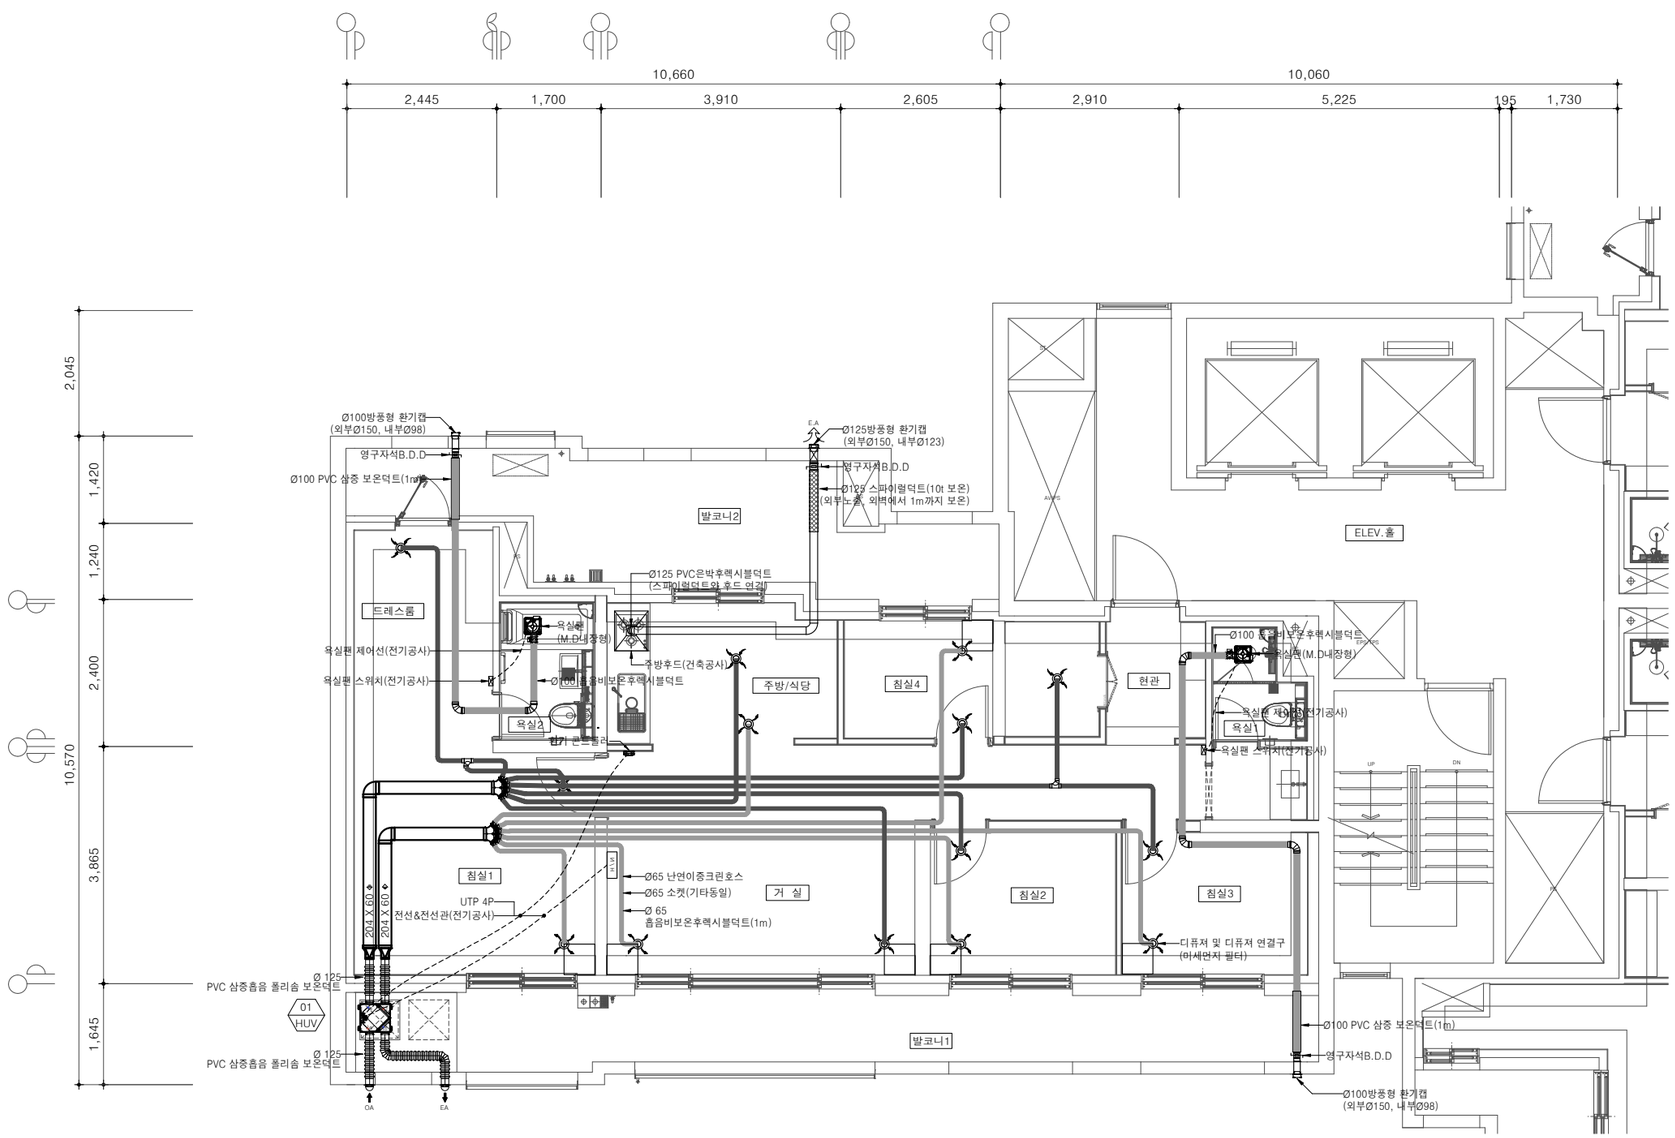

97m²A형 단위세대 환기덕트 평면도(기본형)

축 척 : 1/100

경기주택도시공사
GYEONGGI HOUSING & URBAN DEVELOPMENT CORPORATION

설계명 PROJECT TITLE

화성동탄(2)A76-2BL
민간참여 공동주택사업

주기 NOTE

1. 디퓨저 위치, 수량, 제어반 위치 및 장비사양은 현장여건에 따라 변경 될 수 있음.
2. 환기 콘트롤러 및 욕실팬 스위치는 현장여건에 따라 변경될 수 있음.
3. 환기용 급,배기 덕트의 디퓨저 연결 부분은 흡음비보온 후렉시블덕트 (길이 1m)를 설치하고, 이후 난연이중 크린호스를 설치
4. 디퓨저 연결구에는 이새먼지 필터를 설치
5. 덕트 루트는 현장여건에 따라 변경될 수 있음.
6. 예시와 같은 역풍방지캡은 직배기의 환기캡에 사용하며, 전열교환기의 환기캡은 상단의 도피로가 없는 타입으로 시공한다.
7. 주방후드 직배기는 스파이럴덕트를 통하여 외부로 배출하며, 외부 노출 및 외벽으로부터 1m까지는 10t 보온한다.
8. 욕실 직배기는 욕실에 고정압환을 설치하고 덕트를 통하여 외부로 배출한다. 변경 될 수 있음.
9. 욕실배출덕트 중 욕실 내부에는 흡음 비보온 후렉시블덕트를 설치하고, 거실 등에 설치되는 배기덕트는 난연이중크린호스를 설치하며, 외벽에서 약 1m까지는 PVC 삼중보온덕트를 설치한다.
10. 2이상의 동합 배기를 하는 경우 연결되는 각 실의 배기팬은 MD 부착형을 적용한다.

NO	DATE	REVISION DESCRIPTION	APPD

설 계
DESIGN

대표전화

축 척	SCALE
A1	1 / 50
A3	1 / 100


일 자 DATE
2025. 12.

설계번호 PROJECT NO.
AR - 23 - 026

도면화일명 DWG. FILE NAME

도면번호 SHEET NO.
MD - 009

도면명 SUBJECT TITLE
97m²A형 단위세대
환기덕트 평면도(기본형)

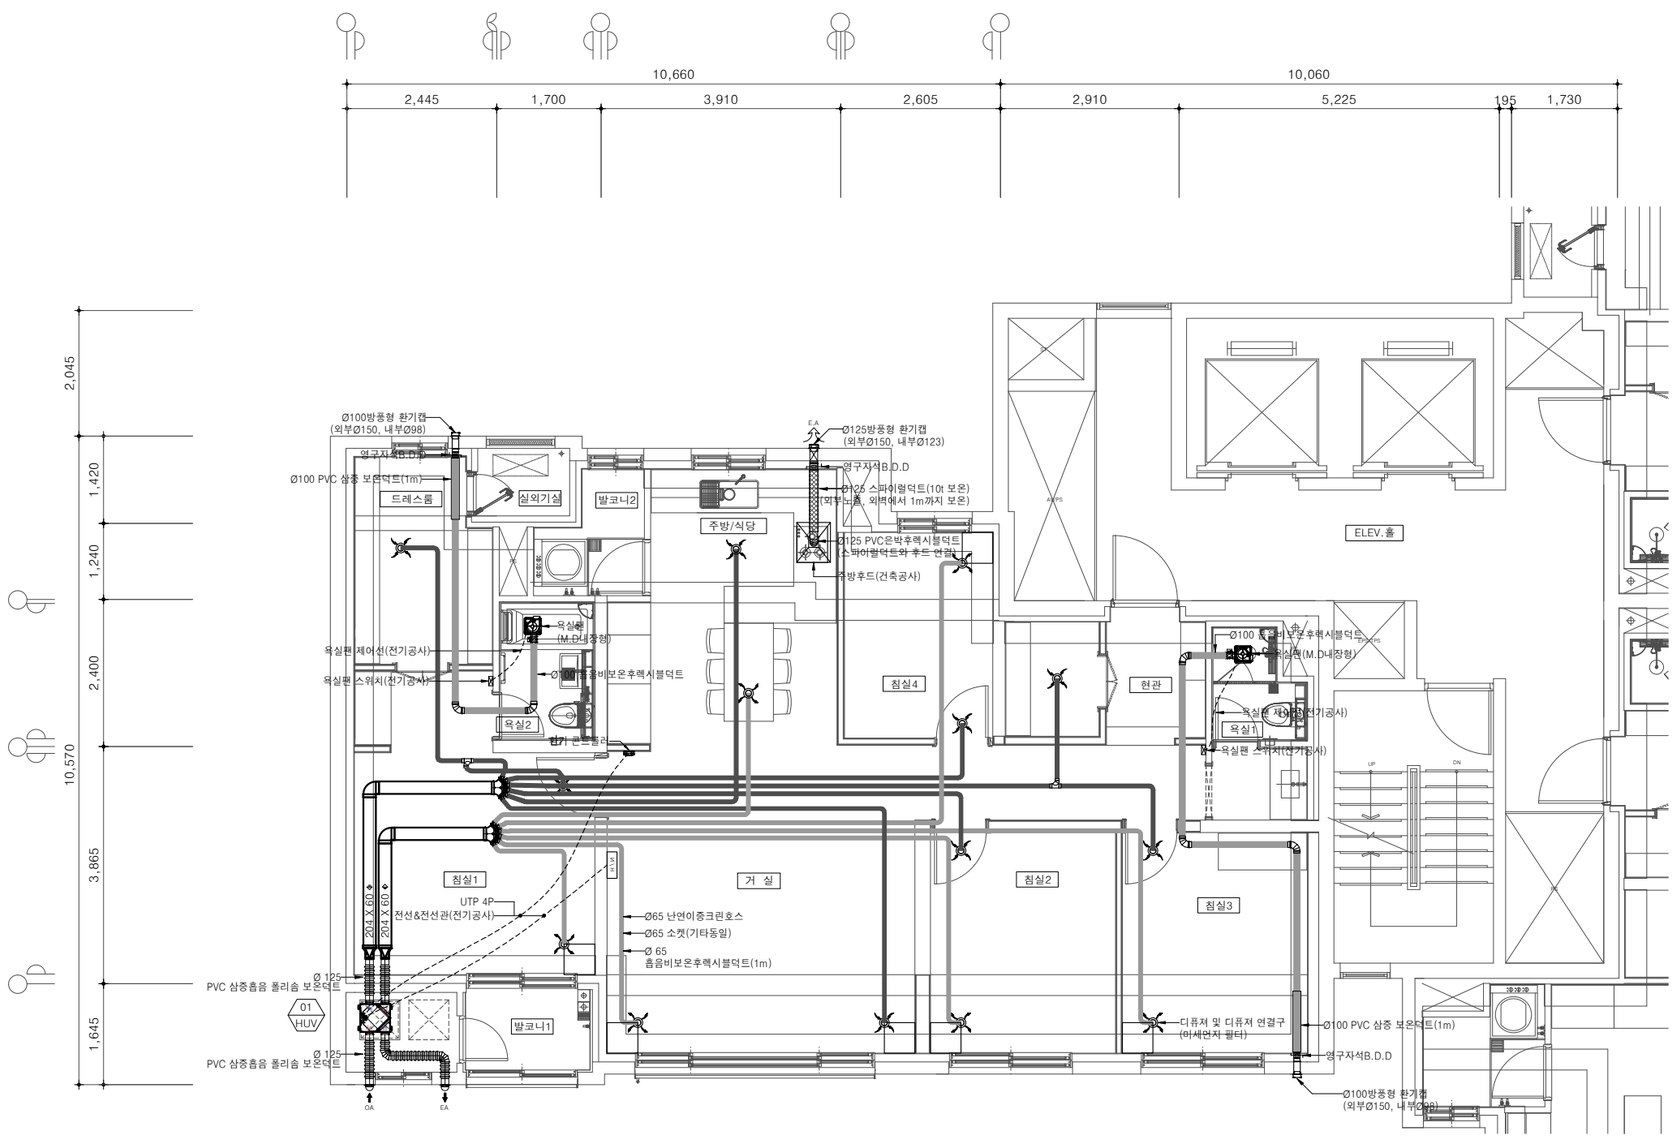

97m²A형 단위세대 환기덕트 평면도(확장형)

축 척 : 1/100

경기주택도시공사
GYEONGGI HOUSING & URBAN DEVELOPMENT CORPORATION

설계명 PROJECT TITLE

화성동탄(2)A76-2BL
민간참여 공동주택사업

주기 NOTE

1. 디퓨저 위치, 수량, 제어반 위치 및 장비사양은 현장여건에 따라 변경 될 수 있음.
2. 환기 콘트롤러 및 욕실팬 스위치는 현장여건에 따라 변경될 수 있음.
3. 환기용 급,배기 덕트의 디퓨저 연결 부분은 흡음비보온 후렉시블덕트 (길이 1m)를 설치하고, 이후 난연이중 크린호스를 설치
4. 디퓨저 연결구에는 미세먼지 필터를 설치
5. 덕트 루트는 현장여건에 따라 변경될 수 있음.
6. 예시와 같은 역풍방지캡은 직배기의 환기캡에 사용하며, 전열교환기의 환기캡은 상단의 도피로가 없는 타입으로 시공한다.
7. 주방후드 직배기는 스파이럴덕트를 통하여 외부로 배출하며, 외부 노출 및 외벽으로부터 1m까지는 10t 보온한다.
8. 욕실 직배기는 욕실에 고정압환을 설치하고 덕트를 통하여 외부로 배출한다. 변경 될 수 있음.
9. 욕실배출덕트 중 욕실 내부에는 흡음 비보온 후렉시블덕트를 설치하고, 거실 등에 설치되는 배기닥트는 난연이중크린호스를 설치하며, 외벽에서 약 1m까지는 PVC 삼중보온덕트를 설치한다.
10. 2이상의 동합 배기를 하는 경우 연결되는 각 실의 배기팬은 MD 부착형을 적용한다.

NO	DATE	REVISION DESCRIPTION	APPD
△			
△			
△			
△			

설 계
DESIGN

대표전화

축 척	SCALE
A1	1 / 50
A3	1 / 100


일 자 DATE
2025. 12.

설계번호 PROJECT NO.
AR - 23 - 026

도면화일명 DWG. FILE NAME

도면번호 SHEET NO.
MD - 010

도면명 SUBJECT TITLE
97m²A형 단위세대
환기덕트 평면도(확장형)

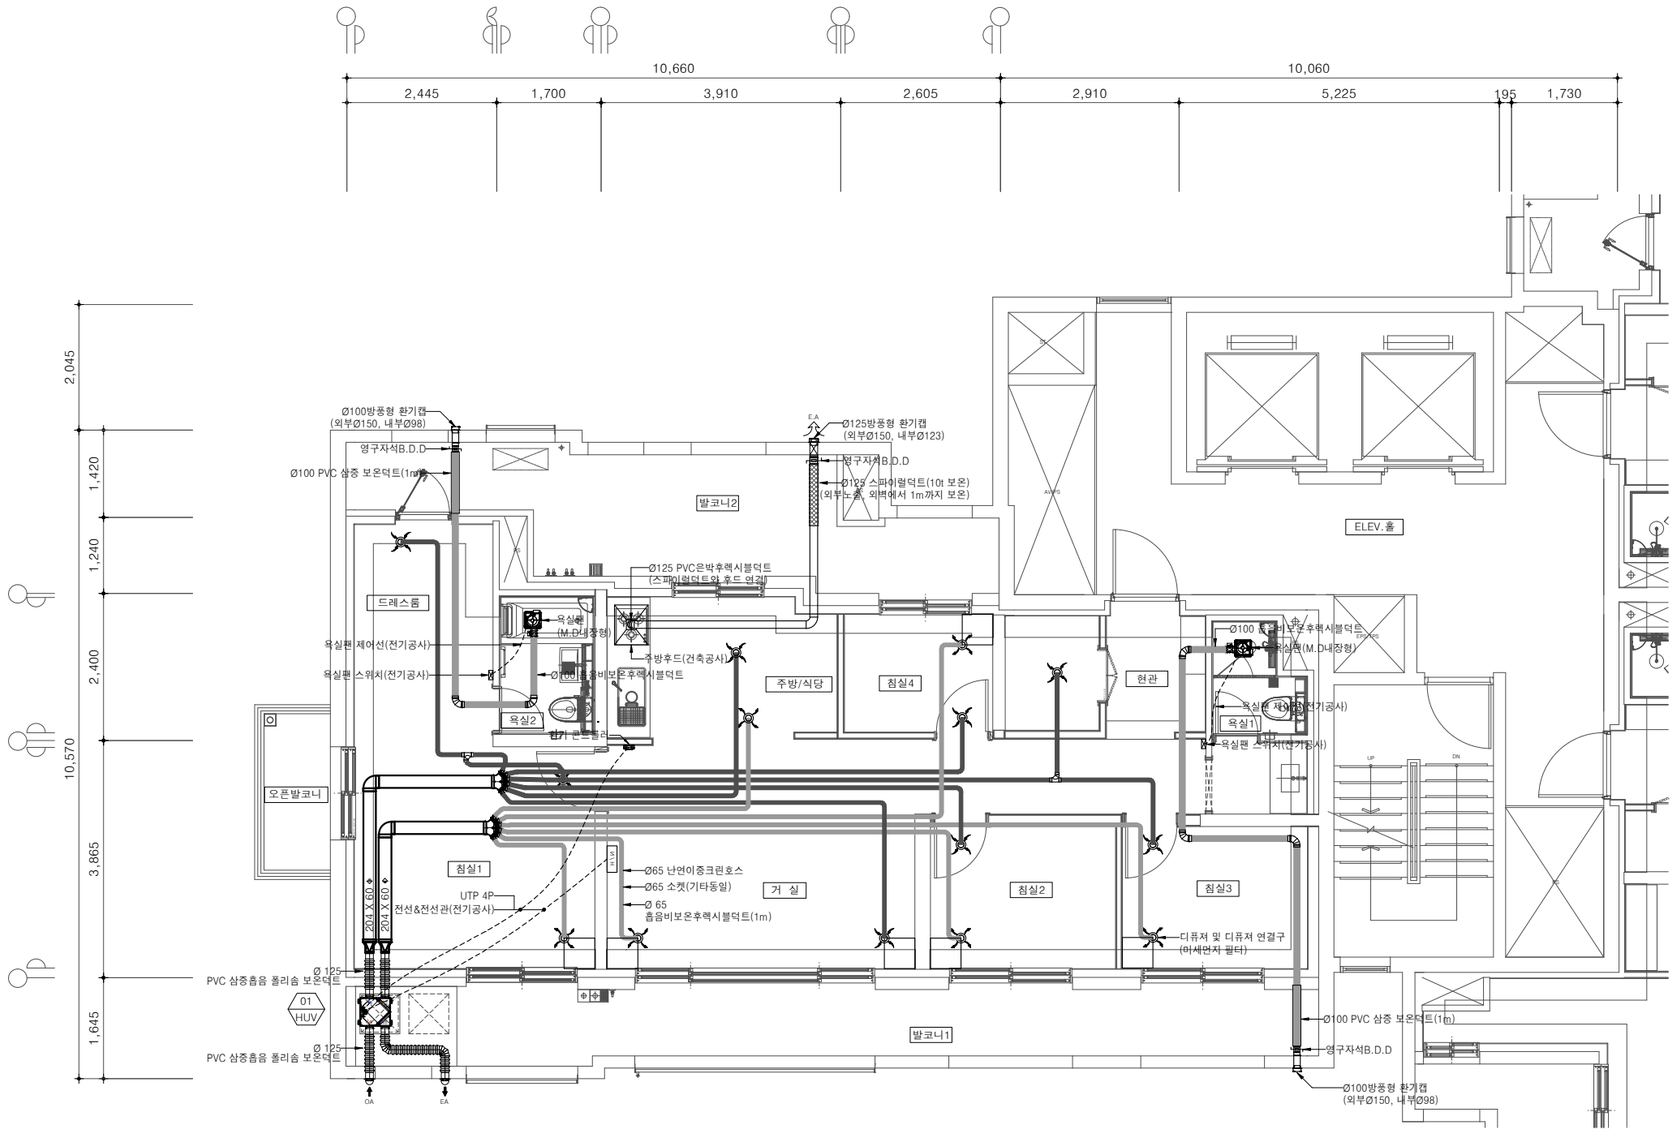

97m²B형 단위세대 환기덕트 평면도(기본형)

축 척 : 1/100

경기주택도시공사
GYEONGGI HOUSING & URBAN DEVELOPMENT CORPORATION

설계명 PROJECT TITLE

화성동탄(2)A76-2BL
민간참여 공동주택사업

주기 NOTE

1. 디퓨저 위치, 수량, 제어반 위치 및 장비사양은 현장여건에 따라 변경 될 수 있음.
2. 환기 콘트롤러 및 욕실팬 스위치는 현장여건에 따라 변경될 수 있음.
3. 환기용 급,배기 덕트의 디퓨저 연결 부분은 흡음비보온 후렉시블덕트 (길이 1m)를 설치하고, 이후 난연이중 크린호스를 설치
4. 디퓨저 연결구에는 이새먼지 필터를 설치
5. 덕트 루트는 현장여건에 따라 변경될 수 있음.
6. 에시와 같은 역풍방지캡은 직배기의 환기캡에 사용하며, 전열교환기의 환기캡은 상단의 도피로가 없는 타입으로 시공한다.
7. 주방후드 직배기는 스파이럴덕트를 통하여 외부로 배출하며, 외부 노출 및 외벽으로부터 1m까지는 10t 보온한다.
8. 욕실 직배기는 욕실에 고정압환을 설치하고 덕트를 통하여 외부로 배출한다. 변경 될 수 있음.
9. 욕실배출덕트 중 욕실 내부에는 흡음 비보온 후렉시블덕트를 설치하고, 거실 등에 설치되는 배기덕트는 난연이중크린호스를 설치하며, 외벽에서 약 1m까지는 PVC 삼중보온덕트를 설치한다.
10. 2이상의 동합 배기를 하는 경우 연결되는 각 실의 배기팬은 MD 부착형을 적용한다.

NO	DATE	REVISION DESCRIPTION	APPD

설 계
DESIGN

대표전화

축 척	SCALE
A1	1 / 50
A3	1 / 100


일 자 DATE
2025. 12.

설계번호 PROJECT NO.
AR - 23 - 026

도면화일명 DWG. FILE NAME

도면번호 SHEET NO.
MD - 011

도면명 SUBJECT TITLE
97m²B형 단위세대
환기덕트 평면도(기본형)

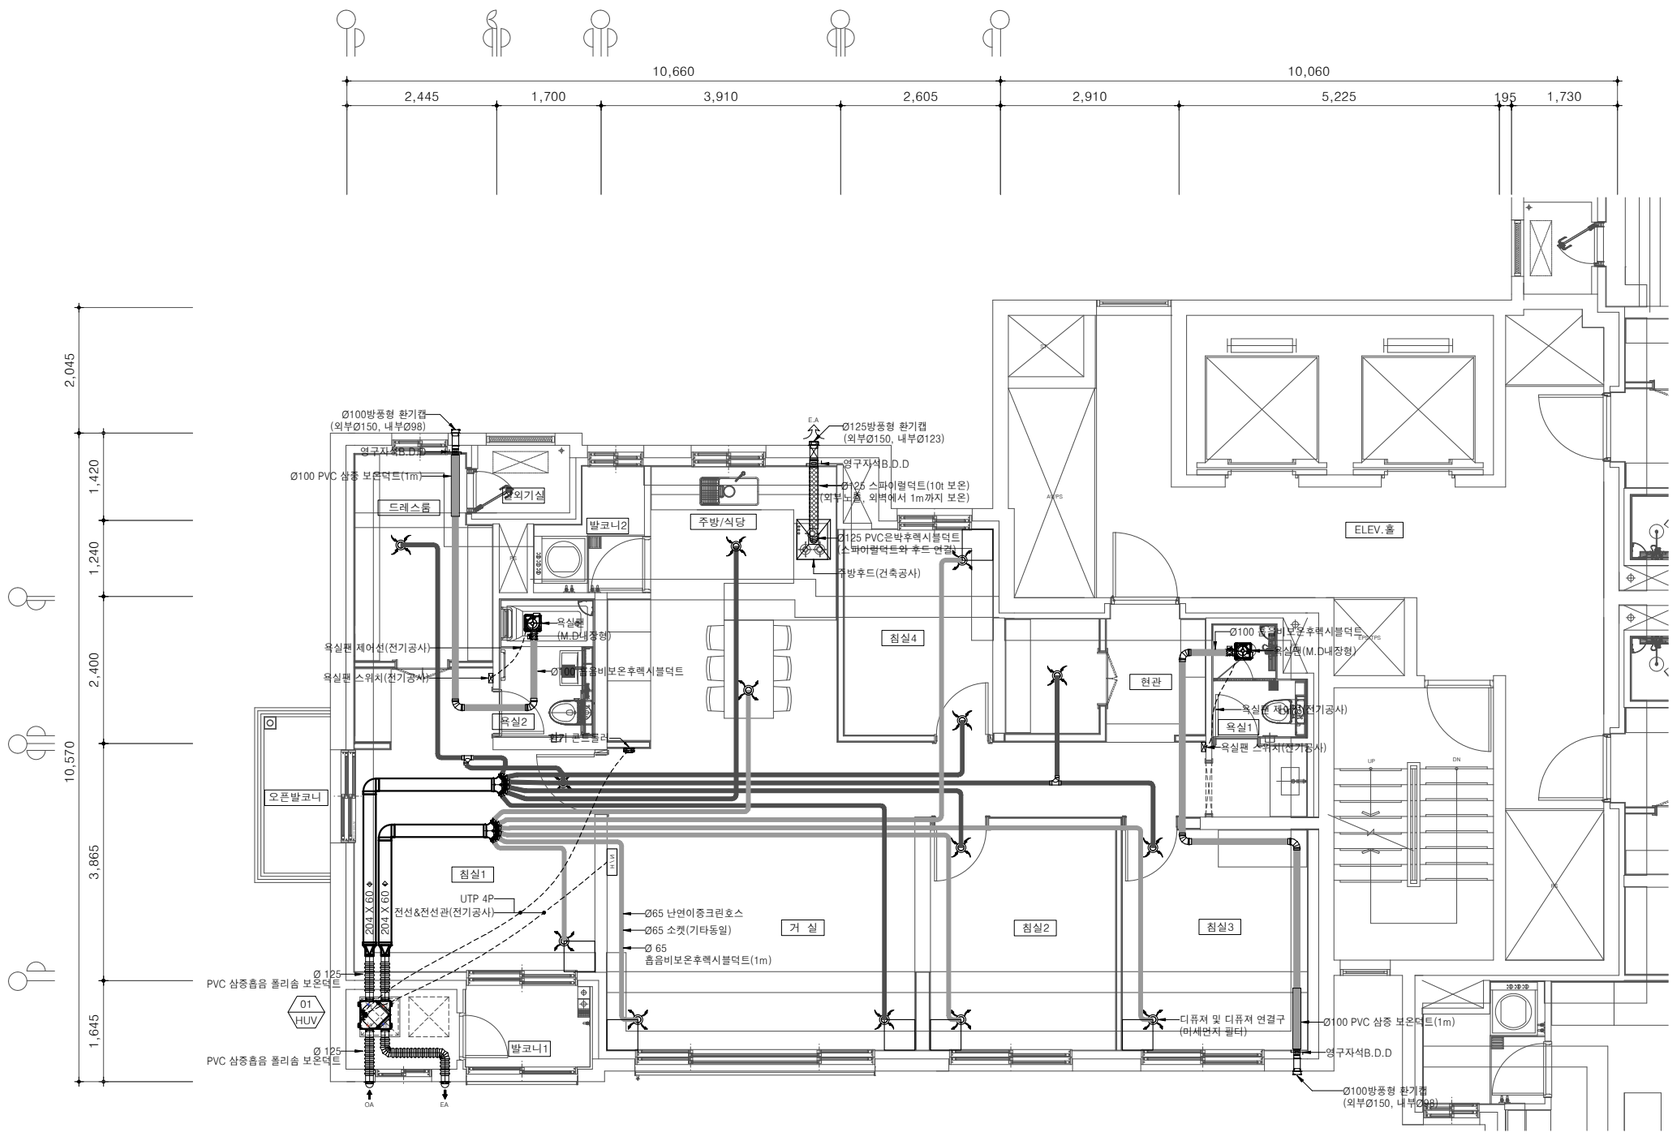

97m²B형 단위세대 환기덕트 평면도(확장형)

축 척 : 1/100

경기주택도시공사

설계명 PROJECT TITLE

화성동탄(2)A76-2BL
민간참여 공동주택사업

주기 NOTE


1. 디퓨저 위치, 수량, 제어반 위치 및 장비사양은 현장여건에 따라 변경 될 수 있음.
2. 환기 콘트롤러 및 욕실팬 스위치는 현장여건에 따라 변경될 수 있음.
3. 환기옹 급,배기 덕트의 디퓨저 연결 부분은 흡음비보온 후렉시블덕트 (길이 1m)를 설치하고, 이후 난연이중 크린호스를 설치
4. 디퓨저 연결구에는 미세먼지 필터를 설치
5. 덕트 루트는 현장여건에 따라 변경될 수 있음.
6. 에시와 같은 역풍방지캡은 직배기의 환기캡에 사용하며, 전열교환기의 환기캡은 상단의 도피로가 없는 타입으로 시공한다.
7. 주방후드 직배기는 스파이럴덕트를 통하여 외부로 배출하며, 외부 노출 및 외벽으로부터 1m까지는 10t 보온한다.
8. 욕실 직배기는 욕실에 고정압환을 설치하고 덕트를 통하여 외부로 배출한다. 변경 될 수 있음.
9. 욕실배출덕트 중 욕실 내부에는 흡음 비보온 후렉시블덕트를 설치하고, 거실 등에 설치되는 배기덕트는 난연이중크린호스를 설치하며, 외벽에서 약 1m까지는 PVC 삼중보온덕트를 설치한다.
10. 2이상의 통합 배기를 하는 경우 연결되는 각 실의 배기팬은 MD 부착형을 적용한다.

NO	DATE	REVISION DESCRIPTION	APPD
△			
△			
△			
△			

설 계
DESIGN

대표전화

축 척	SCALE
A1	1 / 50
A3	1 / 100
일 자 DATE	2025. 12.
설계번호 PROJECT NO.	AR - 23 - 026
도면화일명 DWG. FILE NAME	
도면번호 SHEET NO.	MD - 012
도면명 SUBJECT TITLE	97m²B형 단위세대 환기덕트 평면도(확장형)

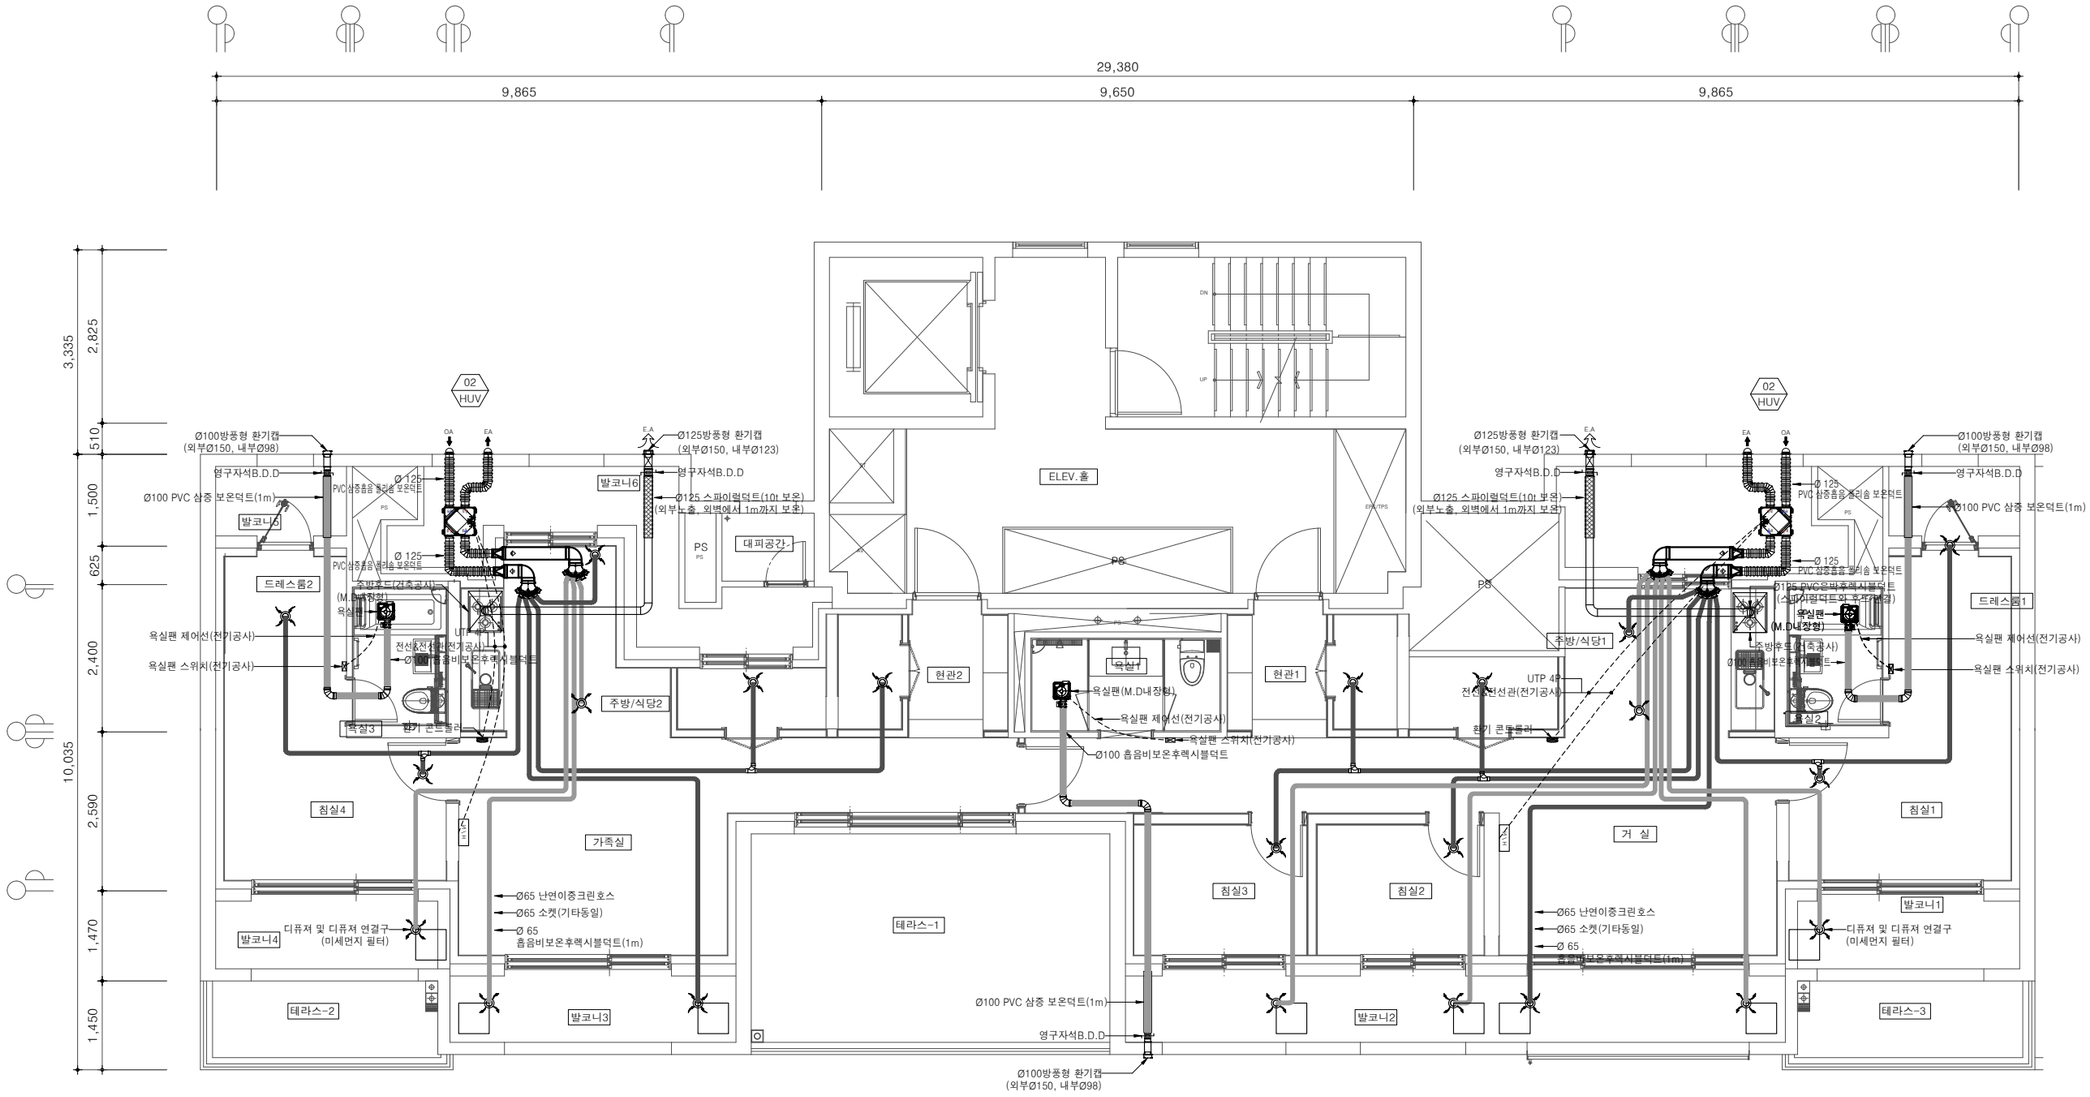

M 142m²P형 단위세대 환기덕트 평면도(기본형)

축 척 : 1/100

경기주택도시공사
GYEONGGI HOUSING & URBAN DEVELOPMENT CORPORATION

설계명 PROJECT TITLE

화성동탄(2)A76-2BL
민간참여 공동주택사업

주기 NOTE


1. 디퓨저 위치, 수량, 제어반 위치 및 장비사양은 현장여건에 따라 변경 될 수 있음.
2. 환기 콘트롤러 및 욕실팬 스위치는 현장여건에 따라 변경될 수 있음.
3. 환기용 급,배기 덕트의 디퓨저 연결 부분은 흡음비보온 후렉시블덕트 (길이 1m)를 설치하고, 이후 난연이중 크린호스를 설치
4. 디퓨저 연결구에는 미세먼지 필터를 설치
5. 덕트 루트는 현장여건에 따라 변경될 수 있음.
6. 예시와 같은 역풍방지캡은 직배기의 환기캡에 사용하며, 전열교환기의 환기캡은 상단의 도피로가 없는 타입으로 시공한다.
7. 주방후드 직배기는 스파이럴덕트를 통하여 외부로 배출하며, 외부 노출 및 외벽으로부터 1m까지는 10t 보온한다.
8. 욕실 직배기는 욕실에 고정압팬을 설치하고 덕트를 통하여 외부로 배출한다. 변경 될 수 있음.
9. 욕실배출덕트 중 욕실 내부에는 흡음 비보온 후렉시블덕트를 설치하고, 거실 등에 설치되는 배기덕트는 난연이중크린호스를 설치하며, 외벽에서 약 1m까지는 PVC 삼중보온덕트를 설치한다.
10. 20상의 통합 배기를 하는 경우 연결되는 각 실의 배기팬은 MD 부착형을 적용한다.

NO	DATE	REVISION DESCRIPTION	APPD

설 계
DESIGN

대표전화

축 척	SCALE
A1	1 / 50
A3	1 / 100
일 자	DATE
	2025. 12.
설계번호	PROJECT NO.
	AR - 23 - 026
도면화일명	DWG. FILE NAME
도면번호	SHEET NO.
	MD - 013
도면명	SUBJECT TITLE
	142m²P형 단위세대 환기덕트 평면도(기본형)

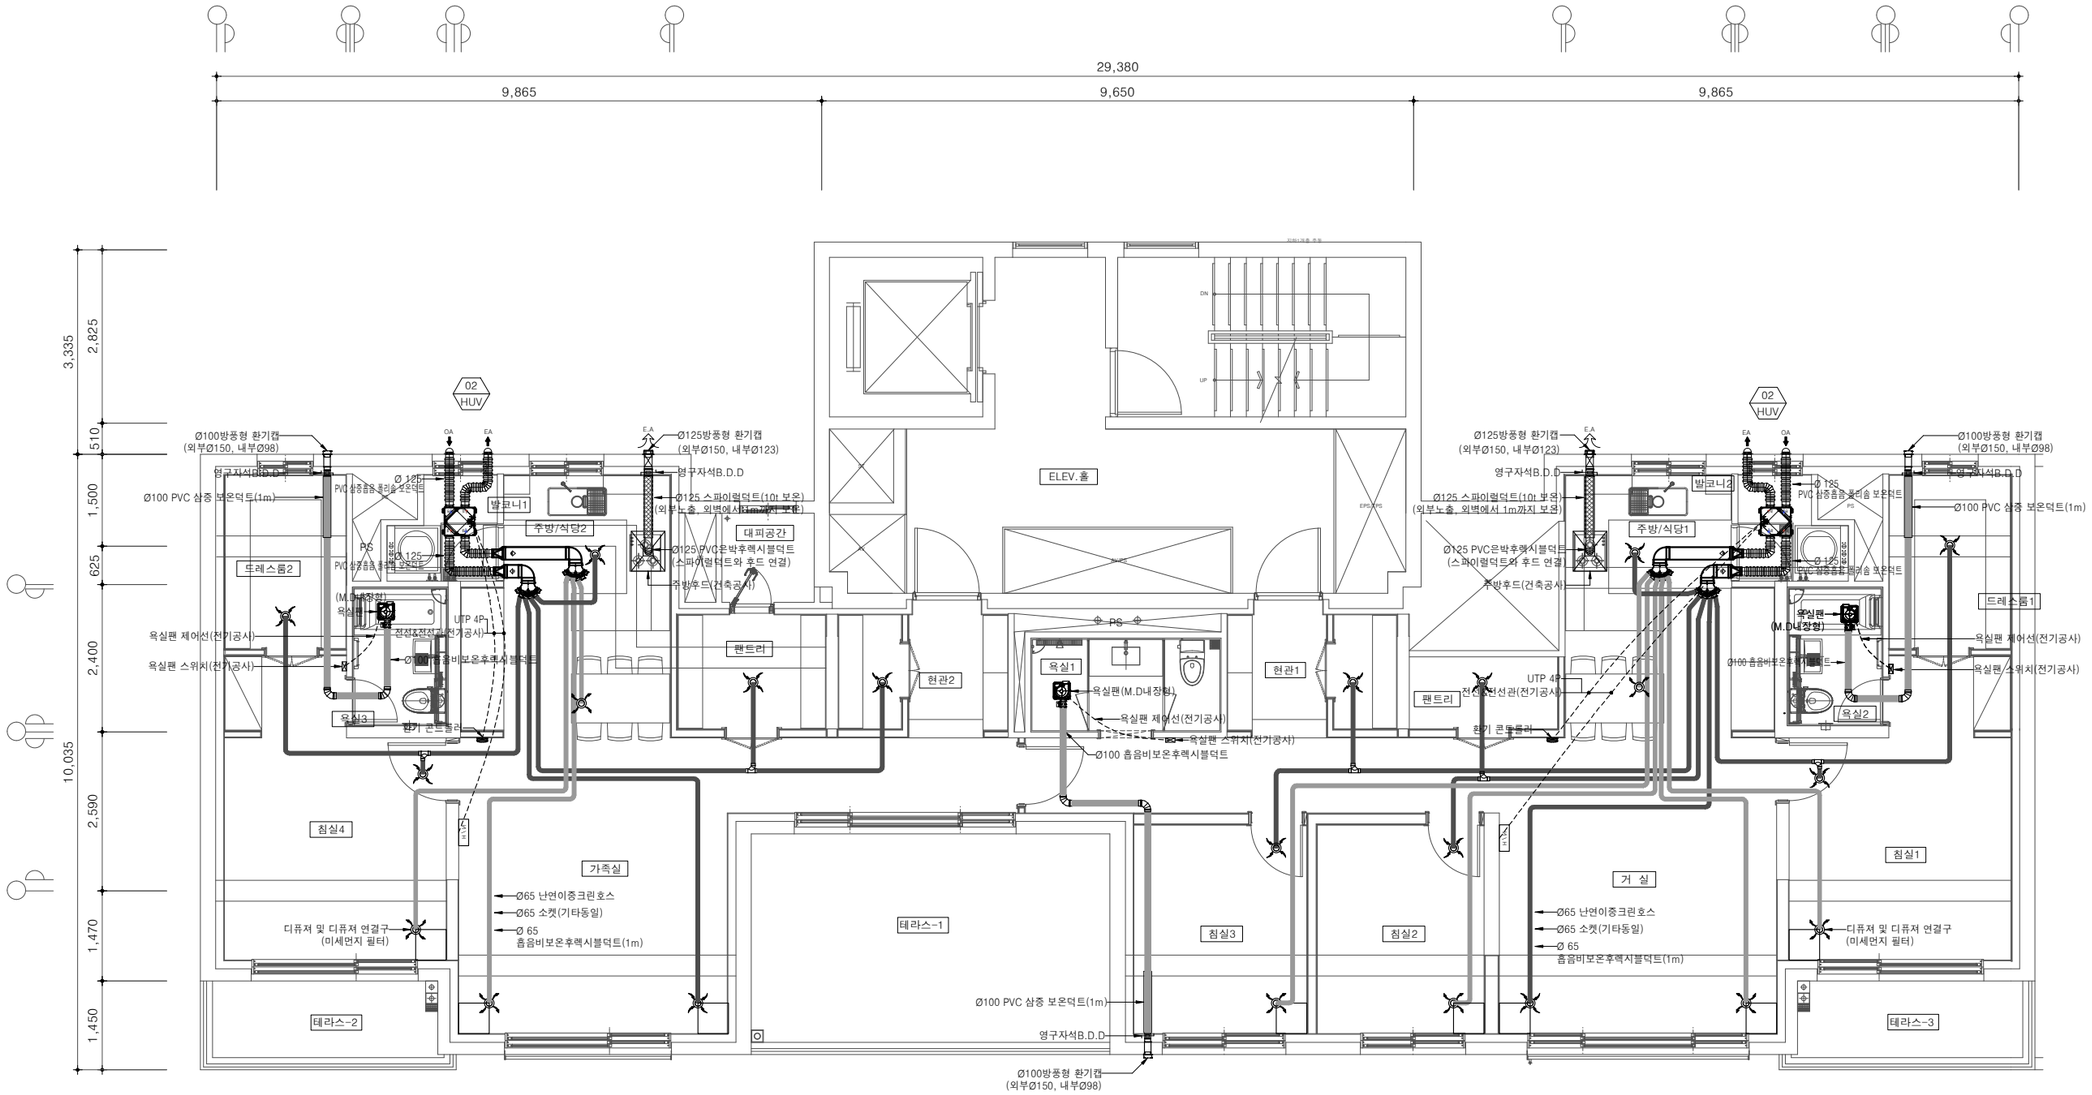

142m²P형 단위세대 환기덕트 평면도(확장형)

축 척 : 1/100

경기주택도시공사
GYEONGGI HOUSING & URBAN DEVELOPMENT CORPORATION

설계명 PROJECT TITLE

화성동탄(2)A76-2BL
민간참여 공동주택사업

주기 NOTE

1. 디퓨저 위치, 수량, 제어반 위치 및 장비사양은 현장여건에 따라 변경 될 수 있음.
2. 환기 콘트롤러 및 욕실팬 스위치는 현장여건에 따라 변경될 수 있음.
3. 환기용 급,배기 덕트의 디퓨저 연결 부분은 흡음비보온 후렉시블덕트 (길이 1m)를 설치하고, 이후 난연이중 크린호스를 설치
4. 디퓨저 연결구에는 미세먼지 필터를 설치
5. 덕트 루트는 현장여건에 따라 변경될 수 있음.
6. 예시와 같은 역풍방지캡은 직배기의 환기캡에 사용하며, 전열교환기의 환기캡은 상단의 도피로가 없는 타입으로 시공한다.
7. 주방후드 직배기는 스파이럴덕트를 통하여 외부로 배출하며, 외부 노출 및 외벽으로부터 1m까지는 10t 보온한다.
8. 욕실 직배기는 욕실에 고정압환을 설치하고 덕트를 통하여 외부로 배출한다. 변경 될 수 있음.
9. 욕실배출덕트 중 욕실 내부에는 흡음 비보온 후렉시블덕트를 설치하고, 거실 등에 설치되는 배기덕트는 난연이중크린호스를 설치하며, 외벽에서 약 1m까지는 PVC 삼중보온덕트를 설치한다.
10. 2이상의 통합 배기를 하는 경우 연결되는 각 실의 배기팬은 MD 부착형을 적용한다.

NO	DATE	REVISION DESCRIPTION	APPD

설 계
DESIGN

대표전화

축 척	SCALE
A1	1 / 50
A3	1 / 100


일 자 DATE 2025. 12.

설계번호 PROJECT NO. AR - 23 - 026

도면화일명 DWG. FILE NAME

도면번호 SHEET NO. MD - 014

도면명 SUBJECT TITLE
142m²P형 단위세대
환기덕트 평면도(확장형)

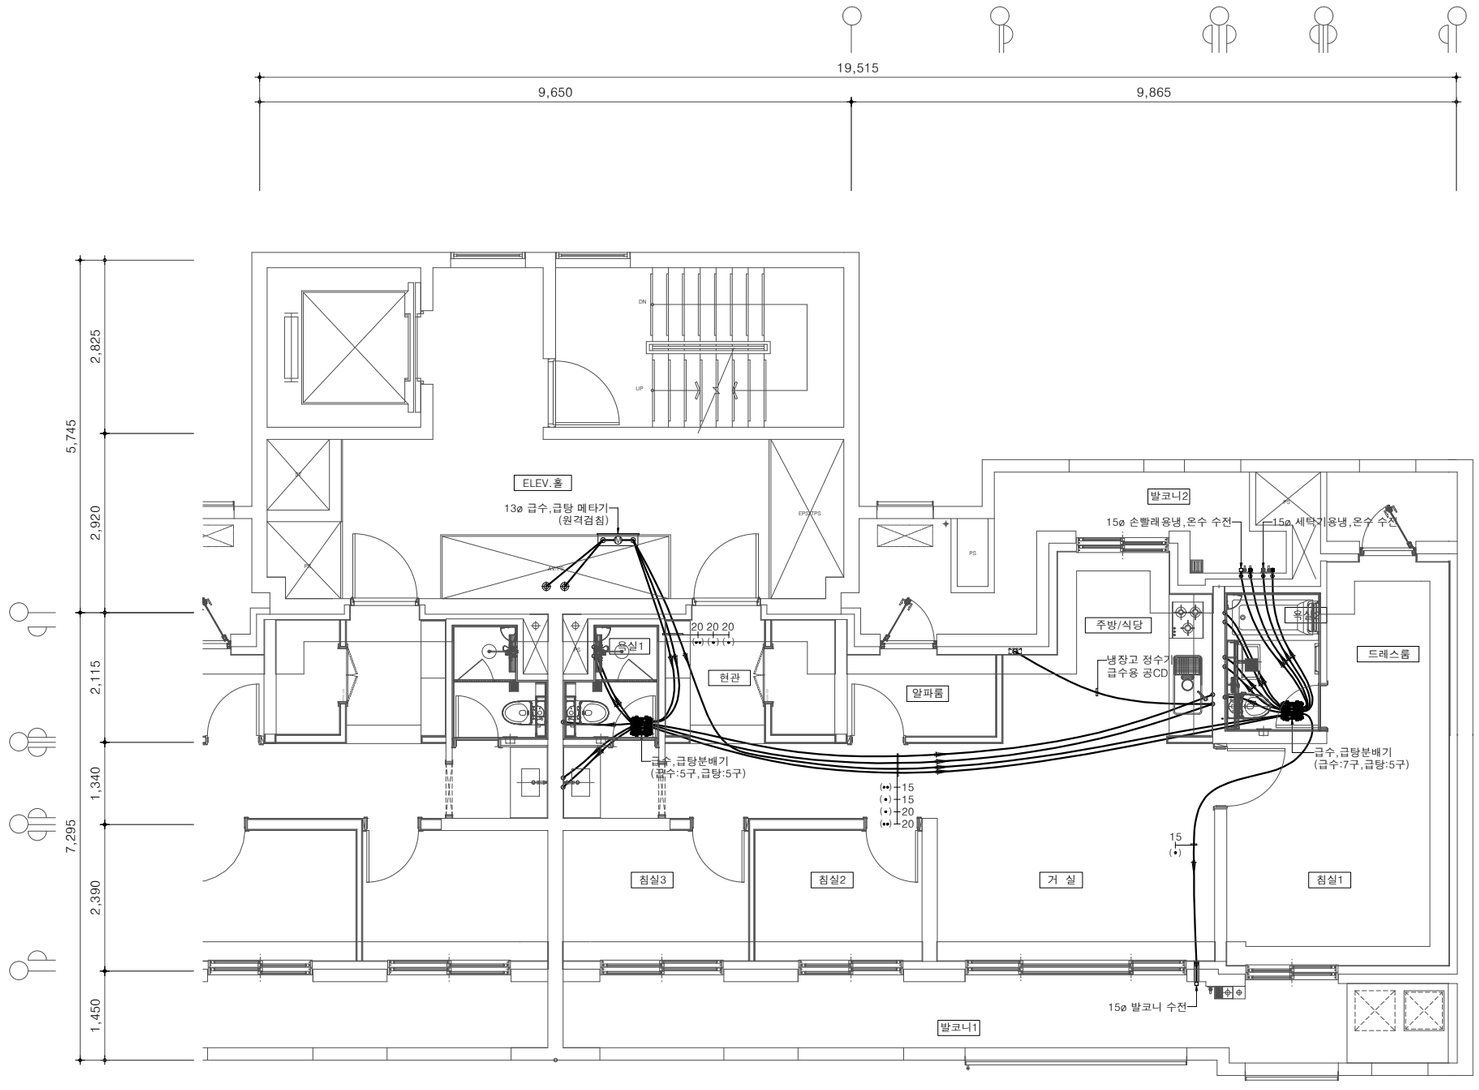

84m²A형 단위세대 급수,급탕배관 평면도(기본형)

축 척 : 1/100

경기주택도시공사
GYEONGGI HOUSING & URBAN DEVELOPMENT CORPORATION

설계명 PROJECT TITLE

화성동탄(2)A76-2BL
민간참여 공동주택사업

주기 NOTE
1. 현장여건에 따라 실시도면은 변경될 수 있다.
2. 세대 감압밸브를 설치해야 한다. (세대 급수압력은 0.245 MPa 이하)
3. 수전 및 배수구는 도서와 건본주택이 상이할 경우 건본주택을 따른다.
4. 급수/급탕배관은 이중관 배관을 적용하며, 급수급탕분배기는 하부층 천장에 설치한다.
5. 센서식 풋밸브 씽크수전 설치

NO	DATE	REVISION DESCRIPTION	APPD
△			
△			
△			
△			

설 계
DESIGN

대표전화

축 척	SCALE
A1	1 / 50
A3	1 / 100


일 자 DATE
2025. 12.

설계번호 PROJECT NO.
AR - 23 - 026

도면화일명 DWG. FILE NAME

도면번호 SHEET NO.
MP - 001

도면명 SUBJECT TITLE
84m²A형 단위세대
급수,급탕배관 평면도(기본형)

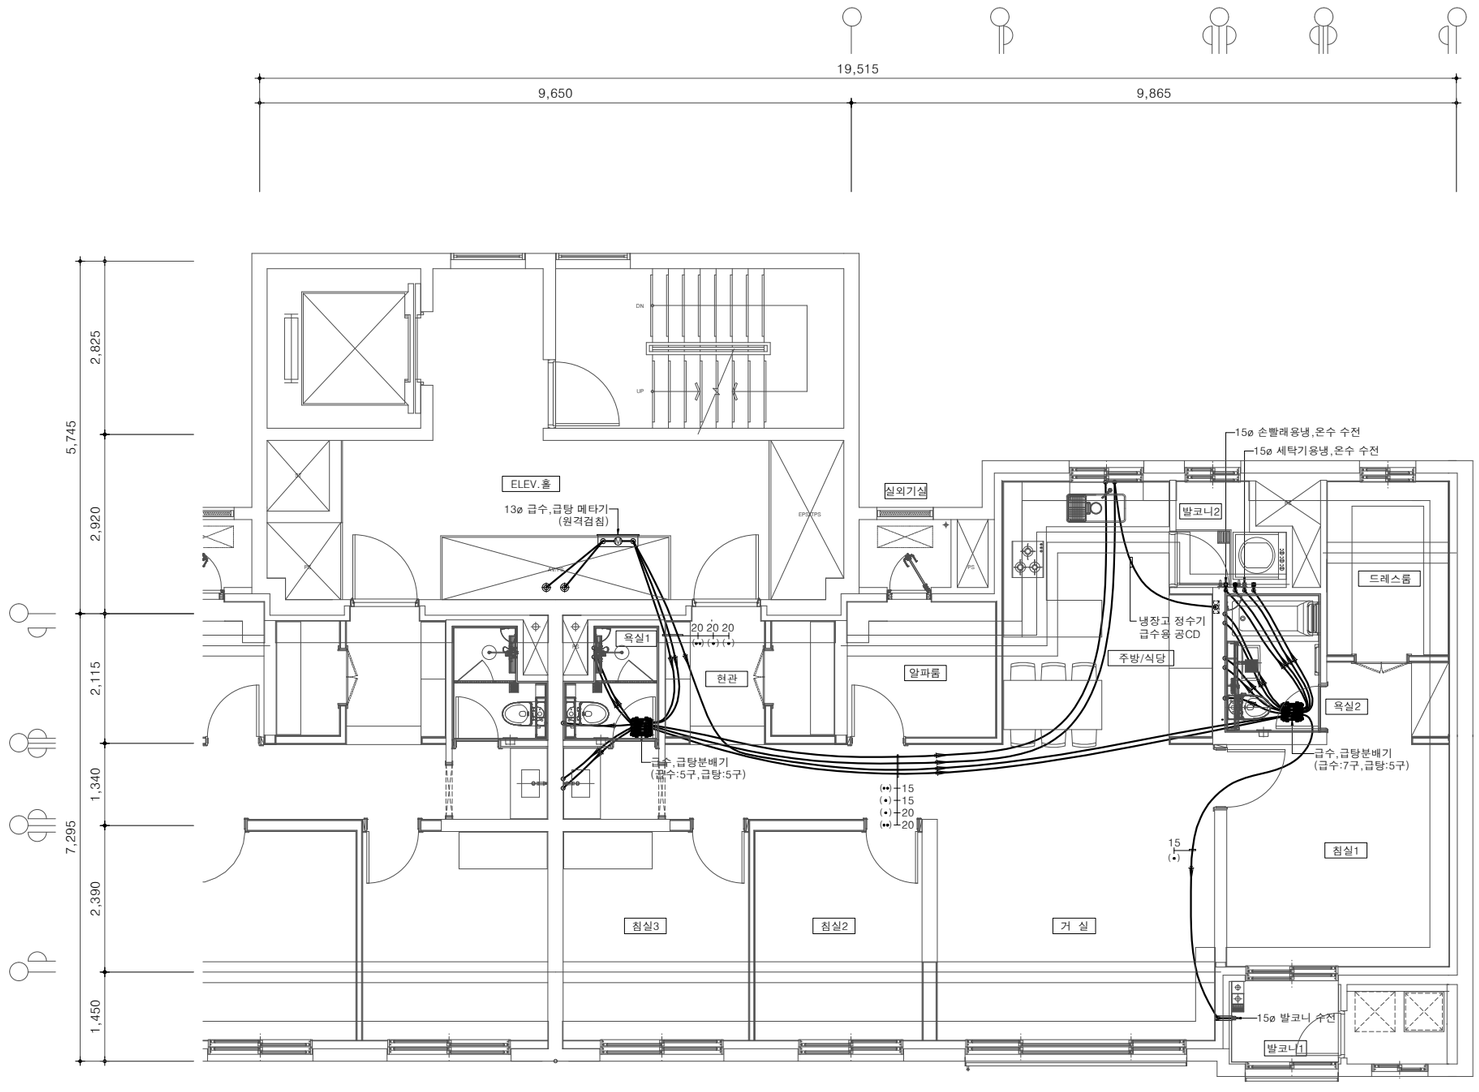

84m²A형 단위세대 급수,급탕배관 평면도(확장형)

축 척 : 1/100

경기주택도시공사
GYEONGGI HOUSING & URBAN DEVELOPMENT CORPORATION

설계명 PROJECT TITLE

화성동탄(2)A76-2BL
민간참여 공동주택사업

주기 NOTE
1. 현장여건에 따라 실시도면은 변경될 수 있다.
2. 세대 감압밸브를 설치해야 한다. (세대 급수압력은 0.245 MPa 이하)
3. 수전 및 배수구는 도서와 건본주택이 상이할 경우 건본주택을 따른다.
4. 급수/급탕배관은 이중관 배관을 적용하며, 급수급탕분배기는 하부층 천장에 설치한다.
5. 센서식 풋밸브 씽크수전 설치

NO	DATE	REVISION DESCRIPTION	APPD
△			
△			
△			
△			

설 계
DESIGN

대표전화

축 척	SCALE
A1	1 / 50
A3	1 / 100


일 자 DATE
2025. 12.

설계번호 PROJECT NO.
AR - 23 - 026

도면화일명 DWG. FILE NAME

도면번호 SHEET NO.
MP – 002

도면명 SUBJECT TITLE
84m²A형 단위세대
급수,급탕배관 평면도(확장형)

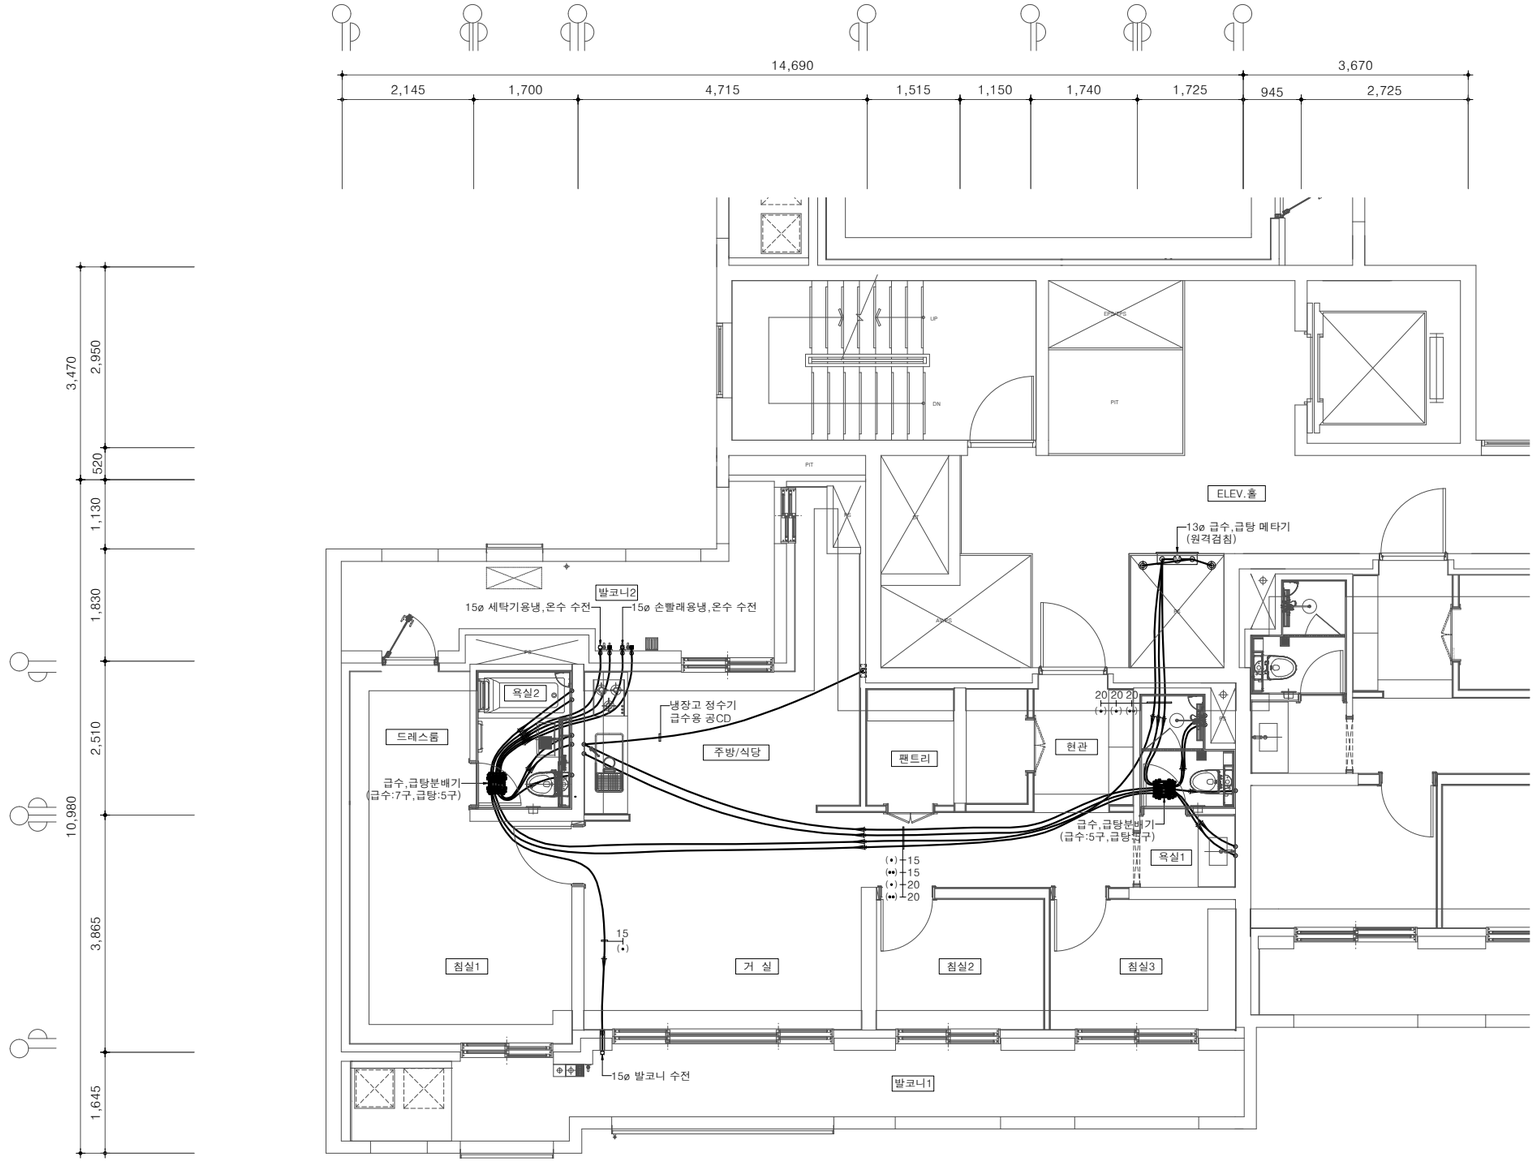

84m²B형 단위세대 급수,급탕배관 평면도(기본형)

축 척 : 1/100

경기주택도시공사
GYEONGGI HOUSING & URBAN DEVELOPMENT CORPORATION

설계명 PROJECT TITLE


화성동탄(2)A76-2BL
민간참여 공동주택사업

주기 NOTE
1. 현장여건에 따라 실시도면은 변경될 수 있다.
2. 세대 감압밸브를 설치해야 한다. (세대 급수압력은 0.245 MPa 이하)
3. 수전 및 배수구는 도서와 건본주택이 상이할 경우 건본주택을 따른다.
4. 급수/급탕배관은 이중관 배관을 적용하며, 급수급탕분배기는 하부층 천장에 설치한다.
5. 센서식 풋밸브 씽크수전 설치

NO	DATE	REVISION DESCRIPTION	APPD
△			
△			
△			
△			

설 계
DESIGN

대표전화	
축 척	SCALE
A1	1 / 50
A3	1 / 100
일 자 DATE	2025. 12.
설계번호 PROJECT NO.	AR - 23 - 026
도면화일명 DWG. FILE NAME	
도면번호 SHEET NO.	MP - 003
도면명 SUBJECT TITLE	84m²B형 단위세대 급수,급탕배관 평면도(기본형)

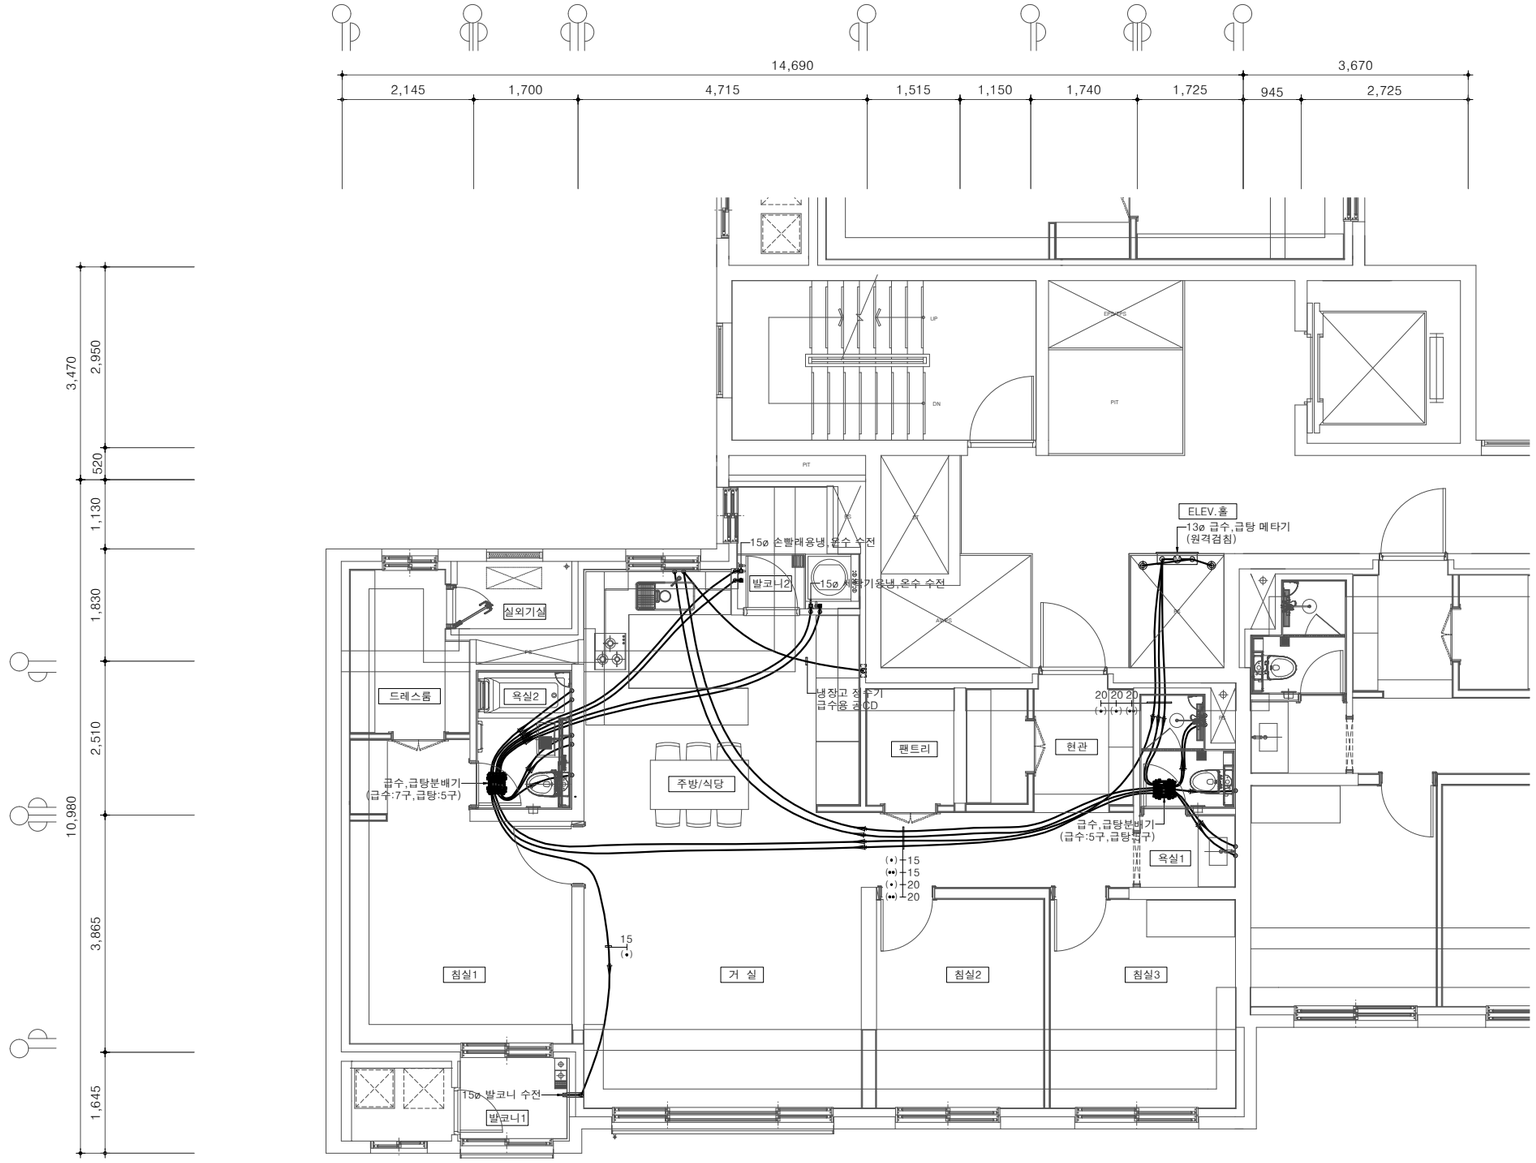

84m²B형 단위세대 급수,급탕배관 평면도(확장형)

축 척 : 1/100

경기주택도시공사
GYEONGGI HOUSING & URBAN DEVELOPMENT CORPORATION

설계명 PROJECT TITLE

화성동탄(2)A76-2BL
민간참여 공동주택사업

주기 NOTE

1. 현장여건에 따라 실시도면은 변경될 수 있다.
2. 세대 감압밸브를 설치해야 한다. (세대 급수압력은 0.245 MPa 이하)
3. 수전 및 배수구는 도서와 건본주택이 상이할 경우 건본주택을 따른다.
4. 급수/급탕배관은 이중관 배관을 적용하며, 급수급탕분배기는 하부층 천장에 설치한다.
5. 센서식 풋밸브 씽크수전 설치

NO	DATE	REVISION DESCRIPTION	APPD

설 계
DESIGN

대표전화

축 척	SCALE
A1	1 / 50
A3	1 / 100


일 자 DATE
2025. 12.

설계번호 PROJECT NO.
AR - 23 - 026

도면화일명 DWG. FILE NAME

도면번호 SHEET NO.
MP – 004

도면명 SUBJECT TITLE
84m²B형 단위세대
급수,급탕배관 평면도(확장형)

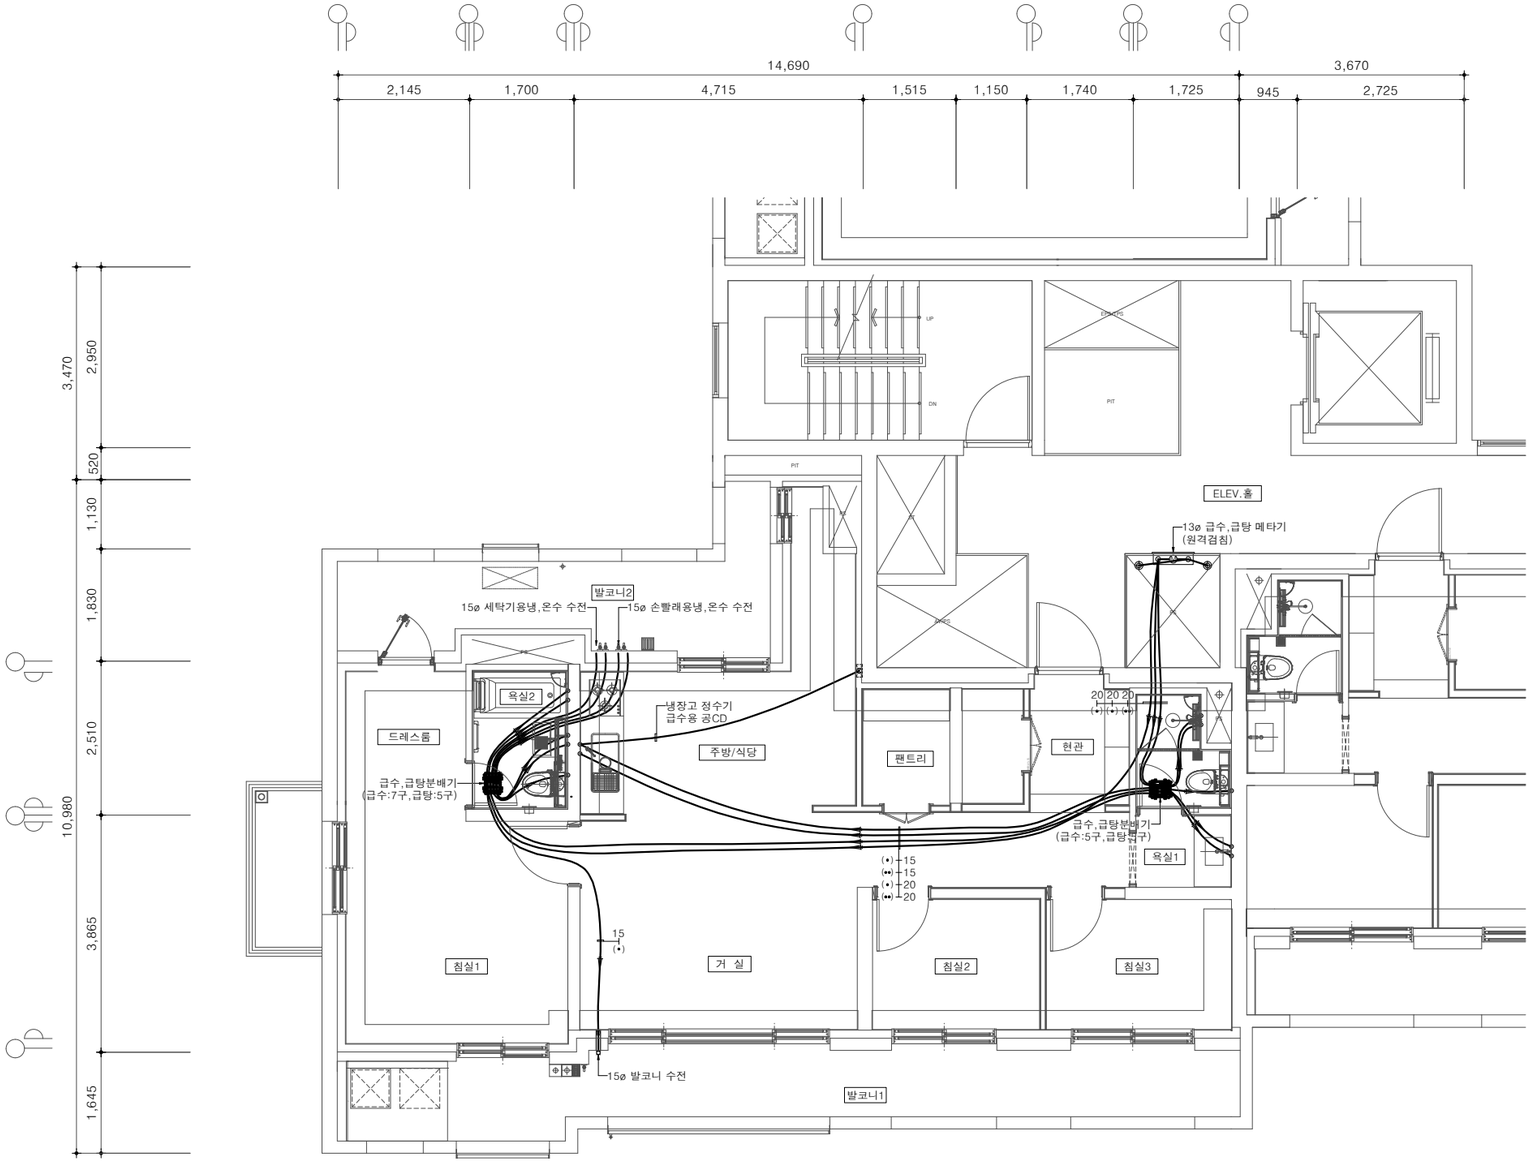

84m²C형 단위세대 급수,급탕배관 평면도(기본형)

축 척 : 1/100

경기주택도시공사
GYEONGGI HOUSING & URBAN DEVELOPMENT CORPORATION

설계명 PROJECT TITLE

화성동탄(2)A76-2BL
민간참여 공동주택사업


주기 NOTE

1. 현장여건에 따라 실시도면은 변경될 수 있다.
2. 세대 감압밸브를 설치해야 한다. (세대 급수압력은 0.245 MPa 이하)
3. 수전 및 배수구는 도서와 건본주택이 상이할 경우 건본주택을 따른다.
4. 급수/급탕배관은 이중관 배관을 적용하며, 급수급탕분배기는 하부층 천장에 설치한다.
5. 센서식 풋밸브 씽크수전 설치

NO	DATE	REVISION DESCRIPTION	APPD
△			
△			
△			
△			

설 계
DESIGN

대표전화	
축 척	SCALE
A1	1 / 50
A3	1 / 100
일 자 DATE	2025. 12.
설계번호 PROJECT NO.	AR - 23 - 026
도면화일명 DWG. FILE NAME	
도면번호 SHEET NO.	MP - 005
도면명 SUBJECT TITLE	84m²C형 단위세대 급수,급탕배관 평면도(기본형)

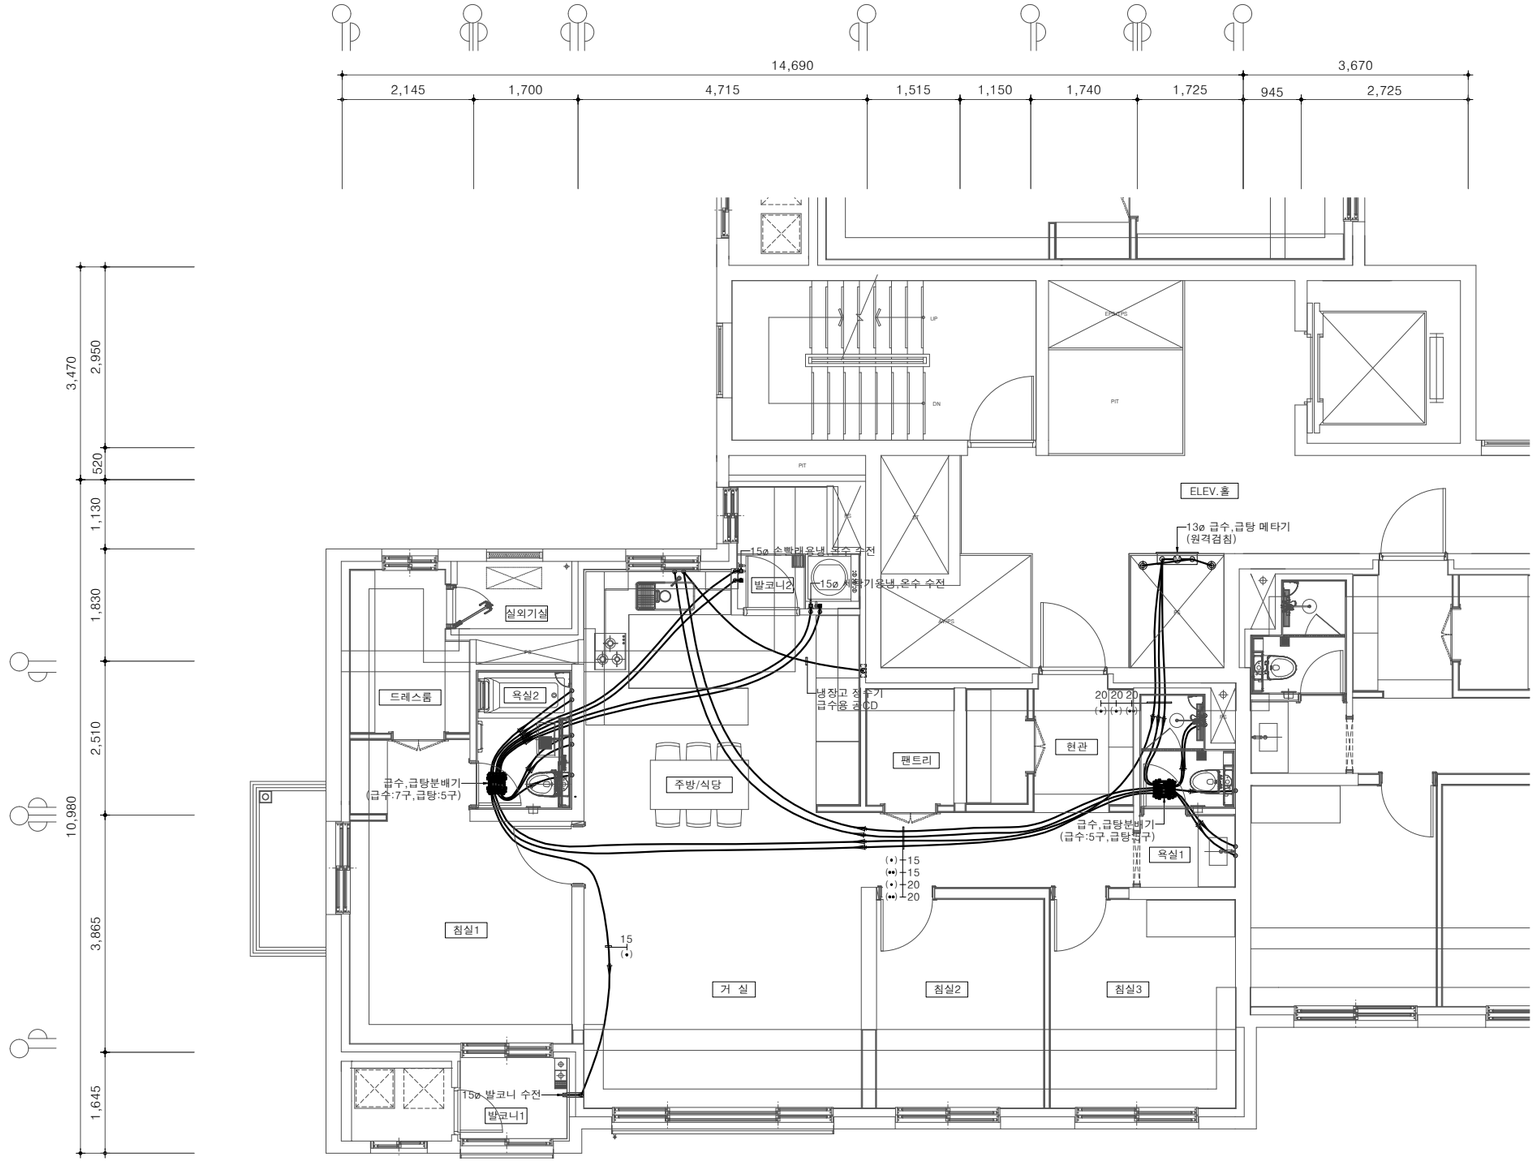

84m²C형 단위세대 급수,급탕배관 평면도(확장형)

축 척 : 1/100

경기주택도시공사
GYEONGGI HOUSING & URBAN DEVELOPMENT CORPORATION

설계명 PROJECT TITLE


화성동탄(2)A76-2BL
민간참여 공동주택사업

주기 NOTE
1. 현장여건에 따라 실시도면은 변경될 수 있다.
2. 세대 감압밸브를 설치해야 한다. (세대 급수압력은 0.245 MPa 이하)
3. 수전 및 배수구는 도서와 건본주택이 상이할 경우 건본주택을 따른다.
4. 급수/급탕배관은 이중관 배관을 적용하며, 급수급탕분배기는 하부층 천장에 설치한다.
5. 센서식 풋밸브 씽크수전 설치

NO	DATE	REVISION DESCRIPTION	APPD
△			
△			
△			
△			

설 계
DESIGN

대표전화	
축 척	SCALE
A1	1 / 50
A3	1 / 100
일 자 DATE	2025. 12.
설계번호 PROJECT NO.	AR - 23 - 026
도면화일명 DWG. FILE NAME	
도면번호 SHEET NO.	MP - 006
도면명 SUBJECT TITLE	84m²C형 단위세대 급수,급탕배관 평면도(확장형)

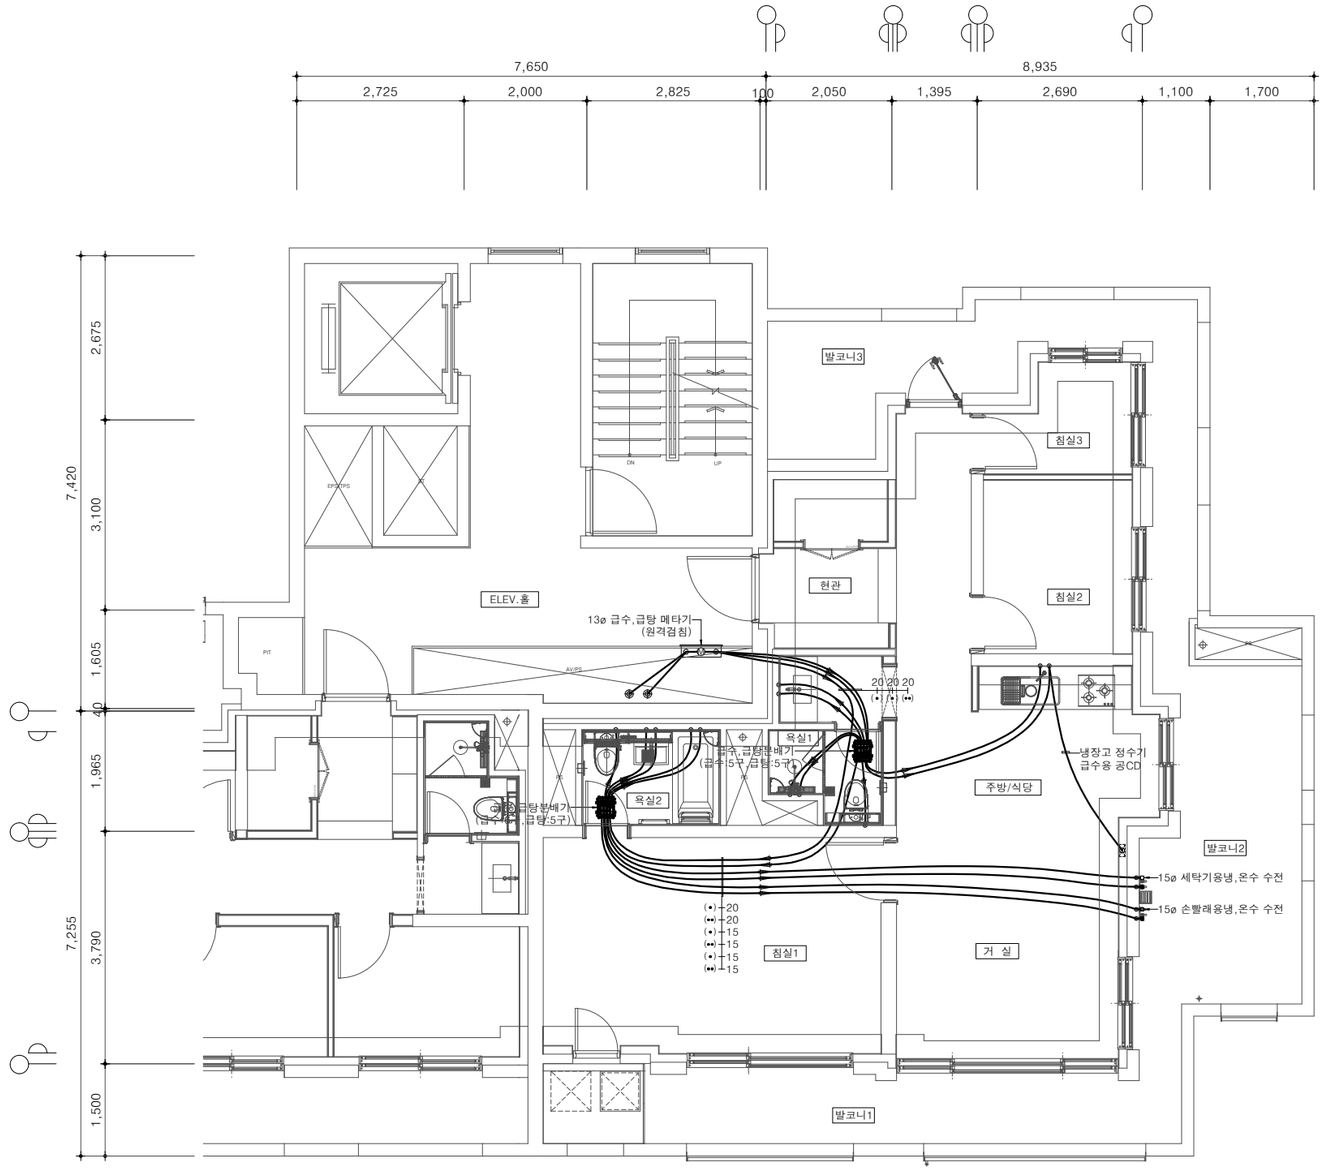

84m²D형 단위세대 급수,급탕배관 평면도(기본형)

축 척 : 1/100

경기주택도시공사
GYEONGGI HOUSING & URBAN DEVELOPMENT CORPORATION

설계명 PROJECT TITLE

화성동탄(2)A76-2BL
민간참여 공동주택사업

주기 NOTE
1. 현장여건에 따라 실시도면은 변경될 수 있다.
2. 세대 감압밸브를 설치해야 한다. (세대 급수압력은 0.245 MPa 이하)
3. 수전 및 배수구는 도서와 건본주택이 상이할 경우 건본주택을 따른다.
4. 급수/급탕배관은 이중관 배관을 적용하며, 급수급탕분배기는 하부층 천장에 설치한다.
5. 센서식 풋밸브 씽크수전 설치

NO	DATE	REVISION DESCRIPTION	APPD
△			
△			
△			
△			

설 계
DESIGN

대표전화

축 척	SCALE
A1	1 / 50
A3	1 / 100


일 자 DATE
2025. 12.

설계번호 PROJECT NO.
AR - 23 - 026

도면화일명 DWG. FILE NAME

도면번호 SHEET NO.
MP - 007

도면명 SUBJECT TITLE
84m²D형 단위세대
급수,급탕배관 평면도(기본형)

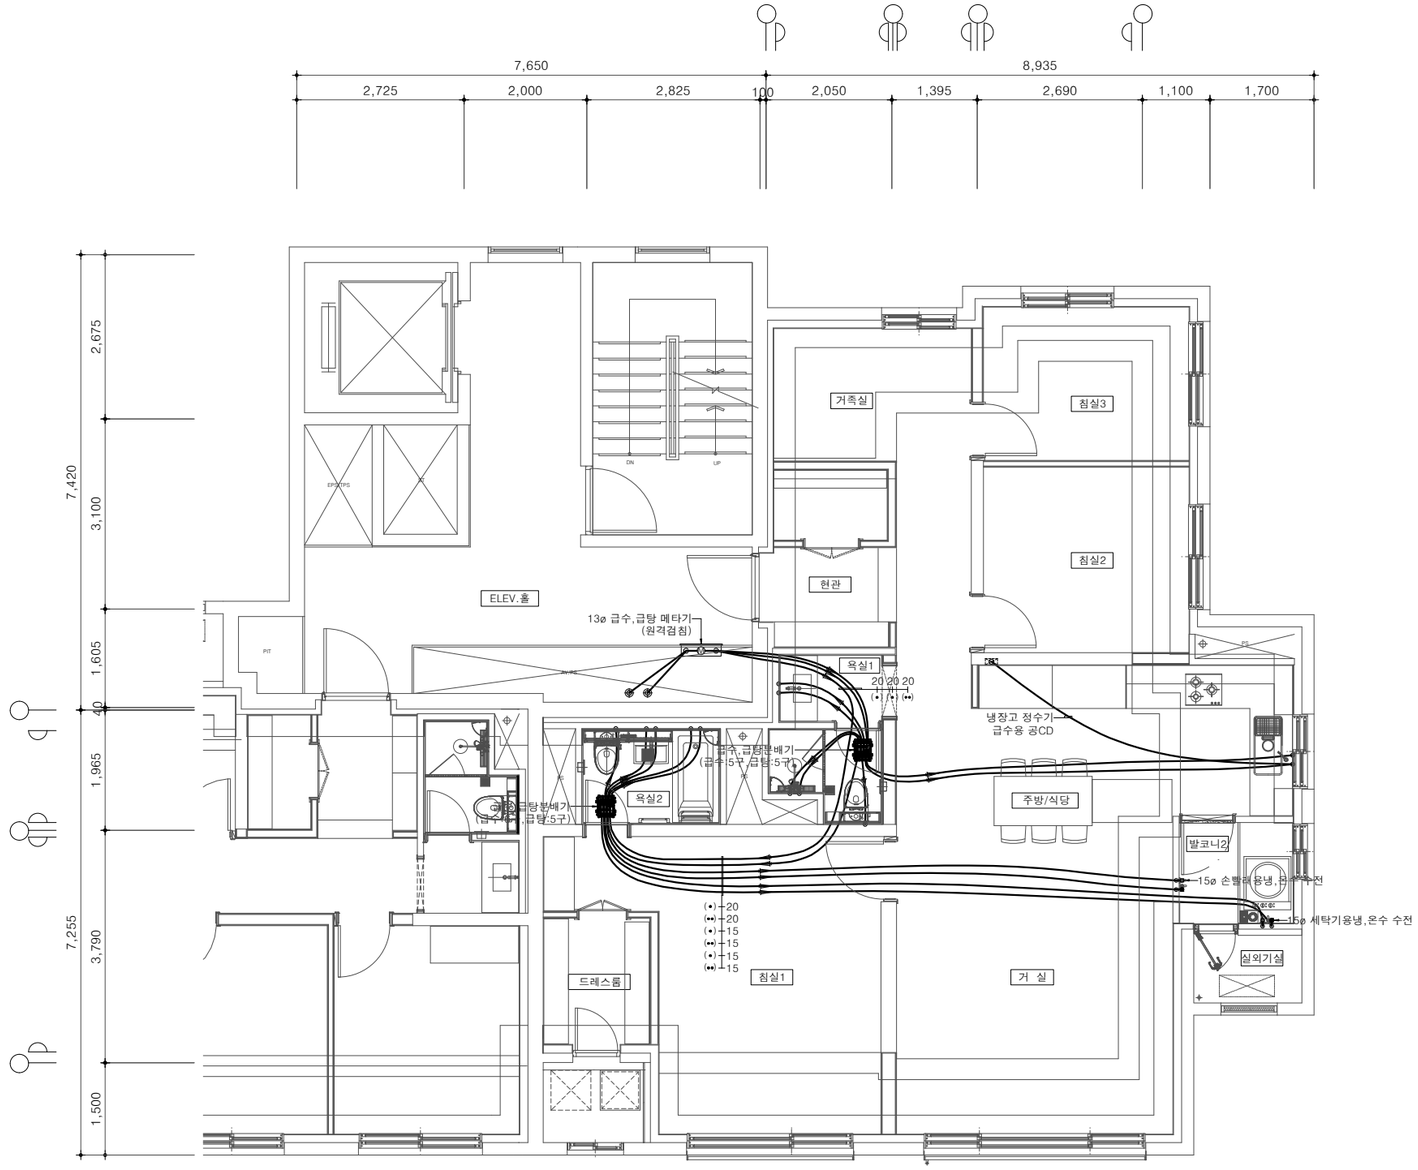

84m²D형 단위세대 급수,급탕배관 평면도(확장형)

축 척 : 1/100

경기주택도시공사
GYEONGGI HOUSING & URBAN DEVELOPMENT CORPORATION

설계명 PROJECT TITLE


화성동탄(2)A76-2BL
민간참여 공동주택사업

주기 NOTE
1. 현장여건에 따라 실시도면은 변경될 수 있다.
2. 세대 감압밸브를 설치해야 한다. (세대 급수압력은 0.245 MPa 이하)
3. 수전 및 배수구는 도서와 건본주택이 상이할 경우 건본주택을 따른다.
4. 급수/급탕배관은 이중관 배관을 적용하며, 급수급탕분배기는 하부층 천장에 설치한다.
5. 센서식 풋밸브 씽크수전 설치

NO	DATE	REVISION DESCRIPTION	APPD

설 계
DESIGN

대표전화	
축 척	SCALE
A1	1 / 50
A3	1 / 100
일 자	DATE
	2025. 12.
설계번호	PROJECT NO.
	AR - 23 - 026
도면화일명	DWG. FILE NAME
도면번호	SHEET NO.
	MP - 008
도면명	SUBJECT TITLE
	84m²D형 단위세대 급수,급탕배관 평면도(확장형)

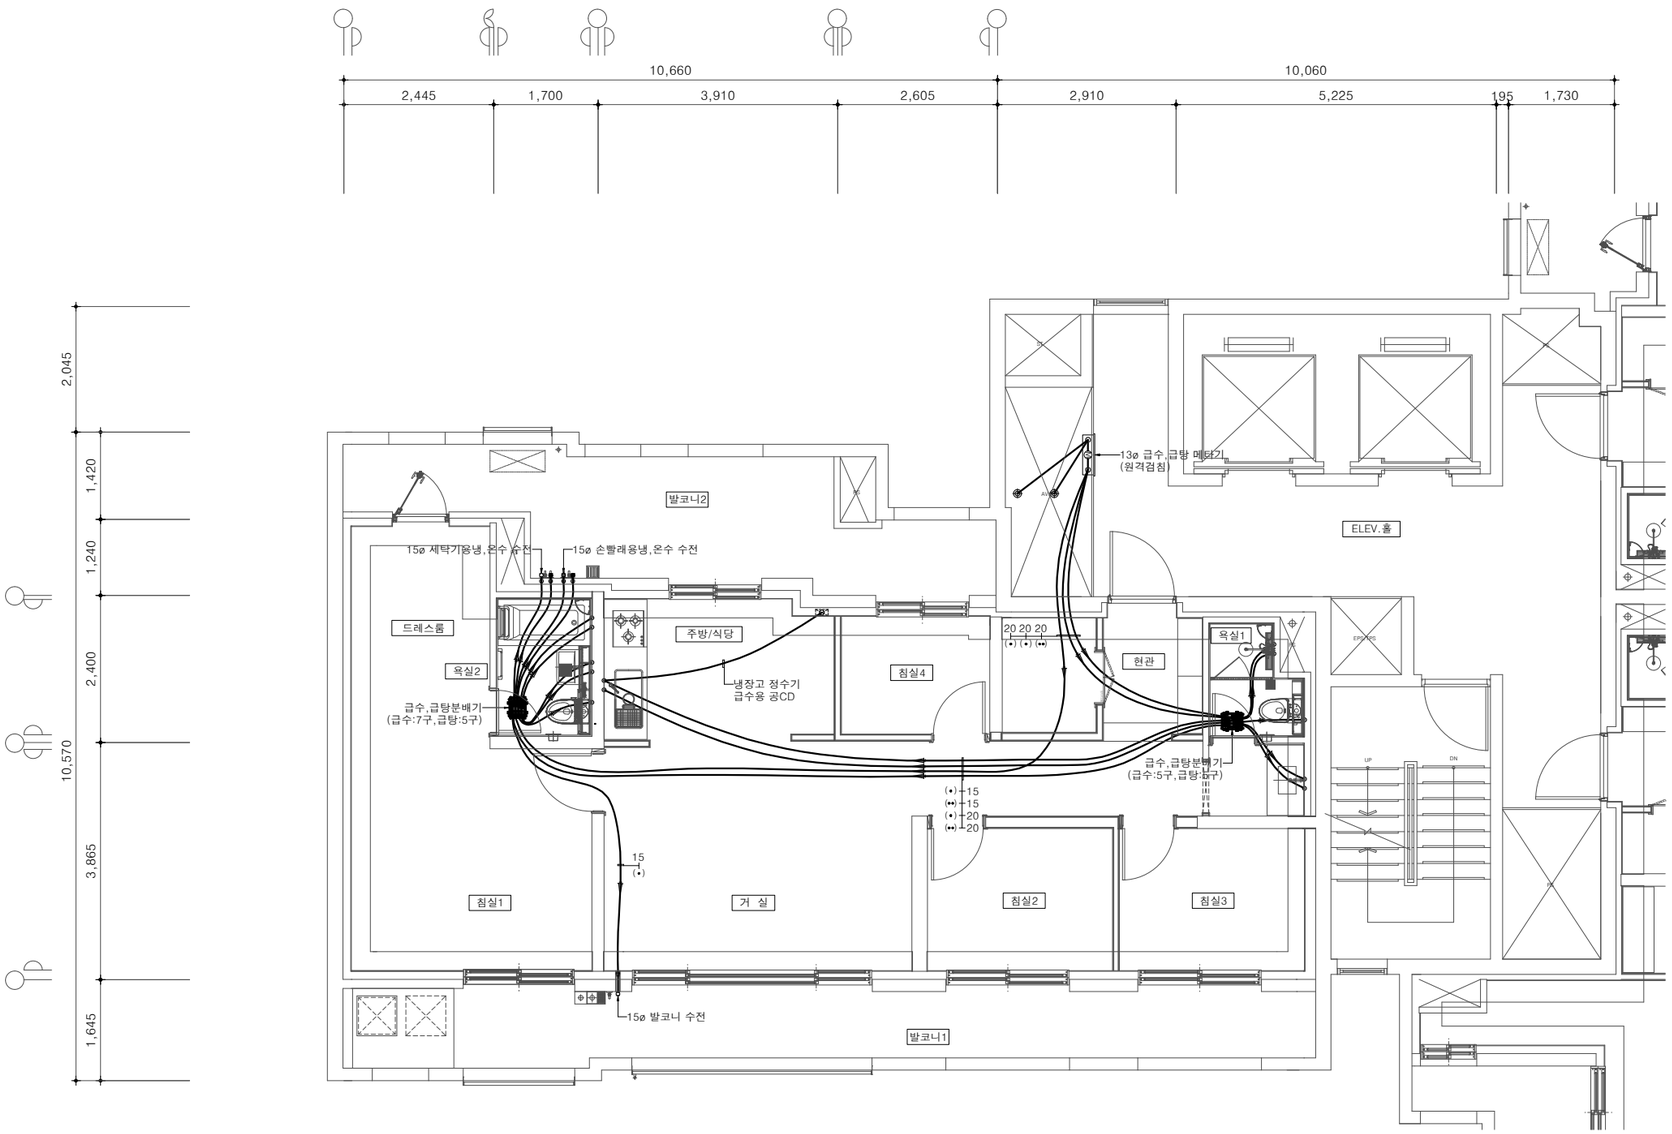

97m²A형 단위세대 급수,급탕배관 평면도(기본형)

축 척 : 1/100

경기주택도시공사
GYEONGGI HOUSING & URBAN DEVELOPMENT CORPORATION

설계명 PROJECT TITLE


화성동탄(2)A76-2BL
민간참여 공동주택사업

주기 NOTE
1. 현장여건에 따라 실시도면은 변경될 수 있다.
2. 세대 감압밸브를 설치해야 한다. (세대 급수압력은 0.245 MPa 이하)
3. 수전 및 배수구는 도서와 건본주택이 상이할 경우 건본주택을 따른다.
4. 급수/급탕배관은 이중관 배관을 적용하며, 급수급탕분배기는 하부층 천장에 설치한다.
5. 센서식 풋밸브 씽크수전 설치

NO	DATE	REVISION DESCRIPTION	APPD
△			
△			
△			
△			

설 계
DESIGN

대표전화	
축 척	SCALE
A1	1 / 50
A3	1 / 100
일 자 DATE	2025. 12.
설계번호 PROJECT NO.	AR - 23 - 026
도면화일명 DWG. FILE NAME	
도면번호 SHEET NO.	MP – 009
도면명 SUBJECT TITLE	97m²A형 단위세대 급수,급탕배관 평면도(기본형)

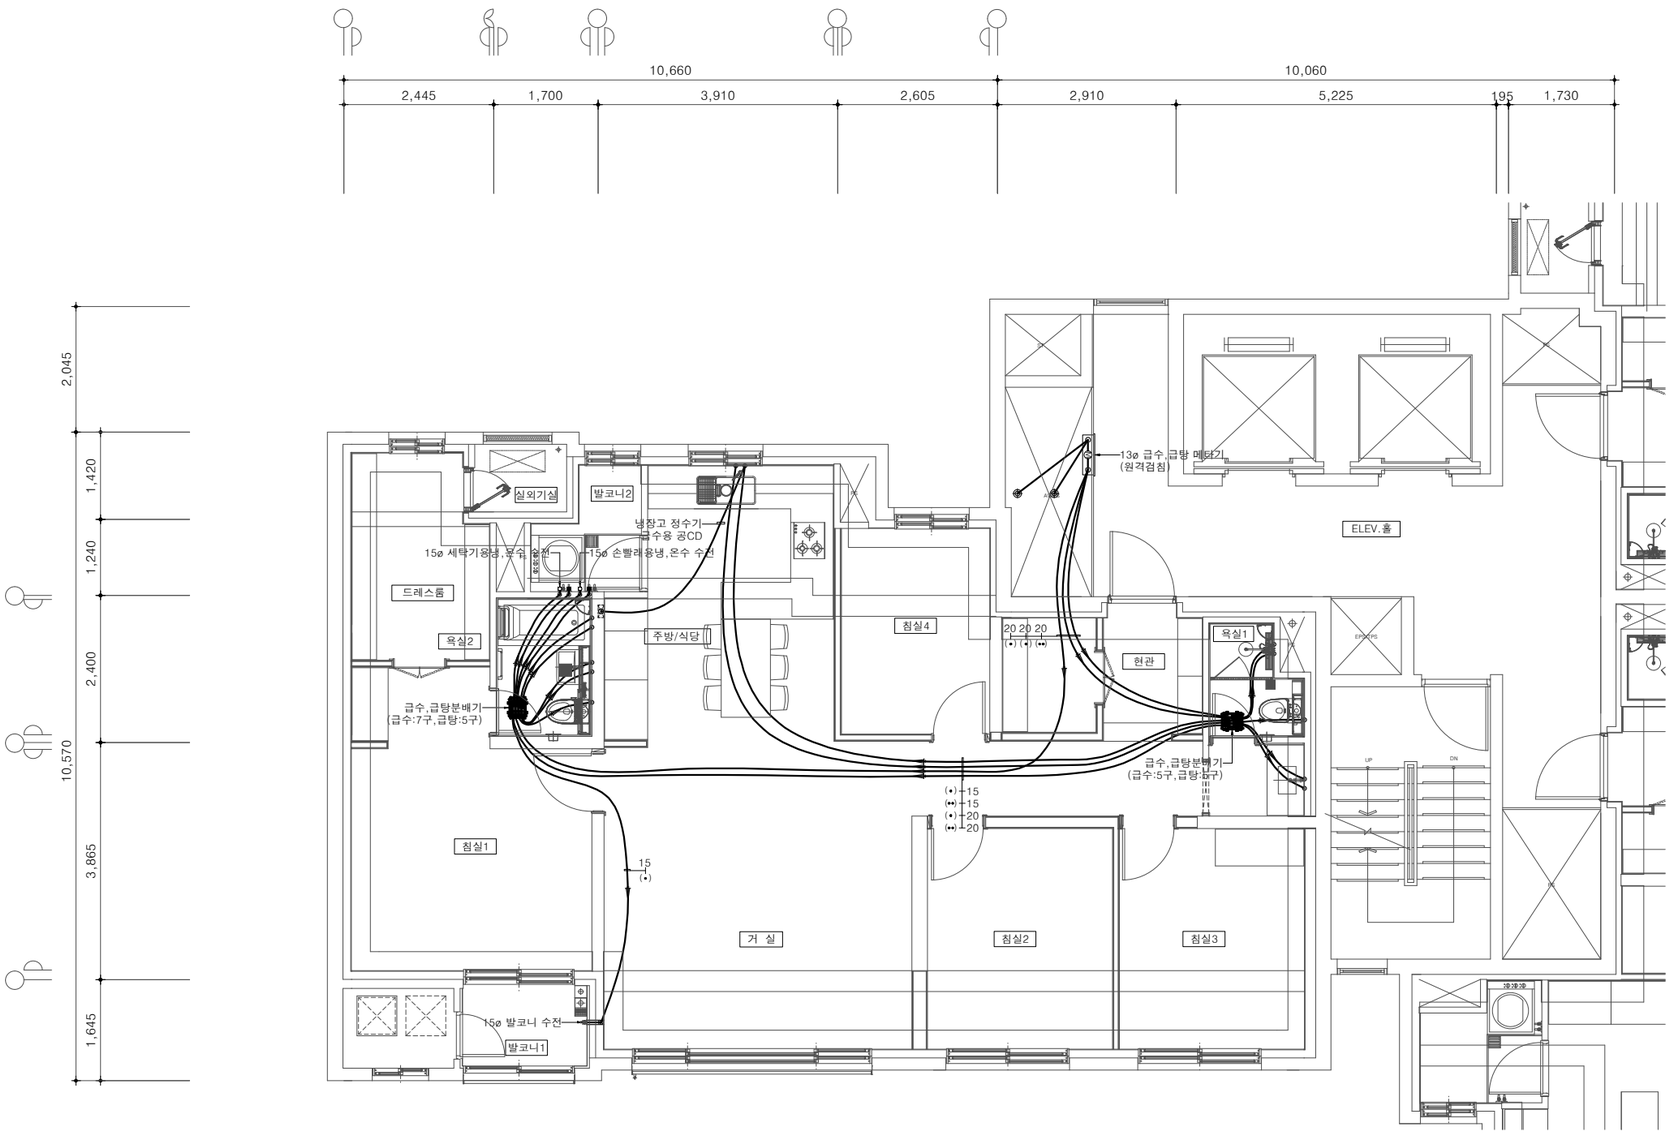

97m²A형 단위세대 급수,급탕배관 평면도(확장형)

축 척 : 1/100

경기주택도시공사
GYEONGGI HOUSING & URBAN DEVELOPMENT CORPORATION

설계명 PROJECT TITLE


화성동탄(2)A76-2BL
민간참여 공동주택사업

주기 NOTE
1. 현장여건에 따라 실시도면은 변경될 수 있다.
2. 세대 감압밸브를 설치해야 한다. (세대 급수압력은 0.245 MPa 이하)
3. 수전 및 배수구는 도서와 건본주택이 상이할 경우 건본주택을 따른다.
4. 급수/급탕배관은 이중관 배관을 적용하며, 급수급탕분배기는 하부층 천장에 설치한다.
5. 센서식 풋밸브 씽크수전 설치

NO	DATE	REVISION DESCRIPTION	APPD
△			
△			
△			
△			

설 계
DESIGN

대표전화	
축 척	SCALE
A1	1 / 50
A3	1 / 100
일 자	DATE
	2025. 12.
설계번호	PROJECT NO.
	AR - 23 - 026
도면화일명	DWG. FILE NAME
도면번호	SHEET NO.
	MP - 010
도면명	SUBJECT TITLE
	97m²A형 단위세대 급수,급탕배관 평면도(확장형)

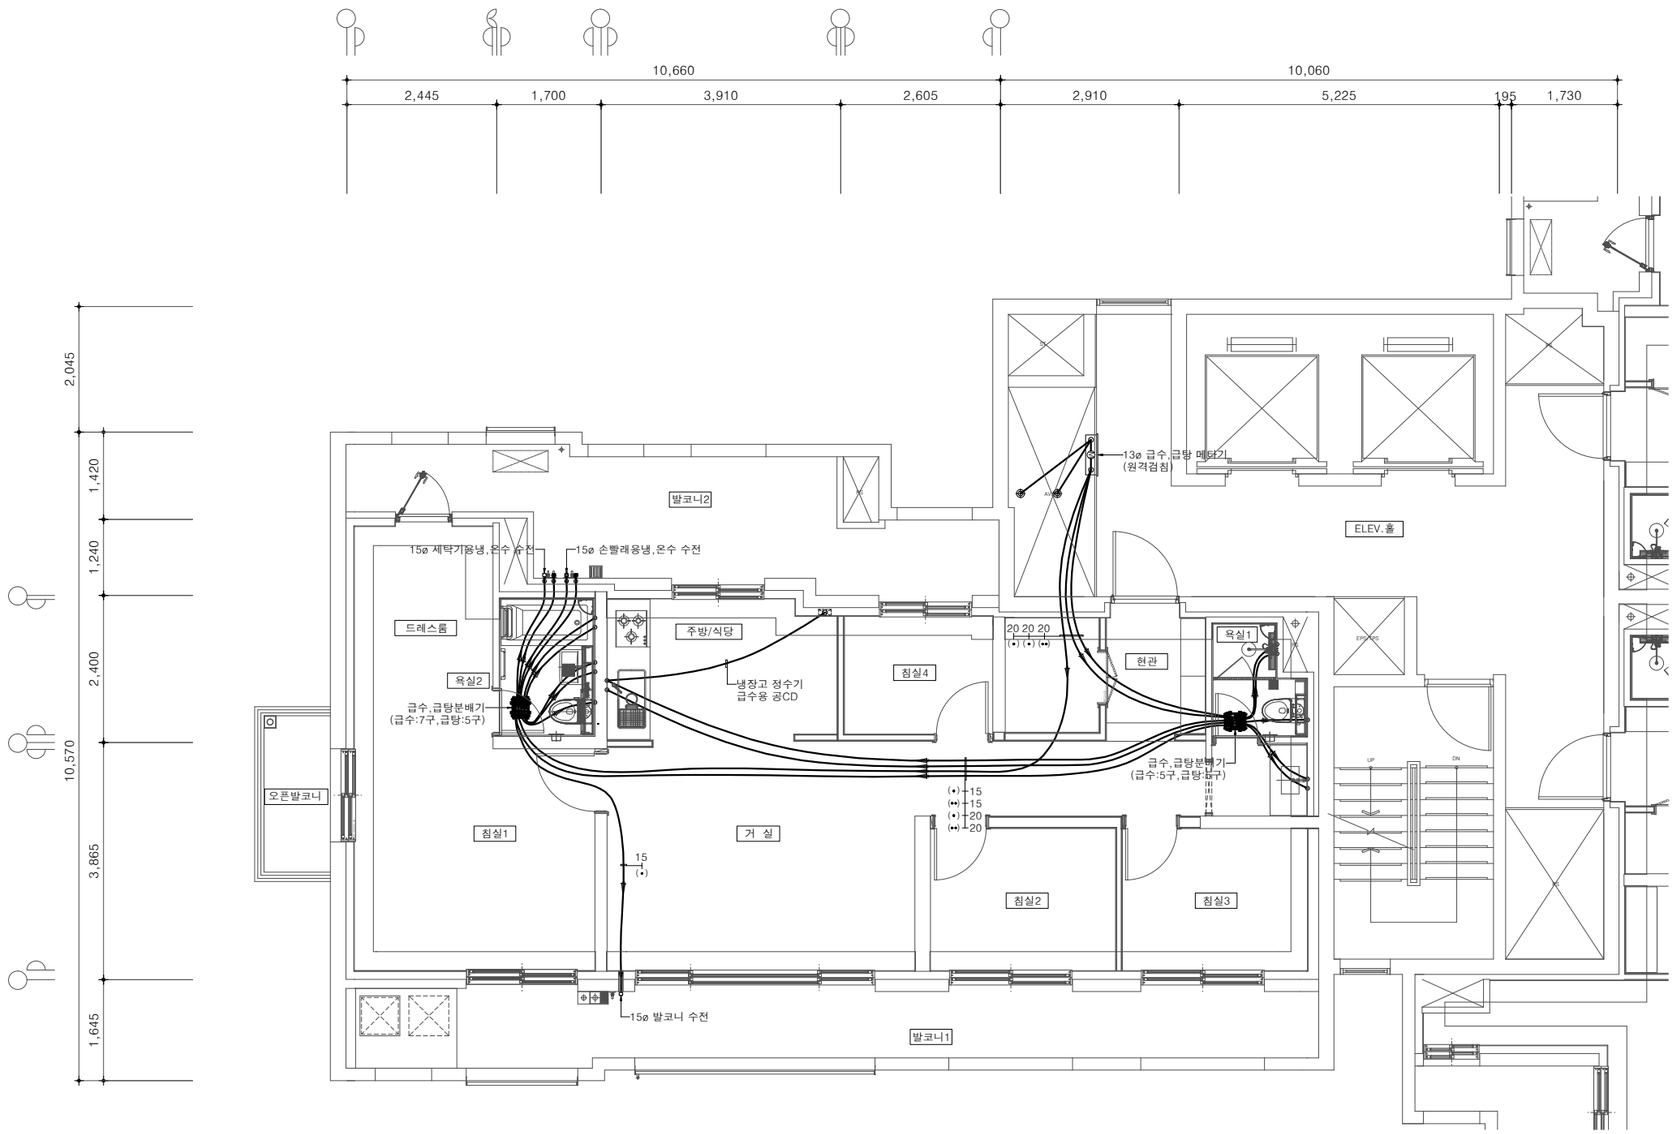

97m²B형 단위세대 급수,급탕배관 평면도(기본형)

축 척 : 1/100

경기주택도시공사
GYEONGGI HOUSING & URBAN DEVELOPMENT CORPORATION

설계명 PROJECT TITLE

화성동탄(2)A76-2BL 민간참여 공동주택사업


주기 NOTE

1. 현장여건에 따라 실시도면은 변경될 수 있다.
2. 세대 감압밸브를 설치해야 한다. (세대 급수압력은 0.245 MPa 이하)
3. 수전 및 배수구는 도서와 건본주택이 상이할 경우 건본주택을 따른다.
4. 급수/급탕배관은 이중관 배관을 적용하며, 급수급탕분배기는 하부층 천장에 설치한다.
5. 센서식 풋밸브 씽크수전 설치

NO	DATE	REVISION DESCRIPTION	APPD
△			
△			
△			
△			

설 계
DESIGN

대표전화	
축 척	SCALE
A1	1 / 50
A3	1 / 100
일 자	DATE
	2025. 12.
설계번호	PROJECT NO.
	AR - 23 - 026
도면화일명	DWG. FILE NAME
도면번호	SHEET NO.
	MP – 011
도면명	SUBJECT TITLE
	97m²B형 단위세대 급수,급탕배관 평면도(기본형)

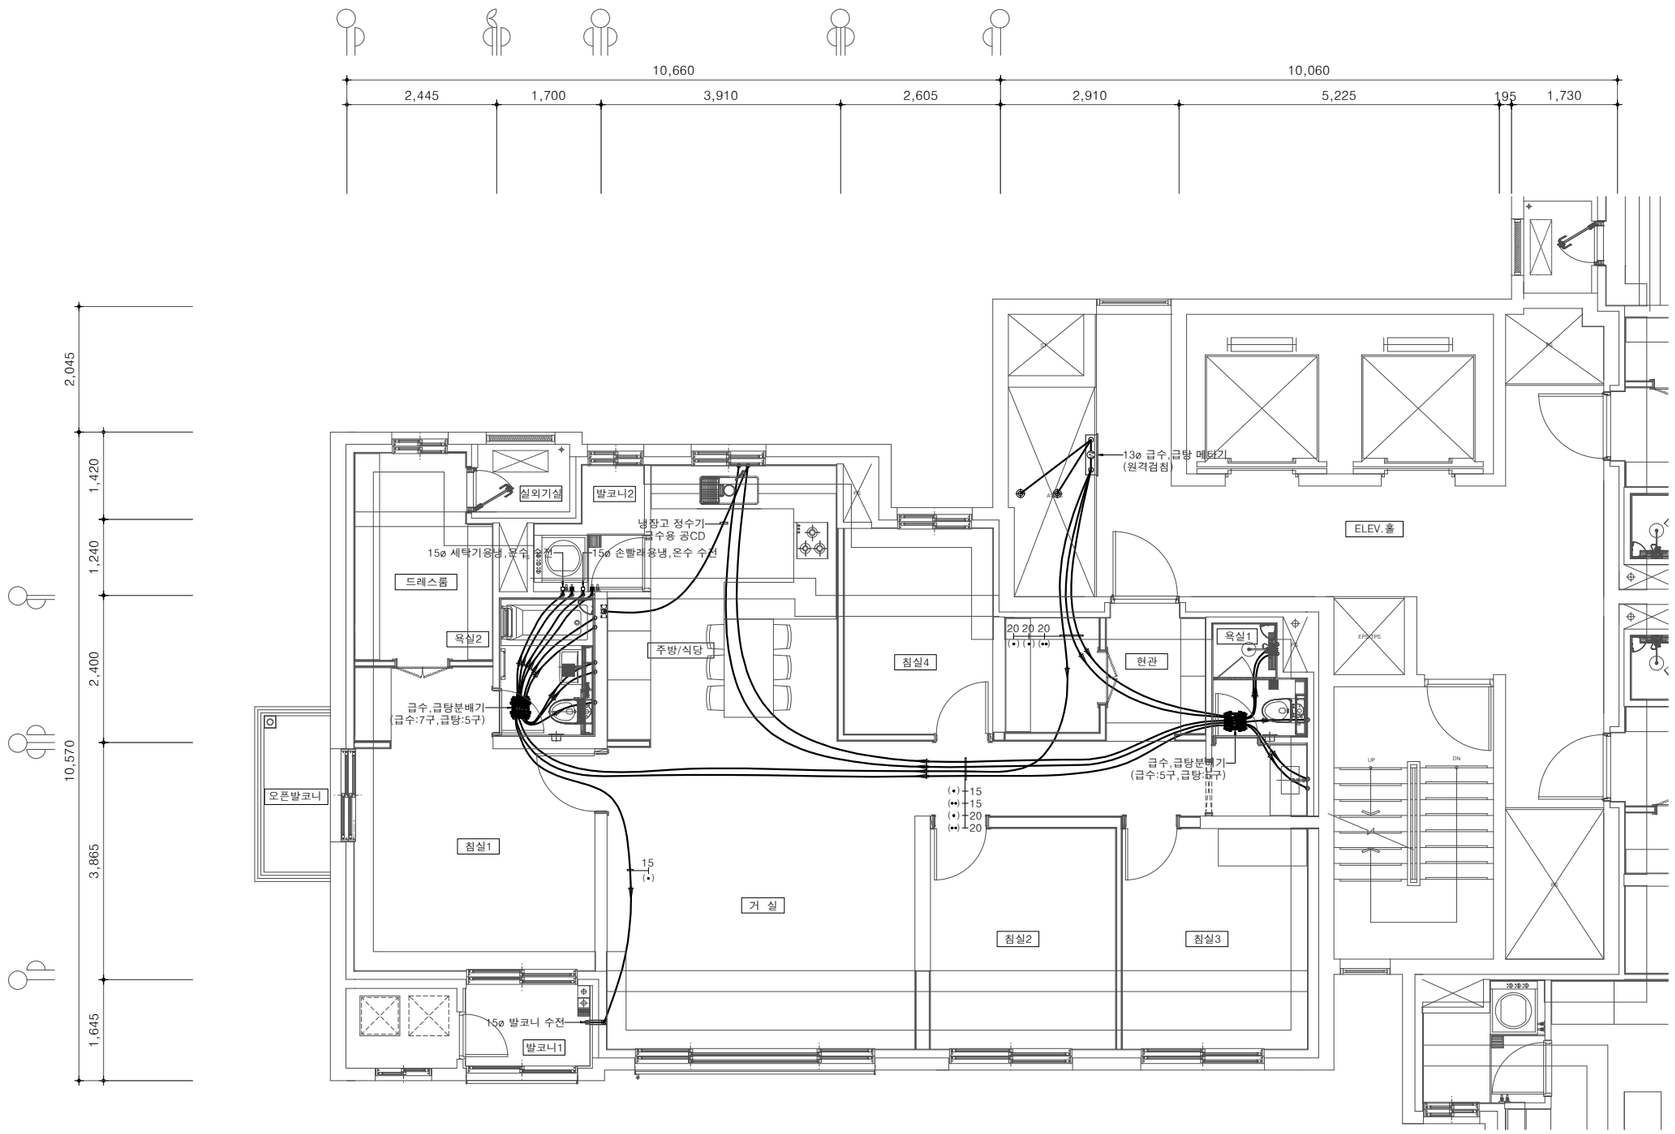

M 97m²B형 단위세대 급수,급탕배관 평면도(확장형)

축 척 : 1/100

경기주택도시공사
GYEONGGI HOUSING & URBAN DEVELOPMENT CORPORATION

설계명 PROJECT TITLE


화성동탄(2)A76-2BL
민간참여 공동주택사업

주기 NOTE
1. 현장여건에 따라 실시도면은 변경될 수 있다.
2. 세대 감압밸브를 설치해야 한다. (세대 급수압력은 0.245 MPa 이하)
3. 수전 및 배수구는 도서와 건본주택이 상이할 경우 건본주택을 따른다.
4. 급수/급탕배관은 이중관 배관을 적용하며, 급수급탕분배기는 하부층 천장에 설치한다.
5. 센서식 풋밸브 씽크수전 설치

NO	DATE	REVISION DESCRIPTION	APPD
△			
△			
△			
△			

설 계
DESIGN

대표전화	
축 척	SCALE
A1	1 / 50
A3	1 / 100
일 자	DATE
	2025. 12.
설계번호	PROJECT NO.
	AR - 23 - 026
도면화일명	DWG. FILE NAME
도면번호	SHEET NO.
	MP - 012
도면명	SUBJECT TITLE
	97m²B형 단위세대 급수,급탕배관 평면도(확장형)

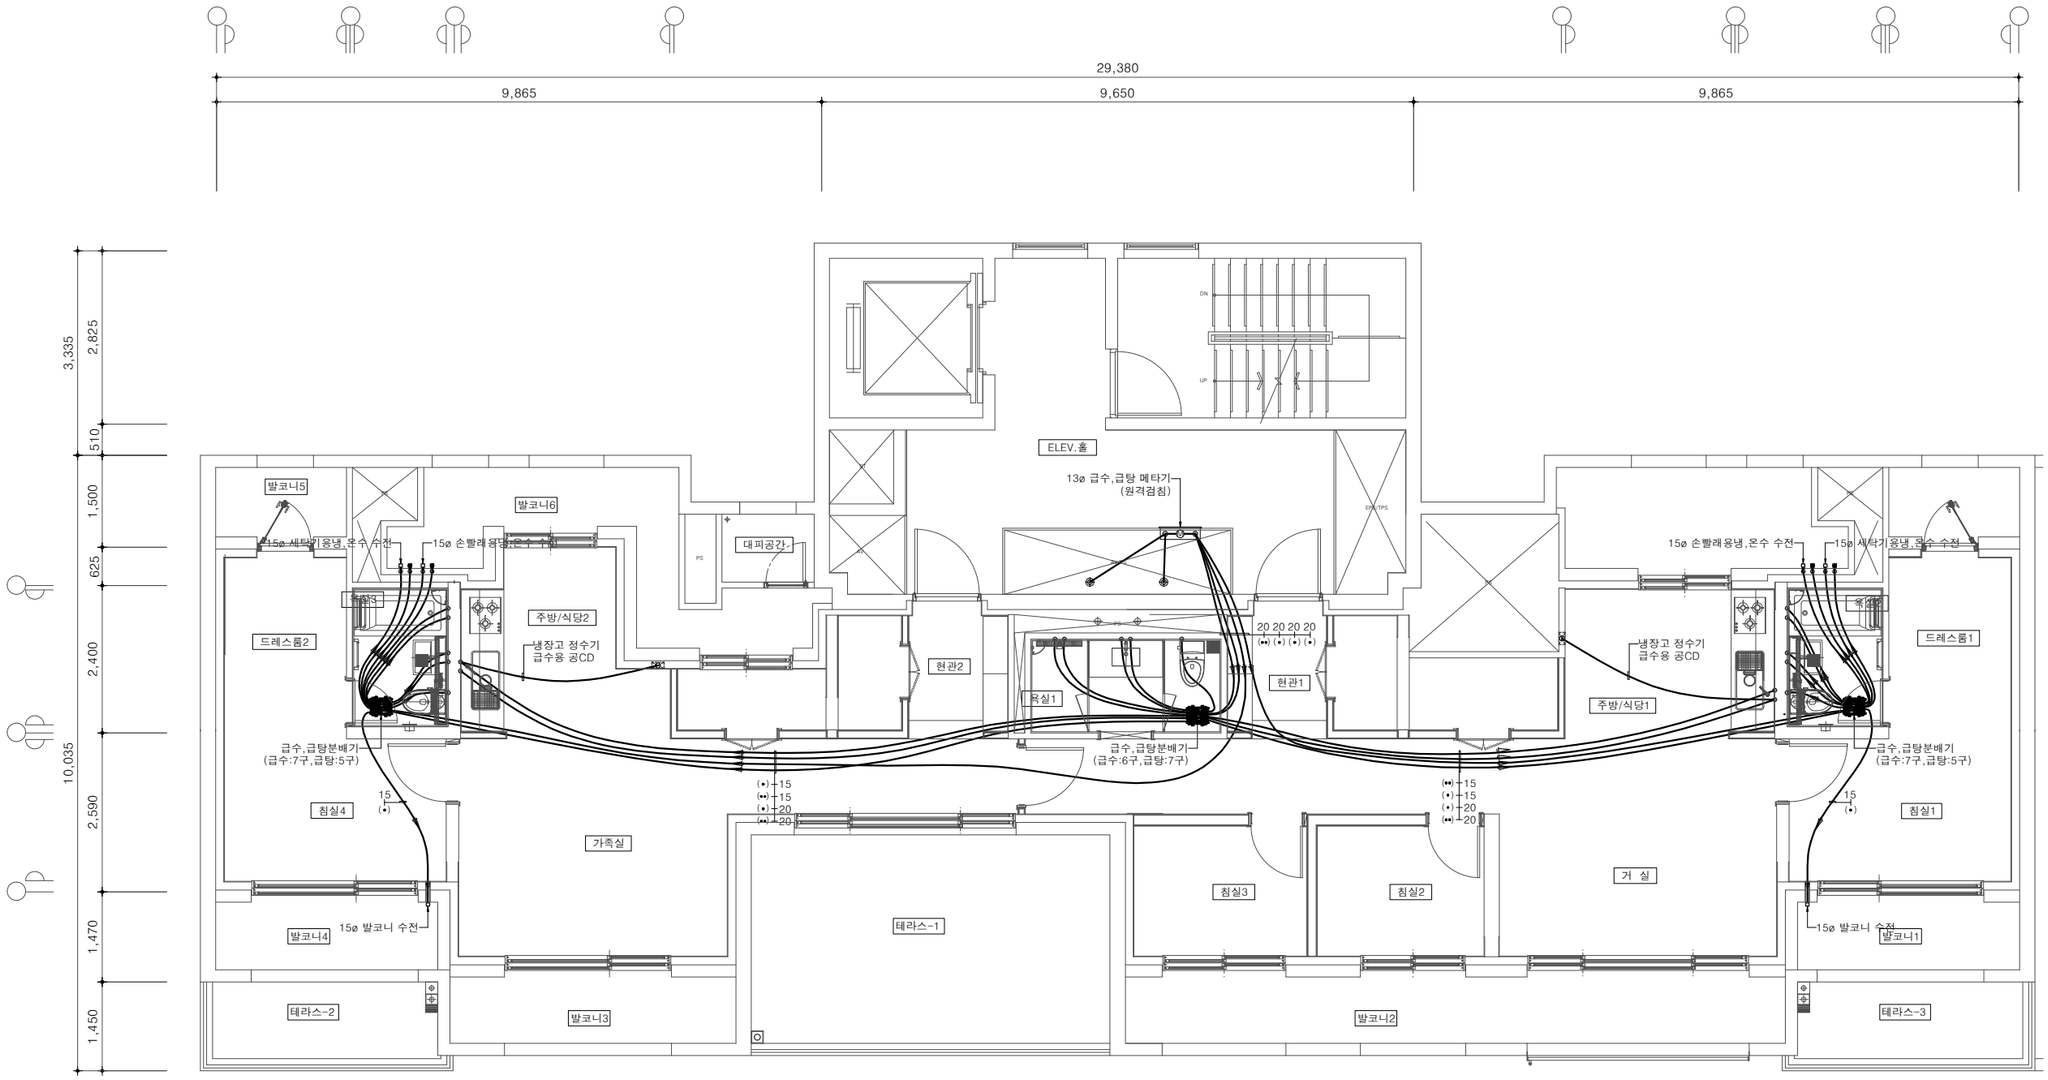

142m²P형 단위세대 급수,급탕배관 평면도(기본형)

축 척 : 1/100

경기주택도시공사
GYEONGGI HOUSING & URBAN DEVELOPMENT CORPORATION

설계명 PROJECT TITLE

화성동탄(2)A76-2BL
민간참여 공동주택사업

주기 NOTE
1. 현장여건에 따라 실시도면은 변경될 수 있다.
2. 세대 감압밸브를 설치해야 한다. (세대 급수압력은 0.245 MPa 이하)
3. 수전 및 배수구는 도서와 건본주택이 상이할 경우 건본주택을 따른다.
4. 급수/급탕배관은 이중관 배관을 적용하며, 급수급탕분배기는 하부층 천장에 설치한다.
5. 센서식 풋밸브 씽크수전 설치

NO	DATE	REVISION DESCRIPTION	APPD

설 계
DESIGN

대표전화

축 척	SCALE
A1	1 / 50
A3	1 / 100


일 자 DATE
2025. 12.

설계번호 PROJECT NO.
AR - 23 - 026

도면화일명 DWG. FILE NAME

도면번호 SHEET NO.
MP - 013

도면명 SUBJECT TITLE
142m²P형 단위세대
급수,급탕배관 평면도(기본형)

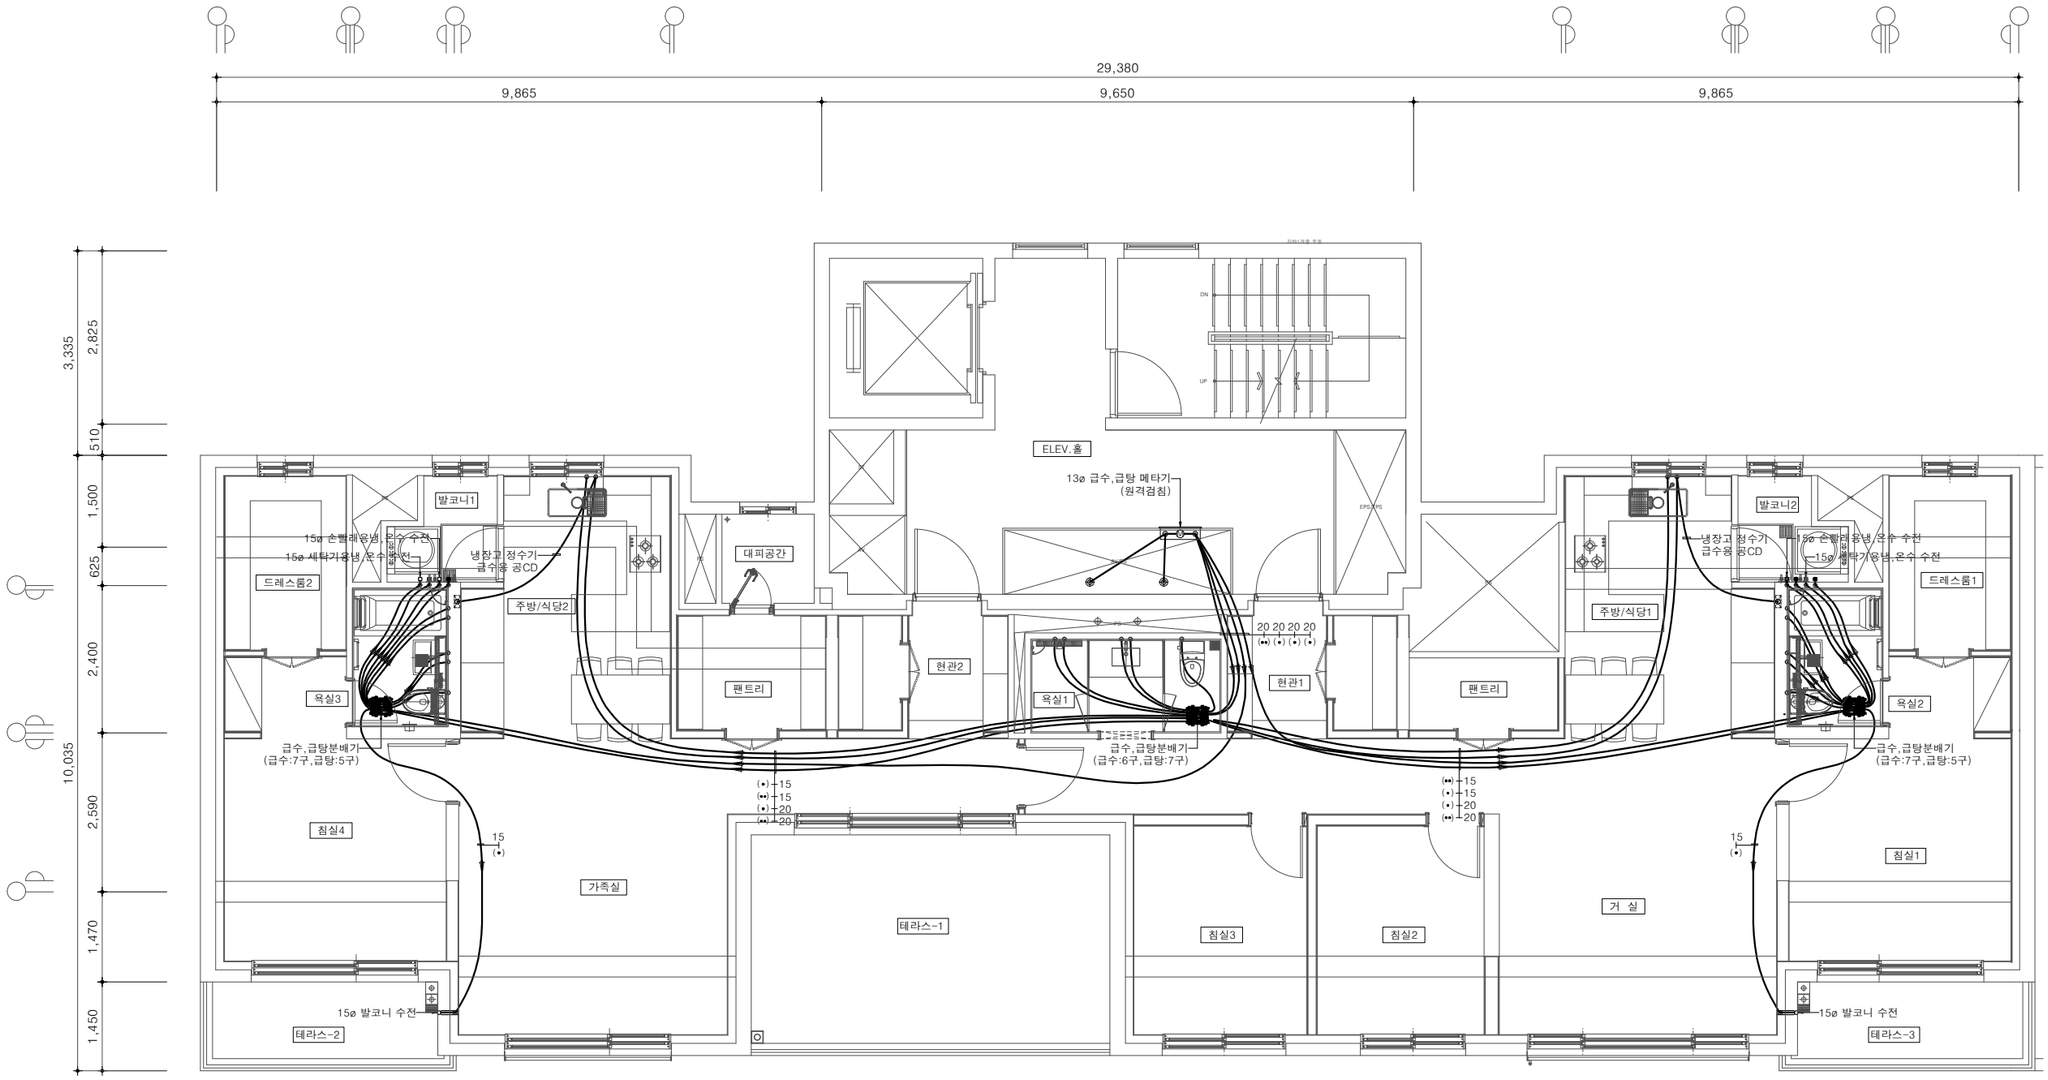

142m²P형 단위세대 급수,급탕배관 평면도(확장형)

축 척 : 1/100

경기주택도시공사
GYEONGGI HOUSING & URBAN DEVELOPMENT CORPORATION

설계명 PROJECT TITLE

화성동탄(2)A76-2BL
민간참여 공동주택사업

주기 NOTE
1. 현장여건에 따라 실시도면은 변경될 수 있다.
2. 세대 감압밸브를 설치해야 한다. (세대 급수압력은 0.245 MPa 이하)
3. 수전 및 배수구는 도서와 건본주택이 상이할 경우 건본주택을 따른다.
4. 급수/급탕배관은 이중관 배관을 적용하며, 급수급탕분배기는 하부층 천장에 설치한다.
5. 센서식 풋밸브 씽크수전 설치

NO	DATE	REVISION DESCRIPTION	APPD

설 계
DESIGN

대표전화

축 척	SCALE
A1	1 / 50
A3	1 / 100


일 자 DATE
2025. 12.

설계번호 PROJECT NO.
AR - 23 - 026

도면화일명 DWG. FILE NAME

도면번호 SHEET NO.
MP - 014

도면명 SUBJECT TITLE
142m²P형 단위세대
급수,급탕배관 평면도(확장형)

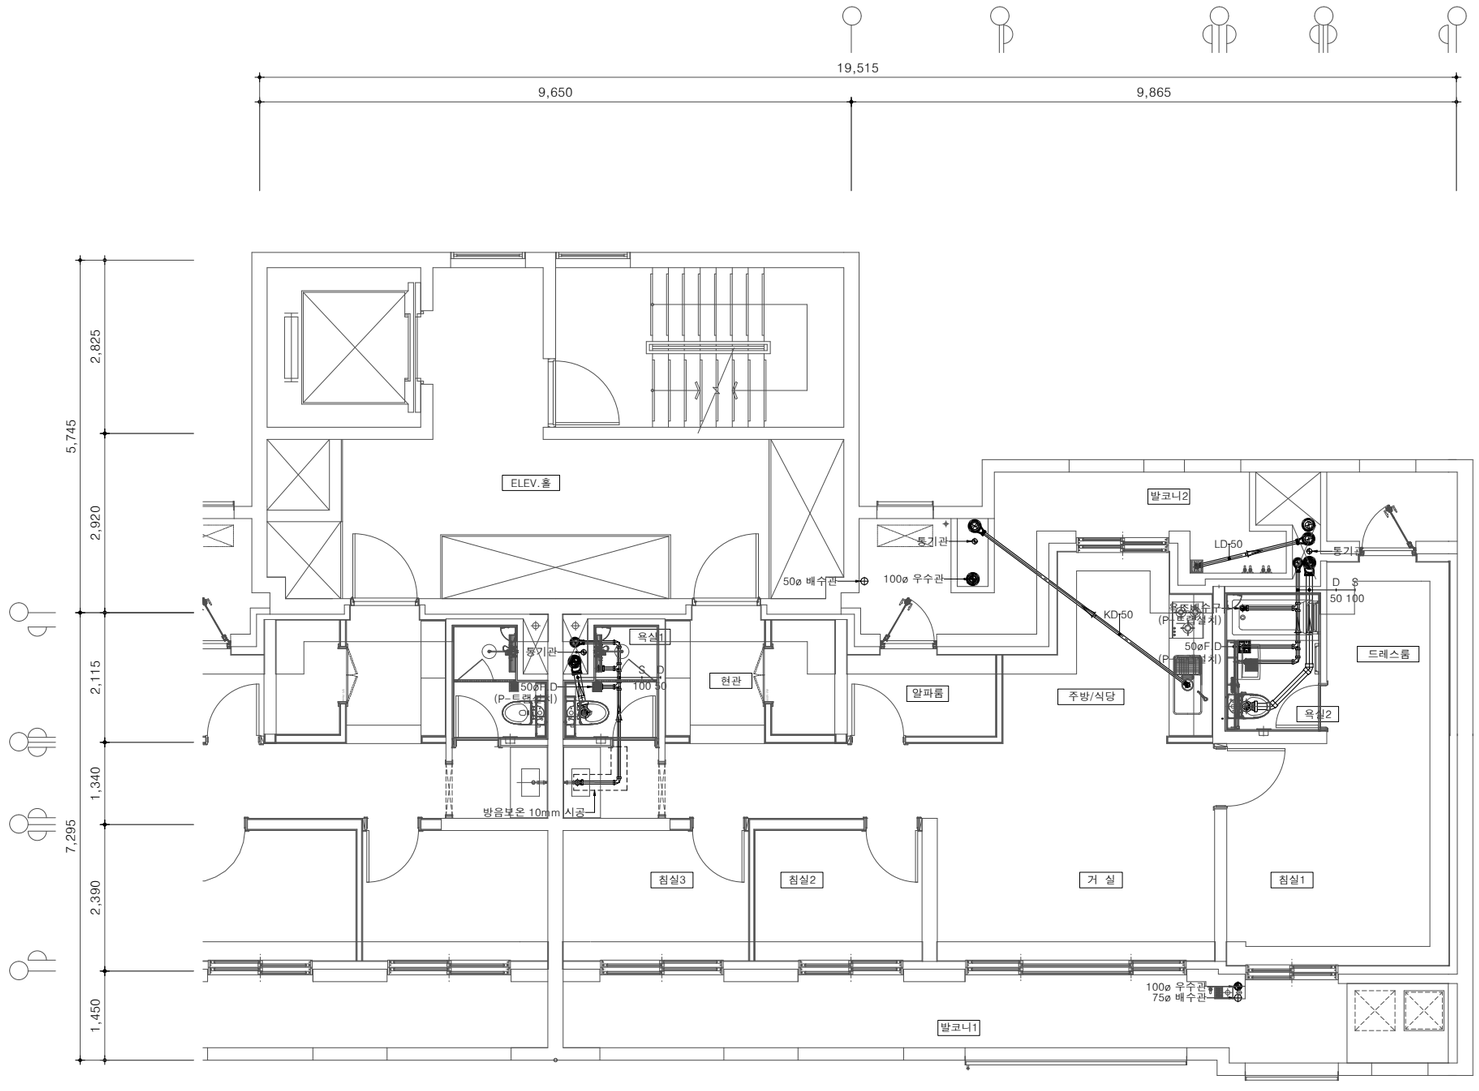

84m²A형 단위세대 오,배수배관 평면도(기본형)

축 척 : 1/100

경기주택도시공사
GYEONGGI HOUSING & URBAN DEVELOPMENT CORPORATION

설계명 PROJECT TITLE

화성동탄(2)A76-2BL
민간참여 공동주택사업

주기 NOTE
1. 현장여건에 따라 실시도면은 변경될 수 있다.
2. 수전 및 배수구는 도서와 건본주택이 상이할 경우 건본주택을 따른다.
3. 욕실 및 다용도실의 오/배수 배관은 하부층 천장에 설치한다.
4. 주방 배관은 당해층 슬라브 상부에 설치한다.
5. 음식물 탈수기 설치

NO	DATE	REVISION DESCRIPTION	APPD
△			
△			
△			
△			

설 계
DESIGN

대표전화

축 척	SCALE
A1	1 / 50
A3	1 / 100


일 자 DATE
2025. 12.

설계번호 PROJECT NO.
AR - 23 - 026

도면화일명 DWG. FILE NAME

도면번호 SHEET NO.
MP – 015

도면명 SUBJECT TITLE
84m²A형 단위세대
오,배수배관 평면도(기본형)

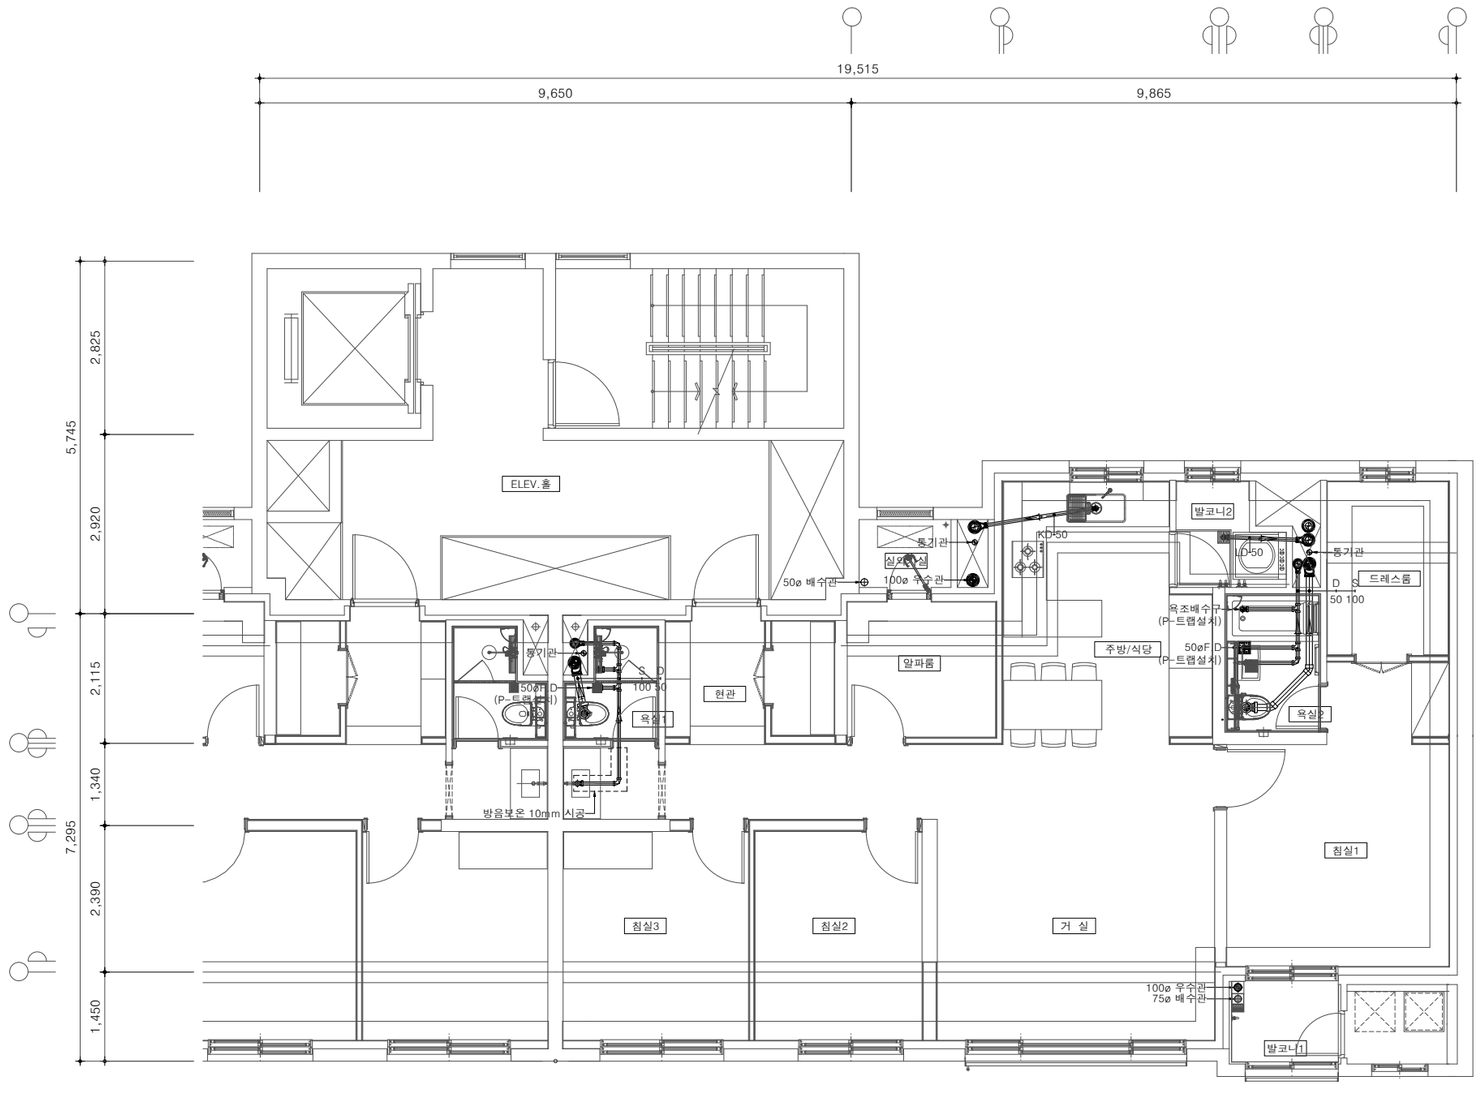

84m²A형 단위세대 오,배수배관 평면도(확장형)

축 척 : 1/100

경기주택도시공사
GYEONGGI HOUSING & URBAN DEVELOPMENT CORPORATION

설계명 PROJECT TITLE

화성동탄(2)A76-2BL
민간참여 공동주택사업


주기 NOTE

1. 현장여건에 따라 실시도면은 변경될 수 있다.
2. 수전 및 배수구는 도서와 건본주택이 상이할 경우 건본주택을 따른다.
3. 욕실 및 다용도실의 오/배수 배관은 하부층 천장에 설치한다.
4. 주방 배관은 당해층 슬라브 상부에 설치한다.
5. 음식물 탈수기 설치

NO	DATE	REVISION DESCRIPTION	APPD
△			
△			
△			
△			

설 계
DESIGN

대표전화	
축 척	SCALE
A1	1 / 50
A3	1 / 100
일 자	DATE
	2025. 12.
설계번호	PROJECT NO.
	AR - 23 - 026
도면화일명	DWG. FILE NAME
도면번호	SHEET NO.
	MP - 016
도면명	SUBJECT TITLE
	84m²A형 단위세대 오,배수배관 평면도(확장형)

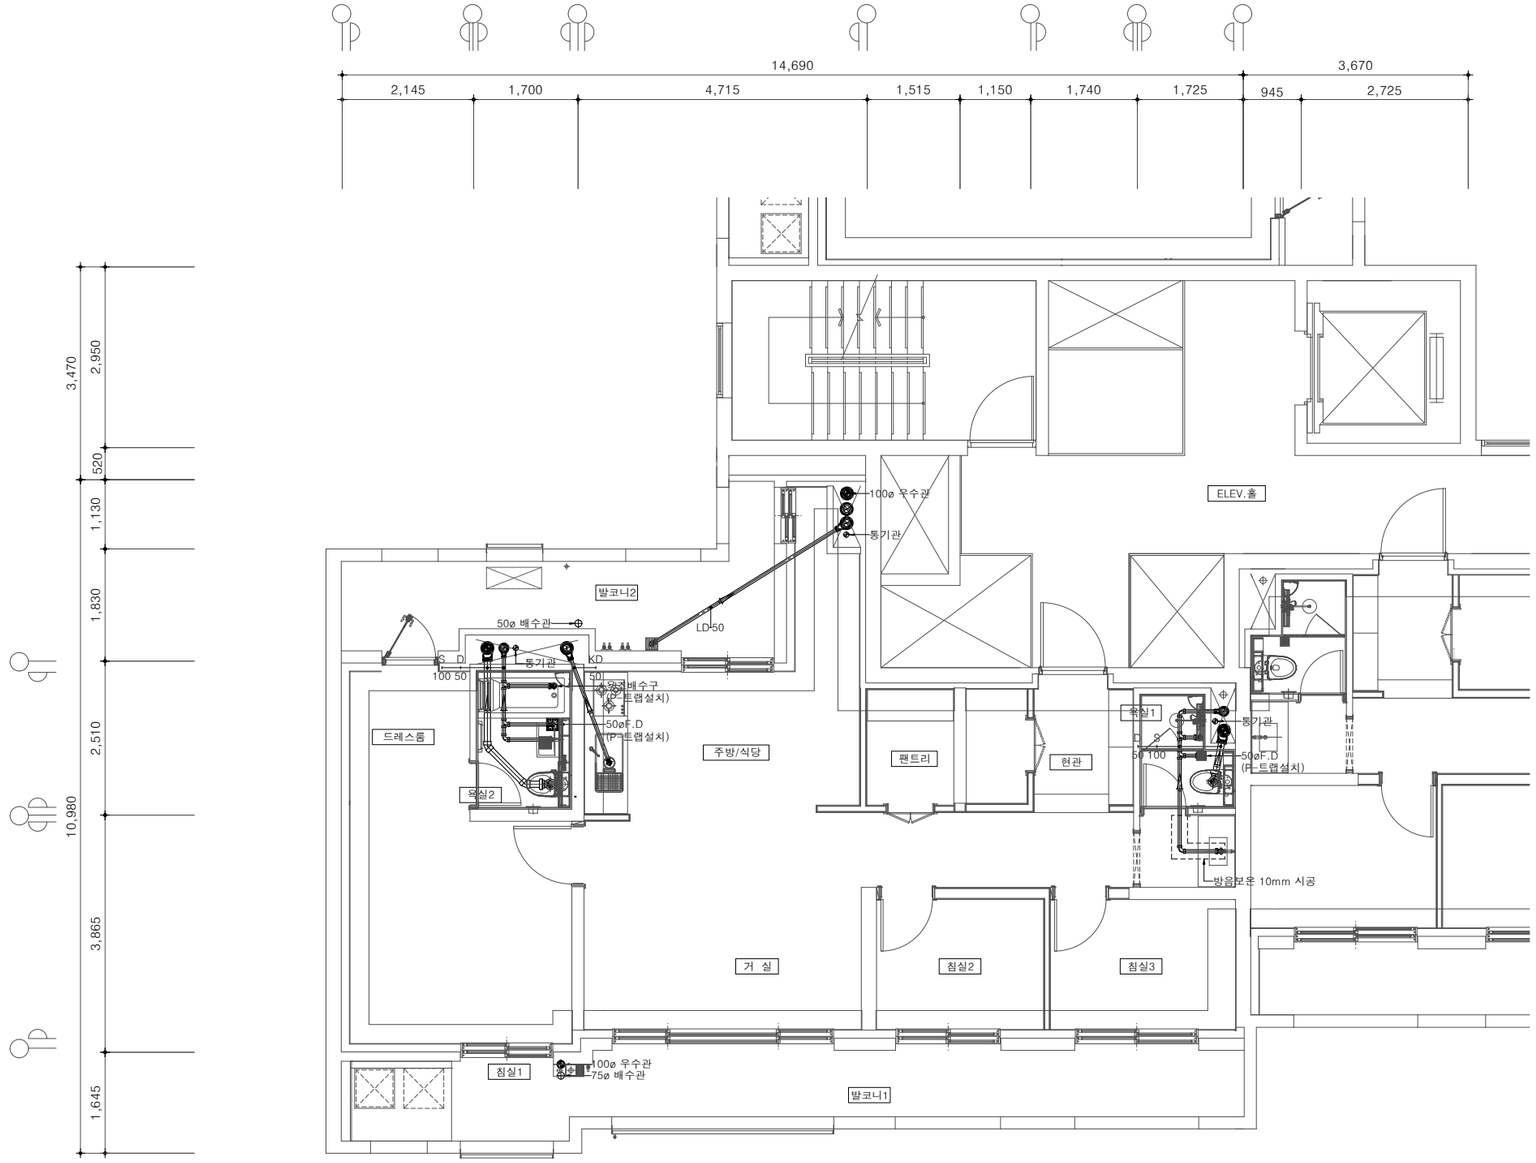

84m²B형 단위세대 오,배수배관 평면도(기본형)

축 척 : 1/100

경기주택도시공사
GYEONGGI HOUSING & URBAN DEVELOPMENT CORPORATION

설계명 PROJECT TITLE

화성동탄(2)A76-2BL
민간참여 공동주택사업

주기 NOTE
1. 현장여건에 따라 실시도면은 변경될 수 있다.
2. 수전 및 배수구는 도서와 건본주택이 상이할 경우 건본주택을 따른다.
3. 욕실 및 다용도실의 오/배수 배관은 하부층 천장에 설치한다.
4. 주방 배관은 당해층 슬라브 상부에 설치한다.
5. 음식물 탈수기 설치

NO	DATE	REVISION DESCRIPTION	APPD

설 계
DESIGN

대표전화

축 척	SCALE
A1	1 / 50
A3	1 / 100


일 자 DATE
2025. 12.

설계번호 PROJECT NO.
AR - 23 - 026

도면화일명 DWG. FILE NAME

도면번호 SHEET NO.
MP – 017

도면명 SUBJECT TITLE
84m²B형 단위세대
오,배수배관 평면도(기본형)

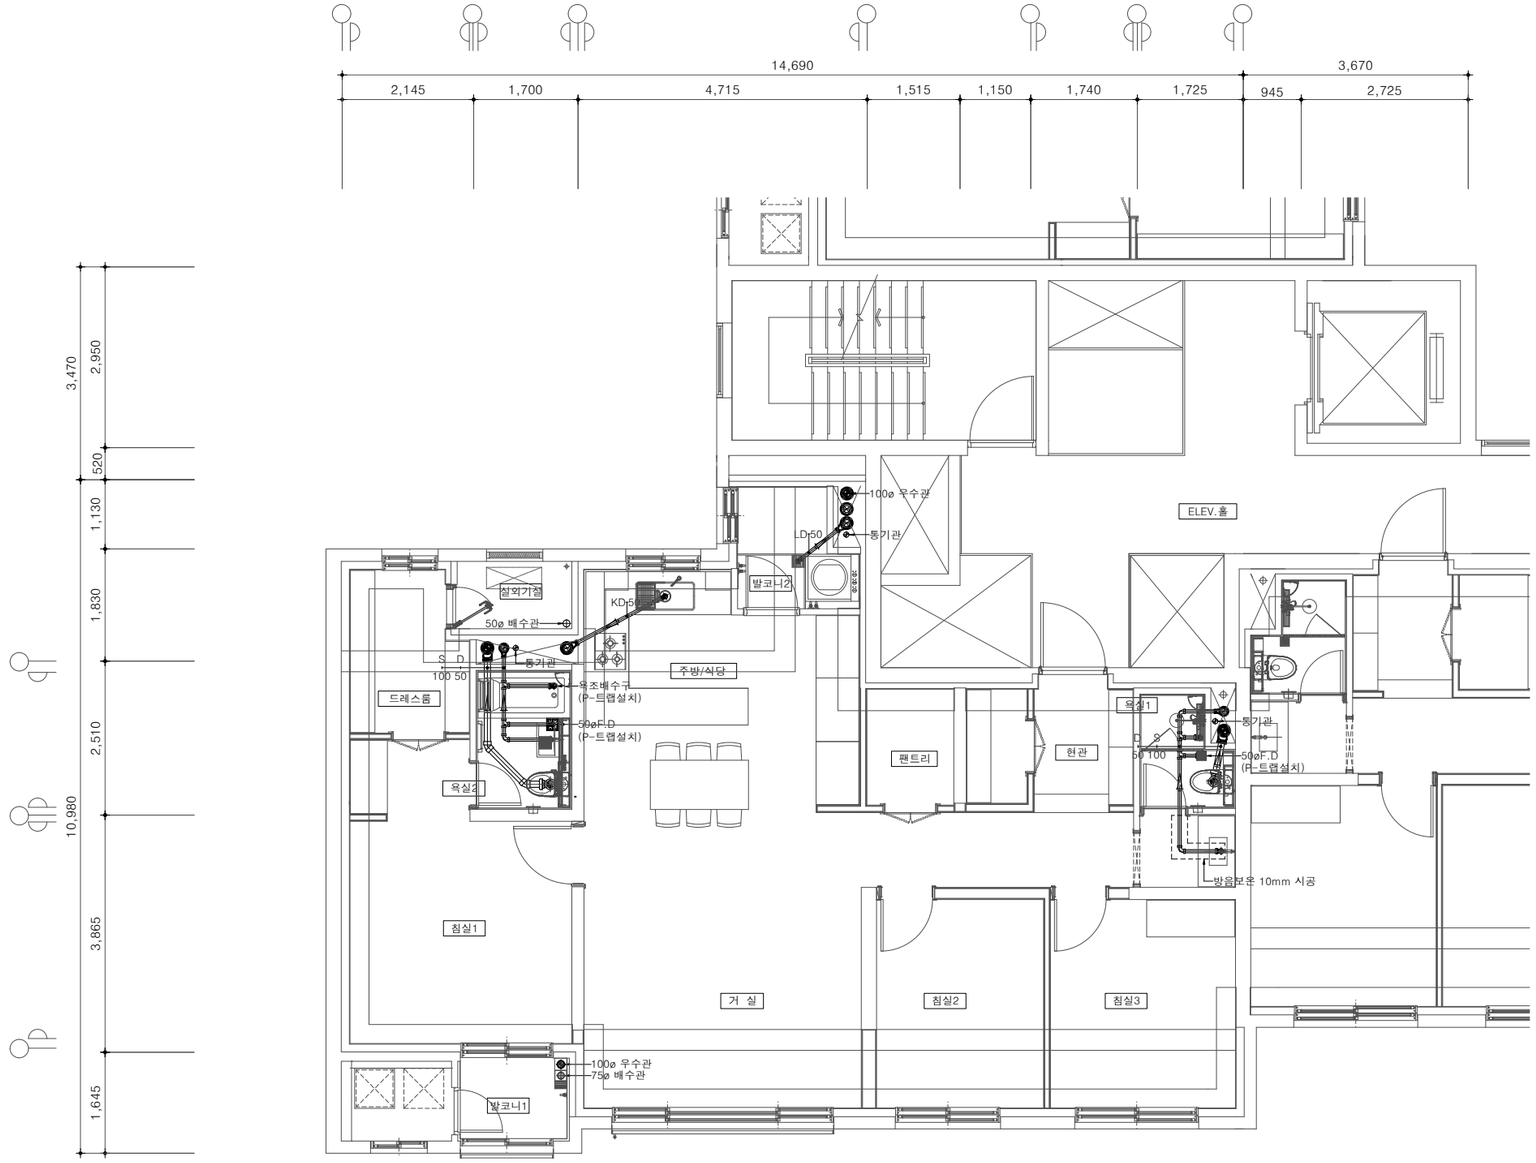

84m²B형 단위세대 오,배수배관 평면도(확장형)

축 척 : 1/100

경기주택도시공사
GYEONGGI HOUSING & URBAN DEVELOPMENT CORPORATION

설계명 PROJECT TITLE

화성동탄(2)A76-2BL
민간참여 공동주택사업

주기 NOTE
1. 현장여건에 따라 실시도면은 변경될 수 있다.
2. 수전 및 배수구는 도서와 건본주택이 상이할 경우 건본주택을 따른다.
3. 욕실 및 다용도실의 오/배수 배관은 하부층 천장에 설치한다.
4. 주방 배관은 당해층 슬라브 상부에 설치한다.
5. 음식물 탈수기 설치

NO	DATE	REVISION DESCRIPTION	APPD

설 계
DESIGN

대표전화

축 척 SCALE	
A1	1 / 50
A3	1 / 100


일 자 DATE
2025. 12.

설계번호 PROJECT NO.
AR - 23 - 026

도면화일명 DWG. FILE NAME

도면번호 SHEET NO.
MP – 018

도면명 SUBJECT TITLE
84m²B형 단위세대
오,배수배관 평면도(확장형)

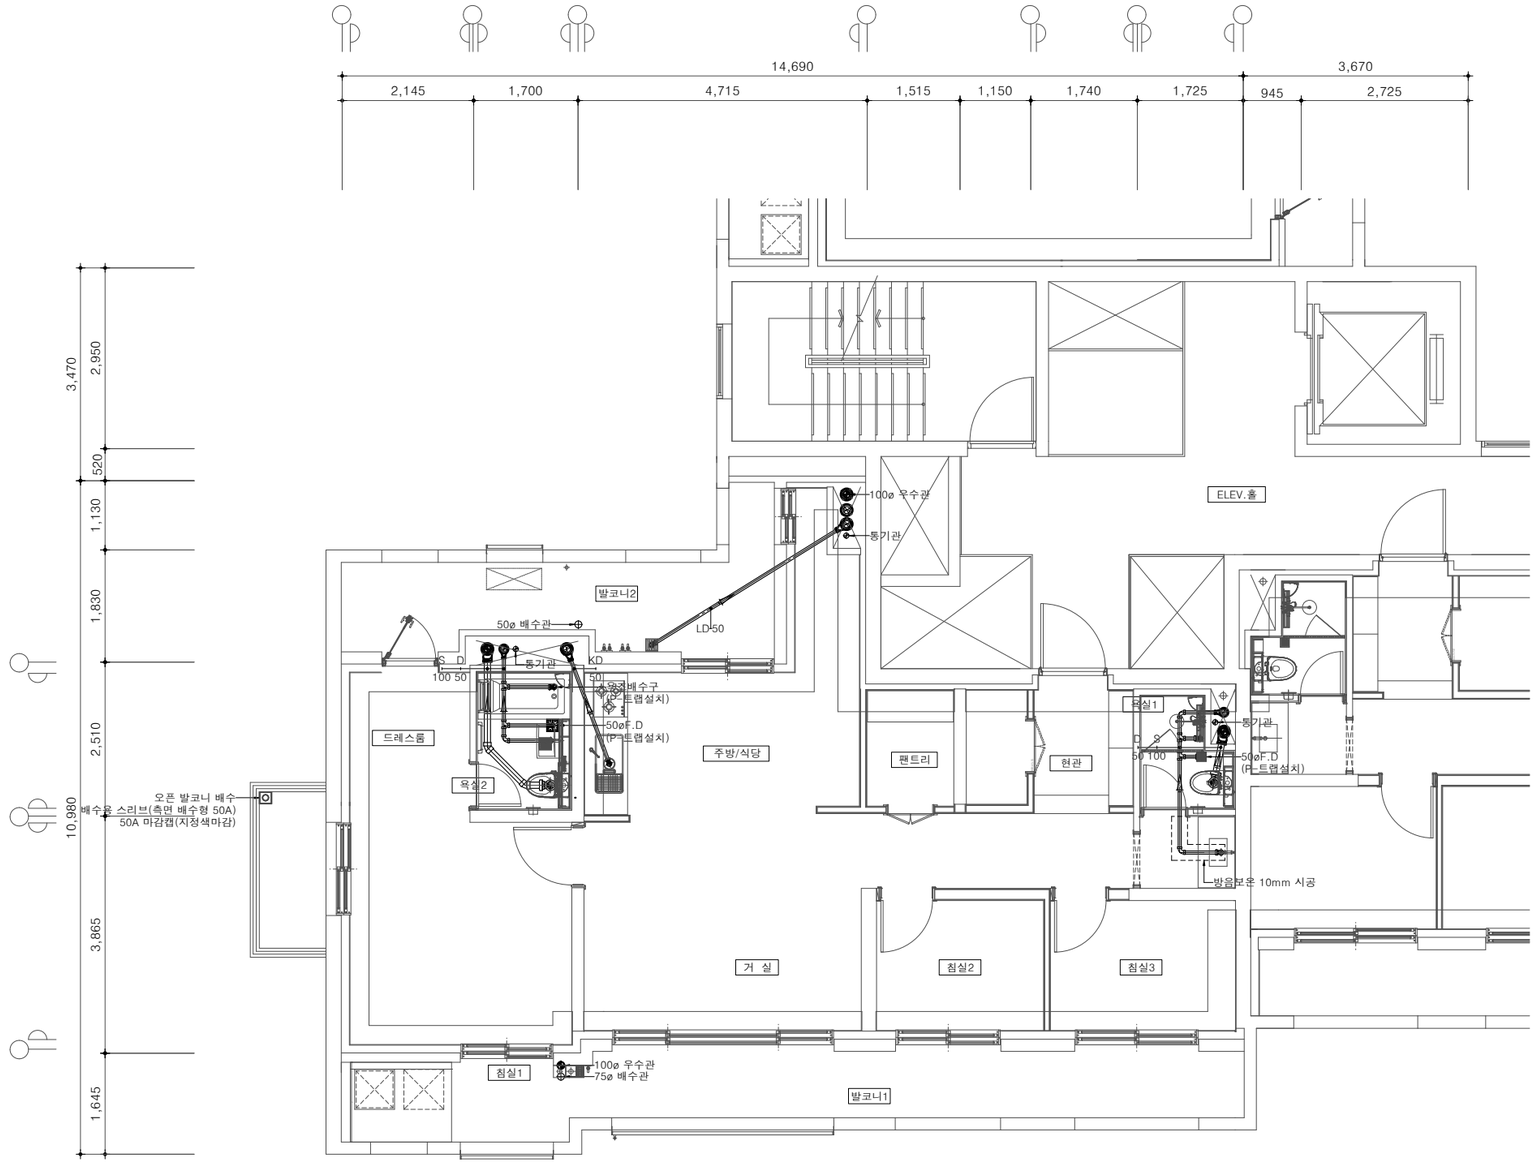

84m²C형 단위세대 오,배수배관 평면도(기본형)

축 척 : 1/100

경기주택도시공사
GYEONGGI HOUSING & URBAN DEVELOPMENT CORPORATION

설계명 PROJECT TITLE

화성동탄(2)A76-2BL
민간참여 공동주택사업

주기 NOTE
1. 현장여건에 따라 실시도면은 변경될 수 있다.
2. 수전 및 배수구는 도서와 건본주택이 상이할 경우 건본주택을 따른다.
3. 욕실 및 다용도실의 오/배수 배관은 하부층 천장에 설치한다.
4. 주방 배관은 당해층 슬라브 상부에 설치한다.
5. 음식물 탈수기 설치

NO	DATE	REVISION DESCRIPTION	APPD
△			
△			
△			
△			

설 계
DESIGN

대표전화

축 척	SCALE
A1	1 / 50
A3	1 / 100


일 자 DATE
2025. 12.

설계번호 PROJECT NO.
AR - 23 - 026

도면화일명 DWG. FILE NAME

도면번호 SHEET NO.
MP – 019

도면명 SUBJECT TITLE
84m²C형 단위세대
오,배수배관 평면도(기본형)

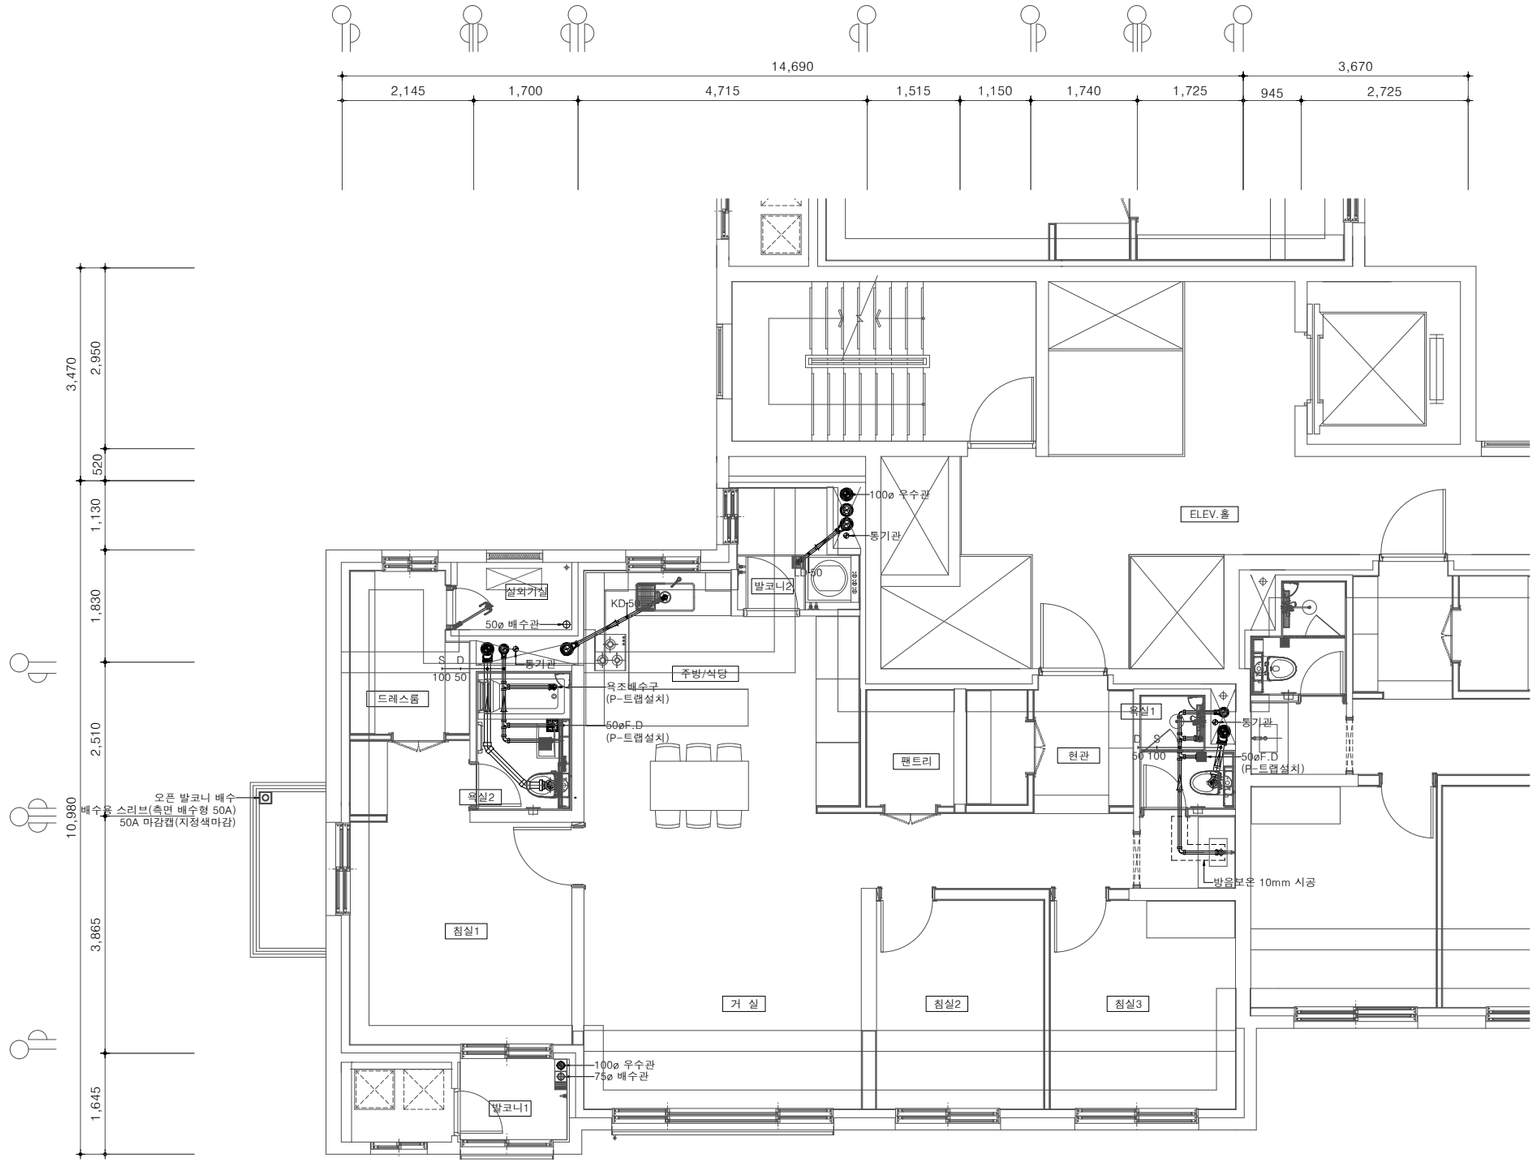

84m²C형 단위세대 오,배수배관 평면도(확장형)

축 척 : 1/100

경기주택도시공사
GYEONGGI HOUSING & URBAN DEVELOPMENT CORPORATION

설계명 PROJECT TITLE


화성동탄(2)A76-2BL
민간참여 공동주택사업

주기 NOTE
1. 현장여건에 따라 실시도면은 변경될 수 있다.
2. 수전 및 배수구는 도서와 건본주택이 상이할 경우 건본주택을 따른다.
3. 욕실 및 다용도실의 오/배수 배관은 하부층 천장에 설치한다.
4. 주방 배관은 당해층 슬라브 상부에 설치한다.
5. 음식물 탈수기 설치

NO	DATE	REVISION DESCRIPTION	APPD
△			
△			
△			
△			

설 계
DESIGN

대표전화	
축 척	SCALE
A1	1 / 50
A3	1 / 100
일 자	DATE
	2025. 12.
설계번호	PROJECT NO.
	AR - 23 - 026
도면화일명	DWG. FILE NAME
도면번호	SHEET NO.
	MP - 020
도면명	SUBJECT TITLE
	84m²C형 단위세대 오,배수배관 평면도(확장형)

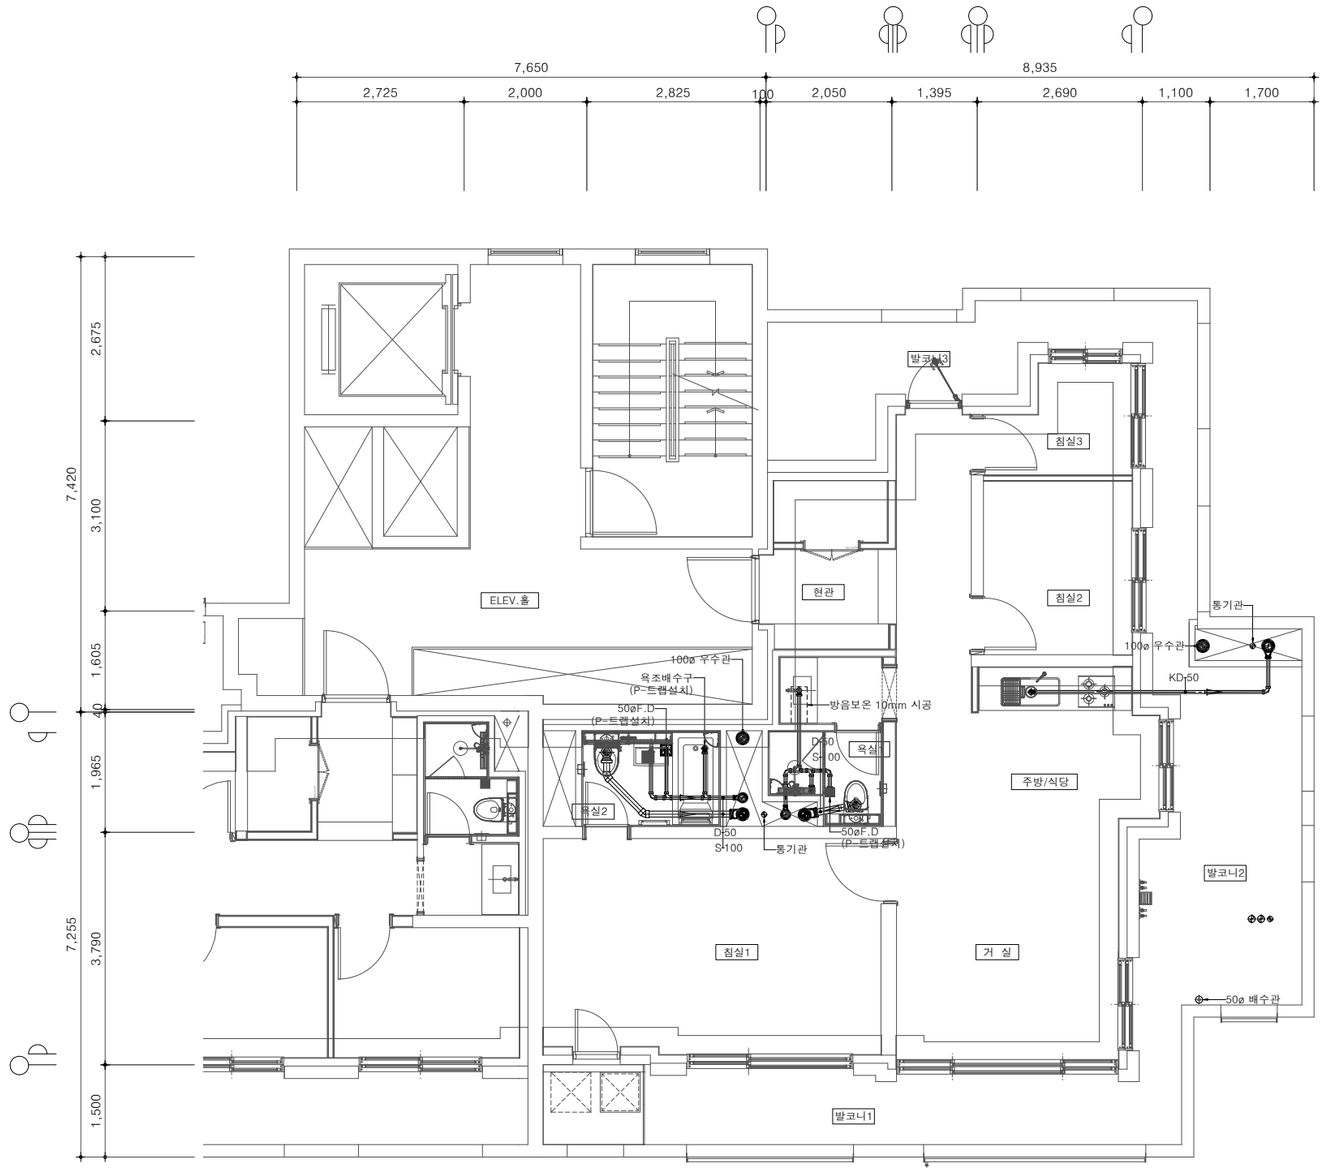

84m²D형 단위세대 오,배수배관 평면도(기본형)

축 척 : 1/100

경기주택도시공사
GYEONGGI HOUSING & URBAN DEVELOPMENT CORPORATION

설계명 PROJECT TITLE


화성동탄(2)A76-2BL
민간참여 공동주택사업

주기 NOTE
1. 현장여건에 따라 실시도면은 변경될 수 있다.
2. 수전 및 배수구는 도서와 건본주택이 상이할 경우 건본주택을 따른다.
3. 욕실 및 다용도실의 오/배수 배관은 하부층 천장에 설치한다.
4. 주방 배관은 당해층 슬라브 상부에 설치한다.
5. 음식물 탈수기 설치

NO	DATE	REVISION DESCRIPTION	APPD

설 계
DESIGN

대표전화	
축 척	SCALE
A1	1 / 50
A3	1 / 100
일 자	DATE
	2025. 12.
설계번호	PROJECT NO.
	AR - 23 - 026
도면화일명	DWG. FILE NAME
도면번호	SHEET NO.
	MP - 021
도면명	SUBJECT TITLE
	84m²D형 단위세대 오,배수배관 평면도(기본형)

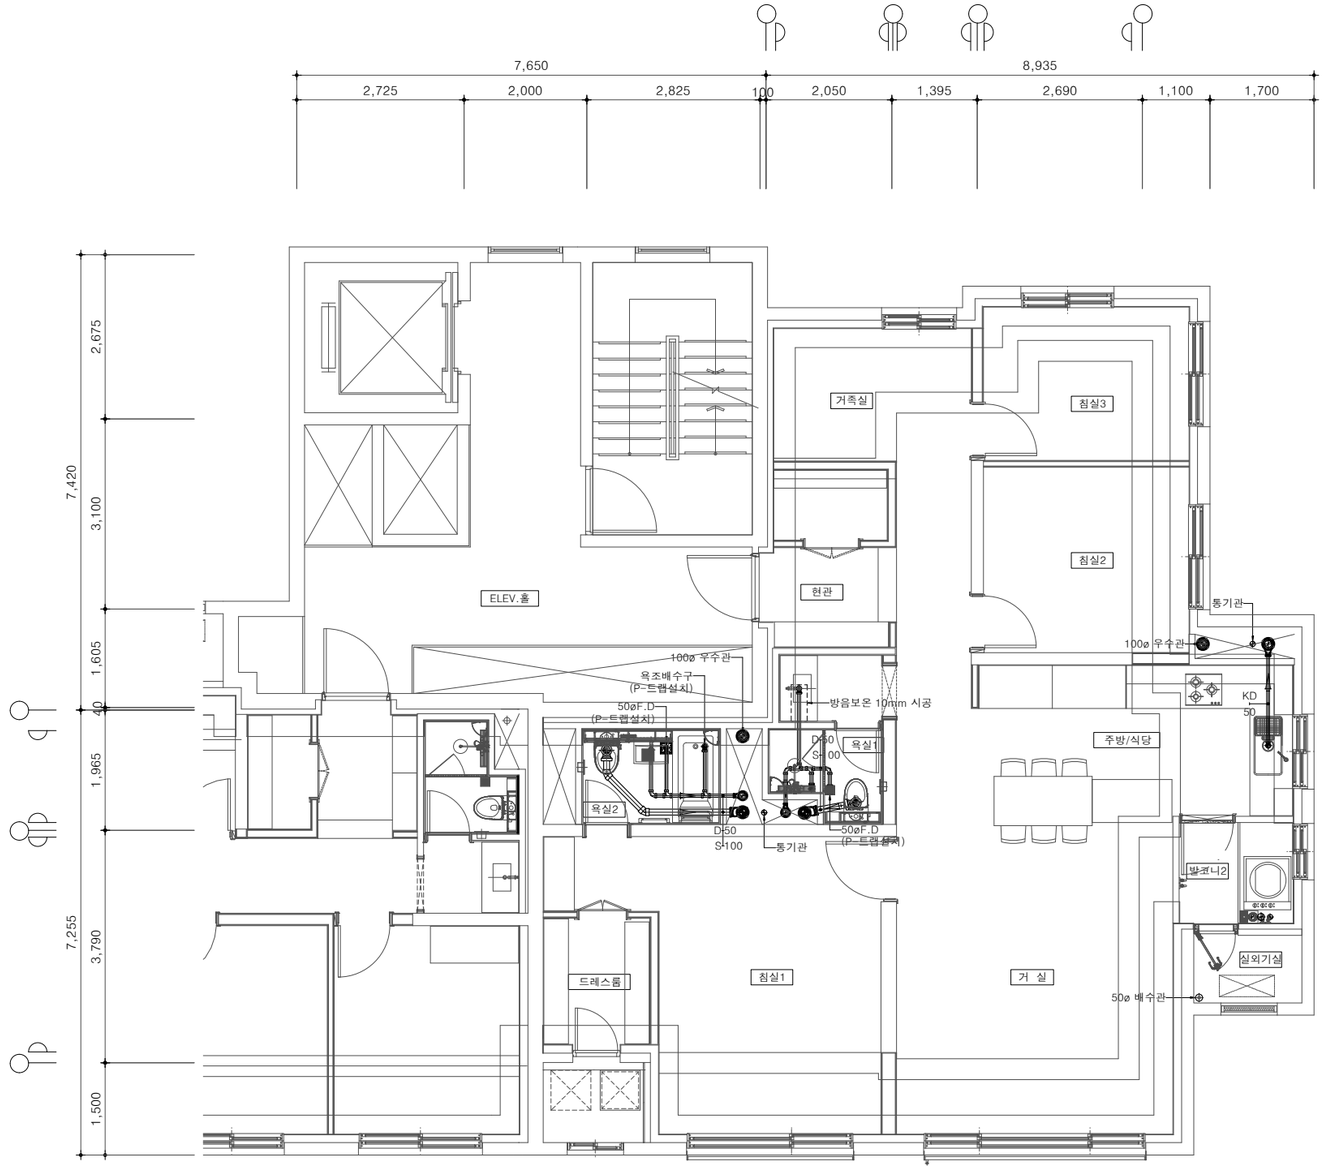

84m²D형 단위세대 오,배수배관 평면도(확장형)

축 척 : 1/100

경기주택도시공사
GYEONGGI HOUSING & URBAN DEVELOPMENT CORPORATION

설계명 PROJECT TITLE


화성동탄(2)A76-2BL
민간참여 공동주택사업

주기 NOTE
1. 현장여건에 따라 실시도면은 변경될 수 있다.
2. 수전 및 배수구는 도서와 건본주택이 상이할 경우 건본주택을 따른다.
3. 욕실 및 다용도실의 오/배수 배관은 하부층 천장에 설치한다.
4. 주방 배관은 당해층 슬라브 상부에 설치한다.
5. 음식물 탈수기 설치

NO	DATE	REVISION DESCRIPTION	APPD
△			
△			
△			
△			

설 계
DESIGN

대표전화	
축 척	SCALE
A1	1 / 50
A3	1 / 100
일 자	DATE
	2025. 12.
설계번호	PROJECT NO.
	AR - 23 - 026
도면화일명	DWG. FILE NAME
도면번호	SHEET NO.
	MP - 022
도면명	SUBJECT TITLE
	84m²D형 단위세대 오,배수배관 평면도(확장형)

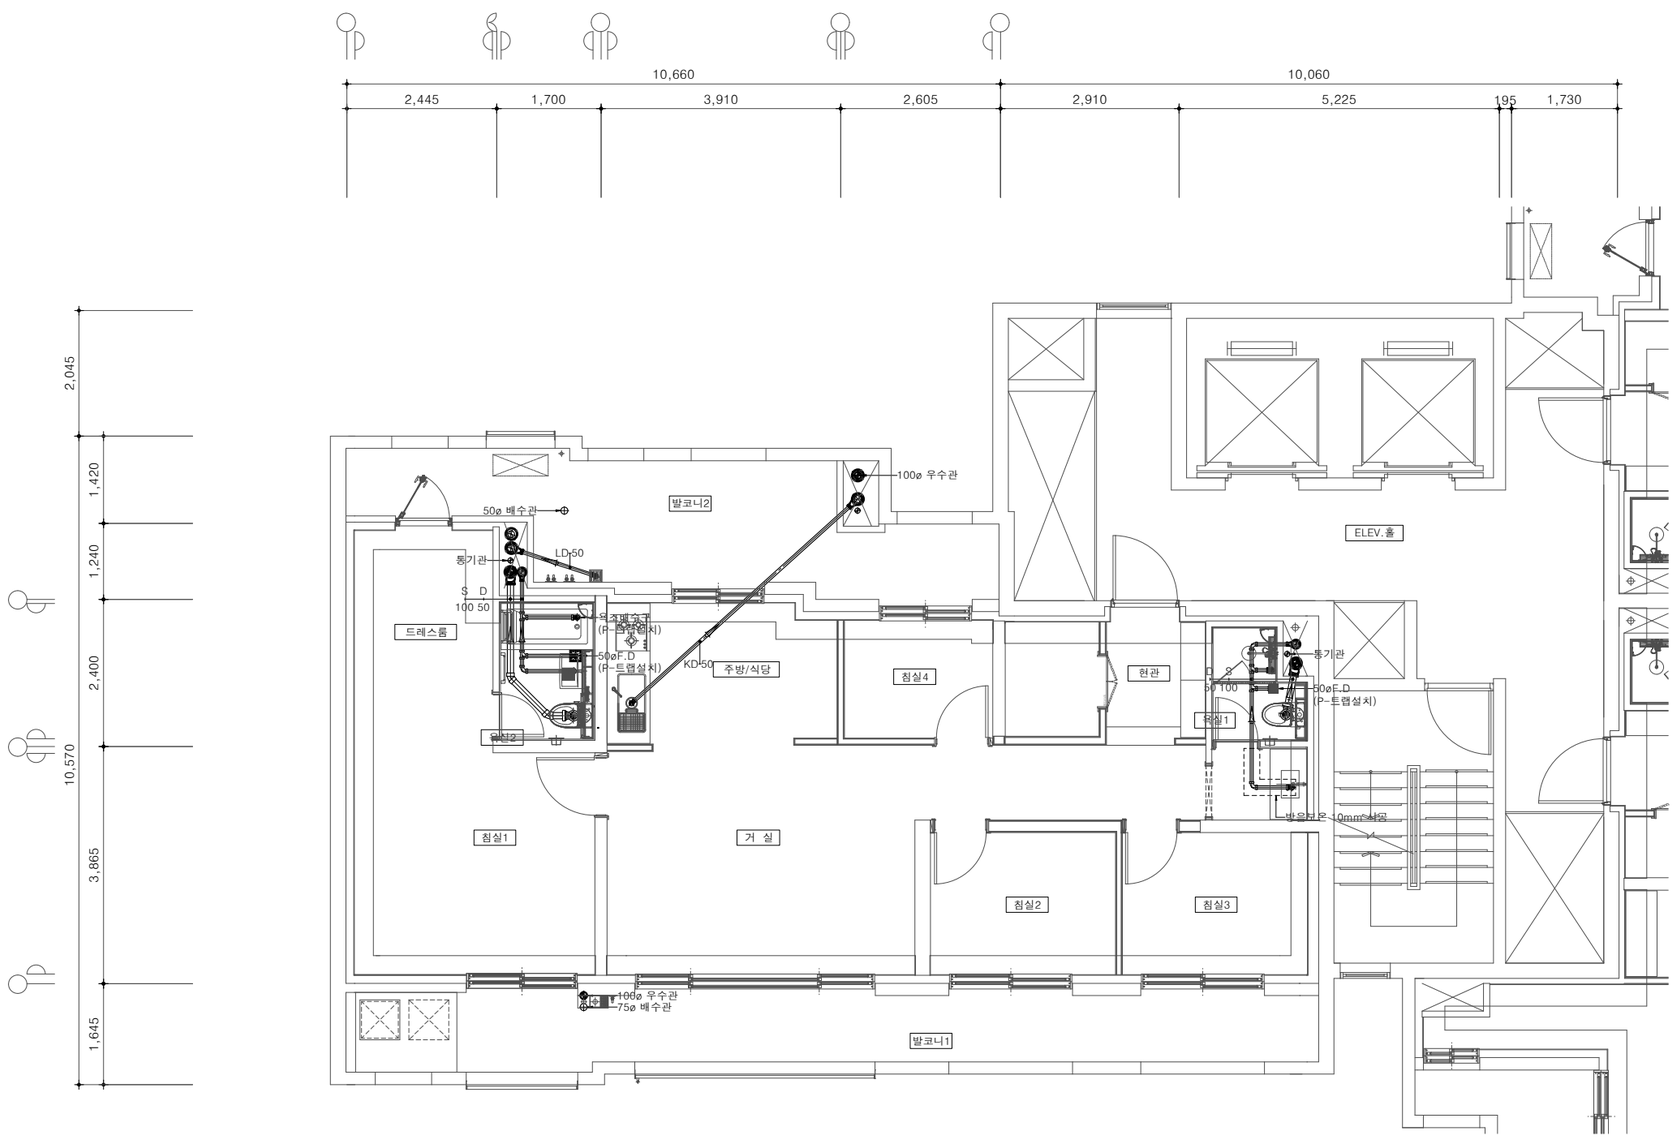

97m²A형 단위세대 오,배수배관 평면도(기본형)

축 척 : 1/100

경기주택도시공사

설계명 PROJECT TITLE


화성동탄(2)A76-2BL
민간참여 공동주택사업

주기 NOTE
1. 현장여건에 따라 실시도면은 변경될 수 있다.
2. 수전 및 배수구는 도서와 건본주택이 상이할 경우 건본주택을 따른다.
3. 욕실 및 다용도실의 오/배수 배관은 하부층 천장에 설치한다.
4. 주방 배관은 당해층 슬라브 상부에 설치한다.
5. 음식물 탈수기 설치

NO	DATE	REVISION DESCRIPTION	APPD

설 계
DESIGN

대표전화	
축 척	SCALE
A1	1 / 50
A3	1 / 100
일 자	DATE
	2025. 12.
설계번호	PROJECT NO.
	AR - 23 - 026
도면화일명	DWG. FILE NAME
도면번호	SHEET NO.
	MP - 023
도면명	SUBJECT TITLE
	97m²A형 단위세대 오,배수배관 평면도(기본형)

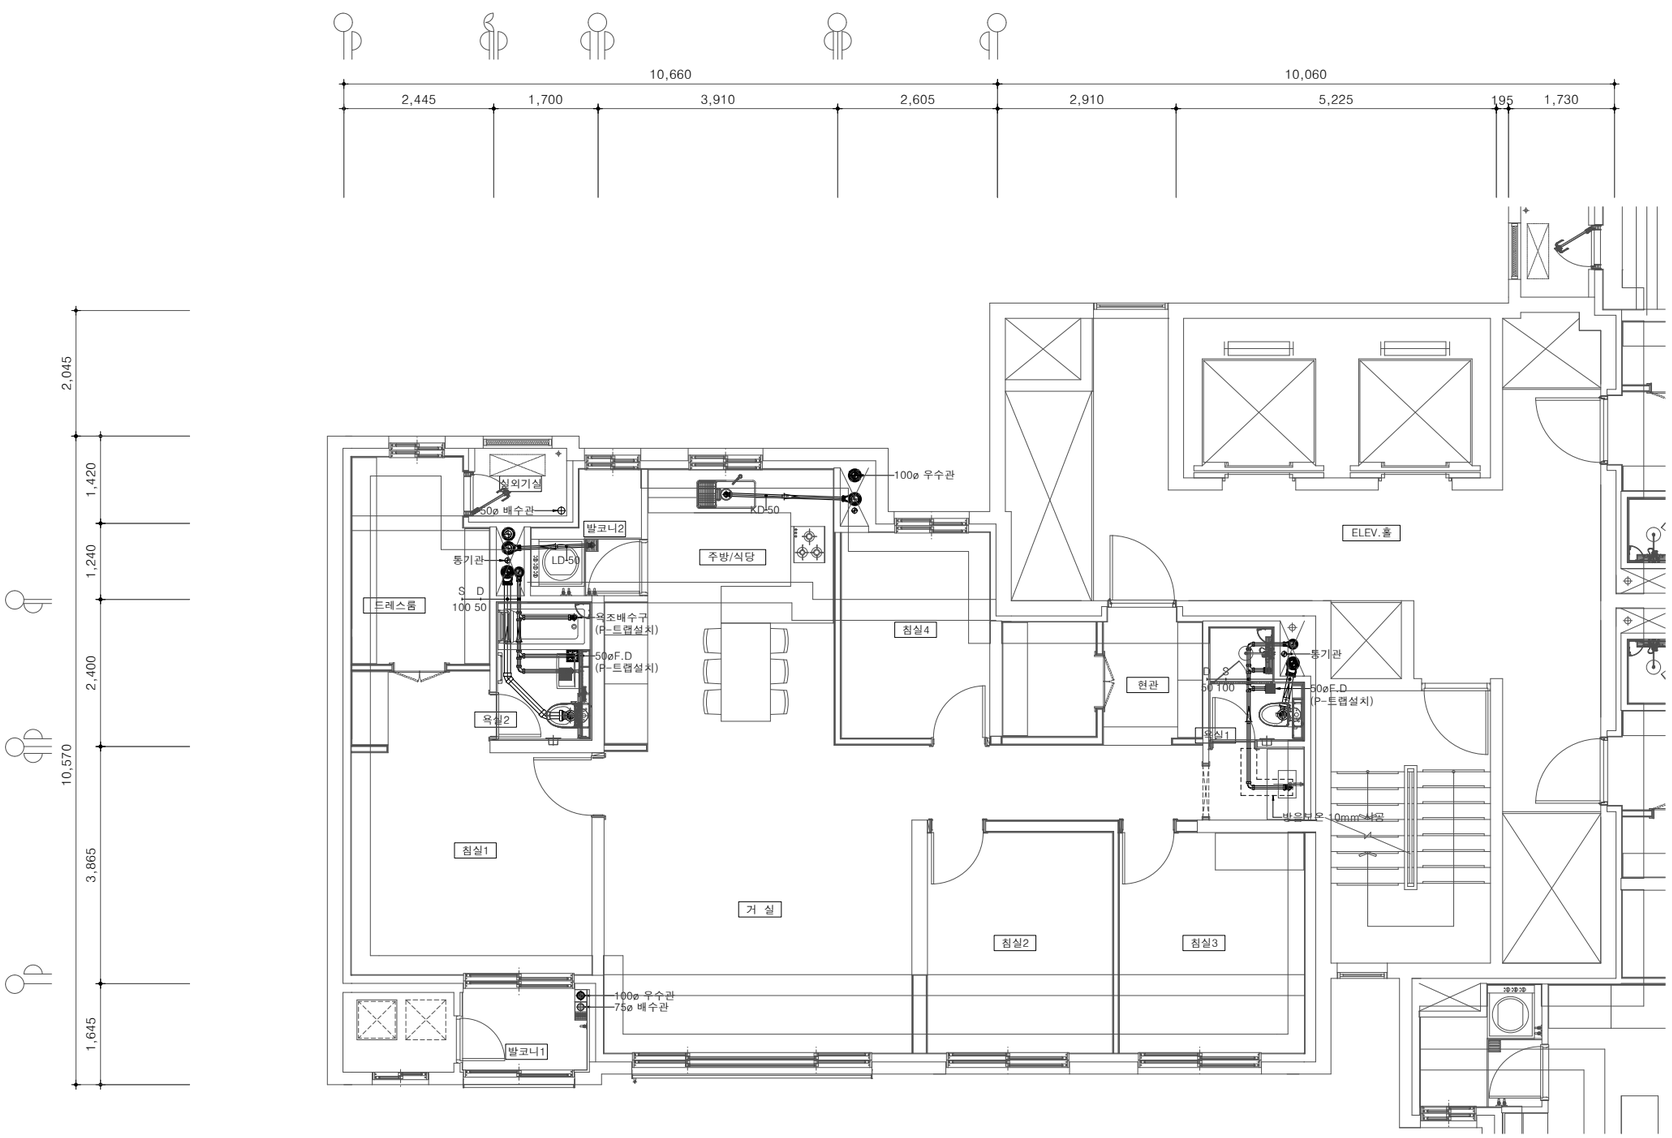

97m²A형 단위세대 오,배수배관 평면도(확장형)

축 척 : 1/100

경기주택도시공사
GYEONGGI HOUSING & URBAN DEVELOPMENT CORPORATION

설계명 PROJECT TITLE


화성동탄(2)A76-2BL
민간참여 공동주택사업

주기 NOTE
1. 현장여건에 따라 실시도면은 변경될 수 있다.
2. 수전 및 배수구는 도서와 건본주택이 상이할 경우 건본주택을 따른다.
3. 욕실 및 다용도실의 오/배수 배관은 하부층 천장에 설치한다.
4. 주방 배관은 당해층 슬라브 상부에 설치한다.
5. 음식물 탈수기 설치

NO	DATE	REVISION DESCRIPTION	APPD

설 계
DESIGN

대표전화	
축 척	SCALE
A1	1 / 50
A3	1 / 100
일 자	DATE
	2025. 12.
설계번호	PROJECT NO.
	AR - 23 - 026
도면화일명	DWG. FILE NAME
도면번호	SHEET NO.
	MP - 024
도면명	SUBJECT TITLE
	97m²A형 단위세대 오,배수배관 평면도(확장형)

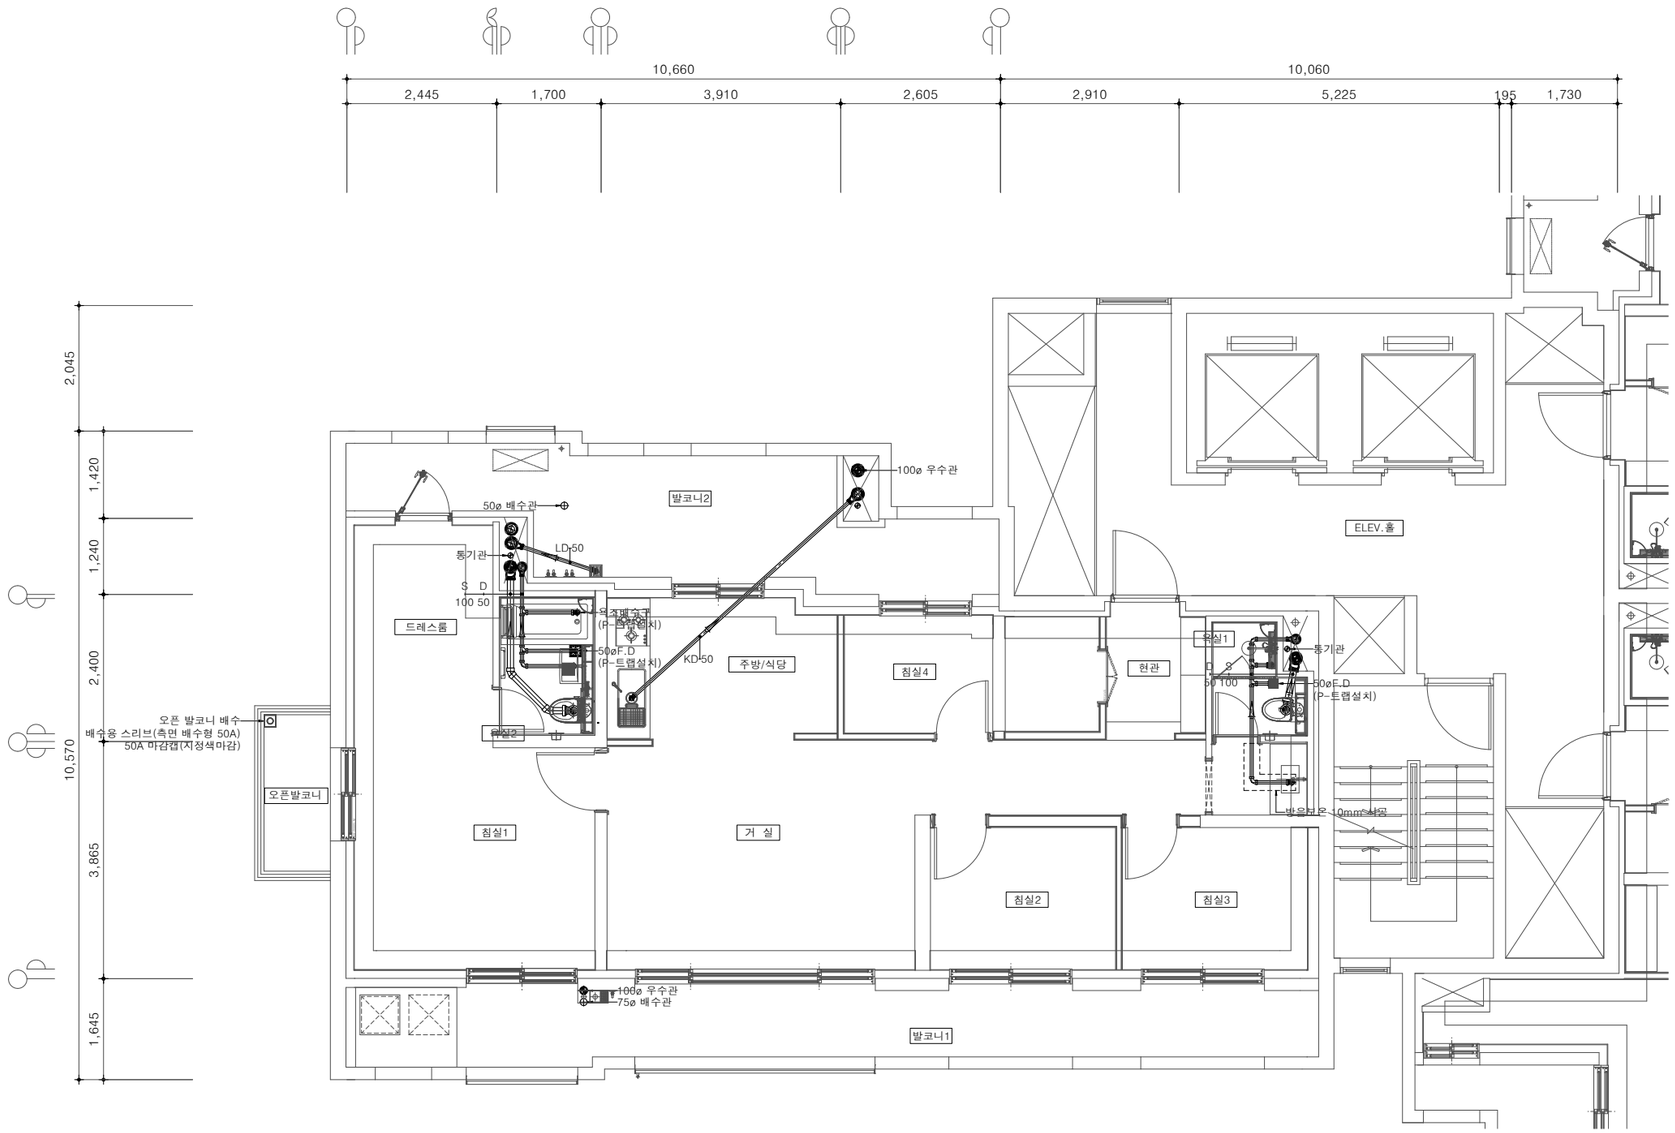

97m²B형 단위세대 오,배수배관 평면도(기본형)

축 척 : 1/100

경기주택도시공사
GYEONGGI HOUSING & URBAN DEVELOPMENT CORPORATION

설계명 PROJECT TITLE

화성동탄(2)A76-2BL 민간참여 공동주택사업


주기 NOTE

1. 현장여건에 따라 실시도면은 변경될 수 있다.
2. 수전 및 배수구는 도서와 건본주택이 상이할 경우 건본주택을 따른다.
3. 욕실 및 다용도실의 오/배수 배관은 하부층 천장에 설치한다.
4. 주방 배관은 당해층 슬라브 상부에 설치한다.
5. 음식물 탈수기 설치

NO	DATE	REVISION DESCRIPTION	APPD

설 계
DESIGN

대표전화	
축 척	SCALE
A1	1 / 50
A3	1 / 100
일 자	DATE
	2025. 12.
설계번호	PROJECT NO.
	AR - 23 - 026
도면화일명	DWG. FILE NAME
도면번호	SHEET NO.
	MP - 025
도면명	SUBJECT TITLE
	97m²B형 단위세대 오,배수배관 평면도(기본형)

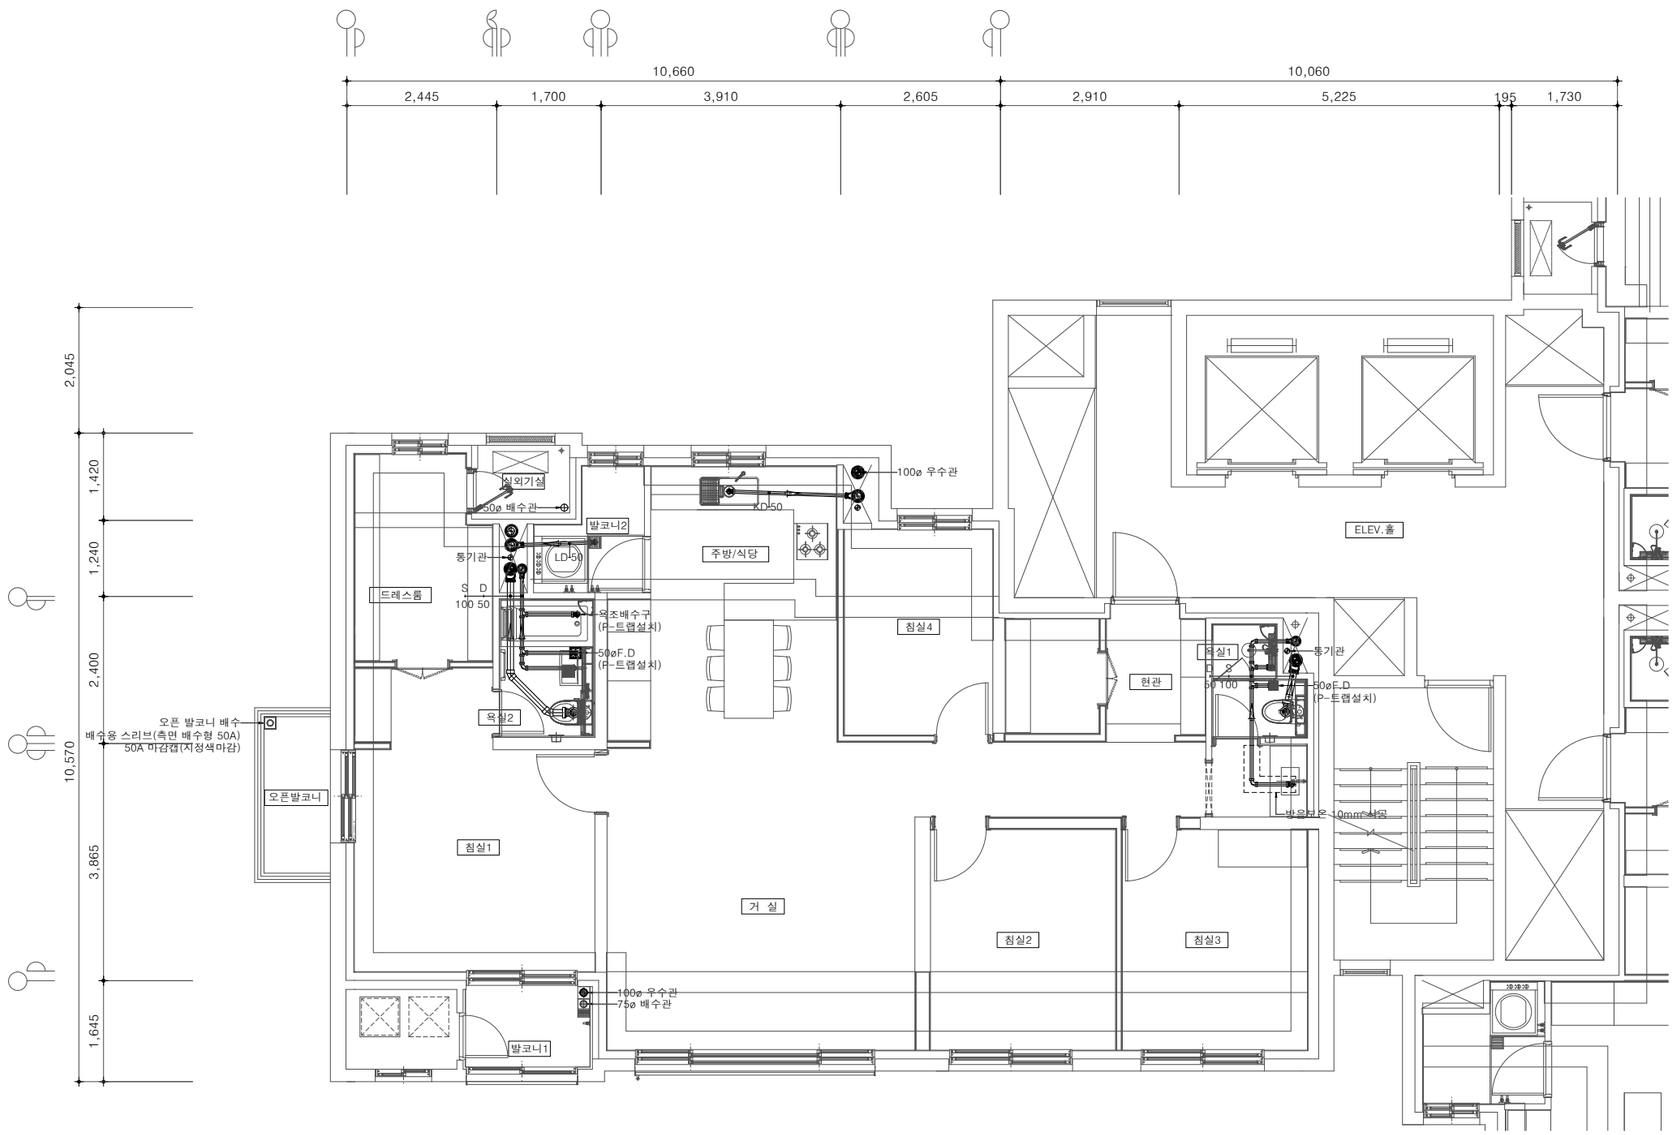

97m²B형 단위세대 오,배수배관 평면도(확장형)

축 척 : 1/100

경기주택도시공사
GYEONGGI HOUSING & URBAN DEVELOPMENT CORPORATION

설계명 PROJECT TITLE


화성동탄(2)A76-2BL
민간참여 공동주택사업

주기 NOTE
1. 현장여건에 따라 실시도면은 변경될 수 있다.
2. 수전 및 배수구는 도서와 건본주택이 상이할 경우 건본주택을 따른다.
3. 욕실 및 다용도실의 오/배수 배관은 하부층 천장에 설치한다.
4. 주방 배관은 당해층 슬라브 상부에 설치한다.
5. 음식물 탈수기 설치

NO	DATE	REVISION DESCRIPTION	APPD

설 계
DESIGN

대표전화	
축 척	SCALE
A1	1 / 50
A3	1 / 100
일 자 DATE	2025. 12.
설계번호 PROJECT NO.	AR - 23 - 026
도면화일명 DWG. FILE NAME	
도면번호 SHEET NO.	MP - 026
도면명 SUBJECT TITLE	97m²B형 단위세대 오,배수배관 평면도(확장형)

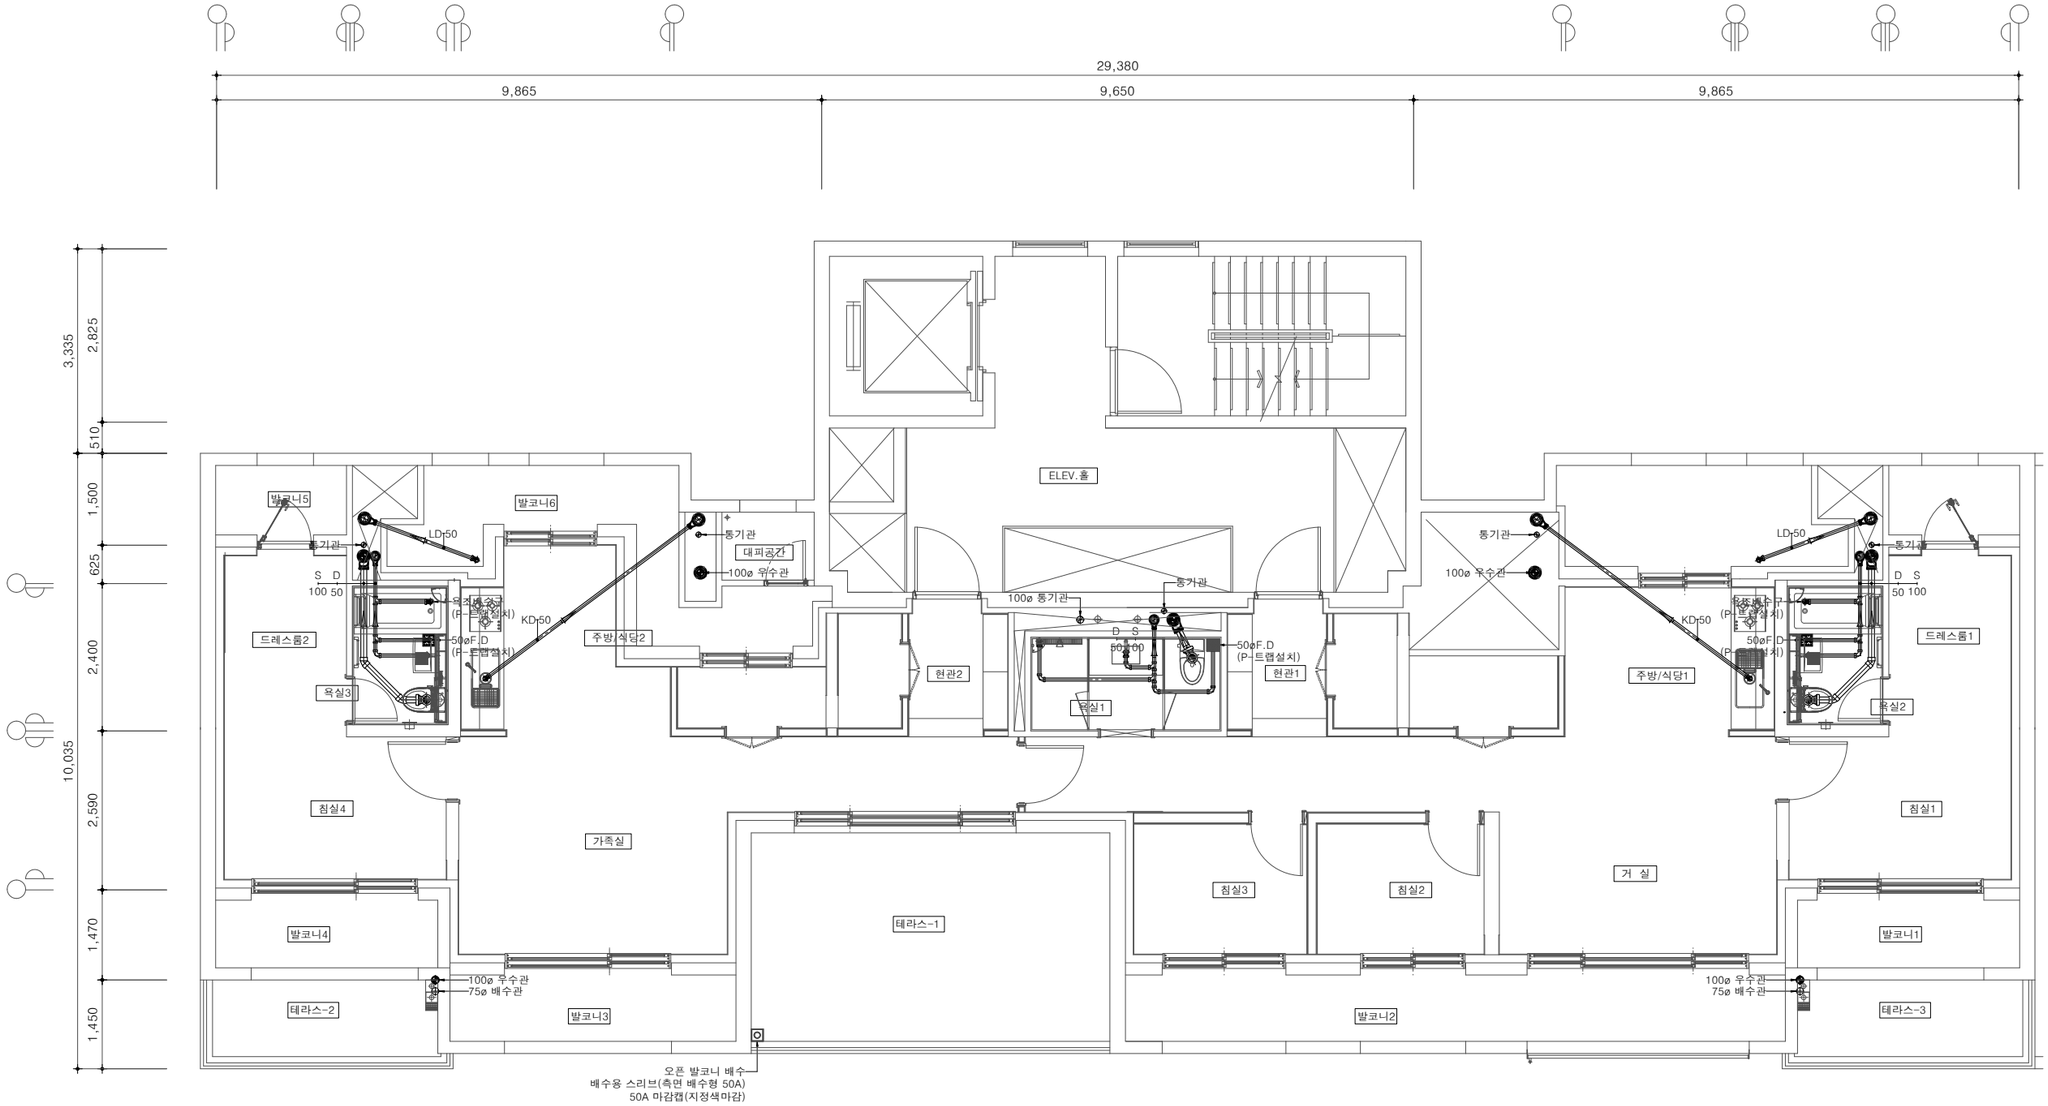

142m²P형 단위세대 오,배수배관 평면도(기본형)

축 척 : 1/100

경기주택도시공사
GYEONGGI HOUSING & URBAN DEVELOPMENT CORPORATION

설계명 PROJECT TITLE

화성동탄(2)A76-2BL
민간참여 공동주택사업

주기 NOTE
1. 현장여건에 따라 실시도면은 변경될 수 있다.
2. 수전 및 배수구는 도서와 건본주택이 상이할 경우 건본주택을 따른다.
3. 욕실 및 다용도실의 오/배수 배관은 하부층 천장에 설치한다.
4. 주방 배관은 당해층 슬라브 상부에 설치한다.
5. 음식물 탈수기 설치

NO	DATE	REVISION DESCRIPTION	APPD
△			
△			
△			
△			

설 계
DESIGN

대표전화

축 척	SCALE
A1	1 / 50
A3	1 / 100


일 자 DATE
2025. 12.

설계번호 PROJECT NO.
AR - 23 - 026

도면화일명 DWG. FILE NAME

도면번호 SHEET NO.
MP - 027

도면명 SUBJECT TITLE
142m²P형 단위세대
오,배수배관 평면도(기본형)

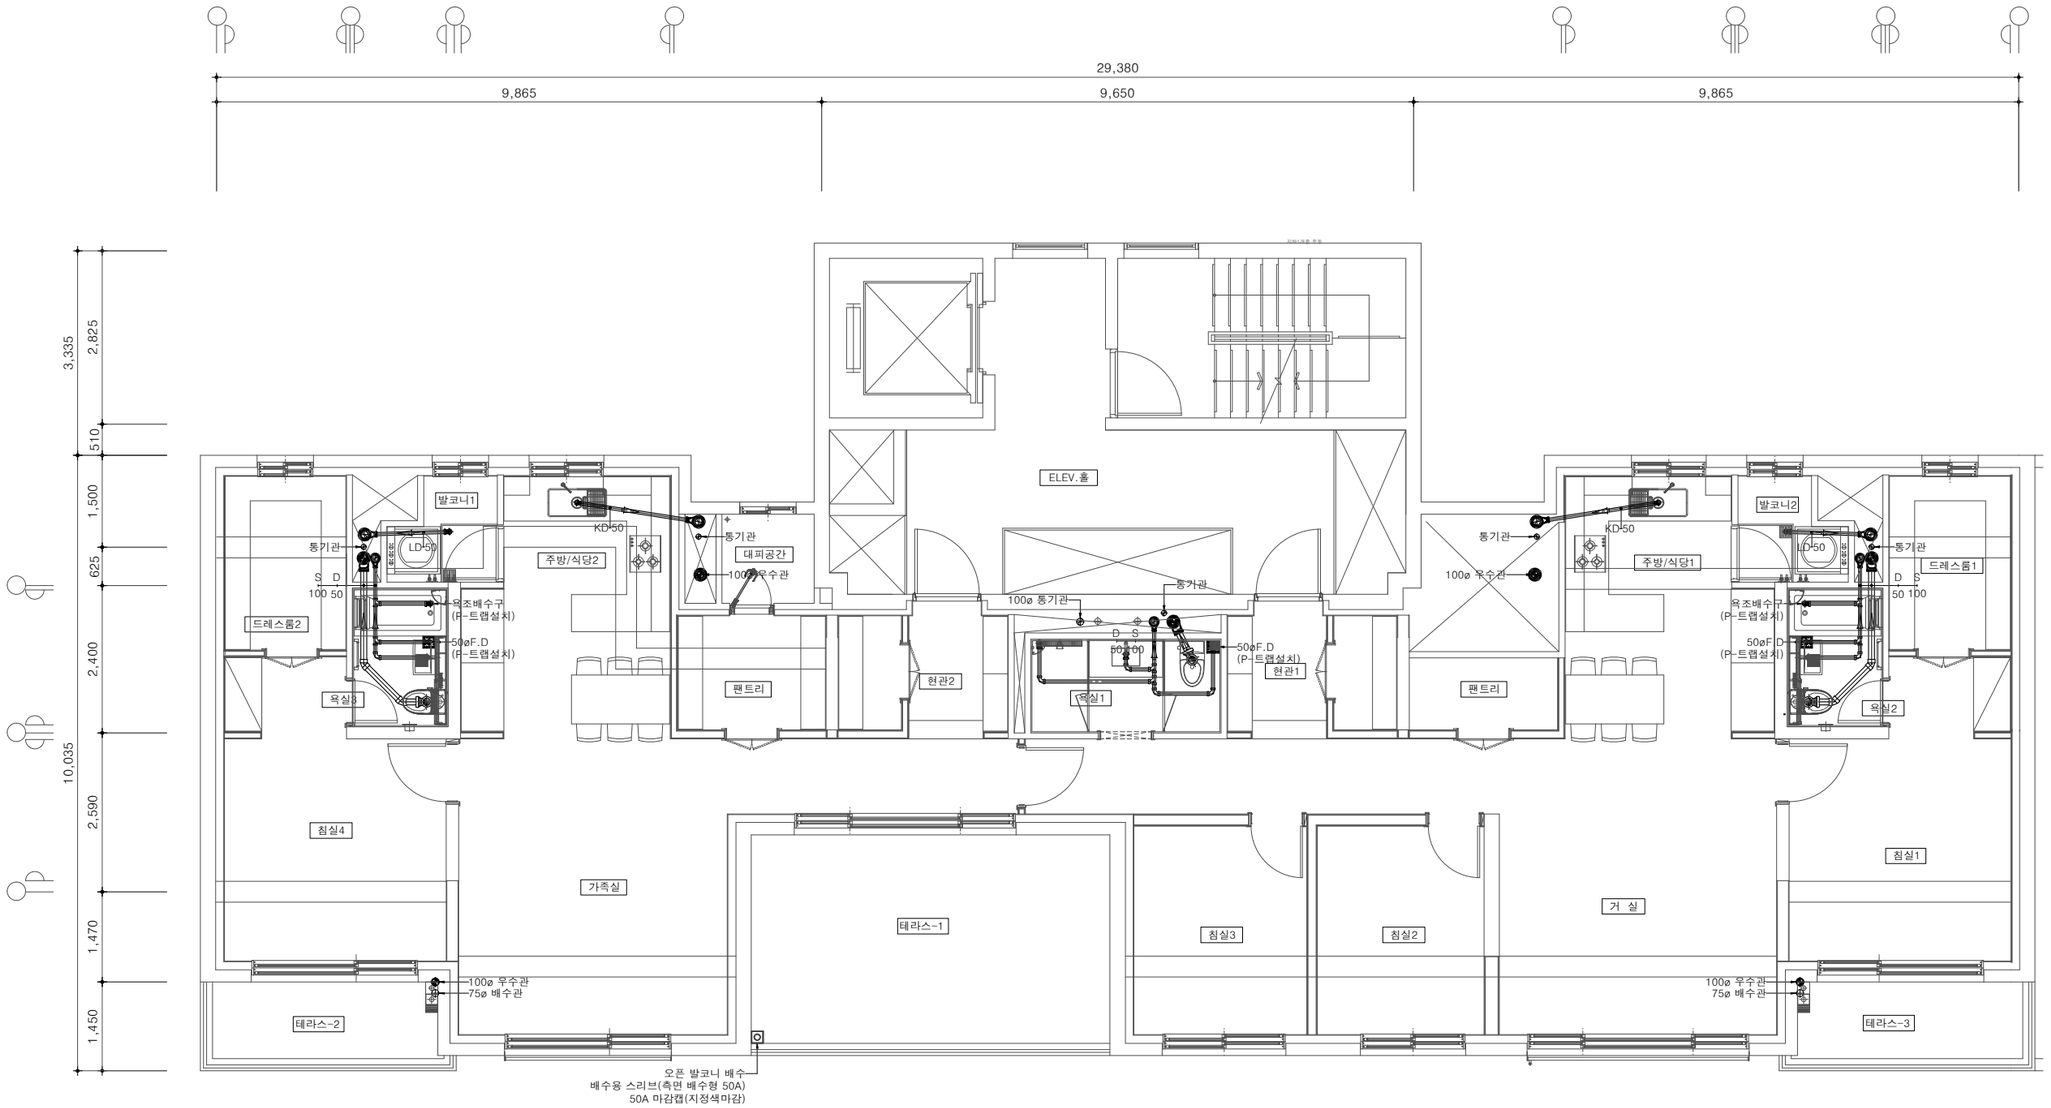

M 142m²P형 단위세대 오,배수배관 평면도(확장형)

축 척 : 1/100

경기주택도시공사
GYEONGGI HOUSING & URBAN DEVELOPMENT CORPORATION

설계명 PROJECT TITLE

화성동탄(2)A76-2BL
민간참여 공동주택사업

주기 NOTE
1. 현장여건에 따라 실시도면은 변경될 수 있다.
2. 수전 및 배수구는 도서와 건본주택이 상이할 경우 건본주택을 따른다.
3. 욕실 및 다용도실의 오/배수 배관은 하부층 천장에 설치한다.
4. 주방 배관은 당해층 슬라브 상부에 설치한다.
5. 음식물 탈수기 설치

NO	DATE	REVISION DESCRIPTION	APPD
△			
△			
△			
△			

설 계
DESIGN

대표전화

축 척 SCALE	
A1	1 / 50
A3	1 / 100


일 자 DATE
2025. 12.

설계번호 PROJECT NO.
AR - 23 - 026

도면화일명 DWG. FILE NAME

도면번호 SHEET NO.
MP - 028

도면명 SUBJECT TITLE
142m²P형 단위세대
오,배수배관 평면도(확장형)

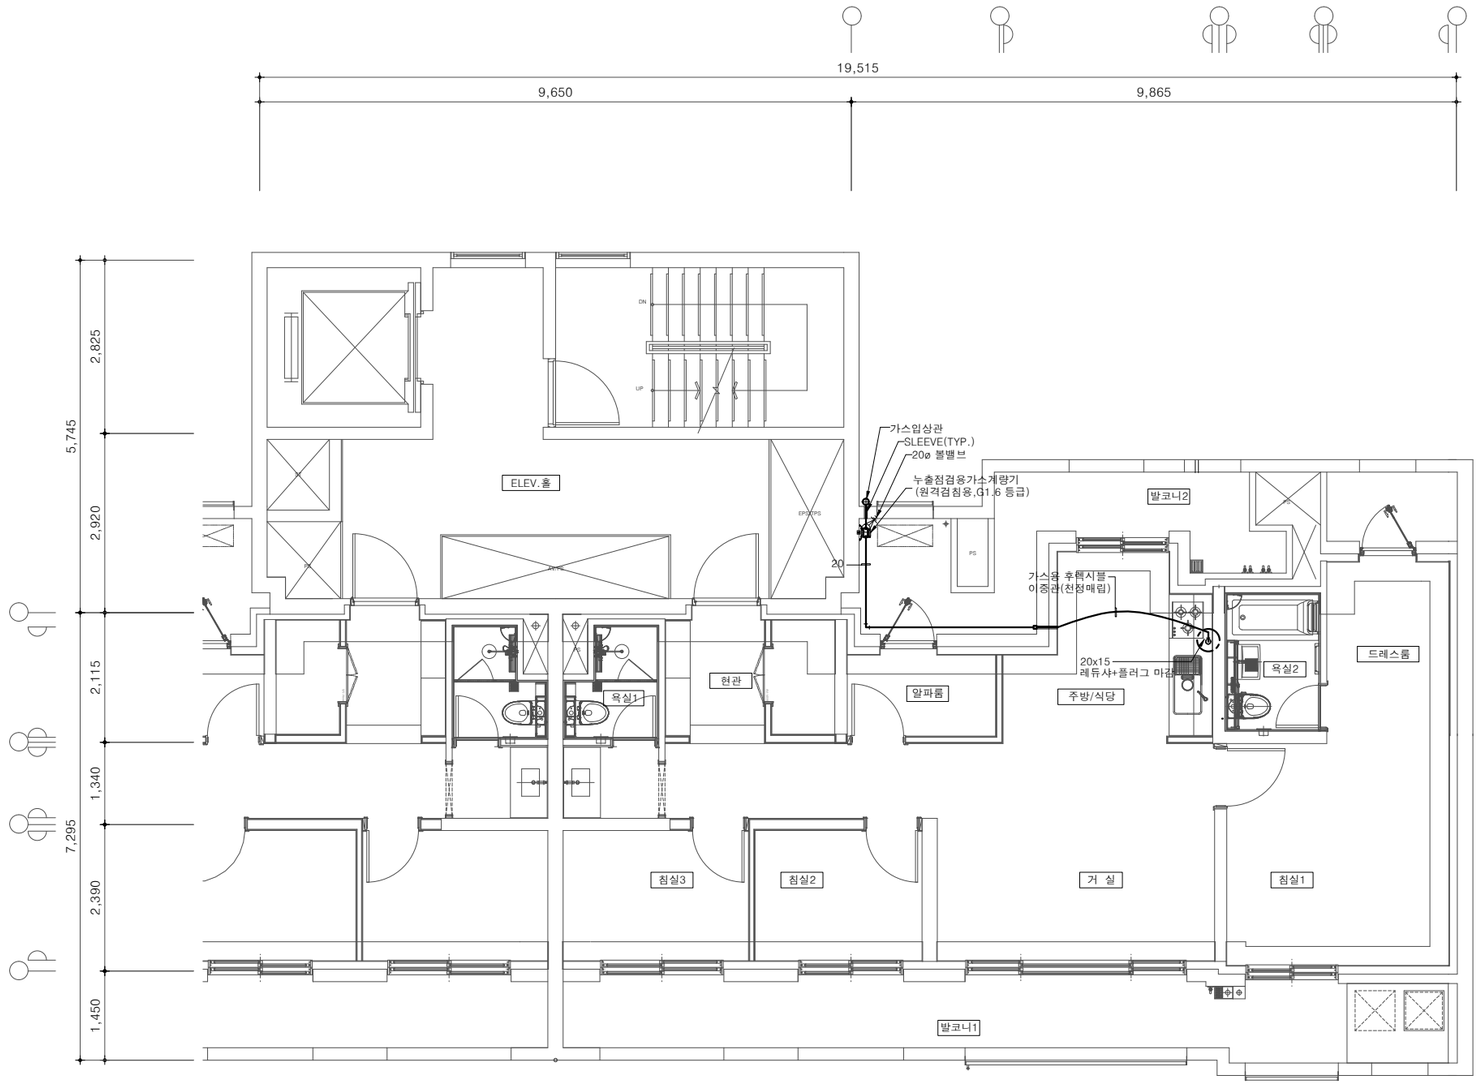

84m²A형 단위세대 가스배관 평면도(기본형)

축 척 : 1/100

경기주택도시공사
GYEONGGI HOUSING & URBAN DEVELOPMENT CORPORATION

설계명 PROJECT TITLE

화성동탄(2)A76-2BL
민간참여 공동주택사업

주기 NOTE
1. 배관위치, 배관 및 밸브류 구경은 현장 여건에 따라 변경 될 수 있음.
2. 신축이음 및 앙카류 등 배관 부속류 위치는 현장 여건에 따라 변경 될 수 있음.
3. 배관의 매립방식은 이중관을 이용하여 수리 및 교체가 용이하도록 함.
4. 센서식 풋밸브 씽크수전 설치

NO	DATE	REVISION DESCRIPTION	APPD
△			
△			
△			
△			

설 계
DESIGN

대표전화

축 척	SCALE
A1	1 / 50
A3	1 / 100


일 자 DATE
2025. 12.

설계번호 PROJECT NO.
AR - 23 - 026

도면화일명 DWG. FILE NAME

도면번호 SHEET NO.
MG - 002

도면명 SUBJECT TITLE
84m²A형 단위세대
가스배관 평면도(기본형)

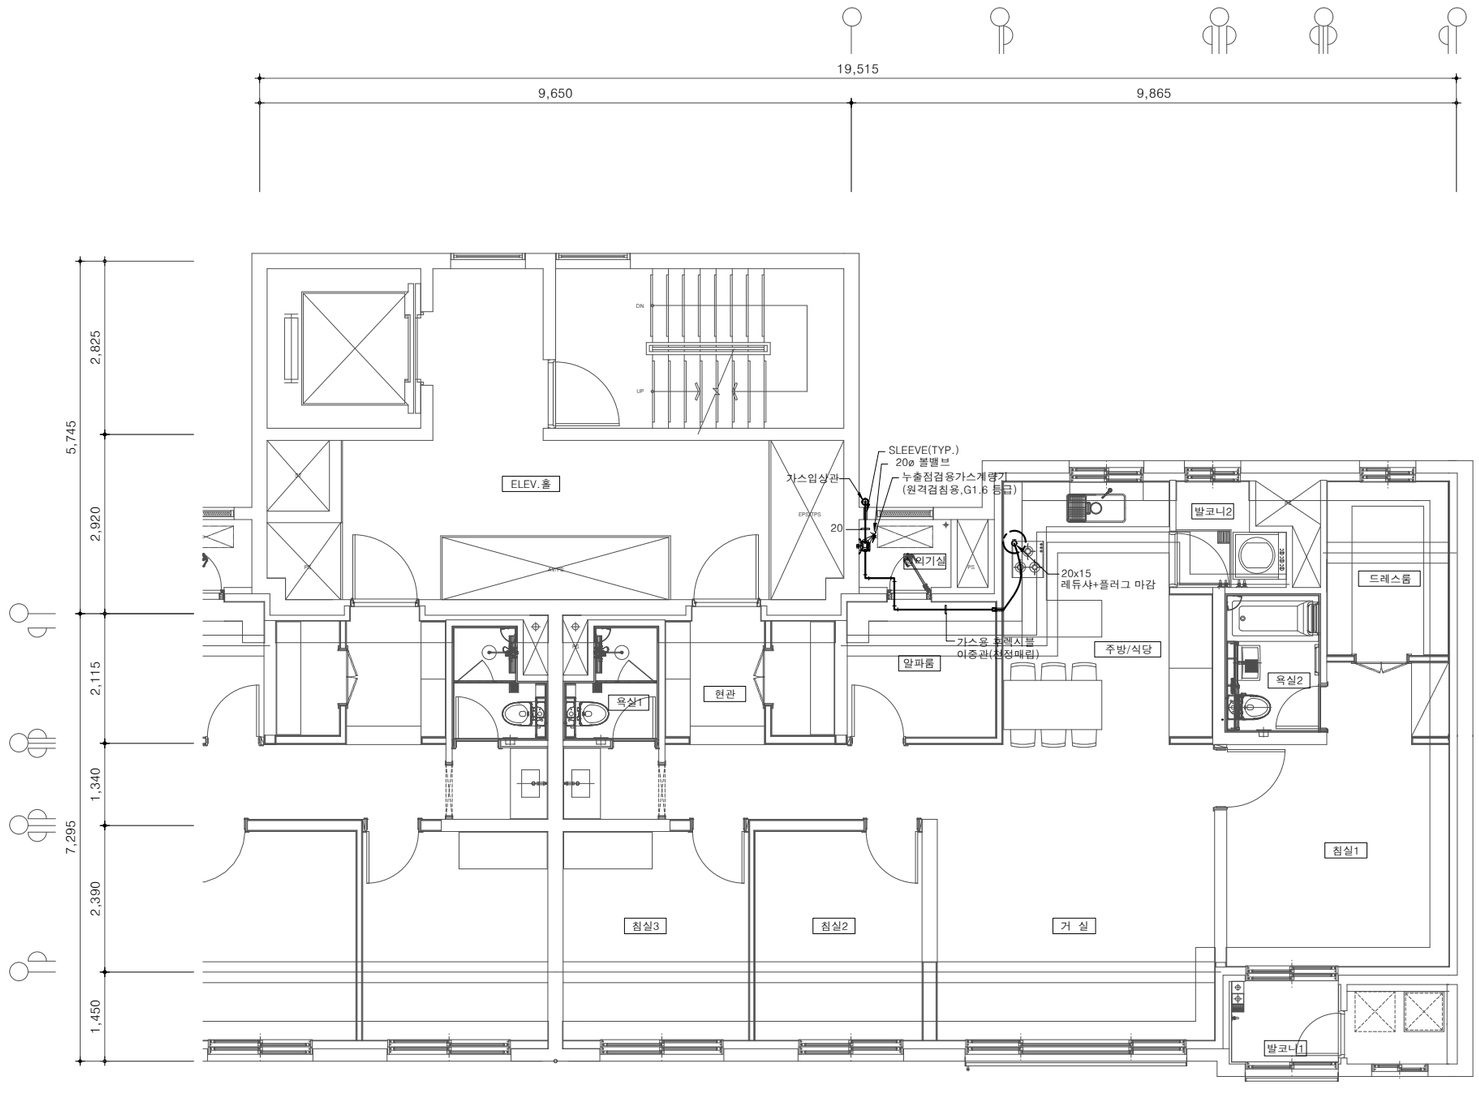

84m²A형 단위세대 가스배관 평면도(확장형)

축 척 : 1/100

경기주택도시공사
GYEONGGI HOUSING & URBAN DEVELOPMENT CORPORATION

설계명 PROJECT TITLE

화성동탄(2)A76-2BL
민간참여 공동주택사업

주기 NOTE
1. 배관위치, 배관 및 밸브류 구경은 현장 여건에 따라 변경 될 수 있음.
2. 신축이음 및 앙카류 등 배관 부속류 위치는 현장 여건에 따라 변경 될 수 있음.
3. 배관의 매립방식은 이중관을 이용하여 수리 및 교체가 용이하도록 함.
4. 센서식 풋밸브 씽크수전 설치

NO	DATE	REVISION DESCRIPTION	APPD
△			
△			
△			
△			

설 계
DESIGN

대표전화

축 척	SCALE
A1	1 / 50
A3	1 / 100


일 자 DATE
2025. 12.

설계번호 PROJECT NO.
AR - 23 - 026

도면화일명 DWG. FILE NAME

도면번호 SHEET NO.
MG – 003

도면명 SUBJECT TITLE
84m²A형 단위세대
가스배관 평면도(확장형)

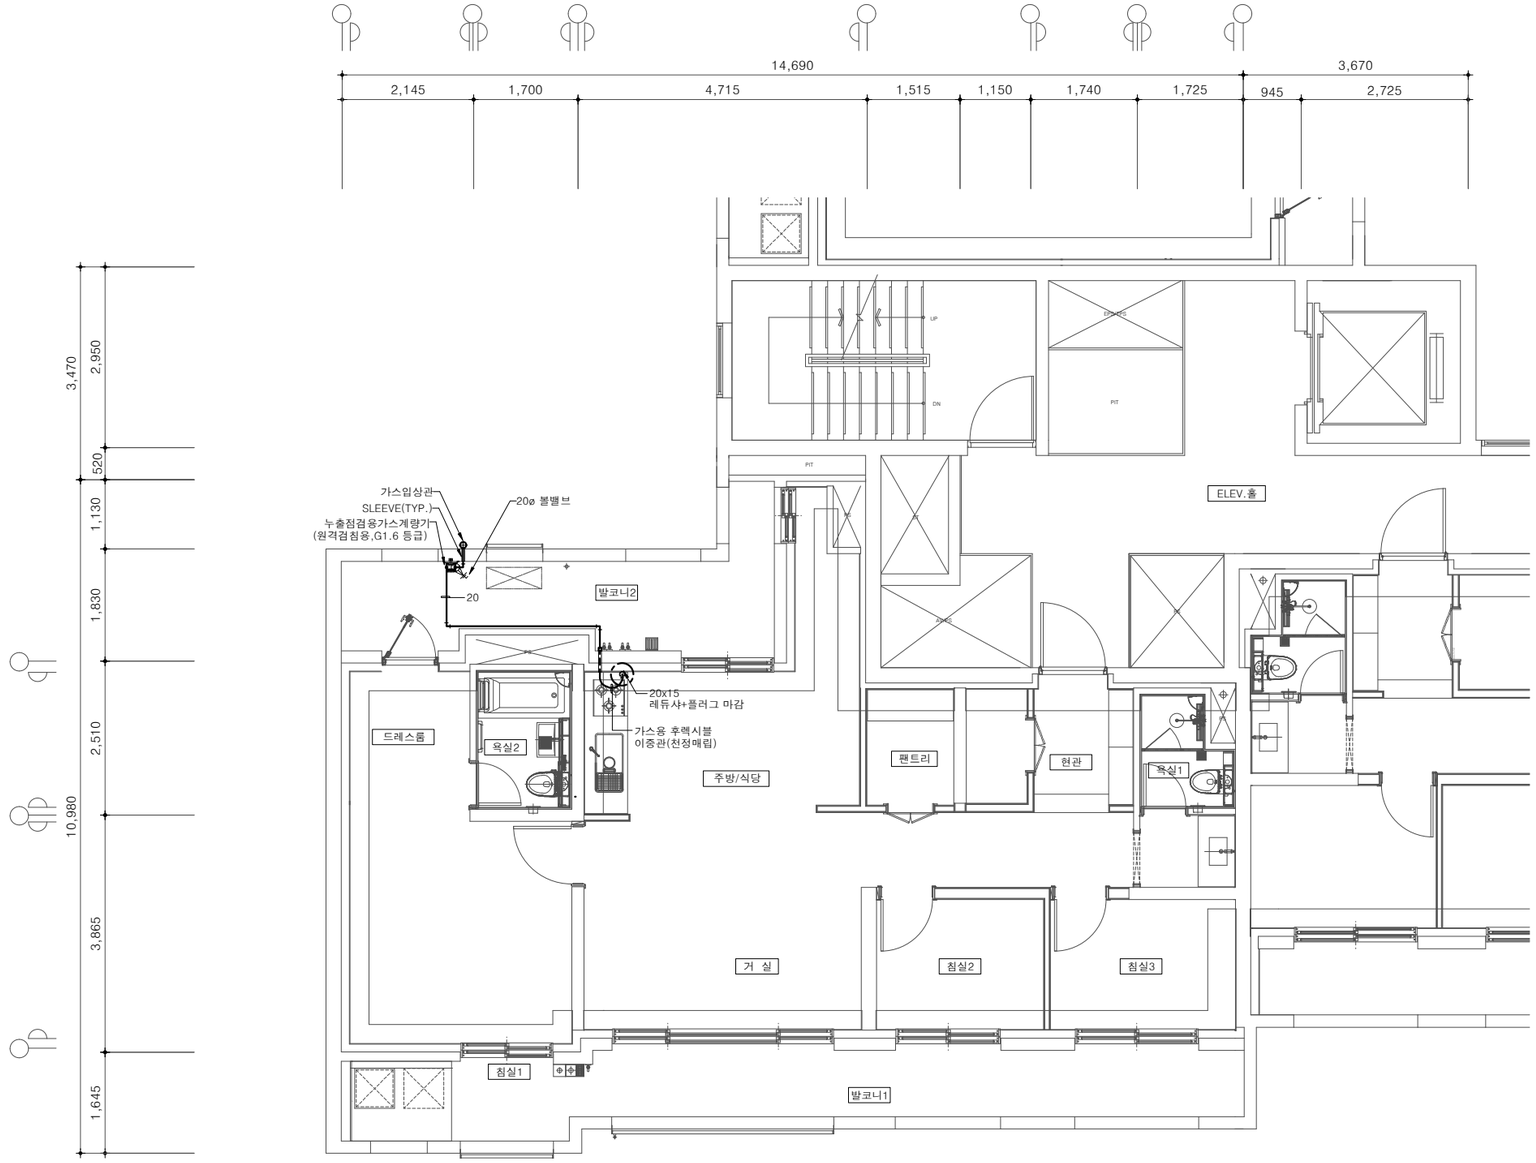

84m²B형 단위세대 가스배관 평면도(기본형)

축 척 : 1/100

경기주택도시공사
GYEONGGI HOUSING & URBAN DEVELOPMENT CORPORATION

설계명 PROJECT TITLE

화성동탄(2)A76-2BL
민간참여 공동주택사업

주기 NOTE
1. 배관위치, 배관 및 밸브류 구경은 현장 여건에 따라 변경 될 수 있음.
2. 신축이음 및 앙카류 등 배관 부속류 위치는 현장 여건에 따라 변경 될 수 있음.
3. 배관의 매립방식은 이중관을 이용하여 수리 및 교체가 용이하도록 함.
4. 센서식 풋밸브 씽크수전 설치

NO	DATE	REVISION DESCRIPTION	APPD

설 계
DESIGN

대표전화

축 척	SCALE
A1	1 / 50
A3	1 / 100


일 자 DATE
2025. 12.

설계번호 PROJECT NO.
AR - 23 - 026

도면화일명 DWG. FILE NAME

도면번호 SHEET NO.
MG – 004

도면명 SUBJECT TITLE
84m²B형 단위세대
가스배관 평면도(기본형)

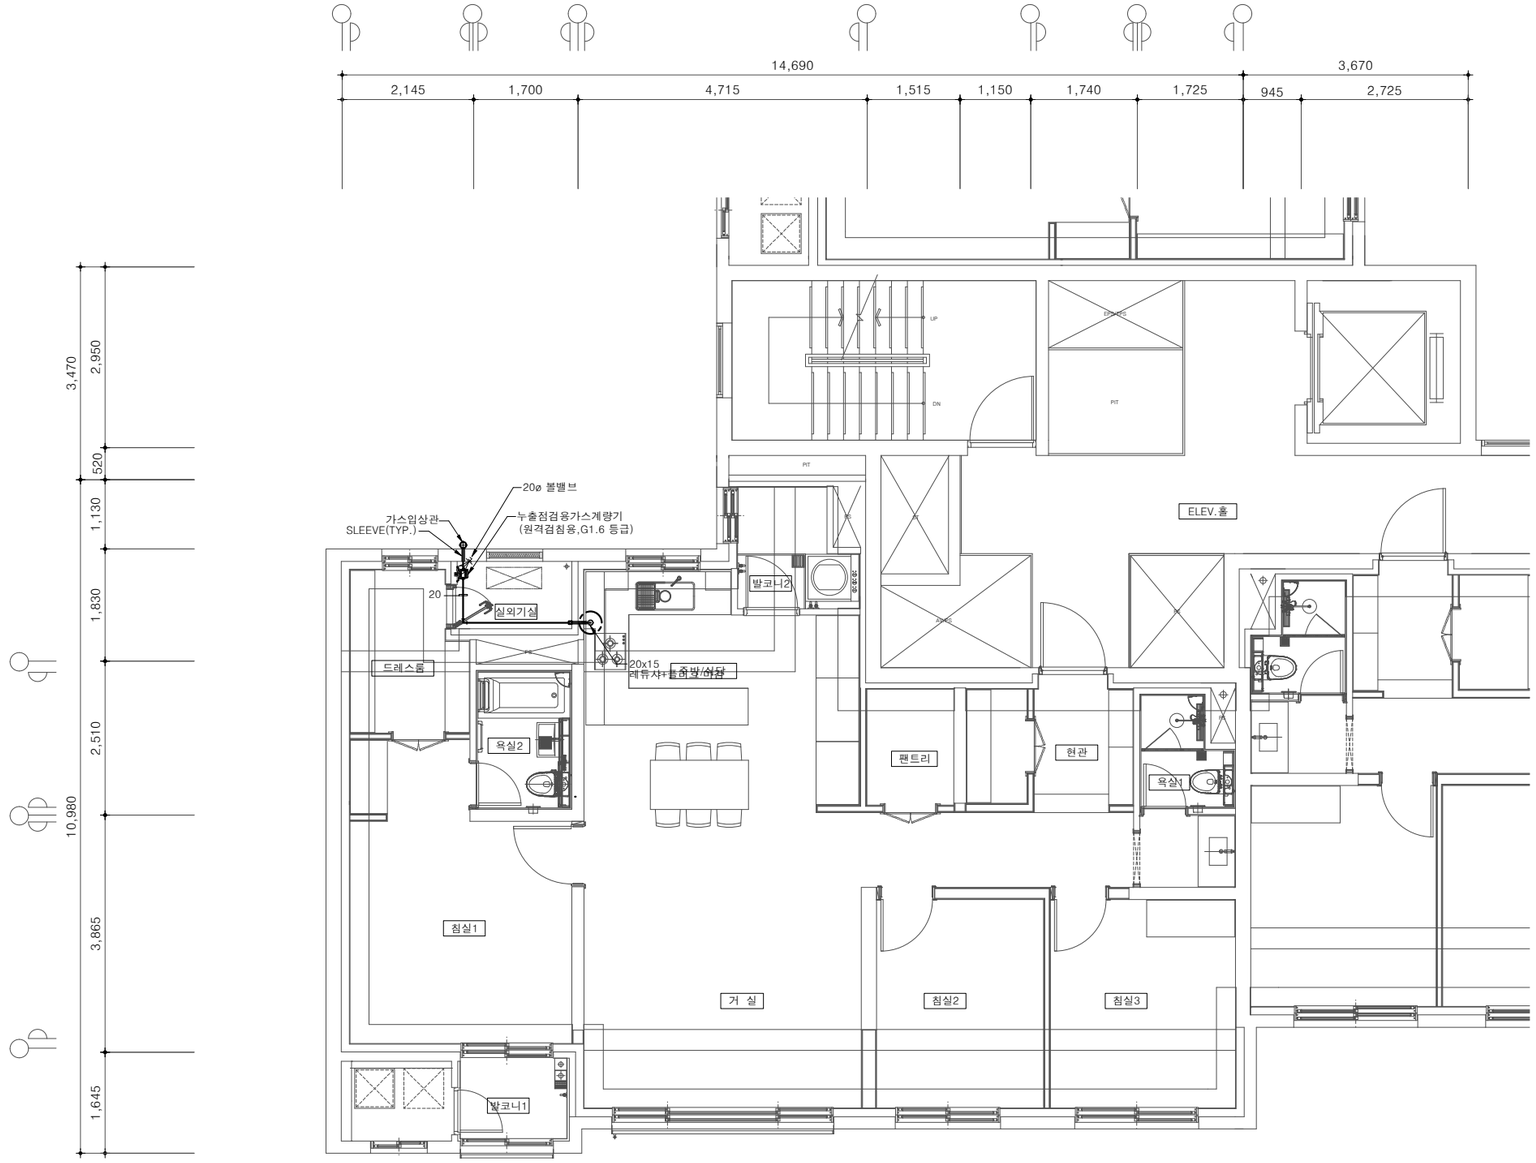

84m²B형 단위세대 가스배관 평면도(확장형)

축 척 : 1/100

경기주택도시공사
GYEONGGI HOUSING & URBAN DEVELOPMENT CORPORATION

설계명 PROJECT TITLE

화성동탄(2)A76-2BL
민간참여 공동주택사업

주기 NOTE
1. 배관위치, 배관 및 밸브류 구경은 현장 여건에 따라 변경 될 수 있음.
2. 신축이음 및 앙카류 등 배관 부속류 위치는 현장 여건에 따라 변경 될 수 있음.
3. 배관의 매립방식은 이중관을 이용하여 수리 및 교체가 용이하도록 함.
4. 센서식 풋밸브 씽크수전 설치

NO	DATE	REVISION DESCRIPTION	APPD

설 계
DESIGN

대표전화

축 척	SCALE
A1	1 / 50
A3	1 / 100


일 자 DATE
2025. 12.

설계번호 PROJECT NO.
AR - 23 - 026

도면화일명 DWG. FILE NAME

도면번호 SHEET NO.
MG – 005

도면명 SUBJECT TITLE
84m²B형 단위세대
가스배관 평면도(확장형)

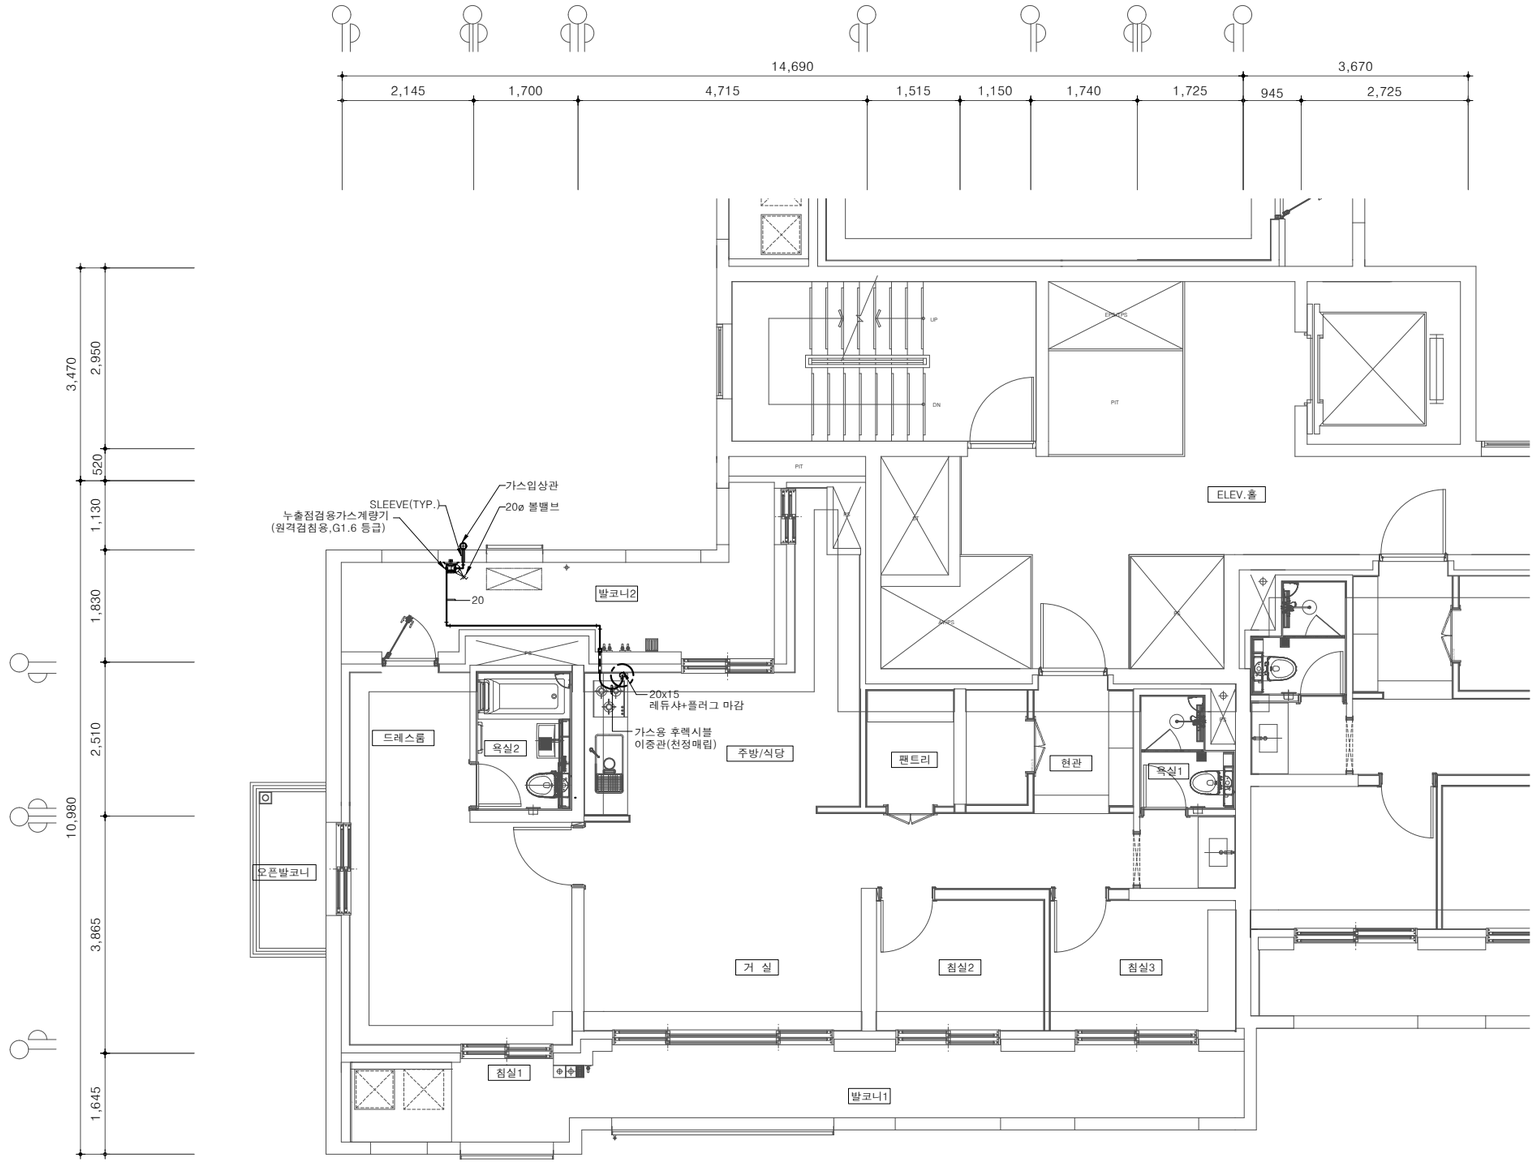

84m²C형 단위세대 가스배관 평면도(기본형)

축 척 : 1/100

경기주택도시공사
GYEONGGI HOUSING & URBAN DEVELOPMENT CORPORATION

설계명 PROJECT TITLE

화성동탄(2)A76-2BL
민간참여 공동주택사업

주기 NOTE
1. 배관위치, 배관 및 밸브류 구경은 현장 여건에 따라 변경 될 수 있음.
2. 신축이음 및 앙카류 등 배관 부속류 위치는 현장 여건에 따라 변경 될 수 있음.
3. 배관의 매립방식은 이중관을 이용하여 수리 및 교체가 용이하도록 함.
4. 센서식 풋밸브 씽크수전 설치

NO	DATE	REVISION DESCRIPTION	APPD

설 계
DESIGN

대표전화

축 척	SCALE
A1	1 / 50
A3	1 / 100


일 자 DATE
2025. 12.

설계번호 PROJECT NO.
AR - 23 - 026

도면화일명 DWG. FILE NAME

도면번호 SHEET NO.
MG – 006

도면명 SUBJECT TITLE
84m²C형 단위세대
가스배관 평면도(기본형)

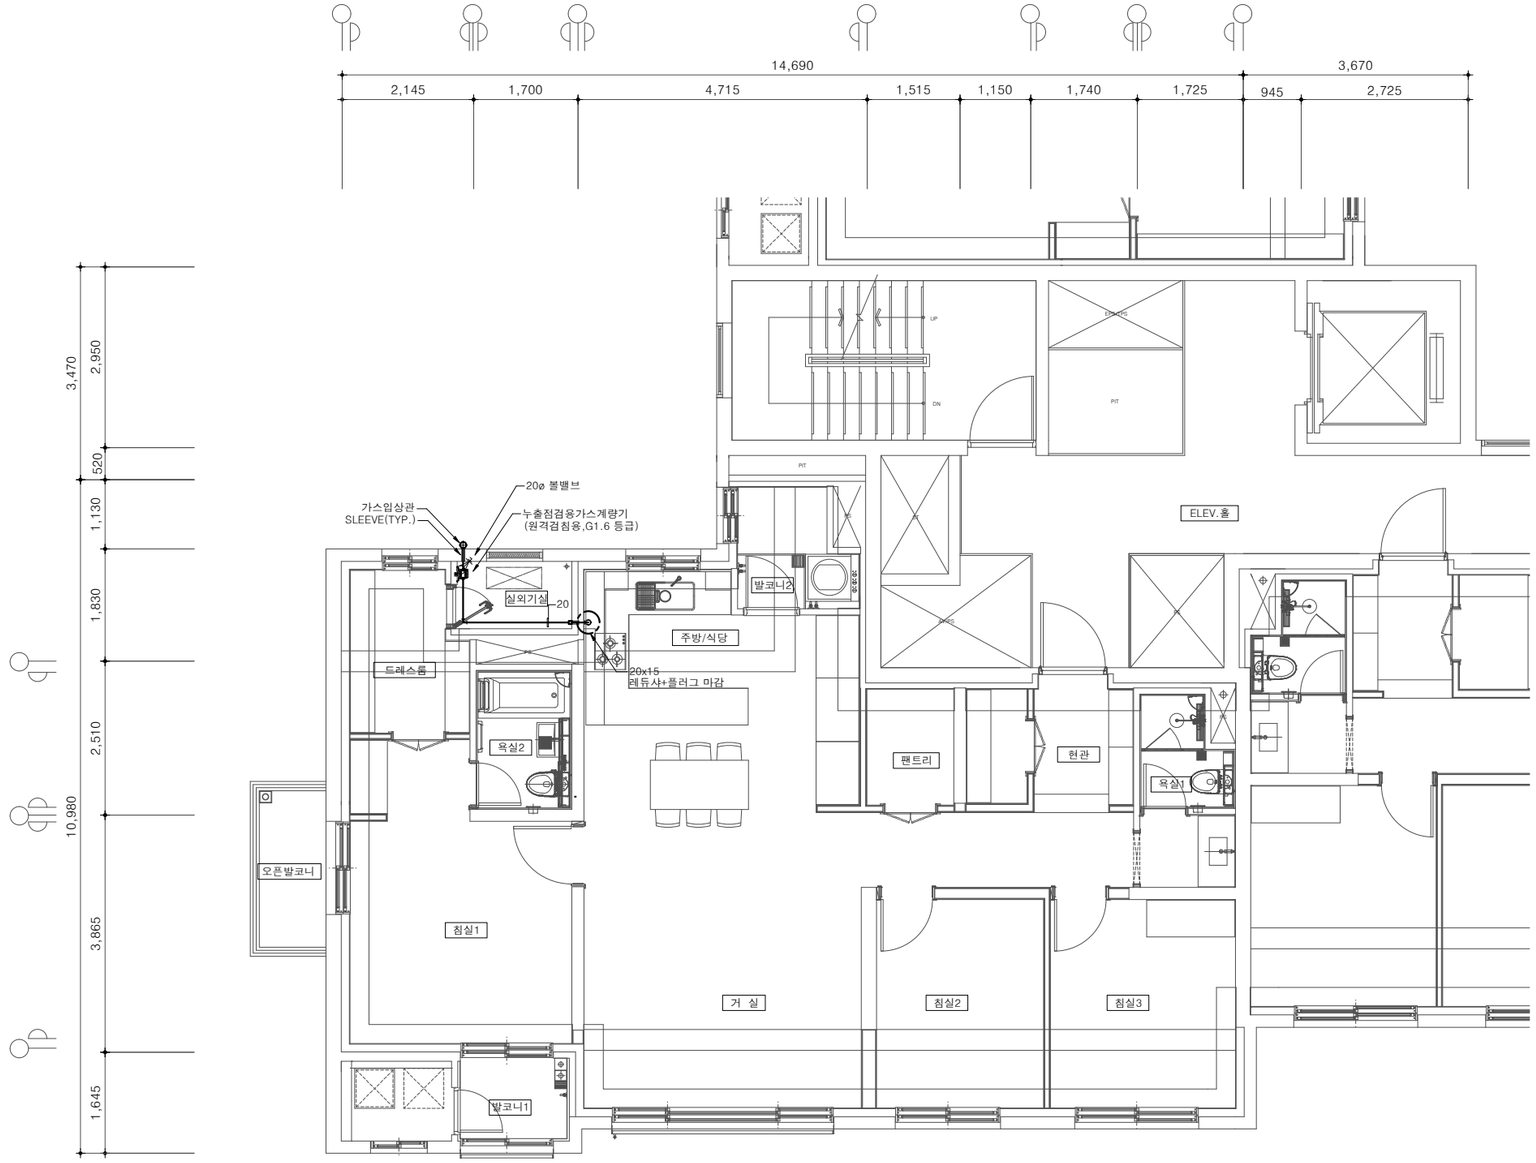

M 84m²C형 단위세대 가스배관 평면도(확장형)

축 척 : 1/100

경기주택도시공사
GYEONGGI HOUSING & URBAN DEVELOPMENT CORPORATION

설계명 PROJECT TITLE

화성동탄(2)A76-2BL
민간참여 공동주택사업

주기 NOTE
1. 배관위치, 배관 및 밸브류 구경은 현장 여건에 따라 변경 될 수 있음.
2. 신축이음 및 앙카류 등 배관 부속류 위치는 현장 여건에 따라 변경 될 수 있음.
3. 배관의 매립방식은 이중관을 이용하여 수리 및 교체가 용이하도록 함.
4. 센서식 풋밸브 씽크수전 설치

NO	DATE	REVISION DESCRIPTION	APPD

설 계
DESIGN

대표전화

축 척	SCALE
A1	1 / 50
A3	1 / 100


일 자 DATE
2025. 12.

설계번호 PROJECT NO.
AR - 23 - 026

도면화일명 DWG. FILE NAME

도면번호 SHEET NO.
MG – 007

도면명 SUBJECT TITLE
84m²C형 단위세대
가스배관 평면도(확장형)

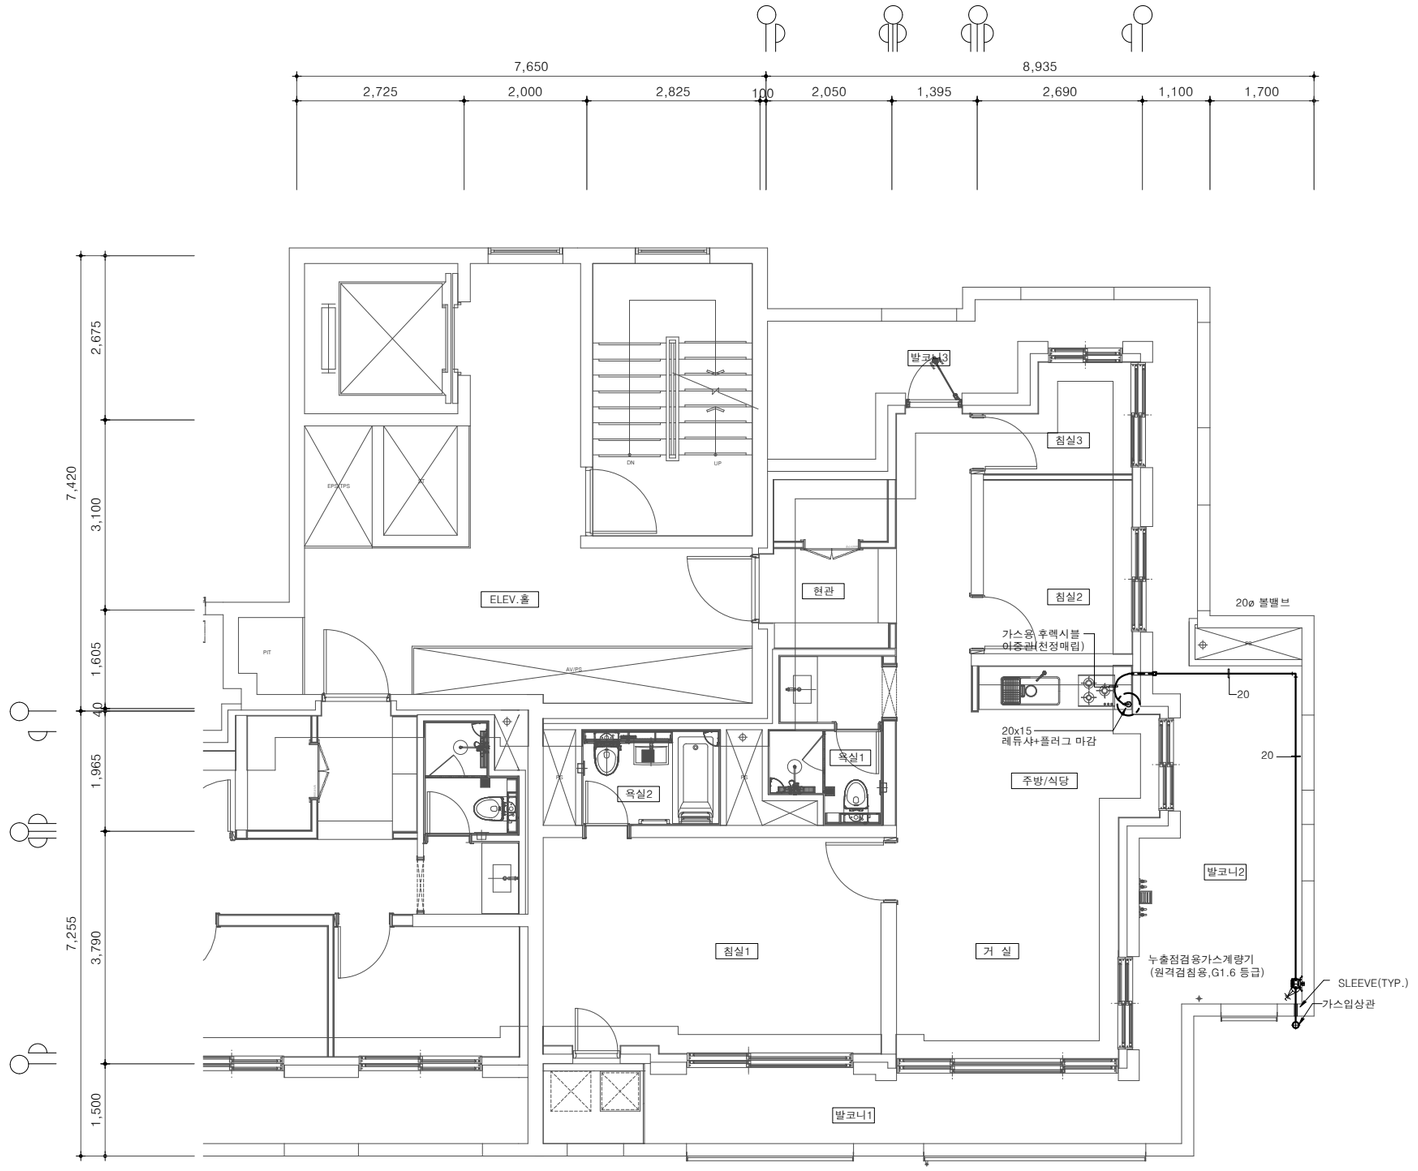

84m²D형 단위세대 가스배관 평면도(기본형)

축 척 : 1/100

경기주택도시공사
GYEONGGI HOUSING & URBAN DEVELOPMENT CORPORATION

설계명 PROJECT TITLE

화성동탄(2)A76-2BL
민간참여 공동주택사업

주기 NOTE
1. 배관위치, 배관 및 밸브류 구경은 현장 여건에 따라 변경 될 수 있음.
2. 신축이음 및 앙카류 등 배관 부속류 위치는 현장 여건에 따라 변경 될 수 있음.
3. 배관의 매립방식은 이중관을 이용하여 수리 및 교체가 용이하도록 함.
4. 센서식 풋밸브 씽크수전 설치

NO	DATE	REVISION DESCRIPTION	APPD
△			
△			
△			
△			

설 계
DESIGN

대표전화

축 척	SCALE
A1	1 / 50
A3	1 / 100


일 자 DATE
2025. 12.

설계번호 PROJECT NO.
AR - 23 - 026

도면화일명 DWG. FILE NAME

도면번호 SHEET NO.
MG - 008

도면명 SUBJECT TITLE
84m²D형 단위세대
가스배관 평면도(기본형)

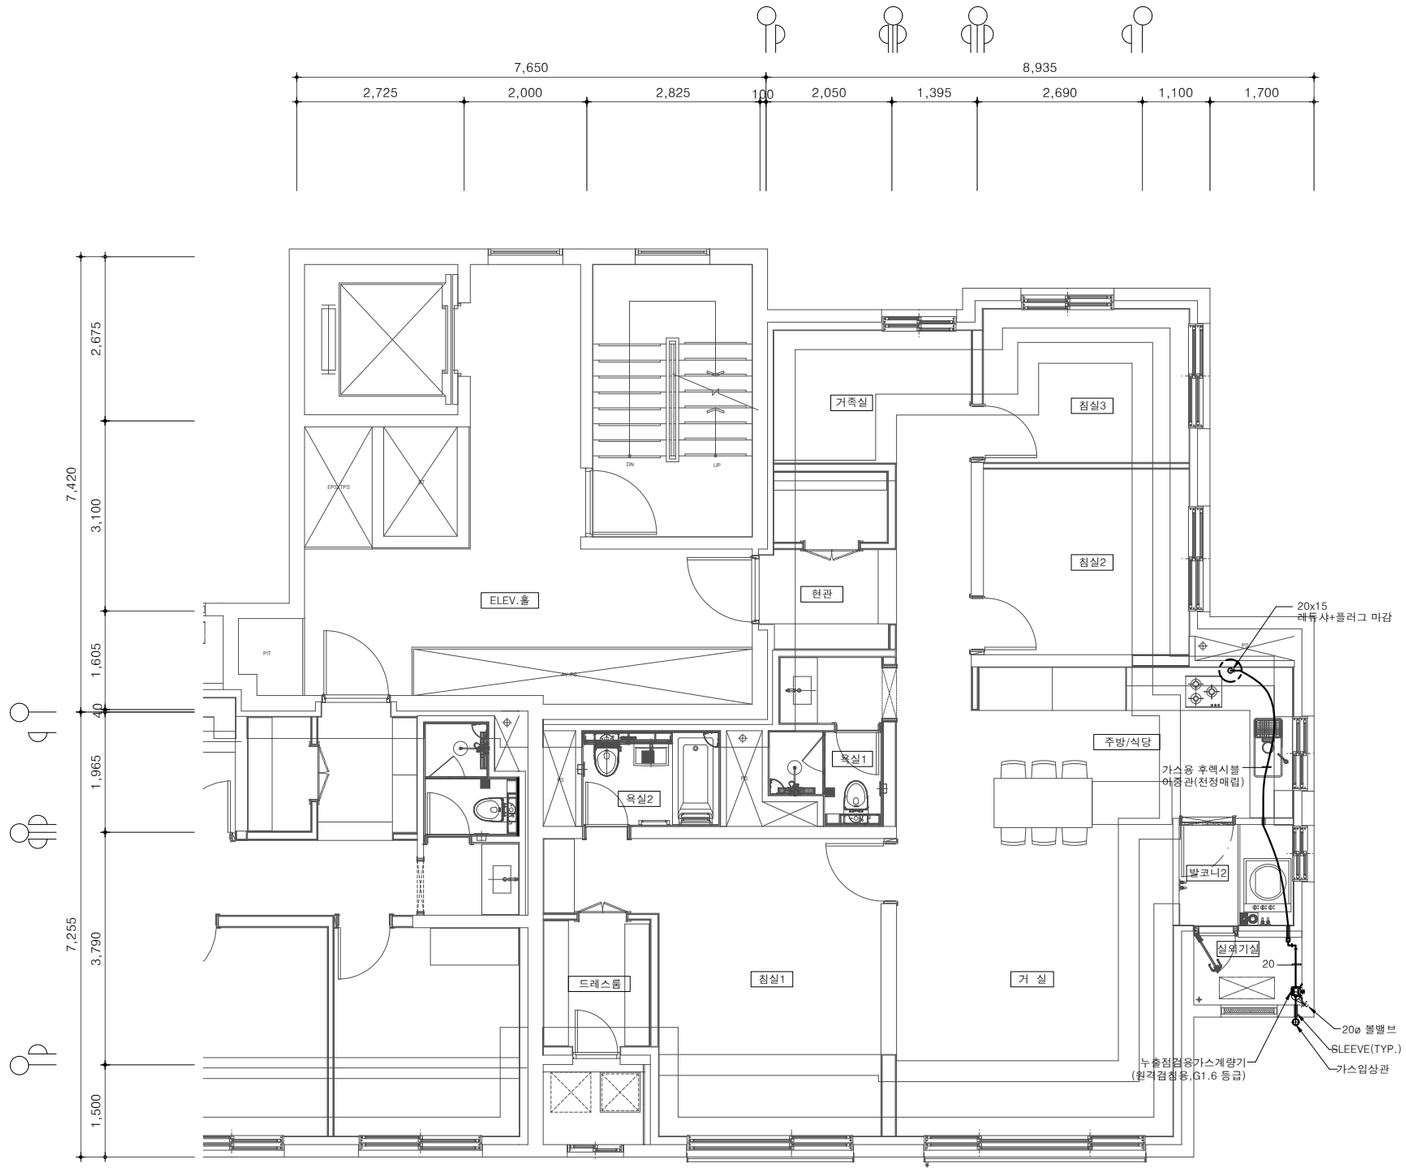

84m²D형 단위세대 가스배관 평면도(확장형)

축 척 : 1/100

경기주택도시공사
GYEONGGI HOUSING & URBAN DEVELOPMENT CORPORATION

설계명 PROJECT TITLE

화성동탄(2)A76-2BL
민간참여 공동주택사업

주기 NOTE
1. 배관위치, 배관 및 밸브류 구경은 현장 여건에 따라 변경 될 수 있음.
2. 신축이음 및 앙카류 등 배관 부속류 위치는 현장 여건에 따라 변경 될 수 있음.
3. 배관의 매립방식은 이중관을 이용하여 수리 및 교체가 용이하도록 함.
4. 센서식 풋밸브 씽크수전 설치

NO	DATE	REVISION DESCRIPTION	APPD
△			
△			
△			
△			

설 계
DESIGN

대표전화

축 척	SCALE
A1	1 / 50
A3	1 / 100


일 자 DATE
2025. 12.

설계번호 PROJECT NO.
AR - 23 - 026

도면화일명 DWG. FILE NAME

도면번호 SHEET NO.
MG - 009

도면명 SUBJECT TITLE
84m²D형 단위세대
가스배관 평면도(확장형)

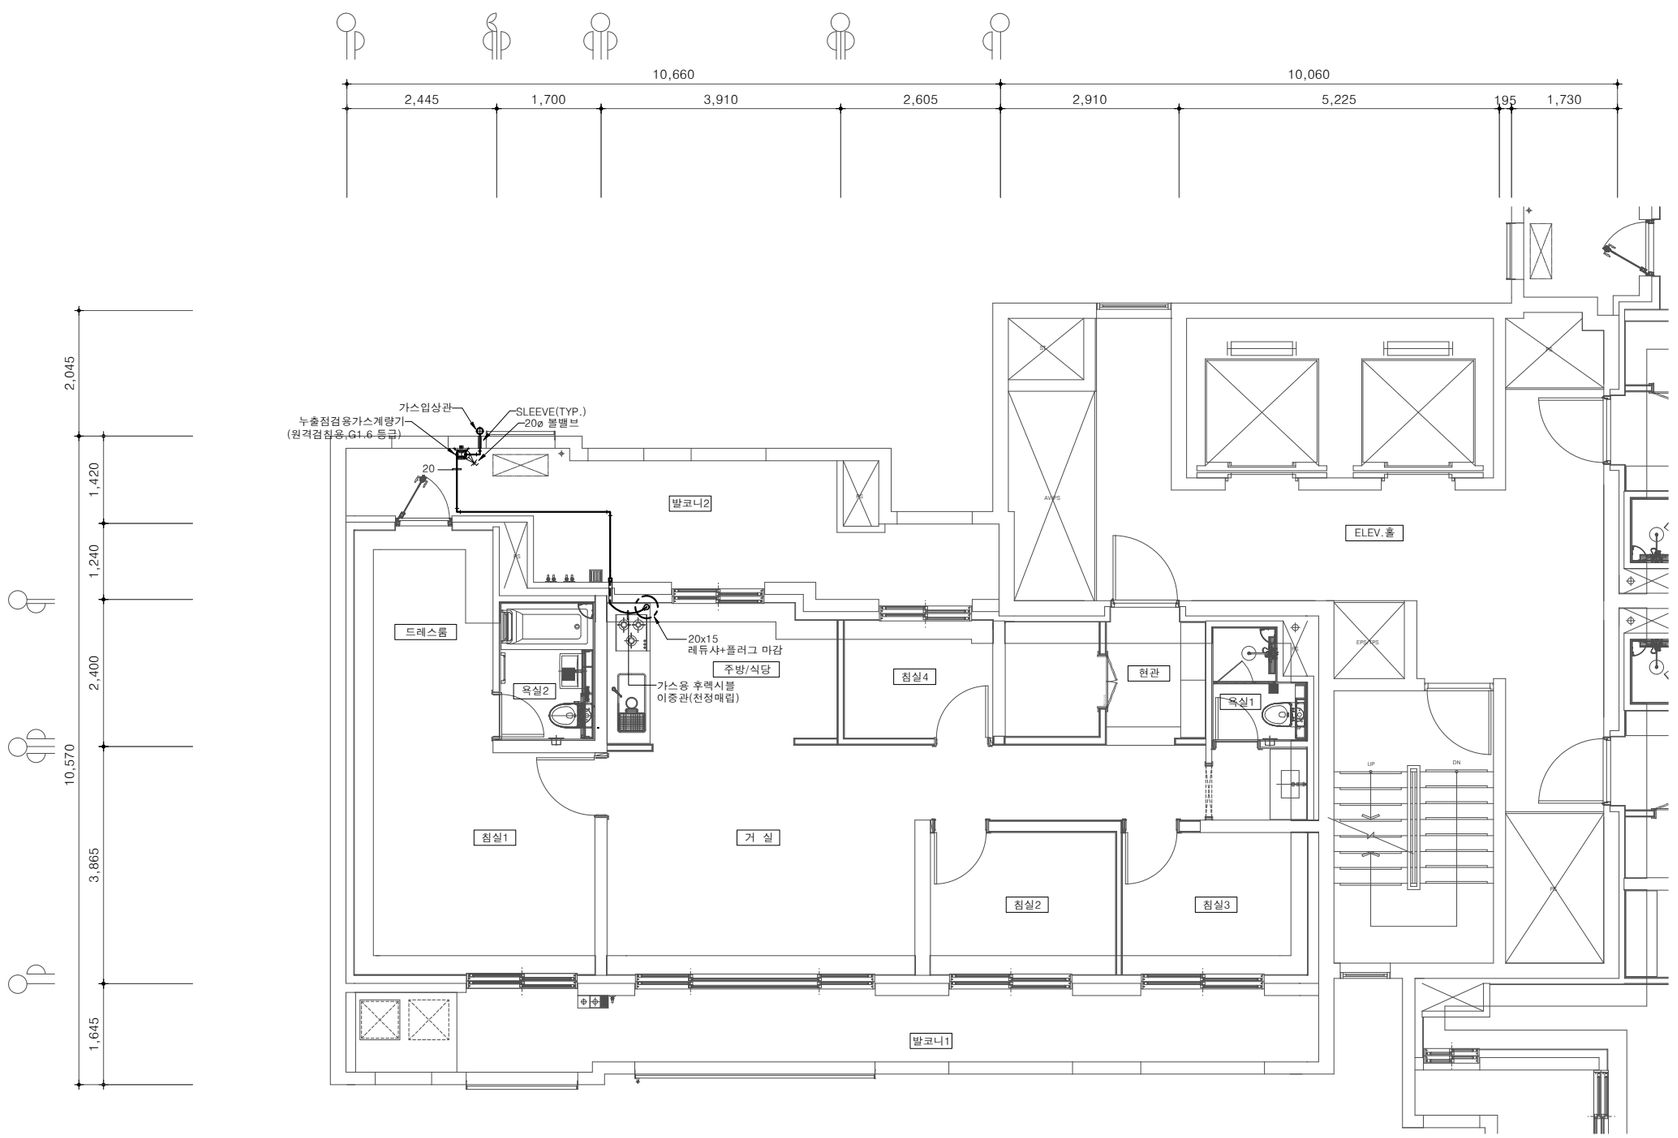

97m²A형 단위세대 가스배관 평면도(기본형)

축 척 : 1/100

경기주택도시공사
GYEONGGI HOUSING & URBAN DEVELOPMENT CORPORATION

설계명 PROJECT TITLE


화성동탄(2)A76-2BL
민간참여 공동주택사업

주기 NOTE

NO	DATE	REVISION DESCRIPTION	APPD
△			
△			
△			
△			

설 계
DESIGN

대표전화	
축 척	SCALE
A1	1 / 50
A3	1 / 100
일 자 DATE	2025. 12.
설계번호 PROJECT NO.	AR - 23 - 026
도면화일명 DWG. FILE NAME	
도면번호 SHEET NO.	MG - 010
도면명 SUBJECT TITLE	97m²A형 단위세대 가스배관 평면도(기본형)

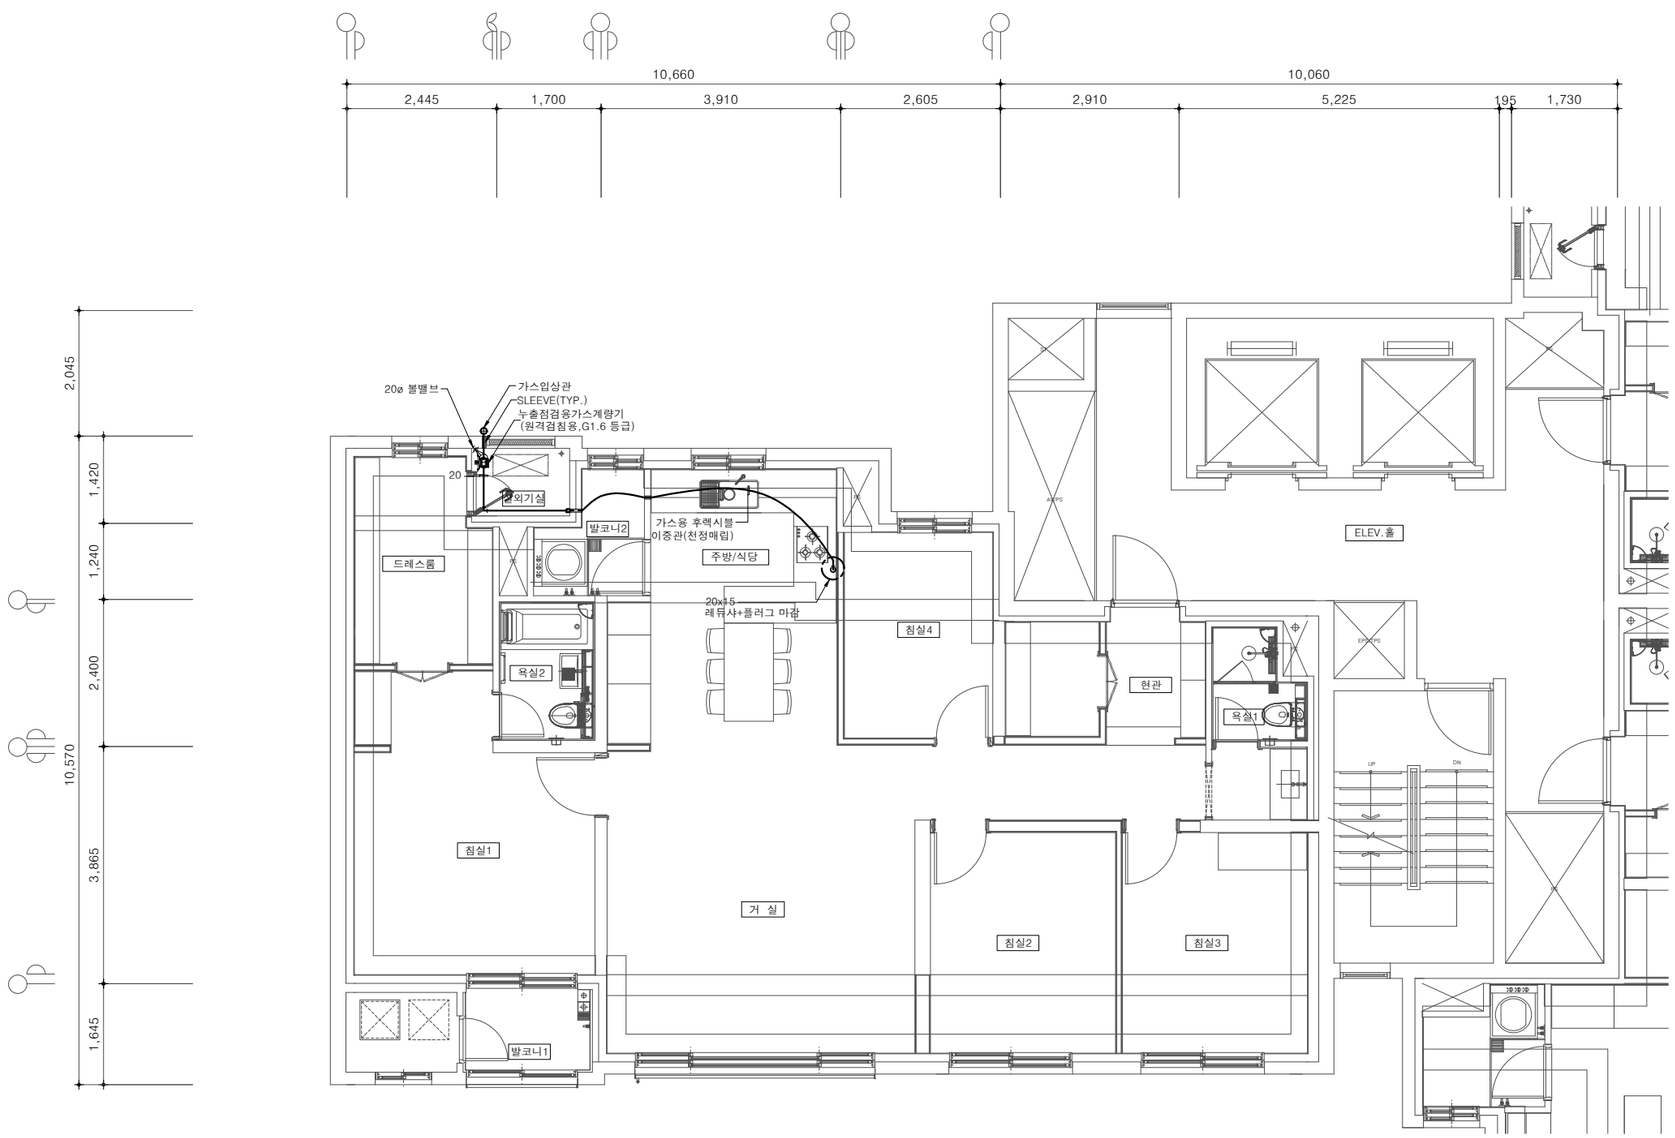

97m²A형 단위세대 가스배관 평면도(확장형)

축 척 : 1/100

경기주택도시공사
GYEONGGI HOUSING & URBAN DEVELOPMENT CORPORATION

설계명 PROJECT TITLE


화성동탄(2)A76-2BL
민간참여 공동주택사업

주기 NOTE

NO	DATE	REVISION DESCRIPTION	APPD
△			
△			
△			
△			

설 계
DESIGN

대표전화	
축 척	SCALE
A1	1 / 50
A3	1 / 100
일 자 DATE	2025. 12.
설계번호 PROJECT NO.	AR - 23 - 026
도면화일명 DWG. FILE NAME	
도면번호 SHEET NO.	MG - 011
도면명 SUBJECT TITLE	97m²A형 단위세대 가스배관 평면도(확장형)

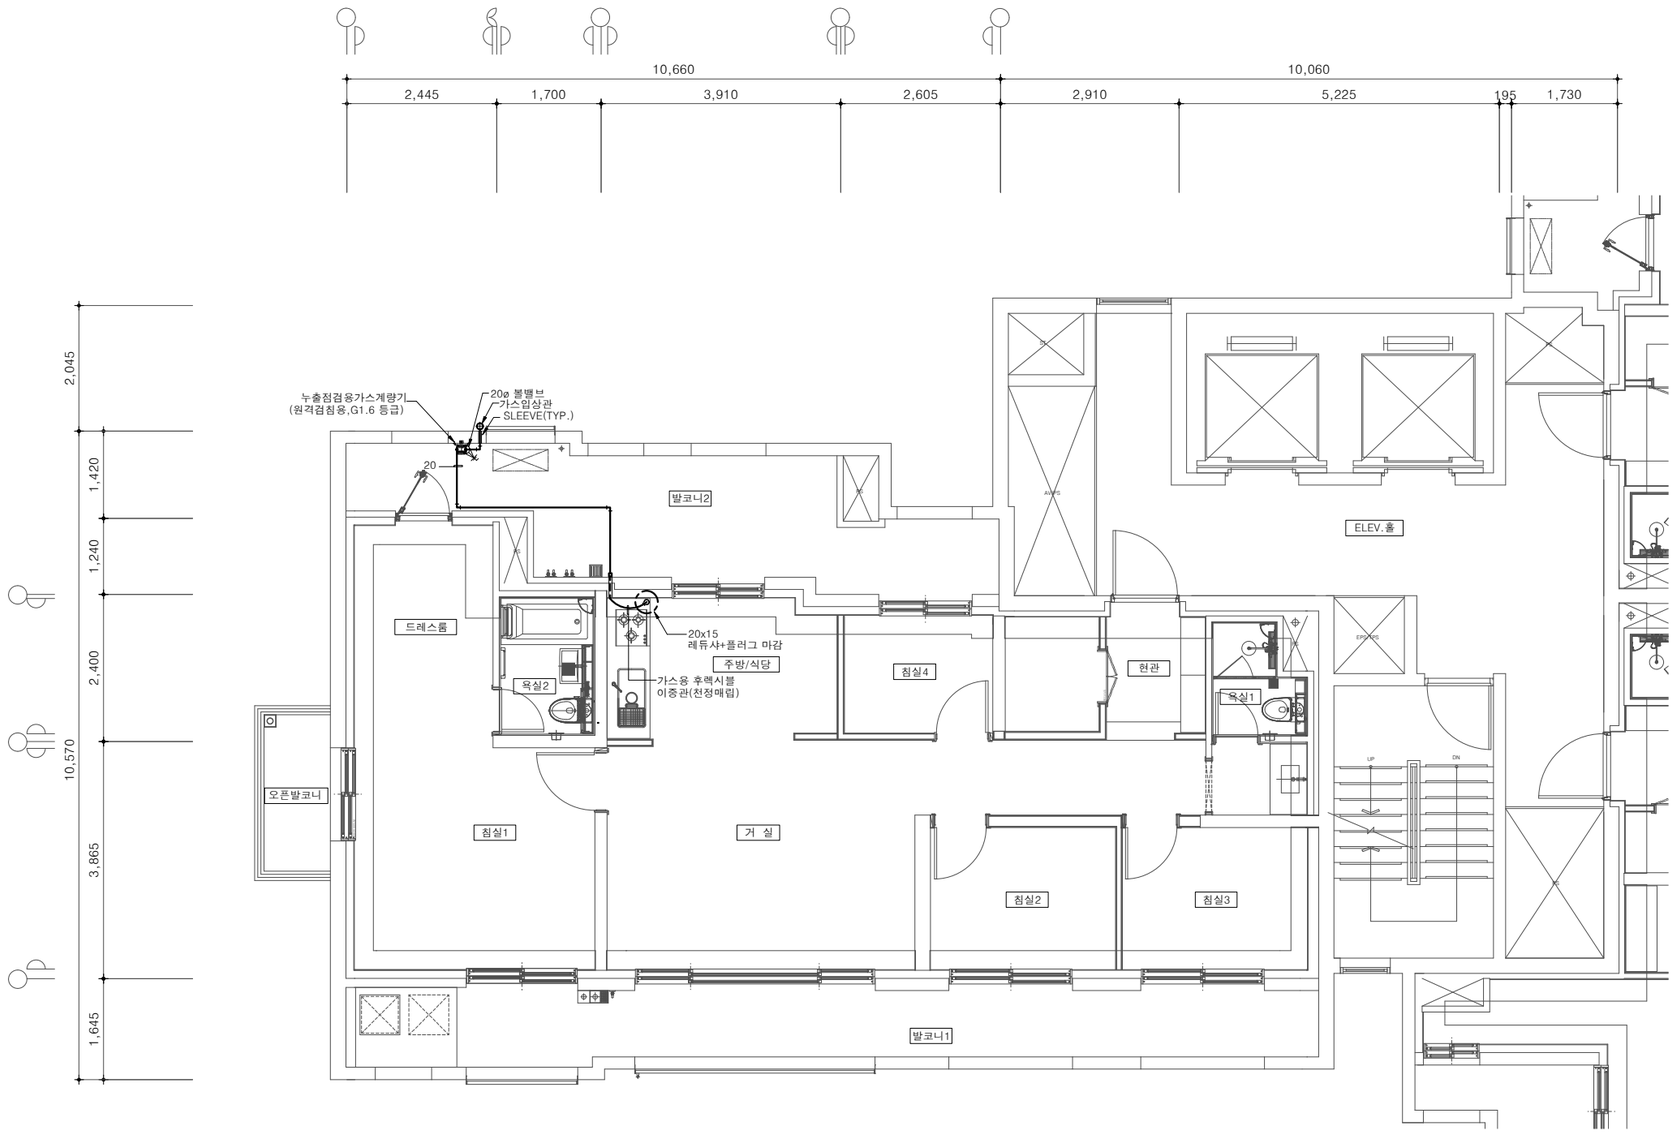

97m²B형 단위세대 가스배관 평면도(기본형)


축 척 : 1/100

경기주택도시공사
GYEONGGI HOUSING & URBAN DEVELOPMENT CORPORATION

설계명 PROJECT TITLE
화성동탄(2)A76-2BL 민간참여 공동주택사업
주기 NOTE

NO	DATE	REVISION DESCRIPTION	APPD

설 계 DESIGN	
대표전화	
축 척	SCALE
A1	1 / 50
A3	1 / 100
일 자 DATE	2025. 12.
설계번호 PROJECT NO.	AR - 23 - 026
도면화일명 DWG. FILE NAME	
도면번호 SHEET NO.	MG - 012
도면명 SUBJECT TITLE	97m²B형 단위세대 가스배관 평면도(기본형)

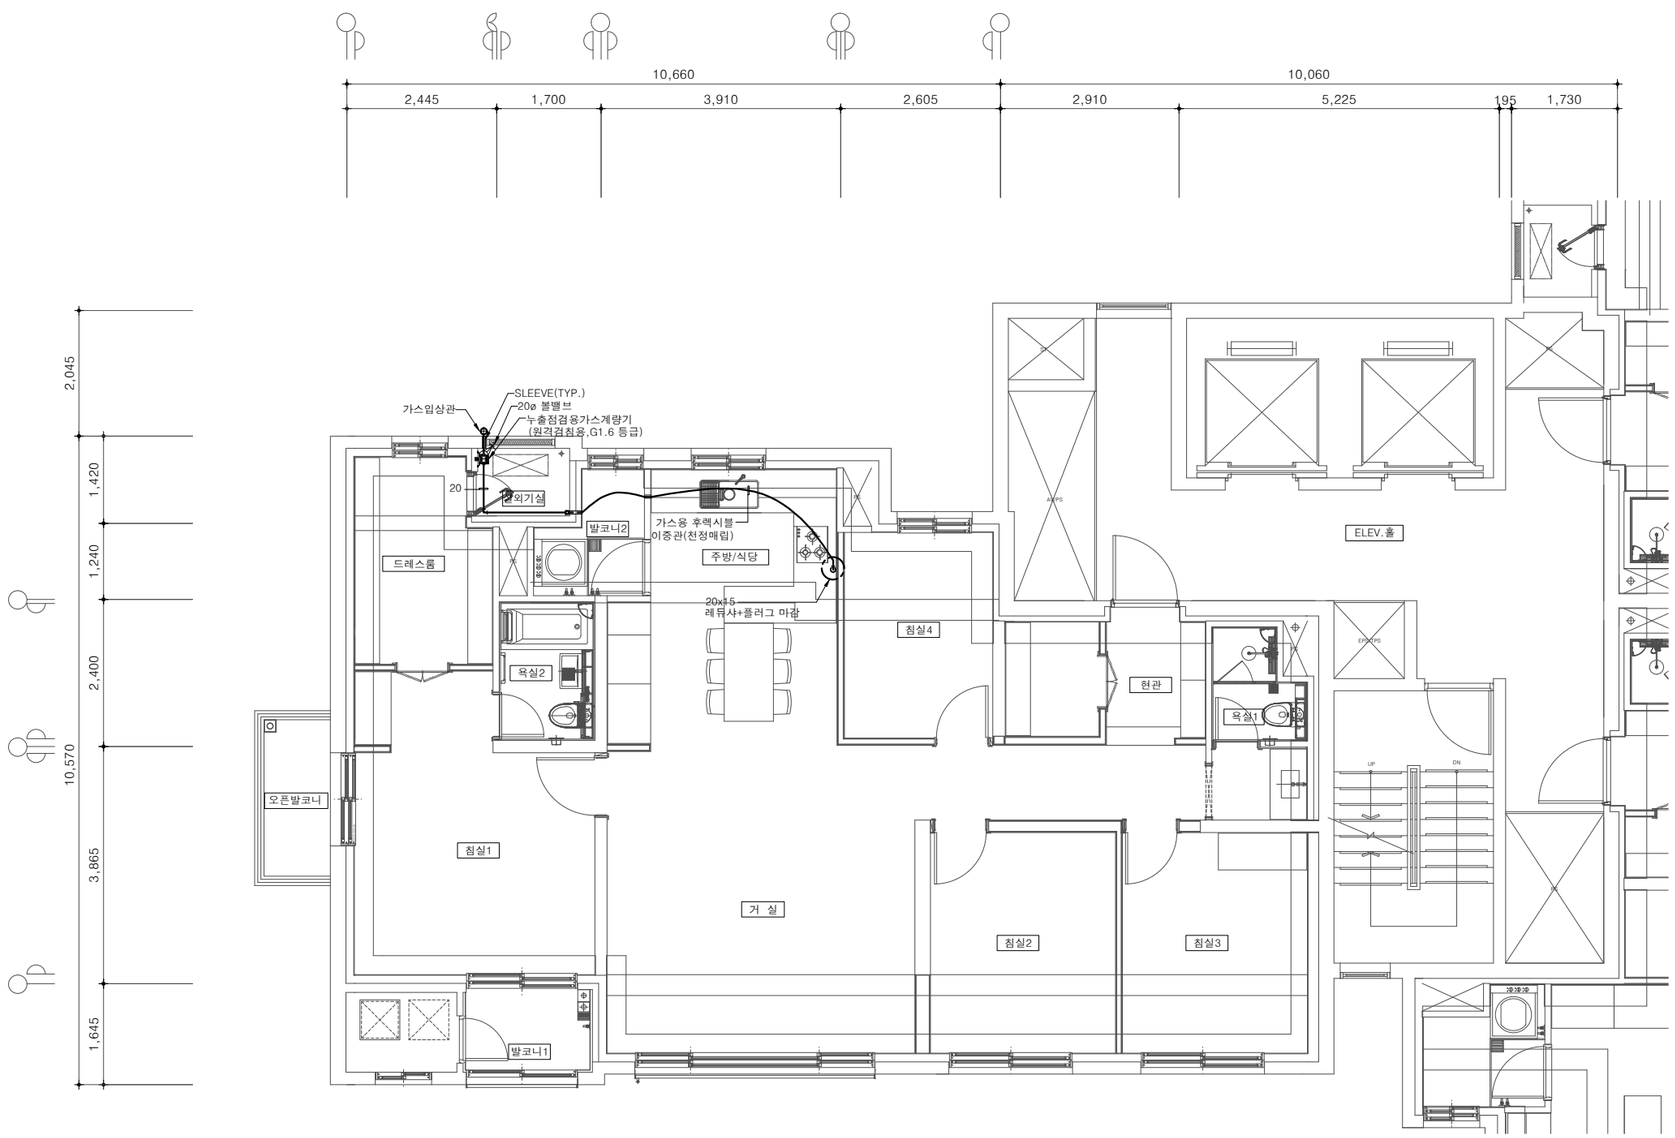

97m²B형 단위세대 가스배관 평면도(확장형)

축 척 : 1/100

경기주택도시공사
GYEONGGI HOUSING & URBAN DEVELOPMENT CORPORATION


설계명	PROJECT TITLE
화성동탄(2)A76-2BL 민간참여 공동주택사업	

주기 NOTE

NO	DATE	REVISION DESCRIPTION	APPD
△			
△			
△			
△			

설 계
DESIGN

대표전화	
축 척	SCALE
A1	1 / 50
A3	1 / 100
일 자 DATE	2025. 12.
설계번호 PROJECT NO.	AR - 23 - 026
도면화일명 DWG. FILE NAME	
도면번호 SHEET NO.	MG - 013
도면명 SUBJECT TITLE	97m²B형 단위세대 가스배관 평면도(확장형)

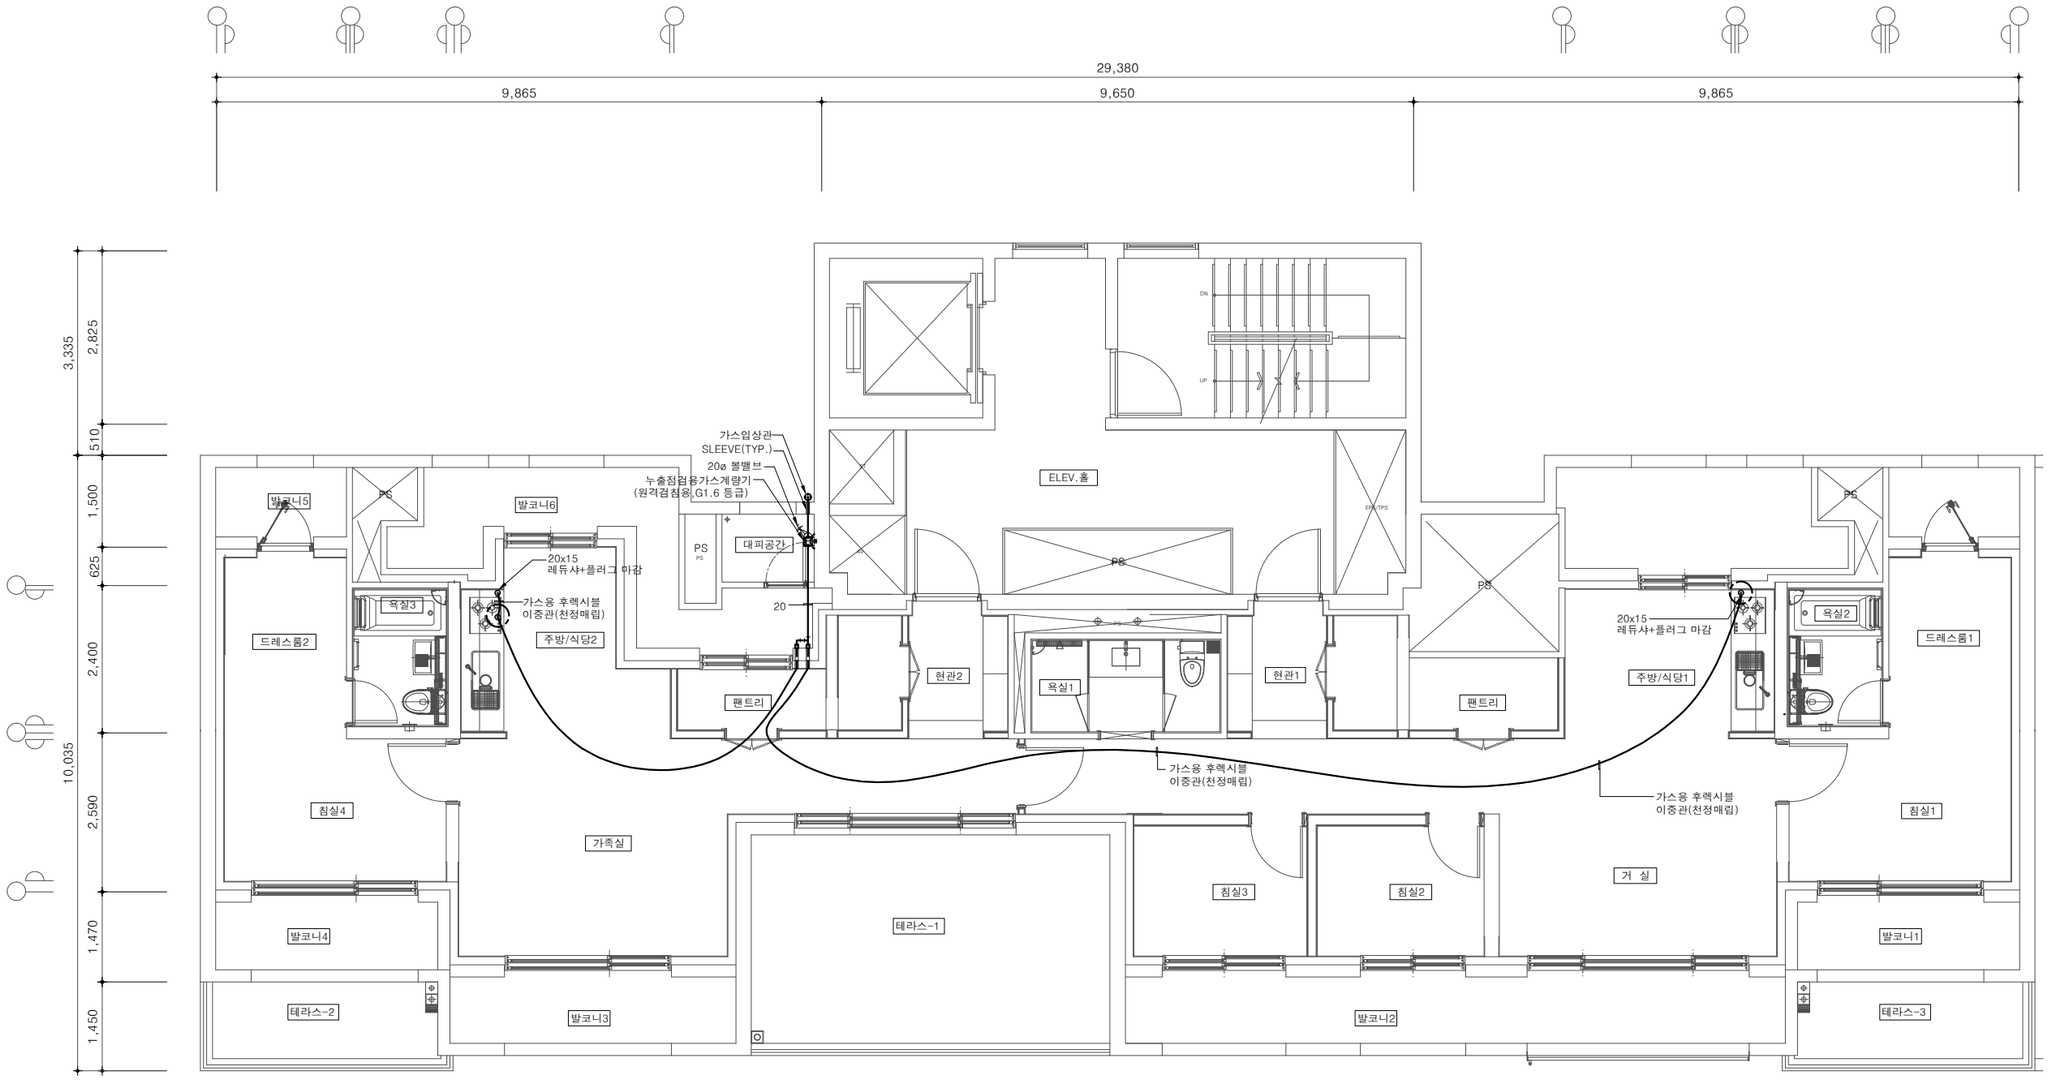

142m²P형 단위세대 가스배관 평면도(기본형)

축 척 : 1/100


경기주택도시공사
GYEONGGI HOUSING & URBAN DEVELOPMENT CORPORATION

설계명	PROJECT TITLE
화성동탄(2)A76-2BL 민간참여 공동주택사업	
주기	NOTE

NO	DATE	REVISION DESCRIPTION	APPD

설 계
DESIGN

대표전화	
축 척	SCALE
A1	1 / 50
A3	1 / 100
일 자	DATE
	2025. 12.
설계번호	PROJECT NO.
	AR - 23 - 026
도면화일명	DWG. FILE NAME
도면번호	SHEET NO.
	MG - 014
도면명	SUBJECT TITLE
	142m²A형 단위세대 가스배관 평면도(기본형)

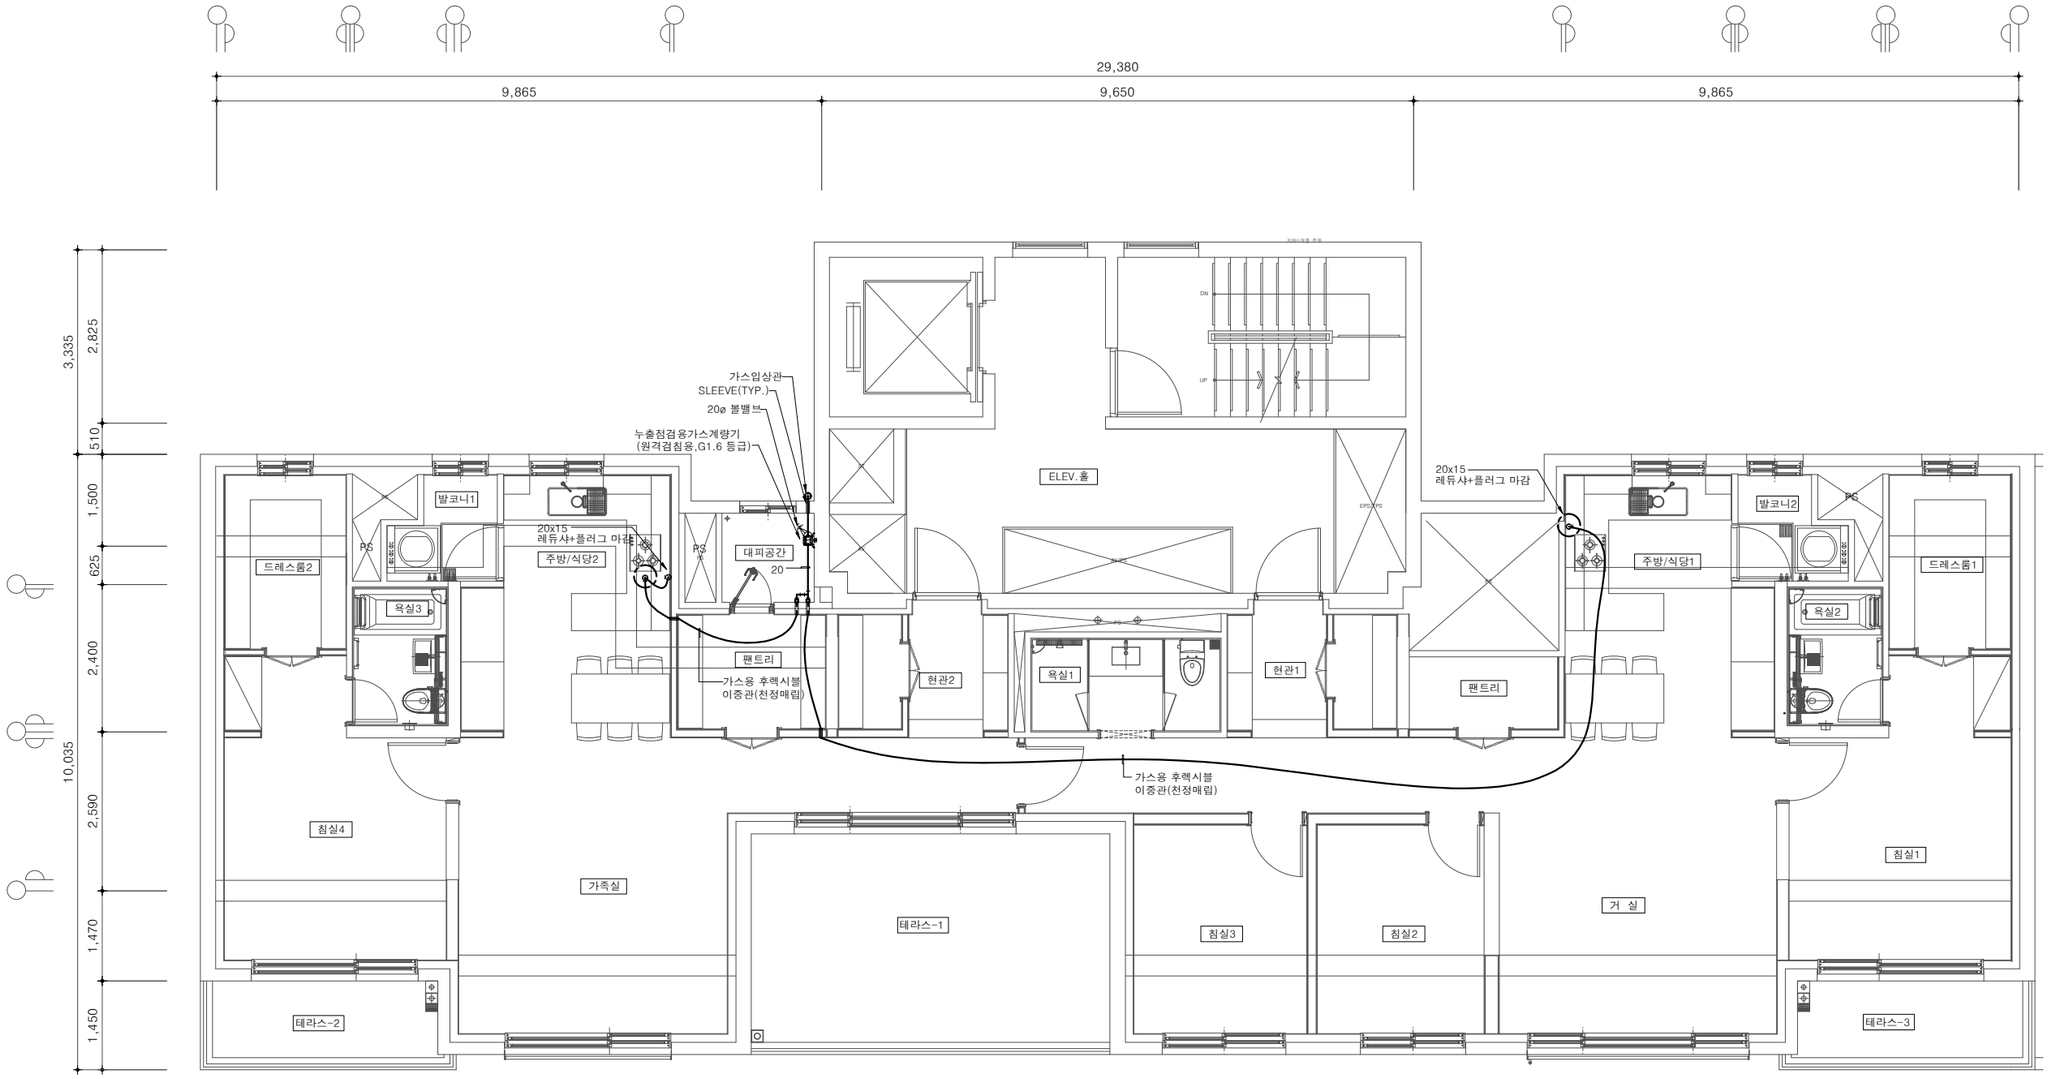

142m²9형 단위세대 가스배관 평면도(확장형)

축 척 : 1/100

경기주택도시공사
GYEONGGI HOUSING & URBAN DEVELOPMENT CORPORATION

설계명 PROJECT TITLE

화성동탄(2)A76-2BL
민간참여 공동주택사업

주기 NOTE

NO	DATE	REVISION DESCRIPTION	APPD
△			
△			
△			
△			
△			

설 계
DESIGN

대표전화

축 척	SCALE
A1	1 / 50
A3	1 / 100

일 자 DATE
2025. 12.

설계번호 PROJECT NO.
AR - 23 - 026

도면화일명 DWG. FILE NAME

도면번호 SHEET NO.
MG - 015

도면명 SUBJECT TITLE
142m²A형 단위세대
가스배관 평면도(확장형)

범 례 표

기 호	명 칭	비 고
D U C T		
	급 기 덕 트	SUPPLY AIR DUCT SECTION
	환 기 덕 트	RETURN AIR DUCT SECTION
	외 기 덕 트	FRESH AIR DUCT SECTION
	배 기 덕 트	EXHAUST AIR DUCT SECTION
V.D	풍 량 조 절 댐 퍼	VOLUME DAMPER
M.F.D	전 동 방 화 댐 퍼	MOTOR FIRE DAMPER
F.V.D	풍 량 조 절 및 방 화 댐 퍼	FIRE VOLUME DAMPER
M.V.D	전 동 풍 량 조 절 댐 퍼	MOTORIZED VOLUME DAMPER
B.D.D	역 류 방 지 댐 퍼	BACKDRAFT DAMPER
	캔 바 스 이 음	CANVAS DUCT CONNECTION
	후 렉 시 블 덕 트	FLEXIBLE DUCT
S.D	분 할 댐 퍼	SPLIT DAMPER
T.V	터 닝 베 인	TURNING VANE
	원 형 디 퓨 져	ROUND TYPE DIFFUSER
	각 형 디 퓨 져	SQUARE TYPE DIFFUSER
	레 지 스 터 및 그 릴	REGISTER OR GRILLE
	SLOT ,브 리 지 라 인 디 퓨 쟈	LINE TYPE DIFFUSER
V.D	덕 트 의 분 기	BRANCH SUPPLY OR RETURN
H V A C PIPING		
DHWS	지 역 난 방 중 온 수 공 급 관	DISTRICT HEATING WATER SUPPLY
DHWR	지 역 난 방 중 온 수 환 수 관	DISTRICT HEATING WATER RETURN
HWS	온 수 공 급 관	HEATING WATER SUPPLY
HWR	온 수 환 수 관	HEATING WATER RETURN
CHS	냉 온 수 공 급 관	CHILLED & HEATING WATER SUPPLY
CHR	냉 온 수 환 수 관	CHILLED & HEATING WATER RETURN
FCS	팬 코 일 공 급 관	FANCOIL UNIT WATER SUPPLY
FCR	팬 코 일 환 수 관	FANCOIL UNIT WATER RETURN
FCD	팬 코 일 배 수 관	FANCOIL UNIT WATER DRAIN
C D	장 비 배 수 관	EQUIPMENT DRAIN
E	팽 창 관	EXPANSION
R G	냉 매 가 스 관	REFRIGERANT GAS PIPE
R L	냉 매 액 관	REFRIGERANT LIQUID
PLUMBING		
CW	시 수 관	CITY WATER
●	급 수 관	DOMESTIC COLD WATER
●●	급 탕 관	DOMESTIC HOT WATER SUPPLY
●●●	환 탕 관	DOMESTIC HOT WATER RETURN

기 호	명 칭	비 고
D	배 수 관	DRAIN
S	오 수 관	SOIL
V	통 기 관	VENT
K D	주 방 배 수	KITCHEN DRAIN
L D	세 탁 배 수	LAUNDRY DRAIN
R D	우 수 배 수 관	ROOF DRAIN
P D	배 수 펌 프 관	PUMPING DRAIN
DWP	영 구 배 수 펌 프 관	DEWATERING PUMPING DRAIN
G	가 스 관	LOW PRESSURE GAS
F.D	바 닥 배 수 구	FLOOR DRAIN
C.O	소 제 구	CLEANOUT
F.C.O	바 닥 소 제 구	FLOOR CLEANOUT
R.D	옥 상 배 수 구	ROOF DRAIN
V.T.R	옥 상 통 기 구	VENT THRU ROOF
VALVE & OTHERS		
	게 이 트 밸 브	GATE VALVE
	글 로 브 밸 브	GLOBE VALVE
	체 크 밸 브	CHECK VALVE
	스 트 레 이 너	STRAINER
	버 터 플 라 이 밸 브	BUTTERFLY VALVE
	볼 밸 브	BALL VALVE
	플 렉 시 블 이 음 / 플 렉 시 블 콘 넥 타	FLEXIBLE JOINT
	신 축 이 음 쇠 (벨 로 우 즈 형 단 식)	EXPANSION JOINT (SINGLE TYPE)
	신 축 이 음 쇠 (벨 로 우 즈 형 복 식)	EXPANSION JOINT (DOUBLE TYPE)
	신 축 이 음 쇠 (루 프 형)	EXPANSION JOINT (LOOP TYPE)
	파 이 프 앙 카	PIPE ANCHOR
	바 란 싱 밸 브	BALANCING VALVE
	이 방 전 동 밸 브	2-WAY CONTROL VALVE
	ON-OFF 전 동 밸 브	MOTOR VALVE (ON/OFF 제어)
	차 압 밸 브	PRESSURE DIFFERENTIAL CONTROL VALVE
	솔 레 노 이 드 밸 브 (정 수 위 조 절 밸 브)	SOLENOID VALVE
	안 전 밸 브	SAFETY VALVE
	감 압 밸 브	PRESSURE REDUCING VALVE
	ON-OFF TYPE 복 합 밸 브	PRESSURE INDEPENDENT CHARACTERIZED CONTROL VALVE
GM	가 스 계 량 기	GAS METER
Ⓜ	유 량 계	FLOW METER
	90도 엘 보	90° ELBOW
	하 향 곡 관	ELBOW TURNED DOWN
	상 향 곡 관	ELBOW TURNED UP
	유 체 의 흐 름 방 향	DIRECTION OF FLOW
A.A.V	자 동 공 기 빼 기 밸 브	AUTOMATIC AIR VENT
W.H.C	수 격 방 지 기	WATER HAMMER CUSHION
P.G	온 도 계 및 압 력 계	THERMOMETER & PRESSURE GAUGE

경기주택도시공사
GYEONGGI HOUSING & URBAN DEVELOPMENT CORPORATION

설계명 PROJECT TITLE

화성동탄(2)A76-2BL
민간참여 공동주택사업

주기 NOTE

NO	DATE	REVISION DESCRIPTION	APPD

설 계
DESIGN

대표전화

축 척	SCALE
A1	1 / NONE
A3	1 / NONE

일 자 DATE
2025. 12.

설계번호 PROJECT NO.
AR - 23 - 026

도면화일명 DWG. FILE NAME

도면번호 SHEET NO.
M – 006

도면명 SUBJECT TITLE
범례표

장 비 일 람 표 - 1

열 교 환 기

※ KS규격이 있는 모든 펌프는 KS 인증제품 또는 KS에서 정한 효율(기준효율의 1.12배)이상 제품채택

장비 번호	수량	용 도	형 식	설치위치	용 량		유체	1 차 측				2 차 측				재 질	장비 번호	수량	형 식	유량	양정	접속구경		전동기		효율		예비	비 고
								입구온도	출구온도	유량	설계압력	입구온도	출구온도	유량	설계압력							흡 입	토 출	동 력	전 원	A	B		
					Mcal/h	kW		℃	℃	ℓ/min	kPa	℃	℃	ℓ/min	kPa	전열판				ℓ/min	m	mm	mm	kW	Ph-V-Hz	%	%		
HX-01	1set	공동주택 A1 ZONE 저층부(1F~12F), 부대시설 난방용	컴팩트형	B2F 기계실	1,280	1,489	온수	115	50	350	1,600	45	60	1,650	1,600	STS316	P-H1	3	인라인	580	24	125	125	3.7	3-380-60	-	-	-	가변속 제어, 교번 및 순차운전 적용
		공동주택 A1 ZONE 저층부(1F~12F) 급탕 재열용			319	371	온수	75	55	273	1,600	35	55	270	1,600	STS316	P-H7	2	인라인	108	6	40	40	0.75	3-380-60	-	-	1	기타 표준 부속품 일체 포함
		공동주택 A1 ZONE 저층부(1F~12F) 급탕 예열용			319	371	온수	55	35	270	1,600	15	35	268	1,600	STS316												
HX-02	1set	공동주택 A2 ZONE 저층부(1F~12F), 부대시설 난방용	컴팩트형	B2F 기계실	1,210	1,407	온수	115	50	360	1,600	45	60	1,480	1,600	STS316	P-H2	3	인라인	550	23	125	125	3.7	3-380-60	-	-	-	가변속 제어, 교번 및 순차운전 적용
		공동주택 A2 ZONE 저층부(1F~12F) 급탕 재열용			313	364	온수	75	55	267	1,600	35	55	265	1,600	STS316	P-H8	2	인라인	106	7	40	40	0.75	3-380-60	-	-	1	기타 표준 부속품 일체 포함
		공동주택 A2 ZONE 저층부(1F~12F) 급탕 예열용			313	364	온수	55	35	265	1,600	15	35	263	1,600	STS316												
HX-03	1set	공동주택 A ZONE 고층부(13F~25F) 난방용	컴팩트형	B2F 기계실	1,460	1,697	온수	115	50	400	1,600	45	60	1,650	1,600	STS316	P-H3	3	인라인	660	24	125	125	5.5	3-380-60	-	-	-	가변속 제어, 교번 및 순차운전 적용
		공동주택 A ZONE 고층부(13F~25F) 급탕 재열용			361	420	온수	75	55	308	1,600	35	55	305	1,600	STS316	P-H9	2	인라인	122	7	40	40	0.75	3-380-60	-	-	1	기타 표준 부속품 일체 포함
		공동주택 A ZONE 고층부(13F~25F) 급탕 예열용			361	420	온수	55	35	305	1,600	15	35	303	1,600	STS316												
HX-04	1set	공동주택 B ZONE 저층부(1F~12F), 부대시설 난방용	컴팩트형	B2F 기계실	1,310	1,523	온수	115	50	360	1,600	45	60	1,480	1,600	STS316	P-H4	3	인라인	600	23	125	125	3.7	3-380-60	-	-	-	가변속 제어, 교번 및 순차운전 적용
		공동주택 B ZONE 저층부(1F~12F) 급탕 재열용			344	400	온수	75	55	294	1,600	35	55	291	1,600	STS316	P-H10	2	인라인	117	7	40	40	0.75	3-380-60	-	-	1	기타 표준 부속품 일체 포함
		공동주택 B ZONE 저층부(1F~12F) 급탕 예열용			344	400	온수	55	35	291	1,600	15	35	289	1,600	STS316												
HX-05	1set	공동주택B ZONE 고층부(13F~25F) 난방용	컴팩트형	B2F 기계실	1,300	1,512	온수	115	50	350	1,600	45	60	1,470	1,600	STS316	P-H5	3	인라인	590	24	125	125	5.5	3-380-60	-	-	-	가변속 제어, 교번 및 순차운전 적용
		공동주택B ZONE 고층부(13F~25F) 급탕 재열용			342	398	온수	75	55	292	1,600	35	55	289	1,600	STS316	P-H11	2	인라인	116	7	40	40	0.75	3-380-60	-	-	1	기타 표준 부속품 일체 포함
		공동주택B ZONE 고층부(13F~25F) 급탕 예열용			342	398	온수	55	35	289	1,600	15	35	287	1,600	STS316												
HX-06	1set	사우나 급탕 재열용	컴팩트형	B2F 기계실	304	354	온수	75	55	260	1,600	35	55	257	1,600	STS316	P-H12	2	인라인	103	6	40	40	0.75	3-380-60	-	-	1	기타 표준 부속품 일체 포함
		사우나 급탕 예열용			304	354	온수	55	35	257	1,600	15	35	255	1,600	STS316												

열 회 수 형 환 기 장 치 (공 동 주 택)

장비 번호	수량	용 도	형 식	설치위치	풍량	정압	소비전력	전원	덕트 관경	전열교환 효율		비 고
										냉방	난방	
					㎥/h	Pa	W	Ph-V-Hz	mm	%	%	
HUV-01	1,521	84A~84D, 97A,97B 세대 환기용	전열교환	단위세대	150	100	66.0	1-220-60	125	45.0	70.0	기타 표준 부속품 일체 포함
HUV-02	6	142P 세대 환기용	전열교환	단위세대	200	100	105.0	1-220-60	200	45.0	70.0	기타 표준 부속품 일체 포함

열 회 수 환 기 장 치 (부 대 시 설)

※ 유효전열교환효율 냉방 : 45%, 난방 : 70%이상

장비 번호	수량	용 도	형 식	설치위치	풍 량	소비전력	정 압	전원	접속구경	비 고
					㎥/h	W	Pa	Ph-V-Hz	Ø	
HUV-03	18	부대시설 환기용	전열교환	당해실	150	55	71	1-220-60	150	기타 표준 부속품 일체 포함
HUV-04	21	부대시설 환기용	전열교환	당해실	250	92	71	1-220-60	150	기타 표준 부속품 일체 포함
HUV-05	6	부대시설 환기용	전열교환	당해실	350	134	100	1-220-60	150	기타 표준 부속품 일체 포함
HUV-06	10	부대시설 환기용	전열교환	당해실	500	178	100	1-220-60	200	기타 표준 부속품 일체 포함
HUV-07	8	부대시설 환기용	전열교환	당해실	800	270	100	1-220-60	250	기타 표준 부속품 일체 포함
HUV-08	5	부대시설 환기용	전열교환	당해실	1000	416	100	1-220-60	250	기타 표준 부속품 일체 포함

중 앙 수 처 리 장 치

장비 번호	수량	용 도	형 식	설치위치	처리량	재질	마이크로 필터	구경	규격		카본 필터	구경	규격		케미컬 피더	약품펌프 용량	약품펌프 동력	재질	약품탱크	CONTOL PANEL	재질	1차 전원	비 고
							필터카트리지		Ø	H	필터카트리지		Ø	H		cc/min	kw		lit				
					㎥/h			mm				mm											
WT-01	1	마이크로 필터+카본필터	VERTICAL	기계실	50	STS304	Ø63 x 500L x 5μ x50EA	100	650	1,000	Ø63 x 500L x 5μ x60EA	100	750	1,000		0~25	0.015	P.E	100		SS400	220V x 60Hz x 1PH x 0.1kw	CL SENSIR & METER 포함. 기타 표준부속품 일체포함

저 수 조

장비 번호	수량	용 도	형 식	설치위치	재 질	유효 용량	규 격			비 고
							가 로	세 로	높 이	
						㎥	mm	mm	mm	
T-01	1	위생 및 소화용수 공급용	각형	저수조실	내식성 자재	815	29.0	8.5	4.5	내진설계, 소방포함(53.2㎥) 보온 및 단열, 기타 표준 부속품 일체포함,

제 습 기

* 동등이상 제품 적용

장비 번호	수량	용 도	형식	설치위치	제습능력	풍 량	전동기		비 고
							소비전력	전 원	
					Liter/day	CMH	W	Ph-V-Hz	
DH- 01	51	ELEV. 홀 제습용	천정 매립형	B2F ELEV.홀	40	550	1.04	1-220-60	N.D 150mm 원형 디퓨저(필터삽입형/대우특허품) 2개소, 연결용 PVC 은박후렉시블 및 비상용 유선리모컨 설치 포함, 무선리모컨 제공 포함, 기타 표준부속품 일체포함

공 기 청 정 기

* 동등이상 제품 적용

장비 번호	수량	용 도	형식	설치위치	청정능력	풍 량	전동기		비 고
							소비전력	전 원	
					Liter/day	CMH	W	Ph-V-Hz	
AR- 01	84	ELEV. 홀 공기정화	천정 매립형	B2F ELEV.홀	-	-	-	1-220-60	기타 표준 부속품 일체 포함

경기주택도시공사
GYEONGGI HOUSING & URBAN DEVELOPMENT CORPORATION

설계명 PROJECT TITLE

화성동탄(2)A76-2BL
민간참여 공동주택사업

주기 NOTE
1. 설계기준 제품시방의 표기의의
도서상에 표기된 설계기준 제품
시방은 성능과 규격 등을 설계자가
설계기준을 하기 위한 참고자료이며,
특정제품의 사용을 권유하거나
유도하려는 의도는 아니다.
따라서 현장시공시 장비선정에
있어서 용량 및 효율이 설계의도대로
될 수 있는 제품을 선정하여야 한다.
다만, 제작회사에 따라 제품사양이
다소 차이는 있을 수 있으므로 타분야
(전기, 건축,구조)와 연계성을
고려하여 각각의 설비장비 뿐만
아니라, 전체 시스템이 요구성능
이상을 발휘할 수 있도록 선정하여야
한다.
또한 변경시에는 심의, 사업승인,
각종 인증 획득시 적용된 기준
이상이 되어야 한다.
2. 모든 진동 장비는 장비 발주시
방진 장치 포함 하여 발주 할것.
3. 0.75kW 이상 3상유도전동기는
최저소비 효율기준 이상 제품 적용

NO	DATE	REVISION DESCRIPTION	APPD

설 계
DESIGN

대표전화

축 척	SCALE
A1	1 / NONE
A3	1 / NONE

일 자 DATE
2025. 12.

설계번호 PROJECT NO.
AR - 23 - 026

도면화일명 DWG. FILE NAME

도면번호 SHEET NO.
M - 007

도면명 SUBJECT TITLE
장비일람표-1

장 비 일 람 표 - 2

송 풍 기

※전동기(0.7kW 이하 전동기)는 프리미엄기자재 인증제품 또는 최저효율기준 만족 제품 적용

장비 번호	수량	용 도	형 식	규 격	풍 량	정 압	전동기		방진		비 고
							소비전력	전원			
					㎥/h	Pa	kW	Ph-V-Hz	스프링	행거	
SF-01	9	지하2층 주차장 급기용	시 로 코	SS# 7.5	19,800	150	2.2	3-380-60	-	-	기타 표준 부속품 일체 포함
SF-02	3	지하1층 주차장 급기용	시 로 코	SS# 8	23,000	150	2.2	3-380-60	-	-	기타 표준 부속품 일체 포함
SF-03	1	지하2층 저수조실/기계실 급기용	인 라 인	Ø1,000	26,400	230	5.5	3-380-60	-	○	기타 표준 부속품 일체 포함
SF-04	1	지하2층 전기실 급기용	인 라 인	Ø650	11,400	200	2.2	3-380-60	-	○	기타 표준 부속품 일체 포함
SF-05	1	지하2층 발전기실 급기용	인 라 인	Ø450	4,700	190	1.5	3-380-60	-	○	기타 표준 부속품 일체 포함
SF-06A	1	지하1층 우수조실-1 급기용	인 라 인	Ø300	1,300	200	0.2	1-220-60	-	○	기타 표준 부속품 일체 포함
SF-06B	1	지하1층 우수조실-2 급기용	인 라 인	Ø300	700	190	0.2	1-220-60	-	○	기타 표준 부속품 일체 포함
SF-06C	1	지하1층 우수조실-3 급기용	인 라 인	Ø300	900	190	0.2	1-220-60	-	○	기타 표준 부속품 일체 포함
SF-06D	1	지하1층 우수조실-4 급기용	인 라 인	Ø250	900	190	0.2	1-220-60	-	○	기타 표준 부속품 일체 포함
SF-06E	1	지하1층 우수조실-5 급기용	인 라 인	Ø250	700	190	0.2	1-220-60	-	○	기타 표준 부속품 일체 포함
SF-06F	1	지하1층 우수조실-6 급기용	인 라 인	Ø300	900	190	0.2	1-220-60	-	○	기타 표준 부속품 일체 포함
SF-06G	1	지하1층 우수조실-7 급기용	인 라 인	Ø300	700	190	0.2	1-220-60	-	○	기타 표준 부속품 일체 포함
SF-06H	1	지하1층 우수조실-8 급기용	인 라 인	Ø300	1,100	200	0.2	1-220-60	-	○	기타 표준 부속품 일체 포함
SF-07	1	지하1층 근생 기계실 급기용	인 라 인	Ø450	3,000	190	0.75	3-380-60	-	○	기타 표준 부속품 일체 포함
SF-08	1	지하2층 사우나 기계실 급기용	인 라 인	Ø650	13,200	190	2.2	3-380-60	-	○	기타 표준 부속품 일체 포함
SF-09	1	재활용품 보관소 급기용	인 라 인	Ø350	1,800	200	0.4	1-220-60	-	○	기타 표준 부속품 일체 포함
SF-10	1	지하1층 사우나 샤워실-남자 급기용	인 라 인	Ø300	1,500	230	0.4	1-220-60	-	○	기타 표준 부속품 일체 포함
SF-11	1	지하1층 사우나 샤워실-여자 급기용	인 라 인	Ø300	1,500	230	0.4	1-220-60	-	○	기타 표준 부속품 일체 포함
BF-01	3,051	세대 화장실 배기용	천 정 형	200x200	80	40	0.03	1-220-60	-	-	기타 표준 부속품 일체 포함
EF-16	245	지하1~2층 기류유인용	기류유인팬	-	1,860	-	0.175	1-220-60	-	-	기타 표준 부속품 일체 포함

배 풍 기

※전동기(0.7kW 이하 전동기)는 프리미엄기자재 인증제품 또는 최저효율기준 만족 제품 적용

장비 번호	수량	용 도	형 식	규 격	풍 량	정 압	전동기		방진		비 고
							소비전력	전원			
					㎥/h	Pa	kW	Ph-V-Hz	스프링	행거	
EF-01	9	지하2층 주차장 배기용	시 로 코	DS# 5.5	19,800	150	2.2	3-380-60	-	-	기타 표준 부속품 일체 포함
EF-02	3	지하1층 주차장 배기용	시 로 코	DS# 5.5	23,000	150	2.2	3-380-60	-	-	기타 표준 부속품 일체 포함
EF-03	1	지하2층 저수조실/기계실 배기용	인 라 인	Ø800	26,400	230	5.5	3-380-60	-	○	기타 표준 부속품 일체 포함
EF-04	1	지하2층 전기실 배기용	인 라 인	Ø650	11,400	200	2.2	3-380-60	-	○	기타 표준 부속품 일체 포함
EF-05	1	지하2층 발전기실 배기용	인 라 인	Ø450	4,700	190	0.75	3-380-60	-	○	기타 표준 부속품 일체 포함
EF-06A	1	지하1층 우수조실-1 배기용	인 라 인	Ø300	1,300	200	0.2	1-220-60	-	○	기타 표준 부속품 일체 포함
EF-06B	1	지하1층 우수조실-2 배기용	인 라 인	Ø300	700	190	0.2	1-220-60	-	○	기타 표준 부속품 일체 포함
EF-06C	1	지하1층 우수조실-3 배기용	인 라 인	Ø300	900	190	0.2	1-220-60	-	○	기타 표준 부속품 일체 포함
EF-06D	1	지하1층 우수조실-4 배기용	인 라 인	Ø300	900	190	0.2	1-220-60	-	○	기타 표준 부속품 일체 포함
EF-06E	1	지하1층 우수조실-5 배기용	인 라 인	Ø250	700	190	0.2	1-220-60	-	○	기타 표준 부속품 일체 포함
EF-06F	1	지하1층 우수조실-6 배기용	인 라 인	Ø250	900	190	0.2	1-220-60	-	○	기타 표준 부속품 일체 포함
EF-06G	1	지하1층 우수조실-7 배기용	인 라 인	Ø300	700	190	0.2	1-220-60	-	○	기타 표준 부속품 일체 포함
EF-06H	1	지하1층 우수조실-8 배기용	인 라 인	Ø300	1,100	200	0.2	1-220-60	-	○	기타 표준 부속품 일체 포함
EF-07	1	지하1층 근생 기계실 배기용	인 라 인	Ø450	3,000	190	0.75	3-380-60	-	○	기타 표준 부속품 일체 포함
EF-08	1	지하2층 사우나 기계실 배기용	인 라 인	Ø350	1,200	190	0.2	1-220-60	-	○	기타 표준 부속품 일체 포함
EF-09	1	재활용품 보관소 배기용	인 라 인	Ø350	1,800	200	0.4	1-220-60	-	○	기타 표준 부속품 일체 포함
EF-10	1	지하1층 사우나 샤워실-남자 배기용	인 라 인	Ø300	1,500	230	0.4	1-220-60	-	○	기타 표준 부속품 일체 포함
EF-11	1	지하1층 사우나 샤워실-여자 배기용	인 라 인	Ø300	1,500	230	0.4	1-220-60	-	○	기타 표준 부속품 일체 포함
EF-12	42	주민공동시설 화장실 배기용	천 정 형	200x200	300	40	0.04	1-220-60	-	-	기타 표준 부속품 일체 포함
EF-13	9	주민공동시설 화장실 배기용	천 정 형	200x200	150	40	0.03	1-220-60	-	-	기타 표준 부속품 일체 포함
EF-14	10	근생시설 화장실 배기용	천 정 형	200x200	300	40	0.04	1-220-60	-	-	기타 표준 부속품 일체 포함
EF-15	34	ELEV 기계실 배기용	벽 부 형	350x350	1,100	40	0.04	1-220-60	-	-	기타 표준 부속품 일체 포함

펌 프

※ KS규격이 있는 모든 펌프는 KS 인증제품 또는 KS에서 정한 효율(기준효율의 1.12배)이상 제품채택

장비 번호	수량	용 도	형 식	설치위치	유 량	양 정	구 경		전 동 기		비상전원	예 비	효 율(%)		비 고
							흡 입	토 출							
					ℓ/min	m	mm	mm	kW	Ph-V-Hz			A효율	B효율	
P-01	1set (3대)	공동주택 A ZONE 저층부 급수 공급용	부 스 터	기 계 실	430 x 3	100	100	100	15.0 x 3	3 - 380 - 60	O	-	-	-	인버터제어, 압력탱크 및 컨트롤 패널 포함, 기타 표준부속품 일체포함
P-02	1set (3대)	공동주택 A ZONE 고층부 급수 공급용	부 스 터	기 계 실	330 x 3	140	100	100	15.0 x 3	3 - 380 - 60	O	-	-	-	인버터제어, 압력탱크 및 컨트롤 패널 포함, 기타 표준부속품 일체포함
P-03	1set (3대)	공동주택 B ZONE 저층부 급수 공급용	부 스 터	기 계 실	310 x 3	99	100	100	11.0 x 3	3 - 380 - 60	O	-	-	-	인버터제어, 압력탱크 및 컨트롤 패널 포함, 기타 표준부속품 일체포함
P-04	1set (3대)	공동주택 B ZONE 고층부 급수 공급용	부 스 터	기 계 실	310 x 3	140	100	100	15.0 x 3	3 - 380 - 60	O	-	-	-	인버터제어, 압력탱크 및 컨트롤 패널 포함, 기타 표준부속품 일체포함
P-05	2	기계실 배수용	수 중 형	기 계 실	400	21	-	100	3.7	3 - 380 - 60	O	-	-	-	교번 및 순차기동, 기타 표준부속품 일체포함
P-06	32	주차장 배수용(16개소)	수 중 형	지하주차장	200	17	-	80	1.5	3 - 380 - 60	O	-	-	-	교번 및 순차기동, 기타 표준부속품 일체포함
P-07	33	동 하부PIT 배수용(33개소)	수 중 형	동 PIT	100	14	-	65	0.75	3 - 380 - 60	-	-	-	-	기타 표준부속품 일체포함
P-08	39	ELEV. PIT 배수용(39개소)	수 중 형	ELEV. PIT	50	9	-	50	0.4	1 - 220 - 60	O	-	-	-	기타 표준부속품 일체포함
P-09	16	우수조 기계실 배수용(8개소)	수 중 형	우수조 펌프실	100	19	-	65	1.5	3 - 380 - 60	-	-	-	-	교번 및 순차기동, 기타 표준부속품 일체포함
P-10	2	근생기계실 배수용	수 중 형	근생기계실	200	15	-	80	1.5	3 - 380 - 60	-	-	-	-	교번 및 순차기동, 기타 표준부속품 일체포함
P-11	8set	조경용 급수 공급용(8개소)	부 스 터	우수조 펌프실	50 x 2	32	100	50	1.5 x 2	3 - 380 - 60	-	-	-	-	인버터제어, 압력탱크 및 컨트롤 패널 포함, 기타 표준부속품 일체포함
P-12	2	경사로 배수용(1개소)	수 중 형	지하주차장	300	18	-	80	2.2	3 - 380 - 60	O	-	-	-	교번 및 순차기동, 기타 표준부속품 일체포함
P-13	48	영구 배수용(24개소)	수 중 형	지하주차장	200	18	-	80	2.2	3 - 380 - 60	O	-	-	-	교번 및 순차기동, 기타 표준부속품 일체포함
P-14	1set (2대)	사우나 탕 배수 펌프	패키지 펌프	지하주차장	130	7	-	65	0.75 x 2	3 - 380 - 60	O	-	-	-	기타 표준부속품 일체포함
P-15	1set (2대)	사우나 배수 펌프	패키지 펌프	지하주차장	160	7	-	65	0.75 x 2	3 - 380 - 60	O	-	-	-	기타 표준부속품 일체포함
P-16	1set (2대)	피트니스 오수 펌프	패키지 펌프	지하주차장	50	7	-	50	0.2 x 2	1 - 220 - 60	O	-	-	-	기타 표준부속품 일체포함
P-17	1set (2대)	작은도서관 오수 펌프	패키지 펌프	지하주차장	120	7	-	65	0.4 x 2	3 - 380 - 60	O	-	-	-	기타 표준부속품 일체포함
P-18	10	부대시설 PIT 배수펌프(5개소)	수 중 형	부대시설 PIT	150	18	-	65	1.5	3 - 380 - 60	-	-	-	-	교번 및 순차기동, 기타 표준부속품 일체포함

팽 창 기 수 분 리 기

장비 번호	수량	용 도	형 식	설치위치	수 량	팽창탱크		기수분리기				배관접속구경(mm)			온수 온도 (°c)		비 고
						용량(LIT)	재질	최고운전압력(Kg/cm^2)	사용압력(Kg/cm^2)	동력(Kw)	전원(V/P/Hz)	보충수관	팽창관	환수관	최고	최저	
ET-01	1	HX-1 난방용 팽창기수분리기	BLADDER	기 계 실	1	1,000	SS400	6.2	5.2	1.1	3-380-60	32	32	32	60	10	기타 표준 부속품 일체포함, 보급수 감압밸브(10 -> 5.2 kg/cm²G) 포함
ET-02	1	HX-2 난방용 팽창기수분리기	BLADDER	기 계 실	1	1,000	SS400	6.2	5.2	1.1	3-380-60	32	32	32	60	10	기타 표준 부속품 일체포함, 보급수 감압밸브(10 -> 5.2 kg/cm²G) 포함
ET-03	1	HX-3 난방용 팽창기수분리기	BLADDER	기 계 실	1	1,000	SS400	9.4	8.4	1.1	3-380-60	32	32	32	60	10	기타 표준 부속품 일체포함, 보급수 감압밸브(14 -> 8.4 kg/cm²G) 포함
ET-04	1	HX-4 난방용 팽창기수분리기	BLADDER	기 계 실	1	1,000	SS400	6.2	5.2	1.1	3-380-60	32	32	32	60	10	기타 표준 부속품 일체포함, 보급수 감압밸브(9.9 -> 5.2 kg/cm²G) 포함
ET-05	1	HX-5 난방용 팽창기수분리기	BLADDER	기 계 실	1	1,000	SS400	9.4	8.4	1.1	3-380-60	32	32	32	60	10	기타 표준 부속품 일체포함, 보급수 감압밸브(14 -> 8.4 kg/cm²G) 포함

경기주택도시공사
GYEONGGI HOUSING & URBAN DEVELOPMENT CORPORATION

설계명 PROJECT TITLE

화성동탄(2)A76-2BL
민간참여 공동주택사업

주기 NOTE
1. 설계기준 제품시방의 표기의의 도서상에 표기된 설계기준 제품 시방은 성능과 규격 등을 설계자가 설계기준을 하기 위한 참고자료이며, 특정제품의 사용을 권유하거나 유도하려는 의도는 아니다. 따라서 현장시공시 장비선정에 있어서 용량 및 효율이 설계의도대로 될 수 있는 제품을 선정하여야 한다. 다만, 제작회사에 따라 제품사양이 다소 차이는 있을 수 있으므로 타분야(전기, 건축,구조)와 연계성을 고려하여 각각의 설비장비 뿐만 아니라, 전체 시스템이 요구성능 이상을 발휘할 수 있도록 선정하여야 한다.
또한 변경시에는 심의, 사업승인, 각종 인증 획득시 적용된 기준 이상이 되어야 한다.
2. 모든 진동 장비는 장비 발주시 방진 장치 포함 하여 발주 할것.
3. 0.75kW 이상 3상유도전동기는 최저소비 효율기준 이상 제품 적용

NO	DATE	REVISION DESCRIPTION	APPD
△			
△			
△			
△			

설 계 DESIGN

대표전화

축 척	SCALE
A1	1 / NONE
A3	1 / NONE
일 자	DATE
	2025. 12.
설계번호	PROJECT NO.
	AR - 23 - 026
도면화일명	DWG. FILE NAME
도면번호	SHEET NO.
	M - 008
도면명	SUBJECT TITLE
	장비일람표-2

장 비 일 람 표 - 3

전 기 방 열 기

장비 번호	수량	용 도	형 식	설치 위치	열량	최대 소비전력	전 원	비 고
					kcal/h	kW	Ph-V-Hz	
ER-01	11	관리사무소(1), 스카이라운지(2),근로자휴게실(2) 여성공동(2), 경비실(2), 티하우스(2) 화장실 동파방지용	벽부착형	당해실	860	1.0	1-220-60	타이머 부착 및 기타 표준 부속품 일체포함
ER-02	2	근린시설-1 화장실 동파방지용	천장형	당해실	430	0.5	1-220-60	타이머 부착 및 기타 표준 부속품 일체포함
ER-03	4	근린시설-2 화장실 동파방지용	천장형	당해실	860	2.0	1-220-60	타이머 부착 및 기타 표준 부속품 일체포함
ER-04	2	피트니스(2) 화장실 동파방지용	벽부착형	당해실	2,150	2.5	1-220-60	타이머 부착 및 기타 표준 부속품 일체포함
ER-05	4	작은도서관(2), 근린시설-2(2)화장실 동파방지용	벽부착형	당해실	2,580	3.0	1-220-60	타이머 부착 및 기타 표준 부속품 일체포함

전 기 온 수 기

과열방지기 및 기타표준부속품 일체포함

장비 번호	수량	용 도	형 식	설치위치	용 량	소비 전력	전 원	규 격			비 고
								가 로	세 로	높 이	
					Liter	kW	Ph-V-Hz	mm	mm	mm	
EHW-01	2	근린생활시설-1(2)	벽걸이형	당해실	15	1.5	1-220-60	360	300	360	
EHW-02	2	근린생활시설-2(2)	벽걸이형	당해실	30	2.5	1-220-60	360	300	360	

팬 코 일 유 니 트

기 호	수 량 (대)	형 식	송 풍 기			코 일								접 속 관 경(A)			비 고
			풍 량 (CMM)	전 원 (PH/V/Hz)	모 터 (W)	냉방능력 (kcal/h)	유 량 (LPM)	냉 수 (°C) 입 구	냉 수 (°C) 출 구	난방능력 (kcal/h)	유 량 (LPM)	온 수 (°C) 입 구	온 수 (°C) 출 구	입 구	출 구	배 수	
FCU-201	9	천정카세트형 (1-WAY)	5.7	1/220/60	25	-	-	-	-	2,720	4	60	45	20	20	20	기타표준부속품일체구비, 자동 ON/OFF 밸브포함 드레인 펌프 포함, 온도조절기 포함
FCU-202	57	천정카세트형 (4-WAY)	11.3	1/220/60	120	-	-	-	-	5,270	8	60	45	20	20	20	기타표준부속품일체구비, 자동 ON/OFF 밸브포함 드레인 펌프 포함, 온도조절기 포함

시스템 에어컨 실내기-피트니스, 관리사무소

장비번호	수량	형식	냉방 용량		난방 용량		팬			기외 정압	냉매	배관			전기 특성			비 고
							형식	풍량	출력			액관	가스관	드레인	소비 전력 (kW)		전원	
			(kW)	(kcal/h)	(kW)	(kcal/h)		(CMH)	(W)	(Pa)		(mm)	(mm)	(mm)	냉방	난방	Ph-V-Hz	
IAC- 01	2	1-Way	2.30	1980	-	-	Crossflow Fan	360.0	27	-	R410A	6.35	12.7	VP20	0.023	-	1 - 220 - 60	기타 표준 부속품 일체구비
IAC- 02	13	1-Way	5.20	4470	-	-	Crossflow Fan	720.0	54	-	R410A	6.35	12.7	VP20	0.059	-	1 - 220 - 60	기타 표준 부속품 일체구비
IAC- 03	10	4-Way	7.20	6190	-	-	Turbo Fan	1050.0	65	-	R410A	9.52	15.88	VP25	0.042	-	1 - 220 - 60	기타 표준 부속품 일체구비
IAC- 04	5	4-Way	8.30	7140	-	-	Turbo Fan	1320.0	65	-	R410A	9.52	15.88	VP25	0.050	-	1 - 220 - 60	기타 표준 부속품 일체구비
IAC- 05	26	4-Way	11.00	9460	-	-	Turbo Fan	1440.0	65	-	R410A	9.52	15.88	VP25	0.082	-	1 - 220 - 60	기타 표준 부속품 일체구비
IAC- 06	12	4-Way	14.50	12470	-	-	Turbo Fan	1740.0	97	-	R410A	9.52	15.88	VP25	0.099	-	1 - 220 - 60	기타 표준 부속품 일체구비

시스템 에어컨 실외기-피트니스, 관리사무소

장비번호	수량	형식	냉방 용량		난방 용량		압축기		팬		냉매	냉매 배관			전기 특성				비 고
							형식	출력	형식	풍량		액관	가스관	고압가스관	정격 소비 전력 (kW)			전원	
			(kW)	(kcal/h)	(kW)	(kcal/h)		(kW)		(CMH)		(mm)	(mm)	(mm)	냉방	난방	저온 난방 (-15℃)	Ph-V-Hz	
OAC-01	1	공랭식	11.00	9460	-	-	Twin BLDC Inv. Rotary	4.12	Propeller	4200	R410A	9.52	15.88	-	2.800	-	-	1 - 220 - 60	기타 표준 부속품 일체구비
OAC-02	1	공랭식	14.50	12470	-	-	Twin BLDC Inv. Rotary	4.12	Propeller	4200	R410A	9.52	15.88	-	3.900	-	-	3 - 380 - 60	기타 표준 부속품 일체구비
OAC-04	1	공랭식	23.00	19780	-	-	Twin BLDC Inv. Rotary	4.92	Propeller	8100	R410A	9.52	19.05	-	6.050	-	-	3 - 380 - 60	기타 표준 부속품 일체구비
OAC-08	1	공랭식	69.60	59850	-	-	SSC Scrollx2	6.67x2	Propeller	20340	R410A	15.88	34.92	-	17.580	-	-	3 - 380 - 60	기타 표준 부속품 일체구비
OAC-10	1	공랭식	78.40	67410	-	-	SSC Scrollx2	6.67x2	Propeller	20640	R410A	19.05	34.92	-	24.700	-	-	3 - 380 - 60	기타 표준 부속품 일체구비
OAC-11	1	공랭식	84.00	72230	-	-	SSC Scrollx2	8.93x2	Propeller	20640	R410A	19.05	34.92	-	28.300	-	-	3 - 380 - 60	기타 표준 부속품 일체구비
OAC-12	2	공랭식	107.40	92350	-	-	SSC Scrollx3	6.67x3	Propeller	9480 20640	R410A	19.05	41.28	-	31.670	-	-	3 - 380 - 60	기타 표준 부속품 일체구비
OAC-13	1	공랭식	113.20	97330	-	-	SSC Scrollx3	6.67x3	Propeller	11220 20640	R410A	19.05	41.28	-	32.700	-	-	3 - 380 - 60	기타 표준 부속품 일체구비
OAC-14	1	공랭식	117.60	101120	-	-	SSC Scrollx3	6.67x3	Propeller	12060 20640	R410A	19.05	41.28	-	34.400	-	-	3 - 380 - 60	기타 표준 부속품 일체구비

경기주택도시공사
GYEONGGI HOUSING & URBAN DEVELOPMENT CORPORATION

설계명 PROJECT TITLE

화성동탄(2)A76-2BL
민간참여 공동주택사업

주기 NOTE
1. 설계기준 제품시방의 표기의의
도서상에 표기된 설계기준 제품
시방은 성능과 규격 등을 설계자가
설계기준을 하기 위한 참고자료이며,
특정제품의 사용을 권유하거나
유도하려는 의도는 아니다.
따라서 현장시공시 장비선정에
있어서 용량 및 효율이 설계의도대로
될 수 있는 제품을 선정하여야 한다.
다만, 제작회사에 따라 제품사양이
다소 차이는 있을 수 있으므로 타분야
(전기, 건축,구조)와 연계성을
고려하여 각각의 설비장비 뿐만
아니라, 전체 시스템이 요구성능
이상을 발휘할 수 있도록 선정하여야
한다.
또한 변경시에는 심의, 사업승인,
각종 인증 획득시 적용된 기준
이상이 되어야 한다.
2. 모든 진동 장비는 장비 발주시
방진 장치 포함 하여 발주 할것.
3. 0.75kW 이상 3상유도전동기는
최저소비 효율기준 이상 제품 적용

NO	DATE	REVISION DESCRIPTION	APPD
△			
△			
△			
△			

설 계
DESIGN

대표전화

축 척	SCALE
A1	1 / NONE
A3	1 / NONE

일 자 DATE
2025. 12.

설계번호 PROJECT NO.
AR - 23 - 026

도면화일명 DWG. FILE NAME

도면번호 SHEET NO.
M - 009

도면명 SUBJECT TITLE
장비일람표-3

장 비 일 람 표 - 4

싱글 천장형 냉난방기-여성공동작업실

장비 번호	수량	형식	냉방 용량		난방 용량		냉매	배관			전기 특성					비 고
											소비 전력 (kW)				전원	
								액관	가스관	드레인	실내기		실외기			
			(kW)	(kcal/h)	(kW)	(kcal/h)		(mm)	(mm)	(mm)	냉방	난방	냉방	난방	Ph-V-Hz	
RAC- 02	2	4-Way	7.20	6190	-	-	R410A	6.35	15.88	-	2.170	-	2.170	-	1 - 220 - 60	기타 표준 부속품 일체구비

시스템 에어컨 실내기-티하우스

장비번호	수량	형식	냉방 용량		난방 용량		팬			기외 정압	냉매	배관			전기 특성			비 고
							형식	풍량	출력			액관	가스관	드레인	소비 전력 (kW)		전원	
			(kW)	(kcal/h)	(kW)	(kcal/h)		(CMH)	(W)	(Pa)		(mm)	(mm)	(mm)	냉방	난방	Ph-V-Hz	
IAC- 05	2	4-Way	11.00	9460	-	-	Turbo Fan	1440.0	65	-	R410A	9.52	15.88	VP25	0.082	-	1 - 220 - 60	기타 표준 부속품 일체구비

시스템 에어컨 실외기-티하우스

장비번호	수량	형식	냉방 용량		난방 용량		압축기		팬		냉매	냉매 배관			전기 특성				비 고
							형식	출력	형식	풍량		액관	가스관	고압가스관	정격 소비 전력 (kW)			전원	
			(kW)	(kcal/h)	(kW)	(kcal/h)		(kW)		(CMH)		(mm)	(mm)	(mm)	냉방	난방	저온 난방 (-15℃)	Ph-V-Hz	
OAC- 05	1	공랭식	29.00	24940	-	-	SSC Scroll	5.18	Propeller	11400	R410A	9.52	22.22	-	7.300	-	-	3 - 380 - 60	기타 표준 부속품 일체구비

시스템 에어컨 실내기-경로당

장비번호	수량	형식	냉방 용량		난방 용량		팬			기외 정압	냉매	배관			전기 특성			비 고
							형식	풍량	출력			액관	가스관	드레인	소비 전력 (kW)		전원	
			(kW)	(kcal/h)	(kW)	(kcal/h)		(CMH)	(W)	(Pa)		(mm)	(mm)	(mm)	냉방	난방	Ph-V-Hz	
IAC- 01	2	1-Way	2.30	1980	-	-	Crossflow Fan	360.0	27	-	R410A	6.35	12.7	VP20	0.023	-	1 - 220 - 60	기타 표준 부속품 일체구비
IAC- 02	2	1-Way	5.20	4470	-	-	Crossflow Fan	720.0	54	-	R410A	6.35	12.7	VP20	0.059	-	1 - 220 - 60	기타 표준 부속품 일체구비
IAC- 04	2	4-Way	8.30	7140	-	-	Turbo Fan	1320.0	65	-	R410A	9.52	15.88	VP25	0.050	-	1 - 220 - 60	기타 표준 부속품 일체구비

시스템 에어컨 실외기-경로당

장비번호	수량	형식	냉방 용량		난방 용량		압축기		팬		냉매	냉매 배관			전기 특성				비 고
							형식	출력	형식	풍량		액관	가스관	고압가스관	정격 소비 전력 (kW)			전원	
			(kW)	(kcal/h)	(kW)	(kcal/h)		(kW)		(CMH)		(mm)	(mm)	(mm)	냉방	난방	저온 난방 (-15℃)	Ph-V-Hz	
OAC- 06	1	공랭식	34.80	29920	-	-	SSC Scroll	6.67	Propeller	11220.0	R410A	12.7	28.58	-	10.600	10.800	15.700	3 - 380 - 60	기타 표준 부속품 일체구비

시스템 에어컨 실내기-게스트하우스

장비번호	수량	형식	냉방 용량		난방 용량		팬			기외 정압	냉매	배관			전기 특성			비 고
							형식	풍량	출력			액관	가스관	드레인	소비 전력 (kW)		전원	
			(kW)	(kcal/h)	(kW)	(kcal/h)		(CMH)	(W)	(Pa)		(mm)	(mm)	(mm)	냉방	난방	Ph-V-Hz	
IAC- 02	1	1-Way	5.20	4470	-	-	Crossflow Fan	720.0	54	-	R410A	6.35	12.7	VP20	0.059	-	1 - 220 - 60	기타 표준 부속품 일체구비
IAC- 03	1	4-Way	7.20	6190	-	-	Turbo Fan	1050.0	65	-	R410A	9.52	15.88	VP25	0.042	-	1 - 220 - 60	기타 표준 부속품 일체구비
IAC- 04	1	4-Way	8.30	7140	-	-	Turbo Fan	1170.0	65	-	R410A	9.52	15.88	VP25	0.050	-	1 - 220 - 60	기타 표준 부속품 일체구비

시스템 에어컨 실외기-게스트하우스

장비번호	수량	형식	냉방 용량		난방 용량		압축기		팬		냉매	냉매 배관			전기 특성				비 고
							형식	출력	형식	풍량		액관	가스관	고압가스관	정격 소비 전력 (kW)			전원	
			(kW)	(kcal/h)	(kW)	(kcal/h)		(kW)		(CMH)		(mm)	(mm)	(mm)	냉방	난방	저온 난방 (-15℃)	Ph-V-Hz	
OAC- 01	1	공랭식	11.00	9460	-	-	Twin BLDC Inv. Rotary	4.12	Propeller	4200.0	R410A	9.52	15.88	-	2.800	-	-	1 - 220 - 60	기타 표준 부속품 일체구비
OAC- 02	1	공랭식	14.50	12470	-	-	Twin BLDC Inv. Rotary	4.12	Propeller	4200.0	R410A	9.52	15.88	-	3.900	-	-	1 - 220 - 60	기타 표준 부속품 일체구비

경기주택도시공사
GYEONGGI HOUSING & URBAN DEVELOPMENT CORPORATION

설계명 PROJECT TITLE

화성동탄(2)A76-2BL
민간참여 공동주택사업

주기 NOTE

1. 설계기준 제품시방의 표기의의
도서상에 표기된 설계기준 제품
시방은 성능과 규격 등을 설계자가
설계기준을 하기 위한 참고자료이며,
특정제품의 사용을 권유하거나
유도하려는 의도는 아니다.
따라서 현장시공시 장비선정에
있어서 용량 및 효율이 설계의도대로
될 수 있는 제품을 선정하여야 한다.
다만, 제작회사에 따라 제품사양이
다소 차이는 있을 수 있으므로 타분야
(전기, 건축,구조)와 연계성을
고려하여 각각의 설비장비 뿐만
아니라, 전체 시스템이 요구성능
이상을 발휘할 수 있도록 선정하여야
한다.
또한 변경시에는 심의, 사업승인,
각종 인증 획득시 적용된 기준
이상이 되어야 한다.
2. 모든 진동 장비는 장비 발주시
방진 장치 포함 하여 발주 할것.
3. 0.75kW 이상 3상유도전동기는
최저소비 효율기준 이상 제품 적용

NO	DATE	REVISION DESCRIPTION	APPD
△			
△			
△			
△			

설 계
DESIGN

대표전화

축 척	SCALE
A1	1 / NONE
A3	1 / NONE

일 자 DATE
2025. 12.

설계번호 PROJECT NO.
AR - 23 - 026

도면화일명 DWG. FILE NAME

도면번호 SHEET NO.
M - 010

도면명 SUBJECT TITLE
장비일람표-4

장 비 일 람 표 - 5

시스템 에어컨 실내기-키즈스테이션-1

장비 번호	수량	형식	냉방 용량		난방 용량		냉매	배관			전기 특성					비 고
											소비 전력 (kW)				전원	
								액관	가스관	드레인	실내기		실외기			
			(kW)	(kcal/h)	(kW)	(kcal/h)		(mm)	(mm)	(mm)	냉방	난방	냉방	난방	Ph-V-Hz	
RAC- 01	1	4-Way	5.20	4470	-	-	R410A	6.35	12.7	-	1.640	-	1.640	-	1 - 220 - 60	기타 표준 부속품 일체구비

시스템 에어컨 실외기-키즈스테이션-2

장비 번호	수량	형식	냉방 용량		난방 용량		냉매	배관			전기 특성					비 고
											소비 전력 (kW)				전원	
								액관	가스관	드레인	실내기		실외기			
			(kW)	(kcal/h)	(kW)	(kcal/h)		(mm)	(mm)	(mm)	냉방	난방	냉방	난방	Ph-V-Hz	
RAC- 02	1	4-Way	7.20	6190	-	-	R410A	6.35	15.88	-	2.170	-	2.170	-	1 - 220 - 60	기타 표준 부속품 일체구비

시스템 에어컨 실내기-스카이라운지

장비번호	수량	형식	냉방 용량		난방 용량		팬			기외 정압	냉매	배관			전기 특성				비 고
							형식	풍량	출력			액관	가스관	드레인	소비 전력 (kW)		전원		
			(kW)	(kcal/h)	(kW)	(kcal/h)		(CMH)	(W)	(Pa)		(mm)	(mm)	(mm)	냉방	난방	Ph-V-Hz		
IAC- 05	2	4-Way	11.00	9460	-	-	Turbo Fan	1440.0	65	-	R410A	9.52	15.88	VP25	0.082	-	1 - 220 - 60		기타 표준 부속품 일체구비

시스템 에어컨 실외기-스카이라운지

장비번호	수량	형식	냉방 용량		난방 용량		압축기		팬		냉매	냉매 배관			전기 특성				비 고
							형식	출력	형식	풍량		액관	가스관	고압가스관	정격 소비 전력 (kW)			전원	
			(kW)	(kcal/h)	(kW)	(kcal/h)		(kW)		(CMH)		(mm)	(mm)	(mm)	냉방	난방	저온 난방 (-15℃)	Ph-V-Hz	
OAC- 05	1	공랭식	29.00	24940	-	-	SSC Scroll	5.18	Propeller	11400	R410A	9.52	22.22	-	7.300	-	-	3 - 380 - 60	기타 표준 부속품 일체구비

시스템 에어컨 실내기-어린이집

장비번호	수량	형식	냉방 용량		난방 용량		팬			기외 정압	냉매	배관			전기 특성				비 고
							형식	풍량	출력			액관	가스관	드레인	소비 전력 (kW)		전원		
			(kW)	(kcal/h)	(kW)	(kcal/h)		(CMH)	(W)	(Pa)		(mm)	(mm)	(mm)	냉방	난방	Ph-V-Hz		
IAC- 01	3	1-Way	2.30	1980	-	-	Crossflow Fan	360.0	27	-	R410A	6.35	12.7	VP20	0.023	-	1 - 220 - 60		기타 표준 부속품 일체구비
IAC- 02	5	1-Way	5.20	4470	-	-	Crossflow Fan	720.0	54	-	R410A	6.35	12.7	VP20	0.059	-	1 - 220 - 60		기타 표준 부속품 일체구비
IAC- 03	1	4-Way	7.20	6190	-	-	Turbo Fan	1050.0	65	-	R410A	9.52	15.88	VP25	0.042	-	1 - 220 - 60		기타 표준 부속품 일체구비
IAC- 04	2	4-Way	8.30	7140	-	-	Turbo Fan	1170.0	65	-	R410A	9.52	15.88	VP25	0.050	-	1 - 220 - 60		기타 표준 부속품 일체구비
IAC- 05	3	4-Way	11.00	9460	-	-	Turbo Fan	1440.0	65	-	R410A	9.52	15.88	VP25	0.082	-	1 - 220 - 60		기타 표준 부속품 일체구비
IAC- 06	2	4-Way	14.50	12470	-	-	Turbo Fan	1740.0	97	-	R410A	9.52	15.88	VP25	0.099	-	1 - 220 - 60		기타 표준 부속품 일체구비

시스템 에어컨 실외기-어린이집

장비번호	수량	형식	냉방 용량		난방 용량		압축기		팬		냉매	냉매 배관			전기 특성				비 고
							형식	출력	형식	풍량		액관	가스관	고압가스관	정격 소비 전력 (kW)			전원	
			(kW)	(kcal/h)	(kW)	(kcal/h)		(kW)		(CMH)		(mm)	(mm)	(mm)	냉방	난방	저온 난방 (-15℃)	Ph-V-Hz	
OAC- 07	1	공랭식	52.20	44880	-	-	SSC Scrollx2	6.67x2	Propeller	16920.0	R410A	15.88	28.58	-	11.300	-	-	3 - 380 - 60	기타 표준 부속품 일체구비
OAC- 09	1	공랭식	75.40	64830	-	-	SSC Scrollx2	6.67x2	Propeller	20640.0	R410A	19.05	34.92	-	20.900	-	-	3 - 380 - 60	기타 표준 부속품 일체구비

시스템 에어컨 실내기-경비실-1

장비번호	수량	형식	냉방 용량		난방 용량		팬			기외 정압	냉매	배관			전기 특성			비 고
							형식	풍량	출력			액관	가스관	드레인	소비 전력 (kW)		전원	
			(kW)	(kcal/h)	(kW)	(kcal/h)		(CMH)	(W)	(Pa)		(mm)	(mm)	(mm)	냉방	난방	Ph-V-Hz	
IAC- 01	1	1-Way	1.60	1380	1.80	1550	Crossflow Fan	288.0	27	-	R410A	6.35	12.7	VP20	0.019	0.019	1 - 220 - 60	기타 표준 부속품 일체구비
IAC- 02	1	1-Way	4.00	3440	4.50	3870	Crossflow Fan	480.0	27	-	R410A	6.35	12.7	VP20	0.035	0.037	1 - 220 - 60	기타 표준 부속품 일체구비

경기주택도시공사
GYEONGGI HOUSING & URBAN DEVELOPMENT CORPORATION

설계명 PROJECT TITLE

화성동탄(2)A76-2BL
민간참여 공동주택사업

주기 NOTE

1. 설계기준 제품시방의 표기의의
도서상에 표기된 설계기준 제품
시방은 성능과 규격 등을 설계자가
설계기준을 하기 위한 참고자료이며,
특정제품의 사용을 권유하거나
유도하려는 의도는 아니다.
따라서 현장시공시 장비선정에
있어서 용량 및 효율이 설계의도대로
될 수 있는 제품을 선정하여야 한다.
다만, 제작회사에 따라 제품사양이
다소 차이는 있을 수 있으므로 타분야
(전기, 건축,구조)와 연계성을
고려하여 각각의 설비장비 뿐만
아니라, 전체 시스템이 요구성능
이상을 발휘할 수 있도록 선정하여야
한다.
또한 변경시에는 심의, 사업승인,
각종 인증 획득시 적용된 기준
이상이 되어야 한다.
2. 모든 진동 장비는 장비 발주시
방진 장치 포함 하여 발주 할것.
3. 0.75kW 이상 3상유도전동기는
최저소비 효율기준 이상 제품 적용

NO	DATE	REVISION DESCRIPTION	APPD
△			
△			
△			
△			

설 계 DESIGN

대표전화

축 척	SCALE
A1	1 / NONE
A3	1 / NONE

일 자 DATE 2025. 12.

설계번호 PROJECT NO. AR - 23 - 026

도면화일명 DWG. FILE NAME

도면번호 SHEET NO. M - 011

도면명 SUBJECT TITLE

장비일람표-5

장 비 일 람 표 - 6

시스템 에어컨 실외기-경비실-1

장비번호	수량	형식	냉방 용량		난방 용량		압축기		팬		냉매	냉매 배관			정격 소비 전력 (kW)			전원	비 고
							형식	출력	형식	풍량		액관	가스관	고압가스관	냉방	난방	저온 난방 (-15℃)		
			(kW)	(kcal/h)	(kW)	(kcal/h)		(kW)		(CMH)		(mm)	(mm)	(mm)				Ph-V-Hz	
OAC- 01	1	공랭식	11.00	9460	12.4	10660	Twin BLDC Inv. Rotary	4.04	Propeller	5700.0	R410A	9.52	15.88	-	2.640	2.840	-	1 - 220 - 60	기타 표준 부속품 일체구비

싱글 천장형 냉난방기-경비실-2

장비 번호	수량	형식	냉방 용량		난방 용량		냉매	배관			전기 특성					비 고
								액관	가스관	드레인	소비 전력 (kW)				전원	
											실내기		실외기			
			(kW)	(kcal/h)	(kW)	(kcal/h)		(mm)	(mm)	(mm)	냉방	난방	냉방	난방	Ph-V-Hz	
RAC- 01	1	4-Way	3.20	2750	3.60	3100	R410A	6.35	9.52	-	0.920	1.020	0.920	1.020	1 - 220 - 60	기타 표준 부속품 일체구비

위 생 기 구 일 람 표 (공동주택)

※ [수도법] 제15조 및 [수도법시행규칙] 제1조의 2, 별표2에 따른 절수형 설비 설치

장비 번호	품 명	규 격	수 량 (타입별)								합 계	비 고
			84A	84B	84C	84D	97A	97B	142			
WC-1	양변기(세대용)	모델하우스 기준 제품 동일	1,334	632	28	228	772	28	9		2,031	기타 표준 부속품 일체 구비 [수도법] 제15조 및 [수도법시행규칙] 제6조에 따른 절수형 설비 설치
LA-1	세면기(세대용)	모델하우스 기준 제품 동일	1,334	632	28	228	772	28	9		2,031	기타 표준 부속품 일체 구비
BT-1	욕 조(세대용)	모델하우스 기준 제품 동일	677	316	14	114	386	14	6		1,527	기타 표준 부속품 일체 구비
SH-1	샤워용 혼합수전(세대용)	모델하우스 기준 제품 동일	677	316	14	114	386	14	3		1,524	기타 표준 부속품 일체 구비 [수도법] 제15조 및 [수도법시행규칙] 제6조에 따른 절수형 설비 설치
JS-1	씽크혼합수전(세대용)	모델하우스 기준 제품 동일	677	316	14	114	386	14	6		1,527	기타 표준 부속품 일체 구비 [수도법] 제15조 및 [수도법시행규칙] 제6조에 따른 절수형 설비 설치
FA-1	세탁수전(세대용)	모델하우스 기준 제품 동일	1,334	632	28	228	772	28	12		2,034	기타 표준 부속품 일체 구비
-	욕조 혼합수전(세대용)	모델하우스 기준 제품 동일	677	316	14	114	386	14	6		1,527	기타 표준 부속품 일체 구비 [수도법] 제15조 및 [수도법시행규칙] 제6조에 따른 절수형 설비 설치
-	세면기 혼합수전(세대용)	모델하우스 기준 제품 동일	1,334	632	28	228	772	28	9		2,031	기타 표준 부속품 일체 구비 [수도법] 제15조 및 [수도법시행규칙] 제6조에 따른 절수형 설비 설치
-	손빨래 수전 (세대용)	모델하우스 기준 제품 동일	1,334	632	28	228	772	28	12		2,034	기타 표준 부속품 일체 구비
-	화초 수전 (세대용)	모델하우스 기준 제품 동일	677	316	14	114	386	14	6		1,527	스프레이건, 호스 포함

위 생 기 구 일 람 표 (부대복리시설)

※ [수도법] 제15조 및 [수도법시행규칙] 제1조의 2, 별표2에 따른 절수형 설비 설치

명 칭	수 량	구 분																비 고
		어린이집	경로당	작은도서관	관리사무소	근로자휴게실	돌봄	사우나	피트니스	게스트	스카이라운	여성공동-1	여성공동-2	티하우스	경비실-1	경비실-2	근린생활시설-1	근린생활시설-2	
양변기(F.V)	10	-	-	-	-	-	-	-	10	-	-	-	-	-	-	-	-	-	기타표준부속품 일체포함
양변기(L.T)	22	-	-	4	1	2	-	2	-	2	-	1	1	2	1	1	-	5	기타표준부속품 일체포함
양변기(장애인용)	16	2	2	2	-	-	2	-	2	-	2	-	-	-	-	-	2	2	기타표준부속품 일체포함
양변기(유아용)	13	6	-	-	-	-	7	-	-	-	-	-	-	-	-	-	-	-	기타표준부속품 일체포함
소변기(일반)	7	-	-	1	-	-	-	-	3	-	-	-	-	1	-	-	-	2	기타표준부속품 일체포함
소변기(장애인용)	7	-	1	1	-	-	1	-	1	-	1	-	-	-	-	-	1	1	기타표준부속품 일체포함
소변기(유아용)	8	6	-	-	-	-	2	-	-	-	-	-	-	-	-	-	-	-	기타표준부속품 일체포함
세면기(원형)	22	-	-	8	-	-	2	2	4	-	-	-	-	-	-	-	-	6	기타표준부속품 일체포함, 마블 및 화장경은 건축공사분
세면기(각형)	14	-	1	-	1	2	-	2	-	2	-	1	1	2	1	1	-	-	기타표준부속품 일체포함, 화장경은 건축공사분
세면기(장애인용)	9	2	1	-	-	-	2	-	-	-	2	-	-	-	-	-	2	-	기타표준부속품 일체포함, 화장경은 건축공사분
세면기(유아용)	8	4	-	-	-	-	4	-	-	-	-	-	-	-	-	-	-	-	기타표준부속품 일체포함, 화장경은 건축공사분
청소 씽크	3	-	-	-	-	-	-	-	-	-	-	-	-	-	-	-	1	2	기타표준부속품 일체포함
세면기 혼합수전	51	6	2	8	1	2	8	-	6	2	2	1	1	2	1	1	2	6	**기타표준부속품 일체포함**
샤워용 혼합수전	34	-	-	-	1	2	-	32	-	2	-	-	-	-	-	-	-	-	**기타표준부속품 일체포함**
주방씽크 혼합수전	6	1	1	-	1	-	1	-	-	2	-	-	-	-	-	-	-	-	**기타표준부속품 일체포함**

경기주택도시공사
GYEONGGI HOUSING & URBAN DEVELOPMENT CORPORATION

설계명 PROJECT TITLE

화성동탄(2)A76-2BL
민간참여 공동주택사업

주기 NOTE

1. 설계기준 제품시방의 표기의의
도서상에 표기된 설계기준 제품
시방은 성능과 규격 등을 설계자가
설계기준을 하기 위한 참고자료이며,
특정제품의 사용을 권유하거나
유도하려는 의도는 아니다.
따라서 현장시공시 장비선정에
있어서 용량 및 효율이 설계의도대로
될 수 있는 제품을 선정하여야 한다.
다만, 제작회사에 따라 제품사양이
다소 차이는 있을 수 있으므로 타분야
(전기, 건축,구조)와 연계성을
고려하여 각각의 설비장비 뿐만
아니라, 전체 시스템이 요구성능
이상을 발휘할 수 있도록 선정하여야
한다.
또한 변경시에는 심의, 사업승인,
각종 인증 획득시 적용된 기준
이상이 되어야 한다.
2. 모든 진동 장비는 장비 발주시
방진 장치 포함 하여 발주 할것.
3. 0.75kW 이상 3상유도전동기는
최저소비 효율기준 이상 제품 적용

NO	DATE	REVISION DESCRIPTION	APPD
△			
△			
△			
△			

설 계
DESIGN

대표전화

축 척	SCALE
A1	1 / NONE
A3	1 / NONE

일 자 DATE
2025. 12.

설계번호 PROJECT NO.
AR - 23 - 026

도면화일명 DWG. FILE NAME

도면번호 SHEET NO.
M - 011-1

도면명 SUBJECT TITLE
장비일람표-6

■ 범 례 표

기 호	내 용	비 고
	게 이 트 밸 브	
	개 폐 표 시 형 밸 브 (OS & Y 형) - 탬퍼스위치부착형	
	스 모 렌 스 키 체 크 밸 브	
	스 트 레 이 너	
	후 렉 시 블 튜 브	
	릴 리 이 프 밸 브	
	소 방 유 량 계 (후루셀형)	
	수 격 방 지 기	
	플 랜 지	
	앵 글 밸 브	
소	ABC 일반소화기(3.3kg)	
d	ABC 일반소화기(1.5kg)	
자	자동식 소화기	
확	자동확산소화기(3.0kg)	
청	청정 소화기(2.5kg)	
완	완강기	
M	공기안전매트	
	옥내소화전(전용)	
	옥내소화전(단구형 방수구 겸용)	
	방수기구함(지하 수평거리 25m기준, 지상 수평거리 50m 기준)	
	연결송수구(쌍구형)	
	상수도소화전	
	알람밸브	
	프리액션밸브	
	스프링클러 헤드 (하향식 105℃)	
	스프링클러 헤드 (상하향식 72℃)	
	스프링클러 헤드 (하향식 72℃)	
	스프링클러 헤드 (상하향식 105℃)	
	스프링클러 헤드 (측벽형 헤드 72℃)	
	스프링클러 헤드 (상하향식 93℃)	
	스프링클러 헤드 (상하향식 68℃)	
	스프링클러 헤드 (상향식 72℃)	
	습식 사이트글라스	
M.V.D	전실제연설비(급기/복합댐퍼)	
M.D.	전실제연설비(배출)	
— H —	옥내소화전 배관	
— SP —	스프링클러 배관	
— LF —	옥내소화전, 스프링클러 겸용 배관 (저층부)	
— HF —	옥내소화전, 스프링클러 겸용 배관 (고층부)	
— SC —	연결송수관설비 배관	
— D —	드레인 배관	

■ 주 기 사 항

1. 소화설비의 공사는 국가 화재안전기준(NFSC)에 따른다.
2. 노출되는 소화수 배관의 재질은 배관용 탄소강관(KS D 3507), 배관내압이 1.2Mpa 이상일 경우에는 압력배관용 탄소강관(KS D 3562) 또는 이와 동등 이상의 것을 적용한다.
3. 기계설비 저수조와 겸용하는 소화펌프 1차측 배관은 KS D 3576(STS)을 적용한다.
4. 소화수가 공급되는 모든 배관에는 무단조작 감시스위치를 설치한다.
5. 배관 및 덕트가 방화구획 및 바닥을 관통할 시에는 내화충전구조로 내화구조의 성능기준과 고시기준에 적합한 구조로 처리한다.
6. 스프링클러헤드는 하향식의 경우 천정재에서 분리되어서는 안되며, 상향식의 경우 디플렉터를 상부슬라브에서 300mm이내에 설치한다.
7. 전기실・발전기실등 전기 관련시설에는 청정소화약제 소화기를 설치한다.
8. 적용하는 소방자재는 한국소방산업기술원의 승인을 득한 제품을 사용한다.
9. 별도의 표기가 없는 길이의 단위는 mm 이다.
10. 옥내소화전 노즐선단의 압력이 0.7MPa 이상인 경우 감압 오리피스를 설치한다.
11. 상부에 설치된 헤드의 방출수에 의해 감열부에 영향을 받을 우려가 있는 헤드에는 차폐판을 설치한다.
12. 습식배관에서 동파의 우려가 있는 장소에는 배관보온 및 동파방지설비를 설치한다.
13. 공조실, 주차장등에 설치되는 덕트의 폭이 1.2미터 이상이거나 살수에 장애가 생길때 에는 그 하부에 스프링클러 헤드를 추가 설치한다.
14. 천정과 반자사이의 벽이 불연재료이고 천정과 반자사이의 거리가 2m 이상인 경우 스프링클러 헤드는 상하향식으로 설치한다.
15. 천정과 반자 중 한쪽이 불연재료이고 천정과 반자사이의 거리가 1m 이상인 경우 스프링클러 헤드는 상하향식으로 설치한다.
16. 준비작동식 스프링클러설비의 하향식헤드는 드라이팬던트 타입을 적용한다.
17. 주방, 보일러실 등 화기를 취급하는 장소에 스프링클러 헤드 설치시 감지온도는 105°C형을 설치한다.
18. 피트 공간에 1제곱미터 이하의 크기에 갑종방화문 이상의 재질로 4곳 이상의 볼트조임 구조로 완전하게 구획한 경우와 완전구획을 한 경우에는 스프링클러 헤드를 제외하고, 그 이외의 피트 공간은 스프링클러 헤드를 설치한다.
19. PD 및 EPS/TPS내 소방시설 적용기준
    1) PD내 배관등을 제외한 공간이 가로 1.2m, 세로 1.2m, 높이 1.2m를 초과할 경우에는 스프링클러 헤드를 설치하고 그 이하일 경우에는 제외한다.
    2) 가로 1.2m, 세로 1.2m, 높이 1.2m를 초과하는 전기시설이 설치되어있는 EPS/TPS 등의 장소에는 자동소화장치를 설치하고 그 이하일 경우에는 제외한다.
20. 소화배관은 다른 설비의 배관과 쉽게 구분이 될 수 있도록 그 배관 표면 또는 배관 보온재 색상은 [한국산업표준(배관계의 식별 표시, KS A 0503)] 또는 적색으로 식별이 가능하도록 소방용설비의 배관임을 표시한다.
21. 가압송수장치는 자동으로 정지하지 아니하도록 한다.
22. 특별피난계단 부속실 및 비상용승강기 승강장에 설치되는 급기댐퍼는 자동차압 과압조절댐퍼를 사용한다.
23. 화재시 전실 급기댐퍼는 전층이 열리는 구조로하며, 배출댐퍼는 화재층만 열리는 구조로 한다.
24. 제연설비는 설계목적이 적합한지 사전에 검토하고 건물의 모든 부분을 완성하는 시점부터 시험 등 (확인, 측정 및 조정)을 화재안전기준에서 정하는 기준에 따라 실시한다.
25. 제연설비의 외기취입구는 연기 또는 공해물질등으로 오염된 공기가 유입되지 않도록 한다.
26. 지하 주차장 노출 배관에는 라인마크를 설치하여 유수의 흐름방향 등을 확인 할 수 있도록 한다.
27. 시공자는 현장 설치 도면을 작성 후 감독관 및 소방감리자의 승인을 득한 후 시공하여야 한다.
28. 금회 공사되는 모든 소화설비 자재는 감독관 및 소방감리자의 승인을 받아야 한다.

[심의 및 소방서 협의 사항]

1. 전기차 충전구역 스프링클러 헤드 방수량 증대 (k-factor 115 이상 설치)
   인근에 질식 소화포 (차량용) 비치
2. 세대 내 C-PVC(비보온)을 제외한 소방 배관의 보온은 난연성능의 배관 보온재와 보온 필름의 재질로 시공 한다.

설계명 PROJECT TITLE

화성동탄(2)A76-2BL
민간참여 공동주택사업

주기 NOTE

NO	DATE	REVISION DESCRIPTION	APPD
△			
△			
△			
△			

설계 DESIGN

파트장
본부장
PM
담당

대표전화

축 척	SCALE
A1	1 / NONE
A3	1 / NONE

일 자 DATE
2025. 12.

설계번호 PROJECT NO.
AR - 23 - 026

도면화일명 DWG. FILE NAME

도면번호 SHEET NO.
MF - 004

도면명 SUBJECT TITLE
범례표 및 주기사항

장 비 일 람 표-1

■ 소 화 펌 프

장비번호	수량	명 칭		설치위치	형 식	구경(mm)		유 량	양 정	MOTOR				비상전원	비 고
						흡입	토출	ℓ/min	m	kW	Ph	V	Hz		
FP 01	1	공동주택용	옥내소화전 주 펌프	지하 2층 펌프실	횡형다단	65	50	260	120	15	3	380	60	○	방진장치, 내진장치 및 기타 표준 부속품 일체 포함 KS 규격에서 정해진 효율 이상의 제품
FP 02	1		옥내소화전 예비 펌프	지하 2층 펌프실	횡형다단	65	50	260	120	15	3	380	60	○	
FP 03	1		옥내소화전 충압 펌프	지하 2층 펌프실	입형다단	32	32	60	120	3.7	3	380	60	○	
FP 04	1		연결송수관 가압펌프	지하 2층 펌프실	횡형다단	100	80	1,200	90	37	3	380	60	○	
FP 05	1		스프링클러 주 펌프	지하 2층 펌프실	횡형다단	125	100	2,520	134	110	3	380	60	○	
FP 06	1		스프링클러 예비 펌프	지하 2층 펌프실	횡형다단	125	100	2,520	134	110	3	380	60	○	
FP 07	1		스프링클러 충압 펌프	지하 2층 펌프실	입형다단	32	32	60	134	3.7	3	380	60	○	
PS 01	2		옥내소화전, 스프링클러 펌프 기동용 압력 스위치	전자식											검정품,전자식 압력스위치20k
															방진장치, 내진장치 및 기타 표준 부속품 일체 포함 KS 규격에서 정해진 효율 이상의 제품
FP 08	1	근린생활시설	옥내소화전 및 스프링클러 주 펌프	근생 펌프실	횡형다단	125	100	1,860	55	30	3	380	60		
FP 09	1		옥내소화전 및 스프링클러 예비 펌프	근생 펌프실	엔진펌프	125	100	1,860	55	30	3	380	60		
FP 10	1		옥내소화전 및 스프링클러 충압 펌프	근생 펌프실	입형다단	32	32	60	55	1.5	3	380	60		
PS 02	1		옥내소화전 및 스프링클러 펌프 기동용 압력 스위치	전자식											검정품,전자식 압력스위치10k

설계명 PROJECT TITLE

화성동탄(2)A76-2BL
민간참여 공동주택사업

주기 NOTE

1. 장비의 수량 및 사양, 형태 등은 제조사 선정에 따라 변경될 수 있음.

NO	DATE	REVISION DESCRIPTION	APPD

설 계 DESIGN

파트장
본부장
PM
담당

대표전화

축 척	SCALE
A1	1 / NONE
A3	1 / NONE

일 자 DATE
2025. 12.

설계번호 PROJECT NO.
AR - 23 - 026

도면화일명 DWG. FILE NAME

도면번호 SHEET NO.
MF - 005

도면명 SUBJECT TITLE
장비일람표-1

장 비 일 람 표-2

■ 제 연 설 비

장비번호	수량	명 칭	설치위치	형 식	풍 량	정 압	동 력	팬 번호	모 터			비상전원	비 고
					CMH	mmHg	kw		Ph	V	Hz		
FSF - 3531- 01	1	공동주택용 특별피난계단 및 비상용승강기 전실 제연설비 급기 FAN	지하2층 제연팬룸	SIROCCO	34,000	45	11	# 7.0 SS	3	380	60	○	
FSF - 3531- 02	1	공동주택용 특별피난계단 및 비상용승강기 전실 제연설비 급기 FAN	지하2층 제연팬룸	SIROCCO	34,000	45	11	# 7.0 SS	3	380	60	○	
FSF - 3532- 01	1	공동주택용 특별피난계단 및 비상용승강기 전실 제연설비 급기 FAN	지하2층 제연팬룸	SIROCCO	20,000	45	7.5	# 5.5 SS	3	380	60	○	
FSF - 3532- 02	1	공동주택용 특별피난계단 및 비상용승강기 전실 제연설비 급기 FAN	지하2층 제연팬룸	SIROCCO	23,000	50	7.5	# 6.0 SS	3	380	60	O	
FSF - 3534- 01	1	공동주택용 특별피난계단 및 비상용승강기 전실 제연설비 급기 FAN	지하2층 제연팬룸	SIROCCO	20,000	45	7.5	# 5.5 SS	3	380	60	○	
FSF - 3534- 02	1	공동주택용 특별피난계단 및 비상용승강기 전실 제연설비 급기 FAN	지하2층 제연팬룸	SIROCCO	23,000	50	7.5	# 6.0 SS	3	380	60	O	
FSF - 3535- 01	1	공동주택용 특별피난계단 및 비상용승강기 전실 제연설비 급기 FAN	지하2층 제연팬룸	SIROCCO	20,000	45	7.5	# 5.5 SS	3	380	60	○	
FSF - 3535- 02	1	공동주택용 특별피난계단 및 비상용승강기 전실 제연설비 급기 FAN	지하2층 제연팬룸	SIROCCO	27,000	50	11	# 6.0 SS	3	380	60	○	
FSF - 3536- 01	1	공동주택용 특별피난계단 및 비상용승강기 전실 제연설비 급기 FAN	지하2층 제연팬룸	SIROCCO	27,000	50	11	# 6.0 SS	3	380	60	○	
FSF - 3537- 01	1	공동주택용 특별피난계단 및 비상용승강기 전실 제연설비 급기 FAN	지하1층 제연팬룸	SIROCCO	22,000	50	7.5	# 5.5 SS	3	380	60	O	
FSF - 3537- 02	1	공동주택용 특별피난계단 및 비상용승강기 전실 제연설비 급기 FAN	지하1층 제연팬룸	SIROCCO	34,000	55	11.0	# 7.0 SS	3	380	60	O	
FSF - 3538- 01	1	공동주택용 특별피난계단 및 비상용승강기 전실 제연설비 급기 FAN	지하1층 제연팬룸	SIROCCO	22,000	50	7.5	# 5.5 SS	3	380	60	O	
FSF - 3538- 02	1	공동주택용 특별피난계단 및 비상용승강기 전실 제연설비 급기 FAN	지하1층 제연팬룸	SIROCCO	22,000	50	7.5	# 5.5 SS	3	380	60	O	
FSF - 3539- 01	1	공동주택용 특별피난계단 및 비상용승강기 전실 제연설비 급기 FAN	지하1층 제연팬룸	SIROCCO	34,000	55	11.0	# 7.0 SS	3	380	60	O	
FSF - 3539- 02	1	공동주택용 특별피난계단 및 비상용승강기 전실 제연설비 급기 FAN	지하1층 제연팬룸	SIROCCO	34,000	55	11.0	# 7.0 SS	3	380	60	O	
FSF - 3540- 01	1	공동주택용 특별피난계단 및 비상용승강기 전실 제연설비 급기 FAN	지하1층 제연팬룸	SIROCCO	40,000	50	15	# 7.0 SS	3	380	60	O	
FSF - 3540- 02	1	공동주택용 특별피난계단 및 비상용승강기 전실 제연설비 급기 FAN	지하1층 제연팬룸	SIROCCO	34,000	55	11.0	# 7.0 SS	3	380	60	O	
FSF - 3541- 01	1	공동주택용 특별피난계단 및 비상용승강기 전실 제연설비 급기 FAN	지하1층 제연팬룸	SIROCCO	40,000	50	15	# 7.0 SS	3	380	60	O	
FSF - 3541- 02	1	공동주택용 특별피난계단 및 비상용승강기 전실 제연설비 급기 FAN	지하1층 제연팬룸	SIROCCO	34,000	55	11.0	# 7.0 SS	3	380	60	O	
FSF - 3542- 01	1	공동주택용 특별피난계단 및 비상용승강기 전실 제연설비 급기 FAN	지하1층 제연팬룸	SIROCCO	40,000	50	15	# 7.0 SS	3	380	60	O	
FSF - 3542- 02	1	공동주택용 특별피난계단 및 비상용승강기 전실 제연설비 급기 FAN	지하1층 제연팬룸	SIROCCO	34,000	55	11.0	# 7.0 SS	3	380	60	O	
FSF - 3543- 01	1	공동주택용 특별피난계단 및 비상용승강기 전실 제연설비 급기 FAN	지하1층 제연팬룸	SIROCCO	40,000	50	15	# 7.0 SS	3	380	60	O	
FSF - 3543- 02	1	공동주택용 특별피난계단 및 비상용승강기 전실 제연설비 급기 FAN	지하1층 제연팬룸	SIROCCO	32,000	45	11.0	# 6.5 SS	3	380	60	○	
FSF - 3544- 01	1	공동주택용 특별피난계단 및 비상용승강기 전실 제연설비 급기 FAN	지하1층 제연팬룸	SIROCCO	34,000	55	11.0	# 7.0 SS	3	380	60	O	
FSF - 3544- 02	1	공동주택용 특별피난계단 및 비상용승강기 전실 제연설비 급기 FAN	지하1층 제연팬룸	SIROCCO	34,000	55	11.0	# 7.0 SS	3	380	60	O	
FSF - 3545- 01	1	공동주택용 특별피난계단 및 비상용승강기 전실 제연설비 급기 FAN	지하1층 제연팬룸	SIROCCO	34,000	55	11.0	# 7.0 SS	3	380	60	O	
FSF - 3545- 02	1	공동주택용 특별피난계단 및 비상용승강기 전실 제연설비 급기 FAN	지하1층 제연팬룸	SIROCCO	40,000	50	15	# 7.0 SS	3	380	60	O	
FSF - 3546- 01	1	공동주택용 특별피난계단 및 비상용승강기 전실 제연설비 급기 FAN	지하2층 제연팬룸	SIROCCO	34,000	45	11	# 7.0 SS	3	380	60	○	
FSF - 3546- 02	1	공동주택용 특별피난계단 및 비상용승강기 전실 제연설비 급기 FAN	지하2층 제연팬룸	SIROCCO	34,000	45	11	# 7.0 SS	3	380	60	○	
FSF - 3547- 01	1	공동주택용 특별피난계단 및 비상용승강기 전실 제연설비 급기 FAN	지하2층 제연팬룸	SIROCCO	40,000	50	15	# 7.0 SS	3	380	60	O	
FSF - 3547- 02	1	공동주택용 특별피난계단 및 비상용승강기 전실 제연설비 급기 FAN	지하2층 제연팬룸	SIROCCO	34,000	45	11	# 7.0 SS	3	380	60	○	

설계명 PROJECT TITLE


화성동탄(2)A76-2BL
민간참여 공동주택사업

주기 NOTE

1. 장비의 수량 및 사양, 형태 등은 제조사 선정에 따라 변경될 수 있음.

NO	DATE	REVISION DESCRIPTION	APPD
△			
△			
△			
△			

설 계 DESIGN	
	파트장
	본부장
	PM
	담당
대표전화	
축 척	SCALE
A1	1 / NONE
A3	1 / NONE
일 자 DATE	2025. 12.
설계번호 PROJECT NO.	AR - 23 - 026
도면화일명 DWG. FILE NAME	
도면번호 SHEET NO.	MF - 006
도면명 SUBJECT TITLE	장비일람표-2

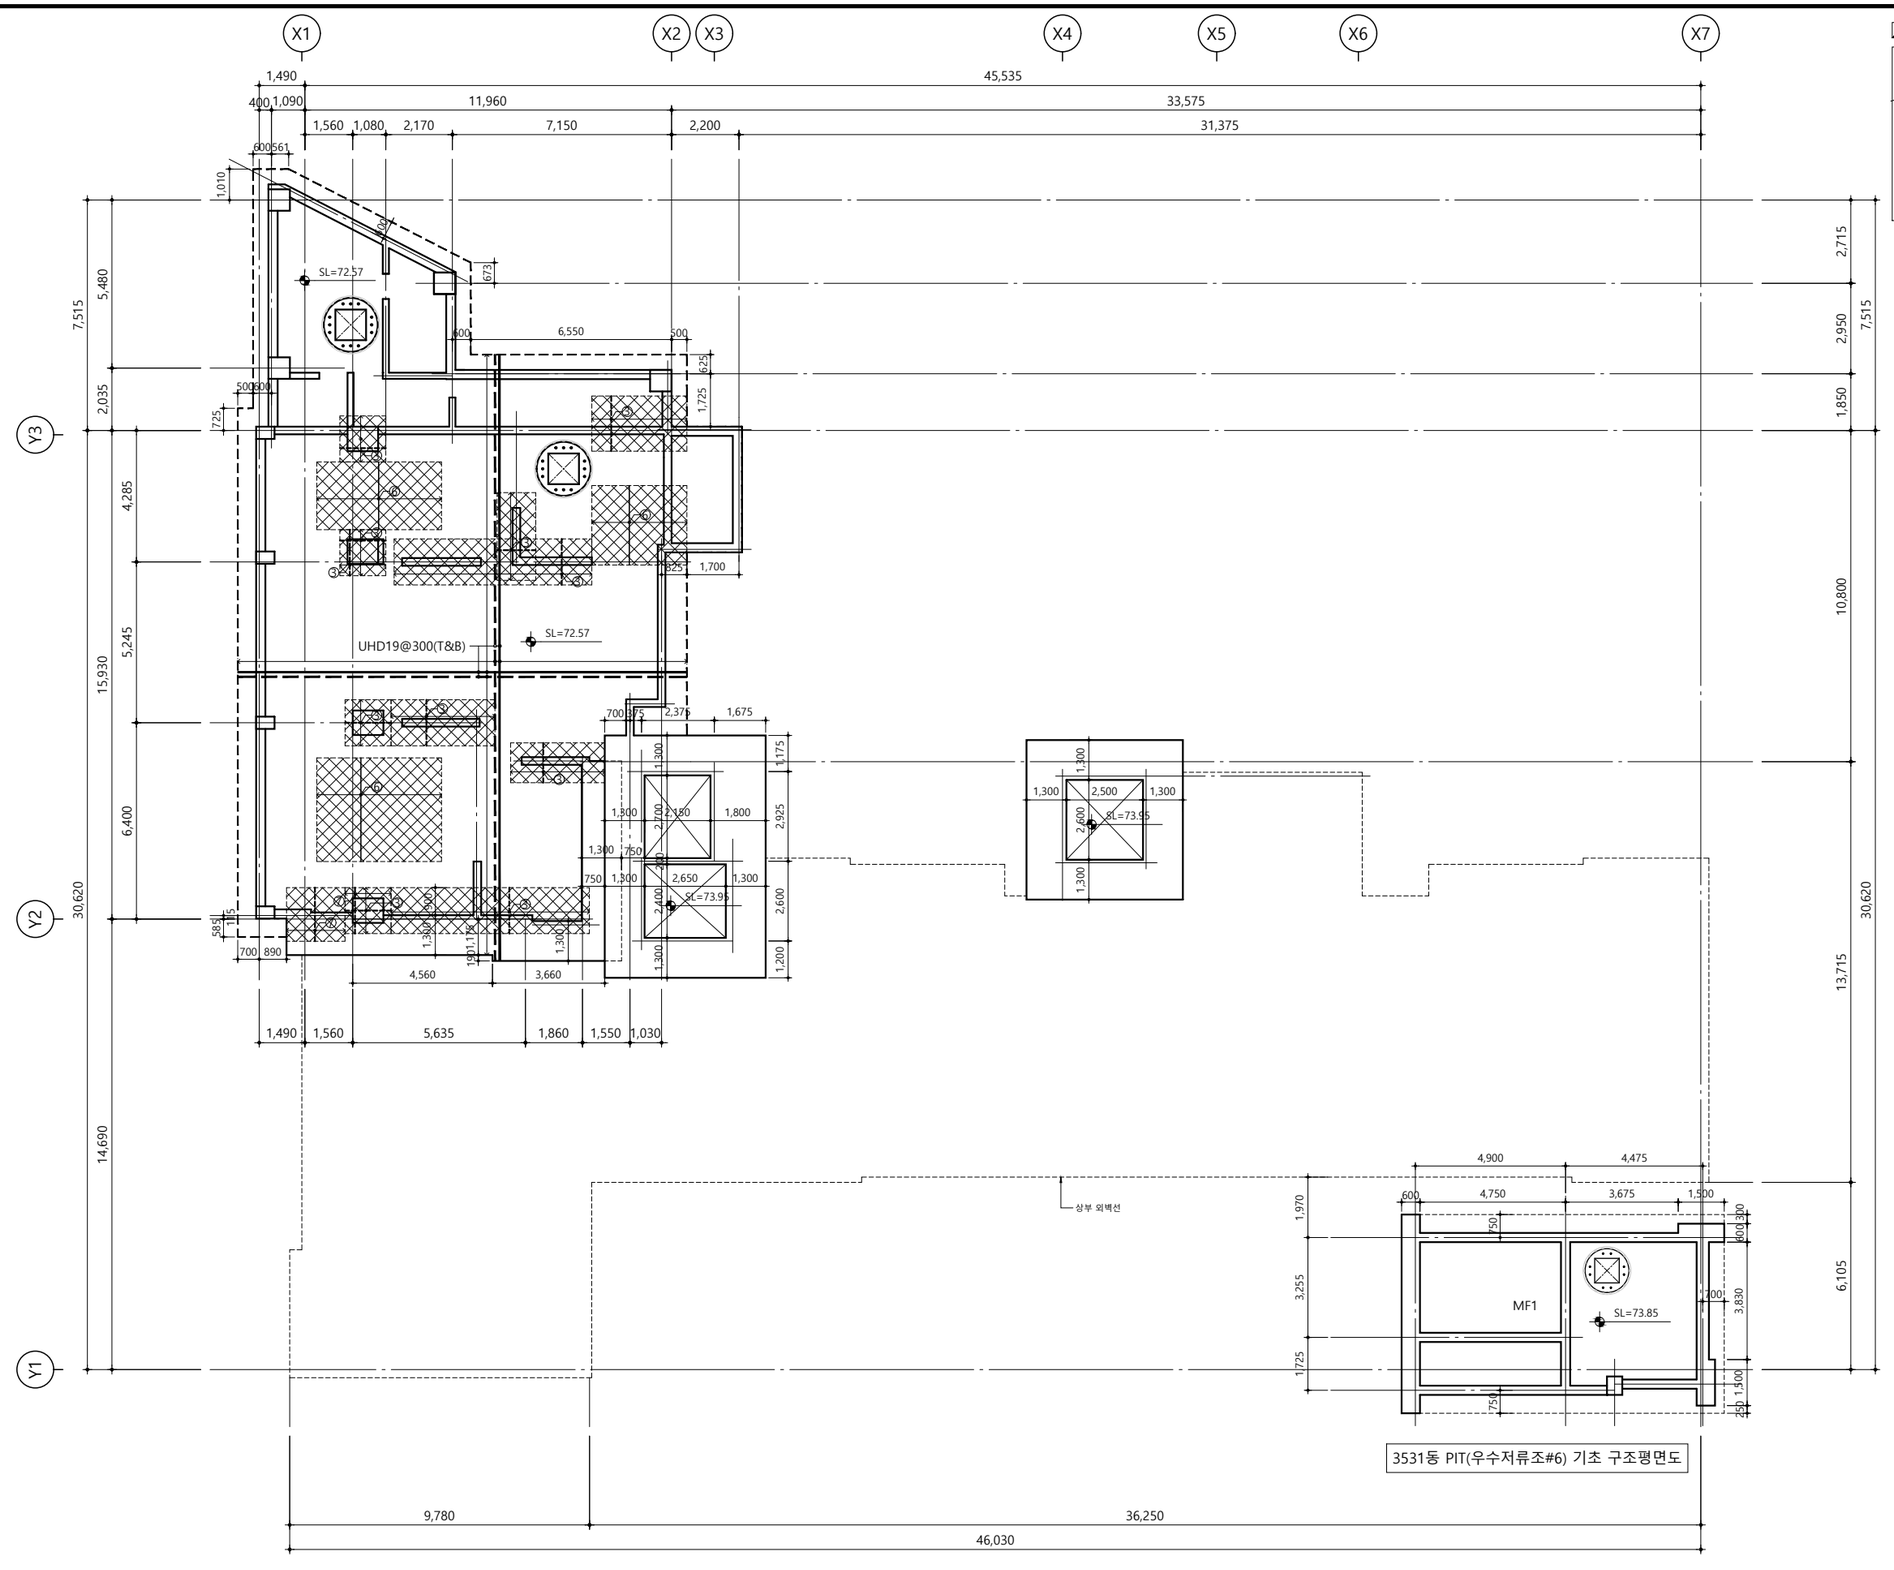

3531동 PIT(우수저류조#6) 기초 구조평면도

1 3531동 PIT 기초 구조평면도

축척 : 1/100(A3:200)

KEY MAP



* 레벨 및 단차

: SL=73.02

경기주택도시공사

설계명 PROJECT TITLE

화성동탄(2)A76-2BL 민간참여 공동주택사업

주기 NOTE


1. 모든 치수, 개구부,설비위치 등은 건축도면과 비교 확인 후 시공 할 것
2. 재료강도는 구조일반사항 참조
3. 지내력기초 시공 전 현장 평판재하시험을 통해 설계지내력 확보 확인이 필요하며, 미확보시 파일기초로 변경될 수 있음. (상세검토시 지내력기초↔파일기초 변경 가능함)
4. 모든 배근, 부재사이즈, 구조계획 등은 현장 여건에 따라 변경될 수 있음
5. 현장여건에 따라 구조전문가의 확인 후 기초형식, 파일종류, 기초절곡부 라인 등 기초 관련 사항은 변경이 가능하며 지반현황에 따라 병용기초로 적용될 수 있습니다. 단, 구조전문가의 확인 후 변경이 가능합니다.
6. 기초두께 : THK.1,300
7. 설계지내력 : fe=500kN/㎡

보강근 :

① UHD19@300(B.ADD) ⑦ UHD19@150(B.ADD)
② UHD22@300(B.ADD) ⑧ UHD22@150(B.ADD)
③ UHD16@300(B.ADD) ⑨ UHD16@150(B.ADD)
④ UHD19@300(T.ADD) ⑩ UHD19@150(T.ADD)
⑤ UHD22@300(T.ADD) ⑪ UHD22@150(T.ADD)
⑥ UHD16@300(T.ADD) ⑫ UHD16@150(T.ADD)


: 기초절곡부
: 기초보강구간

UHD## @ 300 + ## @ 150 보강근 배근 TYP.

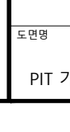

NO	DATE	REVISION DESCRIPTION	APPD

설계 DESIGN	
	파트장
	본부장
	PM
	담당
대표전화	
축 척	SCALE
A1	1 / 100
A3	1 / 200
일 자	DATE 2025. 10.
설계번호	PROJECT NO. AR - 23 - 026
도면화일명	DWG. FILE NAME
도면번호	SHEET NO. S01 - 201
도면명	SUBJECT TITLE 3531동 PIT 기초 구조평면도

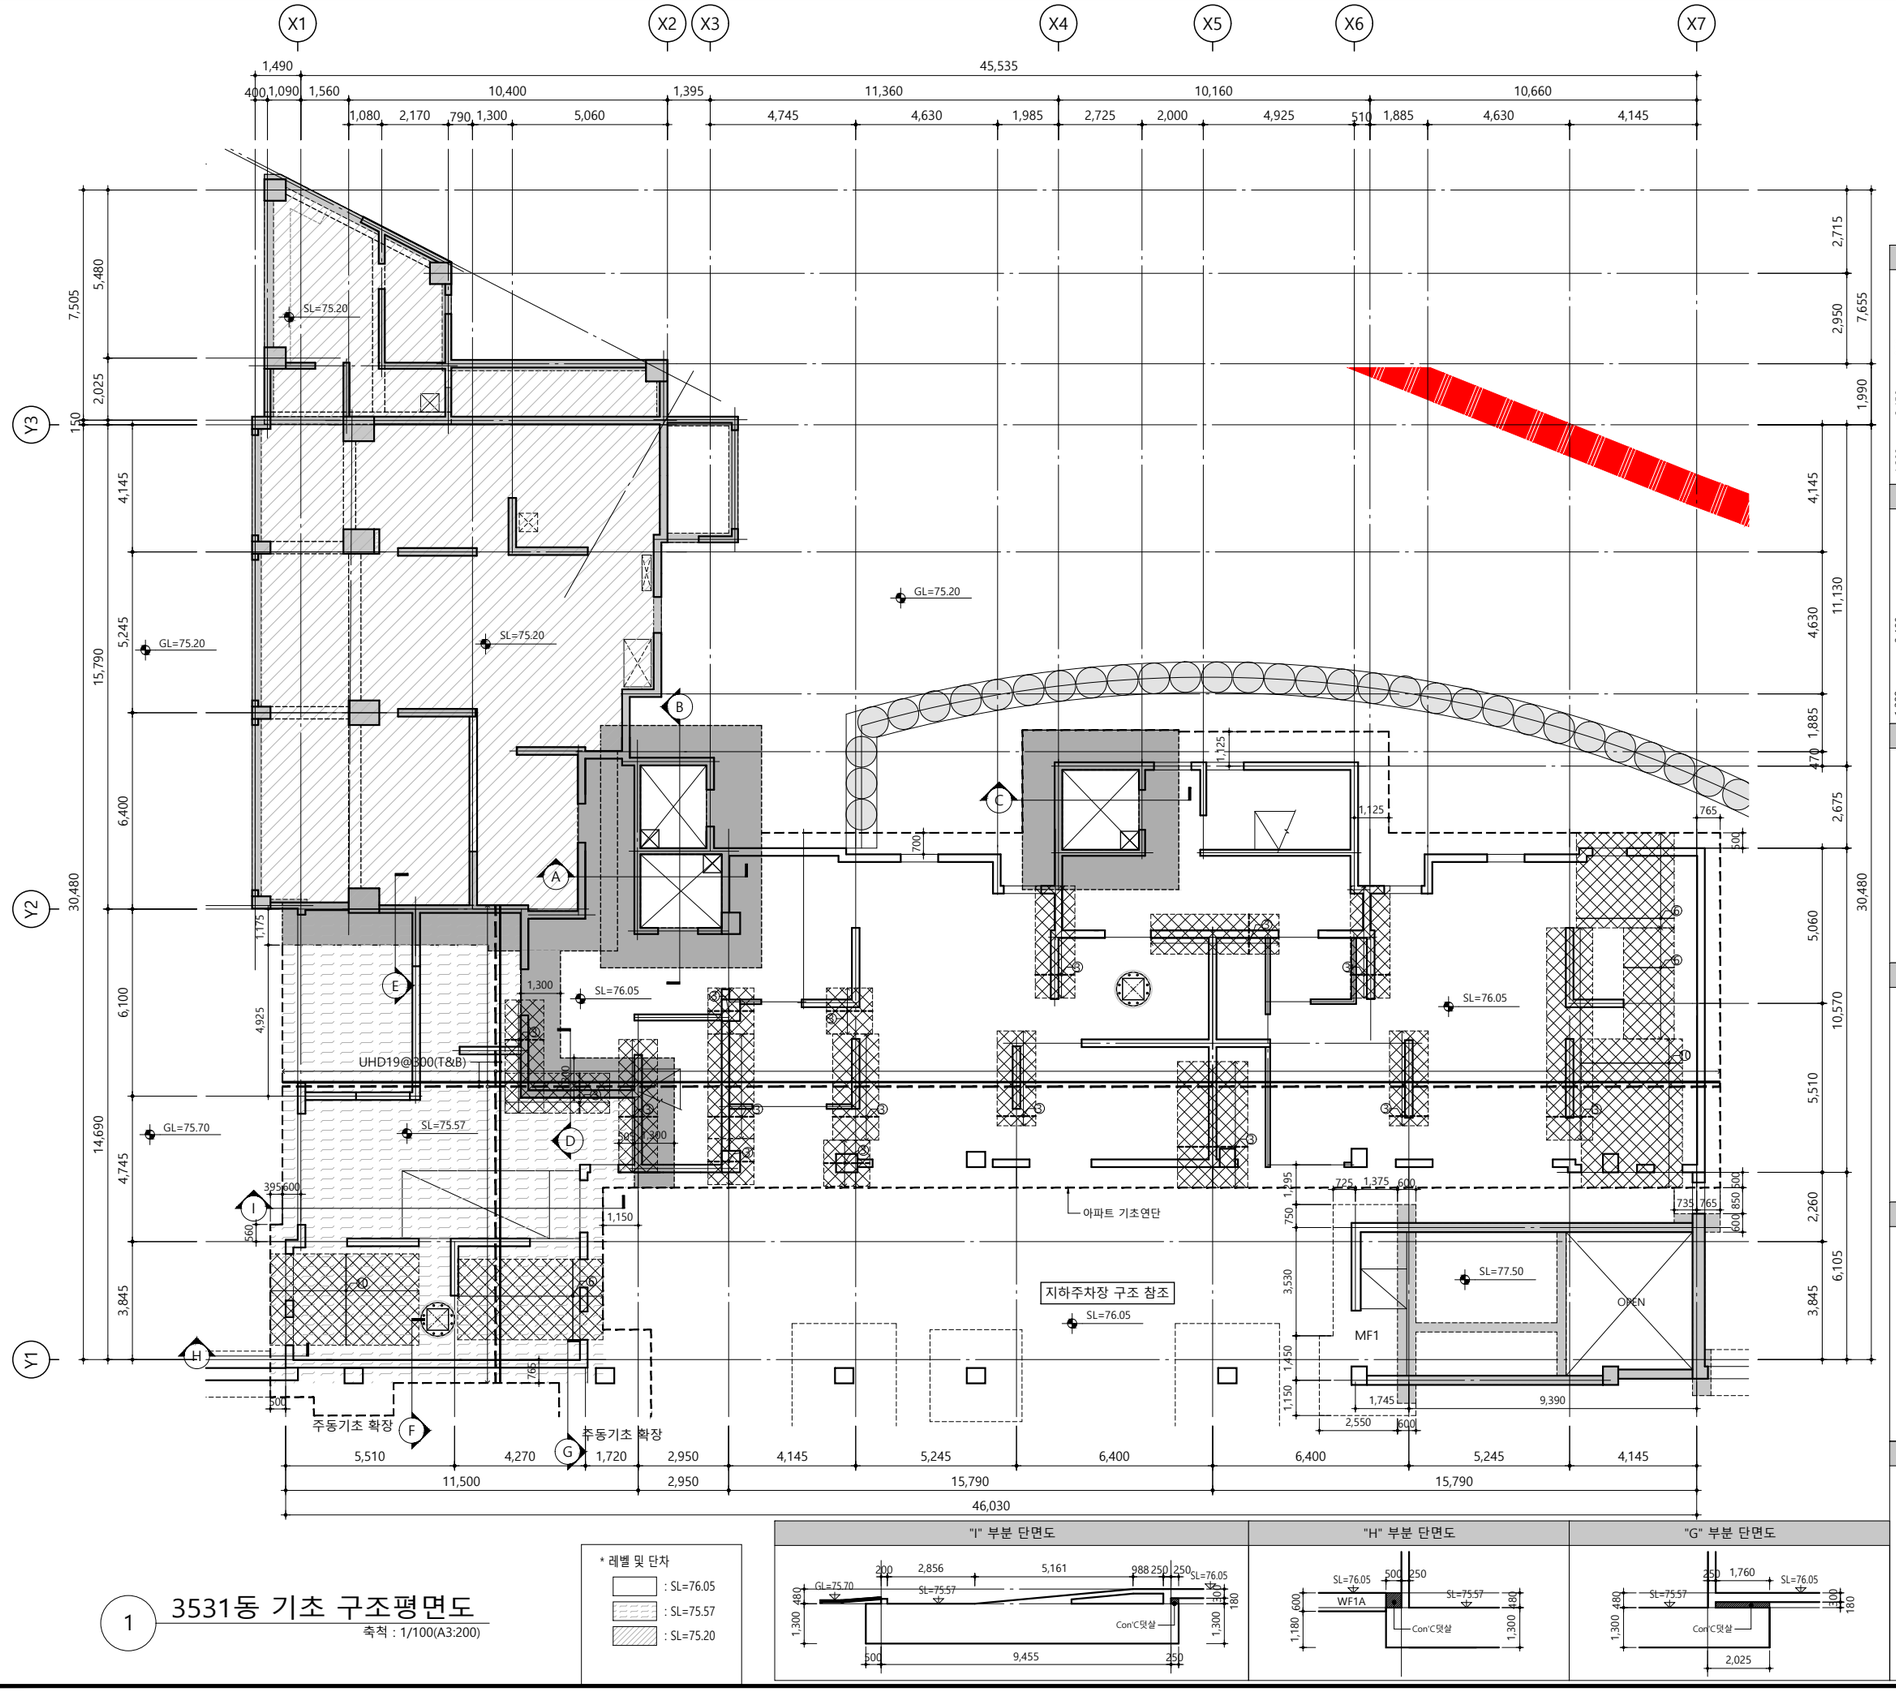

1 3531동 기초 구조평면도

축척 : 1/100(A3:200)

* 레벨 및 단차
: SL=76.05
: SL=75.57
: SL=75.20

"I" 부분 단면도


"H" 부분 단면도

"G" 부분 단면도


KEY MAP




"A" 부분 단면도

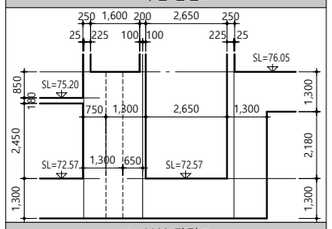


"B" 부분 단면도

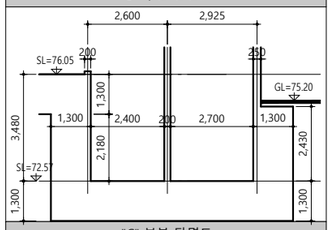


"C" 부분 단면도

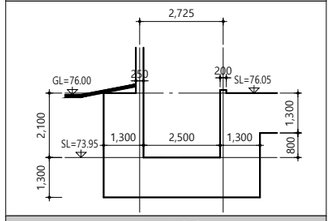


"D" 부분 단면도

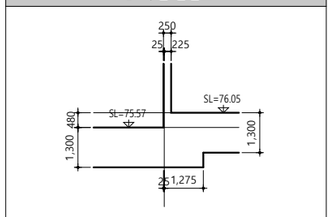

"E" 부분 단면도

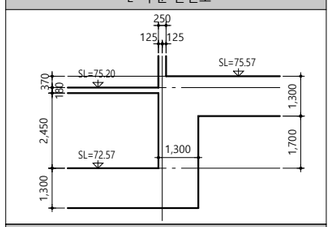

"F" 부분 단면도

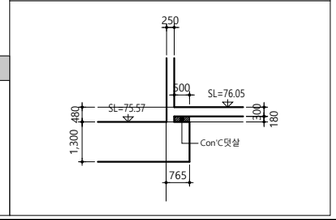

경기주택도시공사

설계명 PROJECT TITLE

화성동탄(2)A76-2BL
민간참여 공동주택사업

주기 NOTE


1. 모든 치수, 개구부,설비위치 등은 건축도면과 비교 확인 후 시공 할 것
2. 재료강도는 구조일반사항 참조
3. 지내력기초 시공 전 현장 평판재하시험을 통해 설계지내력 확보 확인이 필요하며, 미확보시 파일기초로 변경될 수 있음. (상세검토시 지내력기초↔파일기초 변경 가능함)
4. 모든 배근, 부재사이즈, 구조계획 등은 현장 여건에 따라 변경될 수 있음
5. 현장여건에 따라 구조전문가의 확인 후 기초형식, 파일종류, 기초절곡부 라인 등 기초 관련 사항은 변경이 가능하며 지반현황에 따라 병용기초로 적용될 수 있습니다. 단, 구조전문가의 확인 후 변경이 가능합니다.
6. 기초두께 : THK.1,300
7. 설계지내력 : fe=500kN/㎡

보강근 :

① UHD19@300(B.ADD) ⑦ UHD19@150(B.ADD)
② UHD22@300(B.ADD) ⑧ UHD22@150(B.ADD)
③ UHD16@300(B.ADD) ⑨ UHD16@150(B.ADD)
④ UHD19@300(T.ADD) ⑩ UHD19@150(T.ADD)
⑤ UHD22@300(T.ADD) ⑪ UHD22@150(T.ADD)
⑥ UHD16@300(T.ADD) ⑫ UHD16@150(T.ADD)

: 기초절곡부
: 기초보강구간

UHD## @ 300 + ## @ 150 보강근 배근 TYP.

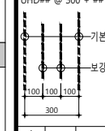

NO	DATE	REVISION DESCRIPTION	APPD

설 계 DESIGN

파트장
본부장
PM
담당

대표전화

축 척	SCALE
A1	1 / 100
A3	1 / 200


일 자 DATE 2025. 10.

설계번호 PROJECT NO. AR - 23 - 026


도면화일명 DWG. FILE NAME

도면번호 SHEET NO. S01 - 202

도면명 SUBJECT TITLE
3531동
기초 구조평면도

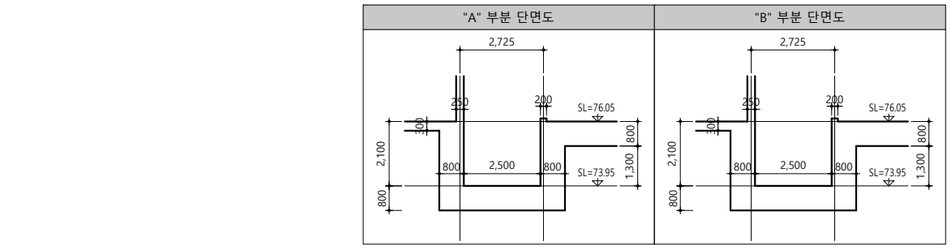



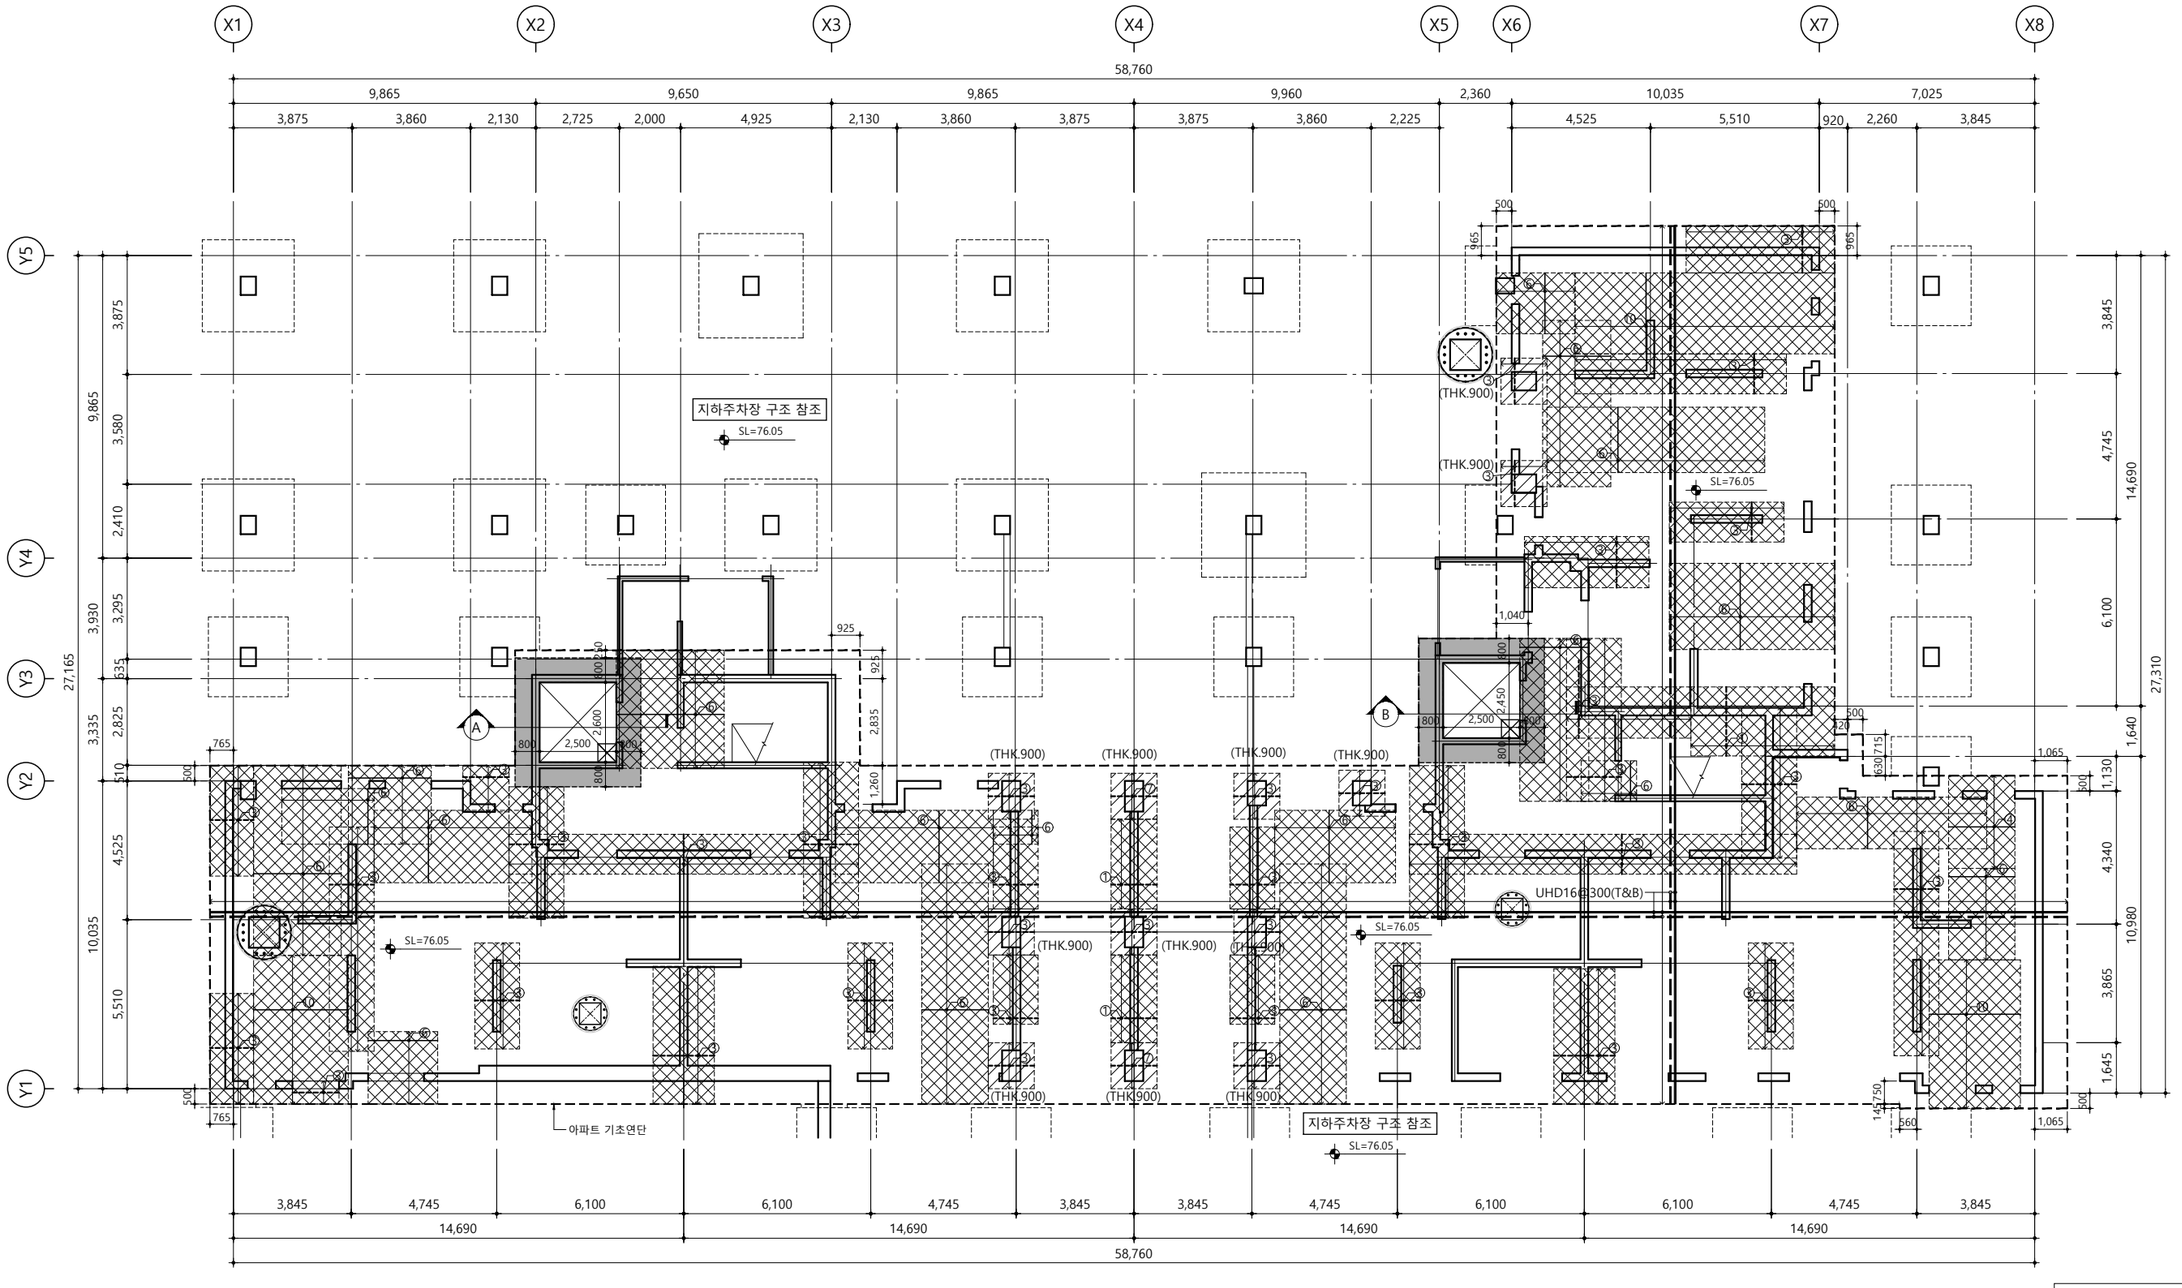

1 3532동 기초 구조평면도(지내력)

축척 : 1/100(A3:200)

* 레벨 및 단차

: SL=76.05

경기주택도시공사

설계명 PROJECT TITLE

화성동탄(2)A76-2BL
민간참여 공동주택사업

주기 NOTE


1. 모든 치수, 개구부,설비위치 등은 건축도면과 비교 확인 후 시공 할 것
2. 재료강도는 구조일반사항 참조
3. 지내력기초 시공 전 현장 평판재하시험을 통해 설계지내력 확보 확인이 필요하며, 미확보시 파일기초로 변경될 수 있음. (상세검토시 지내력기초↔파일기초 변경 가능함)
4. 모든 배근, 부재사이즈, 구조계획 등은 현장 여건에 따라 변경될 수 있음
5. 현장여건에 따라 구조전문가의 확인 후 기초형식, 파일종류, 기초절곡부 라인 등 기초 관련 사항은 변경이 가능하며 지반현황에 따라 병용기초로 적용될 수 있습니다. 단, 구조전문가의 확인 후 변경이 가능합니다.
6. 기초두께 : THK.800 ▨ : THK.900
7. 설계지내력 : fe=500kN/㎡

보강근 :

① UHD19@300(B.ADD) ⑦ UHD19@150(B.ADD)
② UHD22@300(B.ADD) ⑧ UHD22@150(B.ADD)
③ UHD25@300(B.ADD) ⑨ UHD16@150(B.ADD)
④ UHD19@300(T.ADD) ⑩ UHD19@150(T.ADD)
⑤ UHD22@300(T.ADD) ⑪ UHD22@150(T.ADD)
⑥ UHD16@300(T.ADD) ⑫ UHD16@150(T.ADD)

▨ : 기초절곡부
▨ : 기초보강구간

UHD## @ 300 + ## @ 150 보강근 배근 TYP.

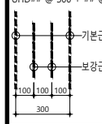

NO	DATE	REVISION DESCRIPTION	APPD

설계 DESIGN	
	파트장
	본부장
	PM
	담당
대표전화	

축 척	SCALE
A1	1 / 100
A3	1 / 200

일 자 DATE 2025. 10.


설계번호 PROJECT NO. AR - 23 - 026

도면화일명 DWG. FILE NAME


도면번호 SHEET NO. S01 - 203


도면명 SUBJECT TITLE

3532동
기초 구조평면도

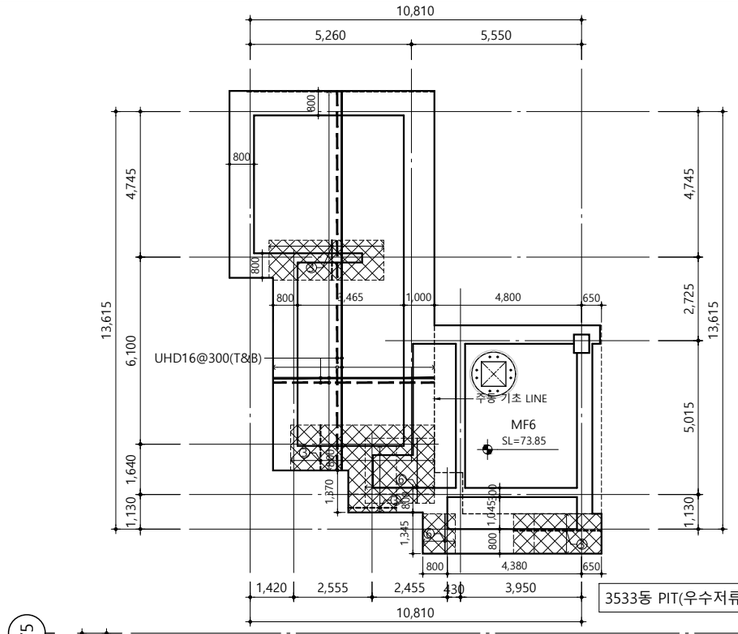


3533동 PIT(우수저류조#8) 기초 구조평면도

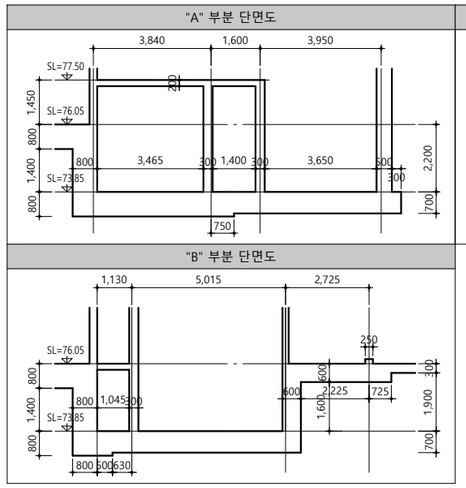

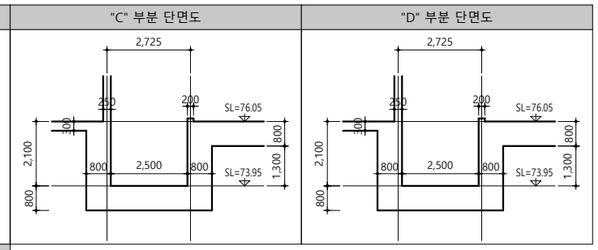



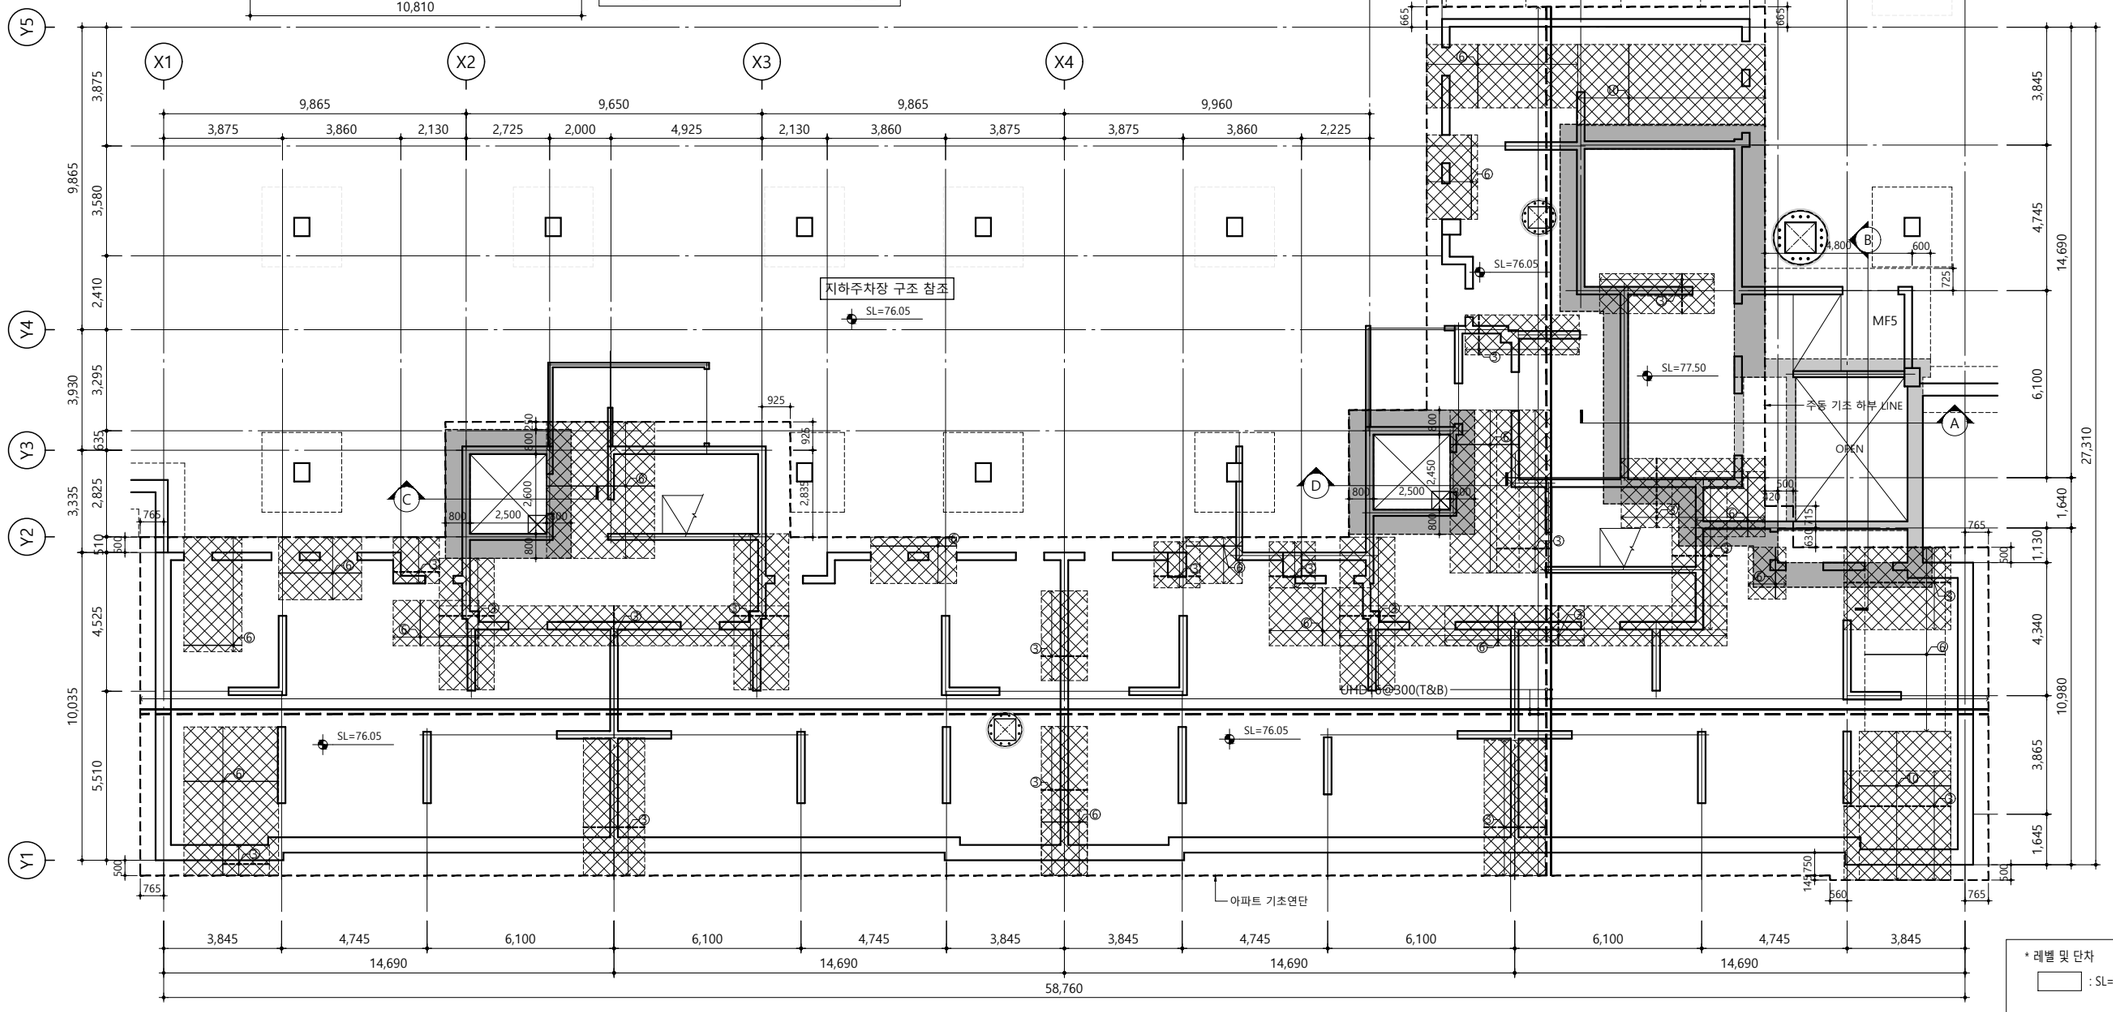

* 레벨 및 단차
: SL=76.05

1 3533동 기초 구조평면도(지내력)
축척 : 1/100(A3:200)

경기주택도시공사

설계명 PROJECT TITLE

화성동탄(2)A76-2BL 민간참여 공동주택사업

주기 NOTE


1. 모든 치수, 개구부,설비위치 등은 건축도면과 비교 확인 후 시공 할 것
2. 재료강도는 구조일반사항 참조
3. 지내력기초 시공 전 현장 평판재하시험을 통해 설계지내력 확보 확인이 필요하며, 미확보시 파일기초로 변경될 수 있음. (상세검토시 지내력기초↔파일기초 변경 가능함)
4. 모든 배근, 부재사이즈, 구조계획 등은 현장 여건에 따라 변경될 수 있음
5. 현장여건에 따라 구조전문가의 확인 후 기초형식, 파일종류, 기초절곡부 라인 등 기초 관련 사항은 변경이 가능하며 지반현황에 따라 병용기초로 적용될 수 있습니다. 단, 구조전문가의 확인 후 변경이 가능합니다.
6. 기초두께 : THK.800
7. 설계지내력 : fe=500kN/㎡

보강근 :

① UHD19@300(B.ADD) ⑦ UHD19@150(B.ADD)
② UHD22@300(B.ADD) ⑧ UHD22@150(B.ADD)
③ UHD16@300(B.ADD) ⑨ UHD16@150(B.ADD)
④ UHD19@300(T.ADD) ⑩ UHD19@150(T.ADD)
⑤ UHD22@300(T.ADD) ⑪ UHD22@150(T.ADD)
⑥ UHD16@300(T.ADD) ⑫ UHD16@150(T.ADD)

: 기초절곡부
: 기초보강구간

UHD## @ 300 + ## @ 150 보강근 배근 TYP.

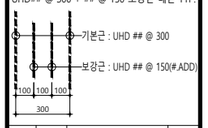

NO	DATE	REVISION DESCRIPTION	APPD
△			
△			
△			
△			

설계 DESIGN	
	파트장
	본부장
	PM
	담당
대표전화	
축 척	SCALE
A1	1 / 100
A3	1 / 200
일 자	DATE 2025. 10.
설계번호	PROJECT NO. AR - 23 - 026
도면화일명	DWG. FILE NAME
도면번호	SHEET NO. S01 - 204
도면명	SUBJECT TITLE 3533동 기초 구조평면도