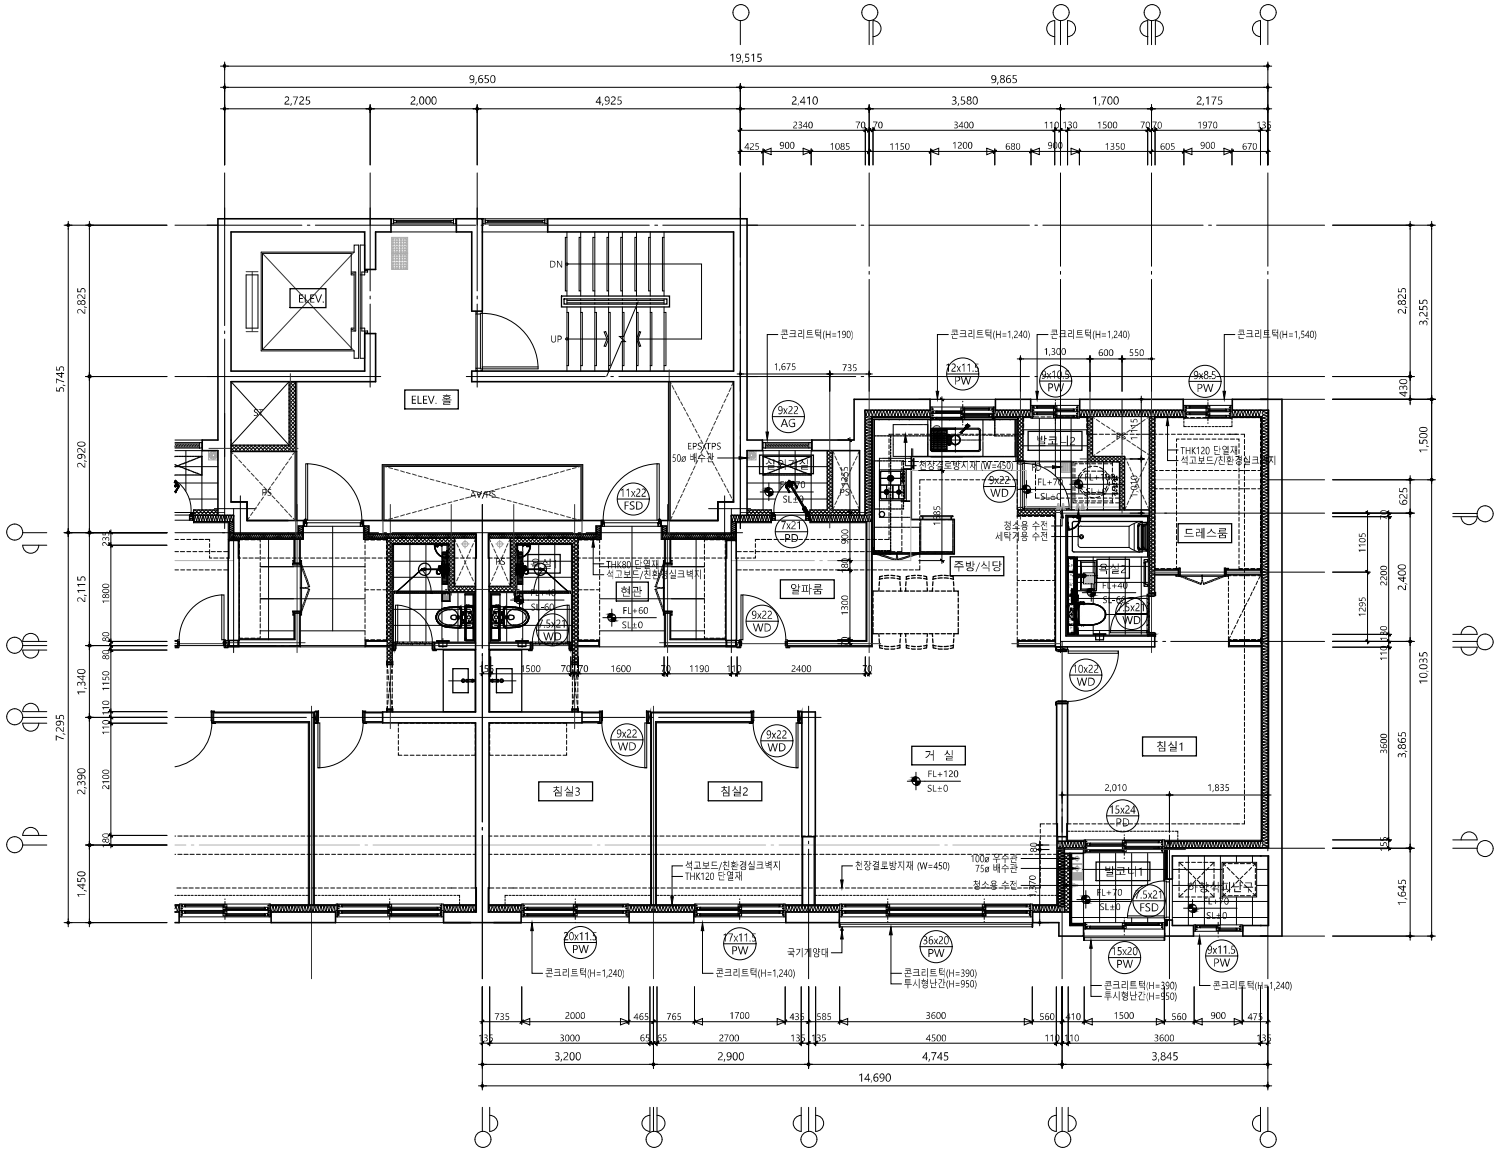


1 84m²A형 단위세대 평면도(확장형)

축척 : 1/50(A3:100)

경기주택도시공사

설계명 PROJECT TITLE

화성동탄(2)A76-2BL
민간참여 공동주택사업

주기 NOTE

1.고정형 가구 및 거울(현관, 주방, 침실, 욕실 등)이 설치되는 곳의 바닥, 벽, 천정에는 최종마감재가 설치되지 않음.
2.선홈통의 개소와 위치는 실시공시 변경될 수 있음.
3.AD/PD 버닥은 배관슬리브 매입후 콘크리트로 타설할 것.
4.AD/PD 나부 설비배관설치 후 배관 주변은 "내화구조의 인정 및 관리기준"에 적합하게 충진할 것.
5.외부창호는 내풍압 구조검토결과에 따라 서대별로 달리 시공될 수 있음.
6.침실2,3 벽체는 가변형벽체로 선택형에 선택형에 따라 변경될 수 있음.
7.부위별 마감은 실내재료마감표 참조.
각 세대의 마감은 견본주택 및 세대별 계약조건에 따라 변경될 수 있음.
8.확장형세대와 기본형세대가 접하는 부위는 에너지절약형 친환경주택의 건설기준에 적합한 단열조치할 것.
(단, 기본형세대 발코니부분 설치)
9.침실1 세대내 설치 바닥은 지정타일 마감.
10.결로방지단열재 (W=450) 두께 10
11.욕실의 결조벽면 역체방수 없음
12.세대내 마감은 인테리어를 기준으로 작성되었으며, 인테리어도면과 상이한 부분이 있을 경우에는 설계담당자와 협의후 시공할 것.
13.외부벽체의 단열은 단열성능 설계도 참조
14.천정평면도 및 욕실 확대평면도, 세대내 DOOR, 점검구 설치 위치는 인테리어도면 참조
15.세대내에 설치되는 진화단자반, 세대분전반 등은 인테리어도면 및 전기도면을 참조하여 시공할 것.
16.주방용, 욕실용 배기덕트의 발코니노출부분은 단열조치후 마감처리할 것.
17.1층, 필로티 세대는 하향식피난구 미설치.
(필로티 세대는 완강기 설치)
18.경량벽체 일부 구간은 옥자, 주방가구 등을 거치하기 위한 합판 보강 적용.
19. 콘크리트턱은 SL기준 높이임.

NO	DATE	REVISION DESCRIPTION	APPD

설계 DESIGN	파트장
	본부장
	PM
	담당
대표전화	
축 척	SCALE
A1	1 / 50
A3	1 / 100
일 자	DATE
	2025. 10.
설계번호	PROJECT NO.
	AR - 23 - 026
도면화일명	DWG. FILE NAME
도면번호	SHEET NO.
	A02 - 102
도면명	SUBJECT TITLE
	84㎡A형 단위세대 평면도(확장형)